


План насосной станции на отм. −2,200 (фрагмент) М 1:50

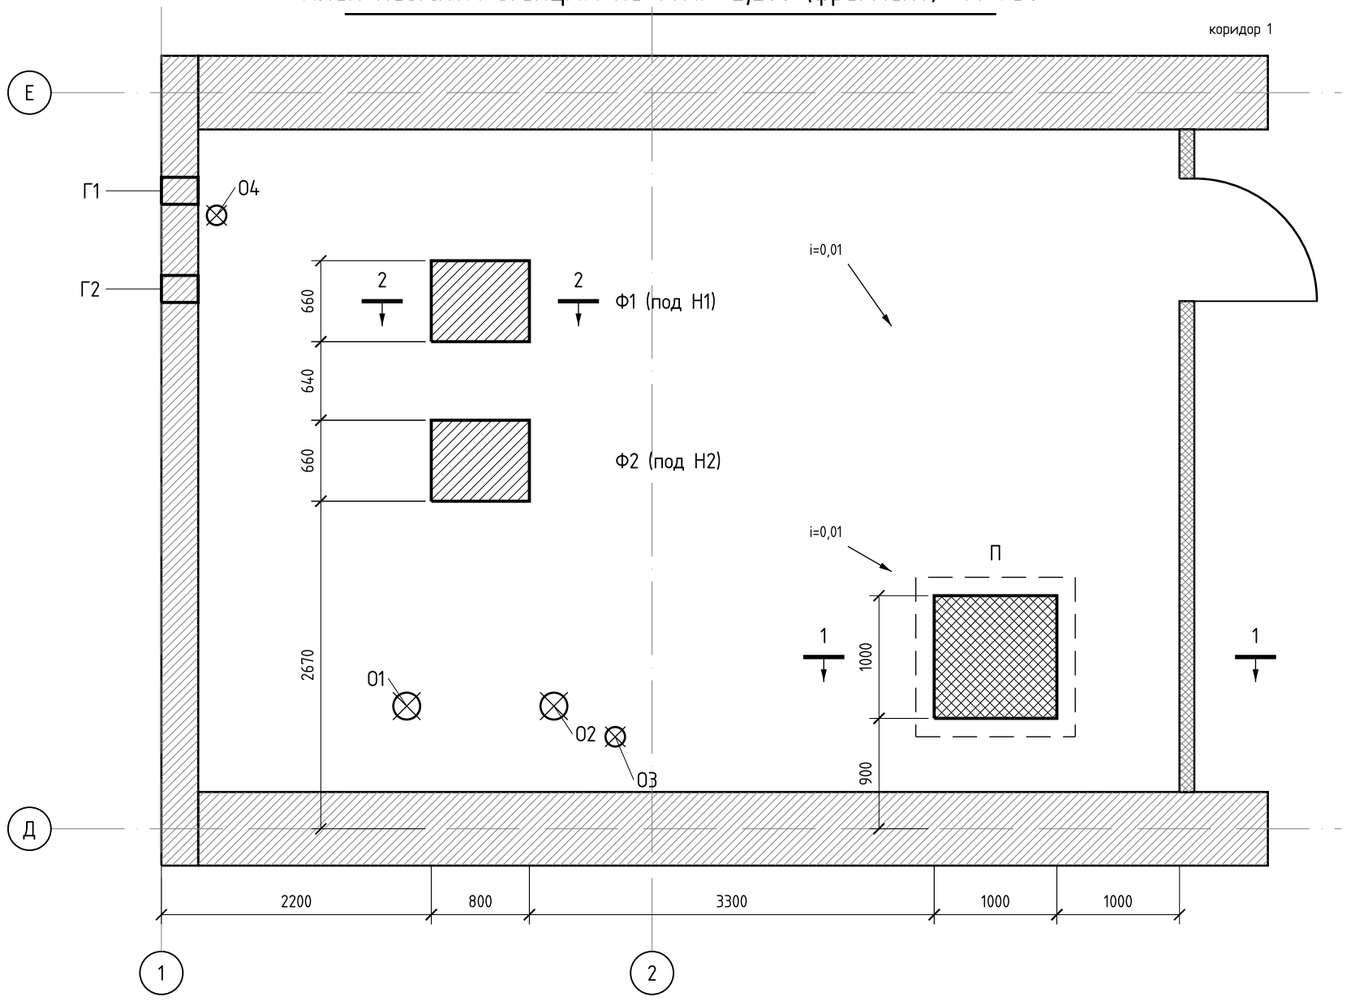

Разрез 1–1 М 1:20

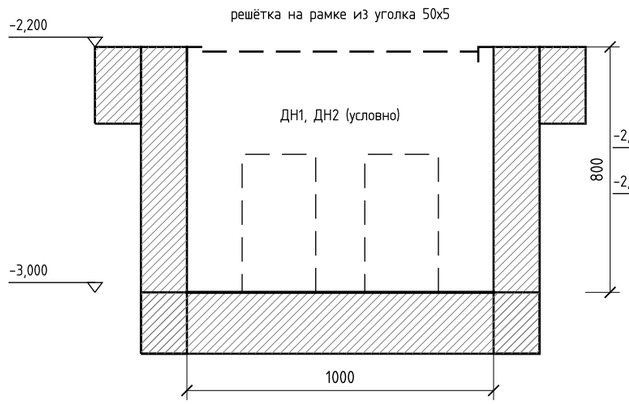

Разрез 2–2 М 1:20

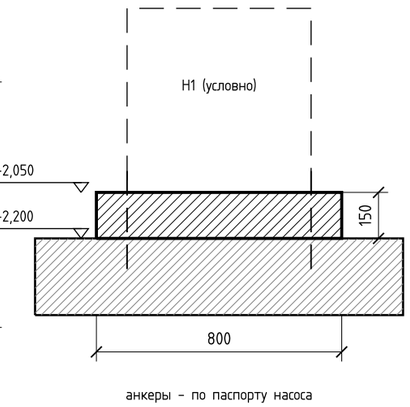

Перечень элементов

Обозн.	Элемент	Размеры, мм	Отметка	От оси 1 / оси Д, мм
П	Приямок	1000х1000х800 (в свету)	дно −3,000	6300 / 900 (угол)
Ф1	Основание под насос Н1	800х660х150	верх −2,050	2200 / 3970 (угол)
Ф2	Основание под насос Н2	800х660х150	верх −2,050	2200 / 2670 (угол)
Г1, Г2	Гильзы вводов в стене по оси 1	труба 219х6, L=500	ось −1,900	ось 1 / 5200 и 4400
О1	Отверстие: стояк Ст.В21-1 Ду150	под гильзу 219х6	перекрытие	2000 / 1000 (ось)
О2	Отверстие: стояк Ст.В22-1 Ду150	под гильзу 219х6	перекрытие	3200 / 1000 (ось)
О3	Отверстие: перемычка В2 Ду100	под гильзу 159х4,5	перекрытие	3700 / 750 (ось)
О4	Отверстие: линия к ГМ-80 Ду100	под гильзу 159х4,5	перекрытие	450 / 5000 (ось)

Задание принял

Раздел	Должность	Фамилия	Подпись	Дата
КР				

Требования к выполнению

1. Приямок – монолитный железобетонный, водонепроницаемый; толщины, армирование и гидроизоляцию определяет раздел КР. По периметру – закладная рамка из уголка 50х5 под съёмную решётку 1000х1000 (решётка – по спецификации ПТ, поз. 28), верх рамки – в уровне чистого пола. В приямке устанавливаются два погружных насоса массой по 16 кг.
2. Пол насосной – с уклоном 0,01 к приямку.
3. Основания Ф1, Ф2 – бетонные, размеры уточняются по паспорту поставленного насоса. Нагрузка на основание – до 3,0 кН (насос с водой и арматурой), анкерные болты – по паспорту насоса.
4. Гильзы Г1, Г2 закладываются в стену подвала по оси 1 при бетонировании; проход вводов – герметичный (узел 1, лист 11). В 300 мм от Г1 – гильза ввода В1 (раздел ВК, ось −2,100).
5. Отверстия О1–О4 – в перекрытии над подвалом (пом. 05 1 этажа), под стальные гильзы, закладываемые при бетонировании (узел 3, лист 11). Балки 20К2 не ослаблять.
6. Погонная нагрузка от трубопроводов обвязки на перекрытие подвала – до 0,7 кН/м (Ду200 с водой), крепление – по узлу 4.
7. Вдоль стен насосной проходят трубопроводы К1 и В1 раздела ВК (ОПР-01/24/2024-ДП1-ВК), приямок размещён в стороне от них.
8. Привязки – от осей здания; размеры – в мм, отметки – в м.

Изм.	Кол.уч	Лист	№ док.	Подп.	Дата
Разраб.					
Пров.					
Н.контр.					
ГИП		Хвостов			10.26

ОПР-01/24/2024-ДП1-ПТ.ЗД1

«Современный коммерческий оптово-продовольственный рынок (ОПР) по адресу: Донецкая область, г. Макеевка, Горняцкий район»

Док-павильон №23, №23.2 Рыба-Мясо. Пожаротушение (ВПВ, АУПТ, АУПП ВРУ)

Стадия	Лист	Листов
Р	1	1

Задание разделу КР. Приямок, основания под насосы, гильзы и отверстия

ООО «Технология»

Взам. инв. №

Подп. и дата

Инв. № подл.

Формат А3