

План насосной станции на отм. −2,200 (фрагмент) М 1:50

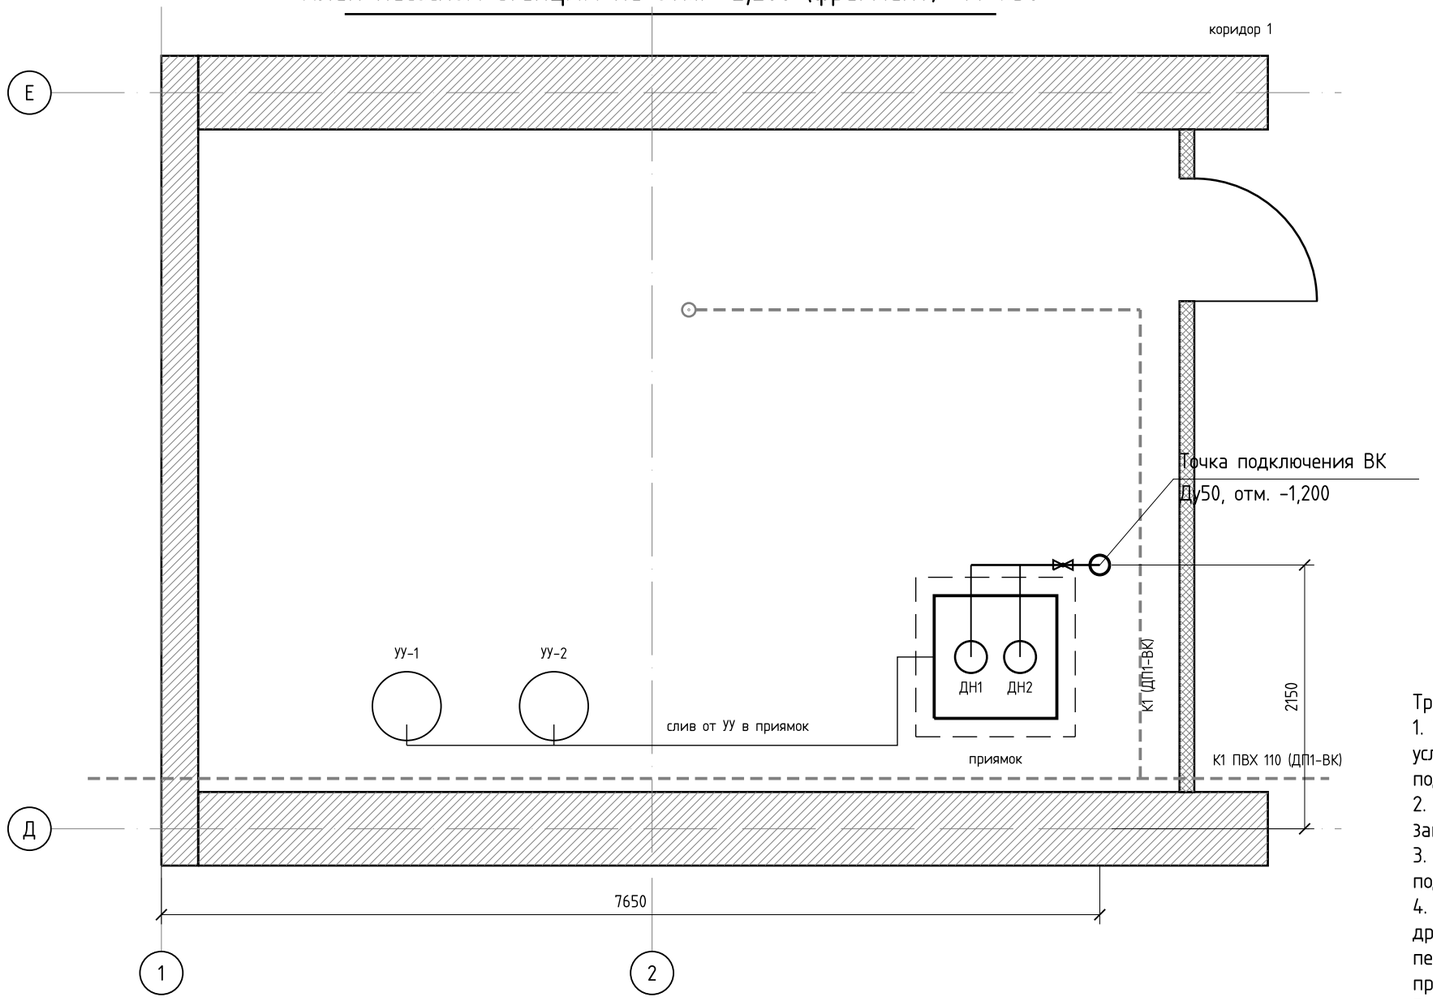

Разрез по напорной линии М 1:25

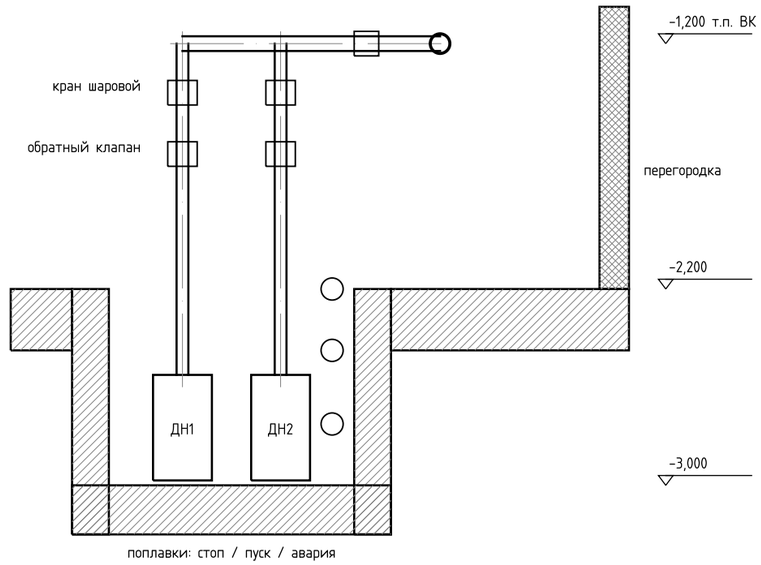

Исходные данные для раздела ВК

Параметр	Значение
Точка подключения	насосная, от оси 1 – 7650 мм, от оси Д – 2150 мм, отм. −1,200; напорный трубопровод Ду50 (труба 60х3,5 ГОСТ 3262), окончание – кран шаровой Ду50 (поз. 21) с муфтой G2″
Отводимая вода	условно чистая: вода систем пожаротушения при опорожнении и опробовании, утечки в насосной
Режим	напорный, погружные насосы ДН1, ДН2 (поз. 23) Q=10 м³/ч, H=10 м – рабочий и резервный, включение по уровню в приямке
Расход	расчётный 10 м³/ч (2,8 л/с); при аварийном уровне – 20 м³/ч (5,6 л/с)
Напор в точке подключения	не менее 7 м при 10 м³/ч
Разовые объёмы	опорожнение секции В21 – 5,3 м³, В22 – 5,1 м³, сети ВПВ – 2,5 м³, обвязки насосной – 0,9 м³; опорожнение – с расходом не более 10 м³/ч (секция – около 32 мин)
Приямок	1000х1000х800, дно −3,000; регулирующий объём между поплавками «стоп» и «пуск» – 0,3 м³

Задание принял

Раздел	Должность	Фамилия	Подпись	Дата
ВК				

Требования к выполнению

1. Трубопровод от точки подключения до сети и выбор сети приёма – раздел ВК, с учётом того, что вода условно чистая. Ближайшая сеть – отвод К1 ПВХ 110 у перегородки насосной (ДП1-ВК), в 330 мм от точки подключения, ось около −0,950.
2. При сбросе в самотечную сеть предусмотреть гашение напора (колодец-гаситель или разрыв струи) и защиту насосной от подтопления обратным подпором.
3. Обратные клапаны (поз. 26) и краны (поз. 27) на напорных патрубках насосов, кран в точке подключения – в составе раздела ПТ.
4. Трубопроводы прокладывать под балками перекрытия подвала (низ −0,248), над приямком и дренажными насосами – не прокладывать. Проходы К1 и В1 через перегородку насосной (1-го типа) и перекрытие над ней – с заделкой, обеспечивающей предел огнестойкости не ниже EI 45, трубы ПВХ – с противопожарными муфтами.
5. Электроснабжение насосов и шкафа управления ШУД – раздел ЭМ, сигнал «Аварийный уровень» – раздел ПТ.
6. Привязки – от осей здания; размеры – в мм, отметки – в м.

Изм.	Кол.уч	Лист	№ док.	Подп.	Дата
Разраб.					
Пров.					
Н.контр.					
ГИП		Хвостов			10.26

ОПР-01/24/2024-ДП1-ПТ.ЗД2

«Современный коммерческий оптово-продовольственный рынок (ОПР) по адресу: Донецкая область, г. Макеевка, Горняцкий район»

Док-павильон №23, №23.2 Рыба-Мясо. Пожаротушение (ВПВ, АУПТ, АУПП ВРУ)

Стадия	Лист	Листов
Р	1	1

Задание разделу ВК. Отвод воды от дренажных насосов насосной станции

ООО «Технология»

Взам. инв. №

Подп. и дата

Инв. № подл.

Формат А3