Ведомость рабочих чертежей основного комплекта

Лист	Наименование	Примечание
1	Общие данные (начало)	А3
2	Общие данные (окончание). Условные обозначения	А3
3	План наружных сетей В1, К1, К2, Др. М 1:200	А2
4	Профиль сети К1	А3
5	Профили дренажа Др и ливневой сети К2 дома	А2
6	Профили Др и К2 бани. Выпуск в ливневую сеть	А3
7	Профиль ввода В1. Подводка полива КХ-8	А3
8	Колодцы. Узлы и детали	А2

Основные показатели

Показатель	Значение	Примечание
Водопотребление (дом и баня): сутки / секунда	1,26 м³/сут / 0,47 л/с	И05.09.26-ВК.П1; с поливом — 2,16 м³/сут
Требуемый напор в точке подключения В1	38,1 м	НВК.П4; гарантированный — по ТУ
Водоотведение бытовое К1: сутки / секунда	1,26 м³/сут / 1,6 л/с	НВК.П1 (залповый сброс унитаза)
Дождевой сток с кровель (К2)	4,2 л/с	F = 525 м², q20 = 80 л/(с·га), НВК.П2
Регулирующий объем КЛ-1 (Ø1,5)	2,55 м³	макс. уровень 185,91 при дожде 5 мин, НВК.П2
Приток дренажных вод	0,039 л/с	L = 135,8 м, НВК.П3
Протяженность сетей: В1 ПЭ Ø32 / подводка полива Ø25	15,3 / 2,5 м	от выпуска ВК до фундамента
К1 ПП SN8 Ø110 / Ø160	6,5 / 55,9 м	выпуски / сеть бани
К2 ПП SN8 Ø110 / ПЭ Ø63	148,6 / 1,25 м	кольца дома и бани, выпуск КЛ-1
Др перфорированная Ø110 / транзит ПП Ø110	135,8 / 8,2 м	кольцевой дренаж зданий
Колодцы: КК Ø630 / Др Ø315 / КЛ-1 Ø1500 / КП-1 Ø400	3 / 8 / 1 / 1 шт.	и врезка в сущ. ДК5-018

Ведомость ссылочных и прилагаемых документов

Обозначение	Наименование	Примечание
	Ссылочные документы	
ГОСТ Р 21.101-2020	СПДС. Основные требования к проектной и рабочей документации	
ГОСТ 21.704-2011	СПДС. Правила выполнения рабочей документации наружных сетей водоснабжения и канализации	
ГОСТ 21.206-2012	СПДС. Условные обозначения трубопроводов	
ГОСТ 18599-2001	Трубы напорные из полиэтилена. Технические условия	
ГОСТ 32413-2013	Трубы и фасонные части из термопластов для систем наружной канализации	
ГОСТ 8020-2016	Конструкции бетонные и железобетонные для колодцев канализационных, водопроводных и газовых сетей	
ГОСТ 3634-2019	Люки смотровых колодцев и дождеприемники ливнесточных колодцев	
СП 31.13330.2021	Водоснабжение. Наружные сети и сооружения	
СП 32.13330.2018	Канализация. Наружные сети и сооружения	
СП 42.13330.2016	Градостроительство. Планировка и застройка городских и сельских поселений	
СП 45.13330.2017	Земляные сооружения, основания и фундаменты	
СП 129.13330.2019	Наружные сети и сооружения водоснабжения и канализации	
СП 40-102-2000	Проектирование и монтаж трубопроводов систем водоснабжения и канализации из полимерных материалов	
И05.09.26-ВК	Водопровод и канализация дома и бани: ввод В1, выпуски К1-1, К1-б, К2-1, подводка КХ-8	
ГП01 (АР, 19.10.2026)	Схема планировочной организации участка — положение дома и бани	
Топосъемка, ИГИ ООО «ЭККЕР», 08.2026	Топографический план и технический отчет по инженерно-геологическим изысканиям, з/у 19 (КН 50:08:0050209:1600)	
ИС-ЗВК, ИС-ЗКК, ИС-ЗЛК	Поселковые сети водопровода, бытовой и ливневой канализации, д. Исаково (ООО «Лика») — фрагменты	
	Прилагаемые документы	
И05.09.26-НВК.СО	Спецификация оборудования, изделий и материалов	
И05.09.26-НВК.П1	Расчет бытовой канализации К1	
И05.09.26-НВК.П2	Расчет ливневой канализации К2 и колодца КЛ-1	
И05.09.26-НВК.П3	Расчет дренажа Др	
И05.09.26-НВК.П4	Расчет ввода В1. Требуемый напор в точке подключения	
И05.09.26-НВК.ВОР	Ведомость объемов работ (Excel)	

Согласовано

Взам.инв.№

Подпись и дата

Инв.№ подл.

Изм.	Кол.уч	Лист	№ док	Подп.	Дата	И05.09.26-НВК		
						Двухэтажный индивидуальный жилой дом с баней. Московская область, кадастровый номер участка 50:08:0050209:1600		
Разраб.						Наружные сети водопровода и канализации	Стадия	Лист	Листов
Пров.							Р	1	8
Н.контр.						Общие данные (начало)			
ГИП									

Копировал

Формат А3

Общие указания

1. Раздел разработан по заданию Заказчика (наружные сети водопровода и канализации с ливневой сетью и дренажом) на основании раздела И05.09.26-ВК, ГП01, топосъемки и ИГИ ООО «ЭККЕР» (08.2026) и фрагментов поселковых сетей д. Исаково. Граница с ВК — наружная грань фундамента (ввод В1, выпуски К1-1, К1-6, К2-1, подводка КХ-8); стояки внутренних водостоков — ВК (в стенах), их выпуски в кольцо К2 — НВК.

2. Система координат — МСК-50, высот — Балтийская; привязки — от пересечения осей 1/А дома (лист 3). Абсолютные отметки ±0,000 приняты: дом 186,90, баня 186,85; планировка у зданий -0,300 — допущение (п. 13).

3. Подключение: К1 — в существующий дворовый колодец ДК5-018 (выпуск дома — напрямую, баня — сетью Ф160 через КК-1...КК-3); В1 — к выпуску ПЭ Ф32 от ВК217 у юго-восточного угла участка; ливневая сеть К2 и дренаж — через сборный колодец КЛ-1 в выпуск ПЭ Ф63 от ЛК355. Подключение к поселковым сетям выполнять по техническим условиям и с допуском эксплуатирующей организации (ООО «Лика»).

4. Трубы: К1 и К2 — ПП гофрированные SN8 (ГОСТ 32413-2013); Др — ПВХ/ПНД перфорированные Ф110 в фильтре из геотекстиля, транзитные участки — ПП SN8 без перфорации; В1 — ПЭ 100 SDR11 питьевая (ГОСТ 18599-2001). Колодцы КК, Др, КП — полимерные заводской готовности, КЛ-1 — из ж/б колец КС15 (ГОСТ 8020-2016), люки — по ГОСТ 3634-2019: в зоне проезда — тяжелые (Т), на газоне — легкие (Л).

5. Грунты — по ИГИ: подземные воды на глубине 2,3–3,0 м (сезонный подъем до 1,0 м, возможна верховодка), к бетону неагрессивны; нормативная глубина промерзания 1,10 м, грунты сильнопучинистые. Траншеи — с вертикальными стенками в креплении или с откосами по СП 45.13330.2017; при появлении воды — открытый водоотлив. Основание труб — песчаное 100 мм, обсыпка песком 300 мм над трубой.

6. Глубина: В1 — не менее 1,60 м до низа трубы (промерзание + 0,5 м, СП 31.13330.2021), у фундамента — подъем к вводу в скорлупе ППУ с греющим кабелем (ЭОМ); К1, К2 — лоток не выше промерзания - 0,3 м и верх трубы не менее 0,7 м (п. 6.2.4 СП 32.13330.2018), где глубина меньше — утепление ЭППС 50 мм (лист 8, узел 6).

7. Дренаж — кольцевой, под утепленной отмосткой дома и бани, с уклоном 0,005; ливневая сеть К2 — в той же траншее выше дренажа на 0,235 м (лист 8, узел 8). Выпуски стояков водостоков из стен — в кольцо К2 косыми тройниками 45° по привязке воронок (лист 5, узел 9). Дренаж входит в КЛ-1 через обратный клапан.

8. КЛ-1 принимает К2 и дренаж, имеет отстойную часть 0,5 м и регулирующий объем над выпуском: выпуск ПЭ Ф63 пропускает меньше расчетного дождя, излишек копится в колодце (НВК.П2). Чистка КЛ-1 и колодцев Др — весной и осенью.

9. Пересечения: К1 и В1 — над Др и К2, зазор не менее 0,1 м (листы 4–7); расстояния по горизонтали — по табл. 12.6 СП 42.13330.2016 (лист 3). Обратный клапан на К1 не нужен: борта приборов и трапов выше крышки ДК5-018.

10. До начала работ — шурфы у ДК5-018 и у выпусков ВК и ЛК (отметки и назначение выпусков); при расхождении с проектом более 0,10 м — сообщить проектировщику.

11. Испытания — по СП 129.13330.2019: К1, К2 — наполнением водой до засыпки, В1 — гидравлически 1,0 МПа, промывка и дезинфекция перед подключением; дренаж — проливом. Скрытые работы (основание, укладка, утепление, обратная засыпка) — с актами освидетельствования; исполнительная съемка — до засыпки.

12. Оборудование и материалы приняты «или аналог» с характеристиками по НВК.СО; при замене — проверить характеристики и габариты.

13. Приняты без данных Заказчика (подтвердить до начала работ): см. «Допущения» на этом листе. При изменении — уточнить отметки, расчеты и объемы.

Условные обозначения

В1	В1 — водопровод (ввод)
К1	К1 — канализация бытовая
К2	К2 — канализация ливневая
Др	Др — дренаж
К1	Существующие поселковые сети
	Утепление ЭППС (контур)
	Колодец КК, КЛ, КП проектируемый
	Колодец дренажный Др
	Колодец существующий
	Граница ВК / НВК (выпуск, ввод)
	Направление стока
КК-1 / 186,55	Марка колодца / отметка крышки
Ф110, i=0,005	Диаметр и уклон участка

Допущения — подтвердить до начала работ

1. Отметки ±0,000: дом 186,90, баня 186,85; планировка у зданий -0,300, вертикальная планировка участка не выполнялась.

2. Назначение выпусков у юго-восточного угла (какой — водопровод, какой — ливневка), лоток ЛК 185,10 и ось ВК 184,60 — по ИС и топосъемке, без шурфов.

3. Гарантированный напор поселковой сети — нет ТУ; требуется 38,1 м в точке подключения (НВК.П4).

4. Сброс дождевых вод с кровель в поселковую ливневку через выпуск Ф63 — согласовать с ООО «Лика».

5. Места выпусков стояков водостоков — по привязке воронок (выдает Заказчик); на листах — ориентировочно.

6. Автополив участка и водопровод беседки — по ландшафтному проекту; в НВК — колодец КП-1 с краном.

Согласовано

Взам.инв.№

Подпись и дата


Инв.№ подл.

Изм.	Кол.уч	Лист	№ док	Подп.	Дата	И05.09.26-НВК			
						Двухэтажный индивидуальный жилой дом с баней. Московская область, кадастровый номер участка 50:08:0050209:1600			
Разраб.						Наружные сети водопровода и канализации	Стадия	Лист	Листов
Пров.							Р	2	8
Н.контр.						Общие данные (окончание). Условные обозначения			
ГИП									

Копировал

Формат А3

План наружных сетей В1, К1, К2, Др. М 1:200

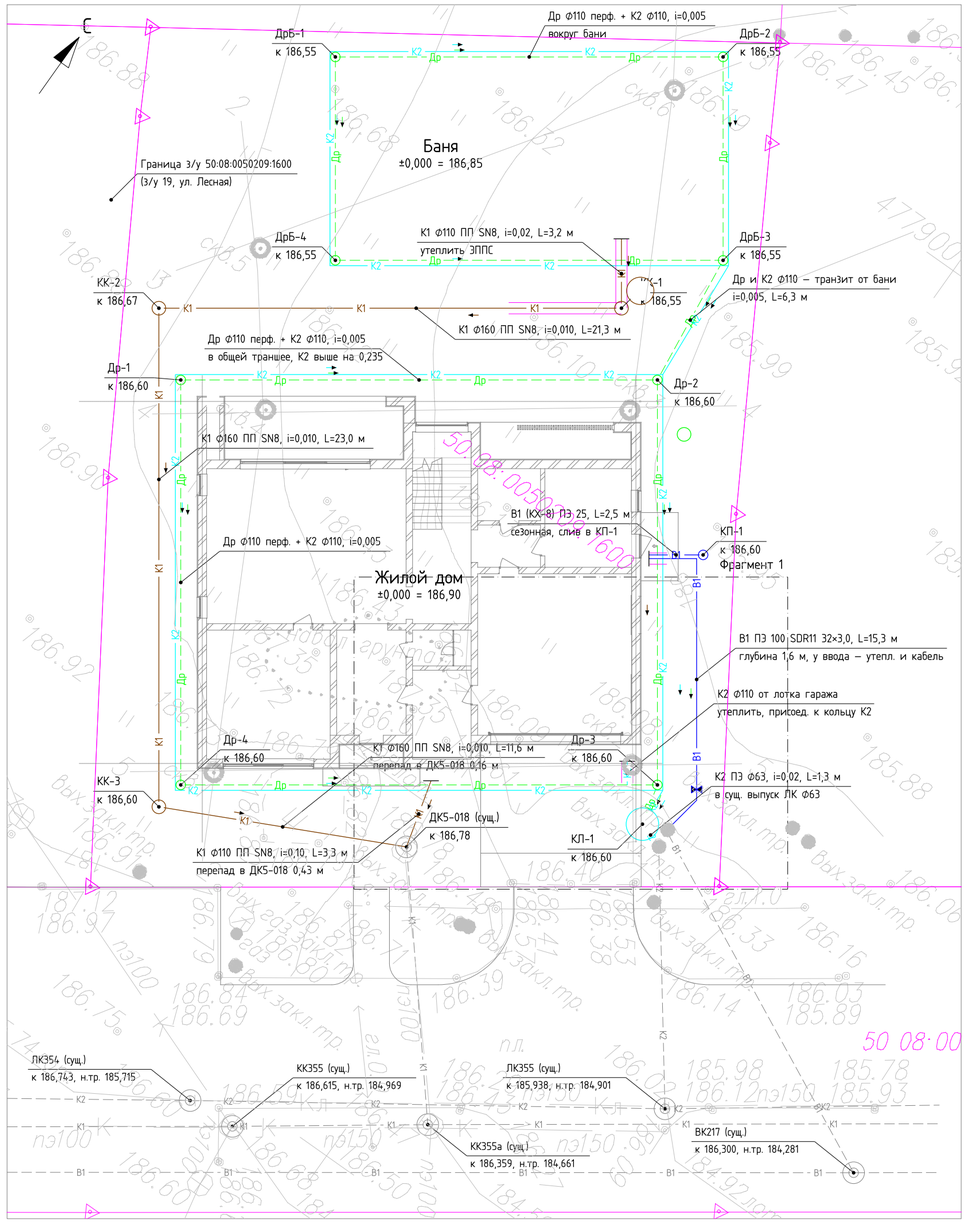

Ведомость колодцев

Колодец	Тип, Ф	X (МСК-50)	Y (МСК-50)	x / y от осей 1/А, м	Крышка	Лоток вх.	Лоток вых.	Глуб., м
ДК5-018	К1, сущ.	477863,74	1352844,79	9,42 / –3,85	186,78	185,41, 185,14	184,98	1,80
КК-1	К1, полим. Ф630	477889,74	1352838,52	19,33 / 21,00	186,55	185,79	185,74	0,81
КК-2	К1, полим. Ф630	477877,42	1352821,11	–2,00 / 21,00	186,67	185,53	185,51	1,16
КК-3	К1, полим. Ф630	477858,65	1352834,40	–2,00 / –2,00	186,60	185,28	185,26	1,34
Др-1	Др, полим. Ф315	477875,30	1352823,85	–0,99 / 17,69	186,60	–	185,39	1,21
Др-2	Др, полим. Ф315	477888,00	1352841,78	20,99 / 17,69	186,60	185,28, 185,29	185,28	1,32
Др-3	Др, полим. Ф315	477872,76	1352852,58	20,99 / –0,99	186,60	185,19, 185,19	185,19	1,41
Др-4	Др, полим. Ф315	477860,05	1352834,64	–0,99 / –0,99	186,60	185,30	185,30	1,30
ДрБ-1	Др, полим. Ф315	477891,58	1352821,05	6,14 / 32,59	186,55	–	185,46	1,09
ДрБ-2	Др, полим. Ф315	477901,91	1352835,65	24,02 / 32,59	186,55	185,37	185,37	1,18
ДрБ-3	Др, полим. Ф315	477894,26	1352841,07	24,02 / 23,21	186,55	185,32, 185,32	185,32	1,23
ДрБ-4	Др, полим. Ф315	477883,92	1352826,47	6,14 / 23,21	186,55	185,41	185,41	1,14
КЛ-1	К2, ж/б Ф1500	477870,88	1352853,06	20,30 / –2,80	186,60	185,18, 185,41	185,12	1,98
КП-1	полив, Ф400	477882,64	1352848,17	23,10 / 9,62	186,60	–	–	0,92


Точки подключения к поселковым сетям (д. Ивково)

Сеть	Точка подключения (сущ.)	Данные ИС / топосъемки	Принято в проекте
К1	ДК5-018 (дворовый колодец з/у)	к 186,750 / 186,78; лоток 185,019 / 184,98	врезка выпусков дома и бани
В1	выпуск ПЭ Ф32 в гильзе Ф63 от ВК217	глубина 1,6–1,8 м (ИС-ЗВК)	ось 184,60 – шурф
К2, Др	выпуск ПЭ Ф63 от ЛК355	глубина 1,0–1,7 м (ИС-ЗЛК)	лоток 185,10 – шурф

Примечания

1. Подложка – топосъемка (ИГИ ООО «ЭККЕР», 08.2026) в осях дома, здания – по ГП01. Отметки абсолютные, Балтийская система. Координаты колодцев – МСК-50 (по границам участка), привязки – от пересечения осей 1/А дома.
2. Абсолютные отметки ±0,000 приняты: дом 186,90, баня 186,85 (наивысшая земля у контура + 0,15); планировка у зданий –0,300. Вертикальная планировка не выполнялась – до начала работ подтвердить отметки ±0,000.
3. Положение и отметки выпусков ВК и ЛК у юго-восточного угла участка и лотка ДК5-018 уточнить шурфованием до начала работ; при расхождении более 0,10 м – сообщить проектировщику.
4. К1 – ПП SN8: выпуски Ф110, дворовая сеть бани Ф160 с уклоном 0,010 (П1). Колодцы КК – полимерные Ф630 с лотком и телескопической шахтой, люк легкий; в зоне проезда – люк тяжелый (Т).
5. Др – перфорированная труба Ф110 в геотекстиле в щебне 20–40 под утепленной отмосткой зданий, колодцы Ф315; К2 – ПП SN8 Ф110 в той же траншее выше дренажа на 0,235 м. Выпуски К2 из стен (стояки внутренних водостоков) присоединяются к кольцу К2 косыми тройниками – места по привязке воронок.
6. Дренаж и К2 – в КЛ-1 (ж/б Ф1500, отстойная часть 0,5 м, регулирующий объем – П2), дренаж – через обратный клапан; выпуск КЛ-1 → существующий выпуск ЛК Ф63.
7. Утепление – плиты ЭППС 50 мм шириной 1,2 м над трубой на участках, где глубина меньше нормы (п. 6.2.4 СП 32.13330.2018); В1 у ввода – в скорлупе ППУ с греющим кабелем (лист 8, узел 1).
8. Пересечения: К1 – над Др и К2, В1 и КК-8 у дома – над Др и К2; зазоры – не менее 0,1 м (листы 4–7). Расстояния по горизонтали: В1 – К2 1,56 м, К1 – Др 1,0 м (табл. 12.6 СП 42.13330.2016).

Фрагмент 1. Южная часть участка. М 1:100

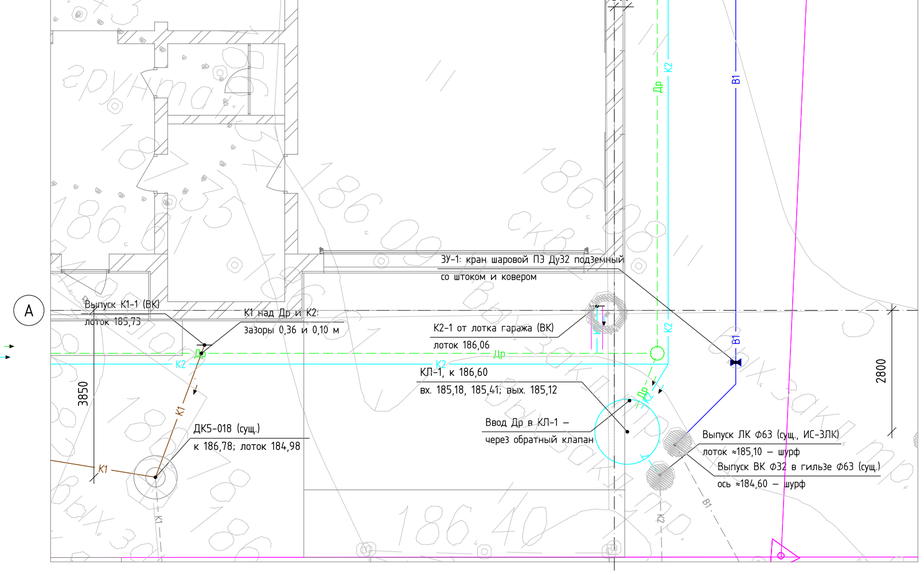

Условные обозначения

- К1 — бытовая канализация (проект)
- К2 — ливневая канализация
- Др — дренаж
- В1 — водопровод
- К1 — существующие поселковые сети
- утепление ЭППС (контур)
- колодец проектируемый
- колодец существующий
- граница ВК / НВК (выпуск, ввод)
- направление стока

Изм.	Кол.уч	Лист	№ док	Подп.	Дата	И05.09.26-НВК			
						Двухэтажный индивидуальный жилой дом с баней. Московская область, кадастровый номер участка 50:08:0050209:1600			
Разраб.						Наружные сети водопровода и канализации	Стадия	Лист	Листов
Пров.							Р	3	8
Н.контр.						План наружных сетей В1, К1, К2, Др. М 1:200			
ГИП									

Согласовано

Взам.инв.№


Подпись и дата

Инв.№ подл.

Копировал

Формат А2


Профиль сети К1: выпуск бани → КК-1 → КК-2 → КК-3 → ДК5-018. Масштабы: гор. 1:200, верт. 1:50

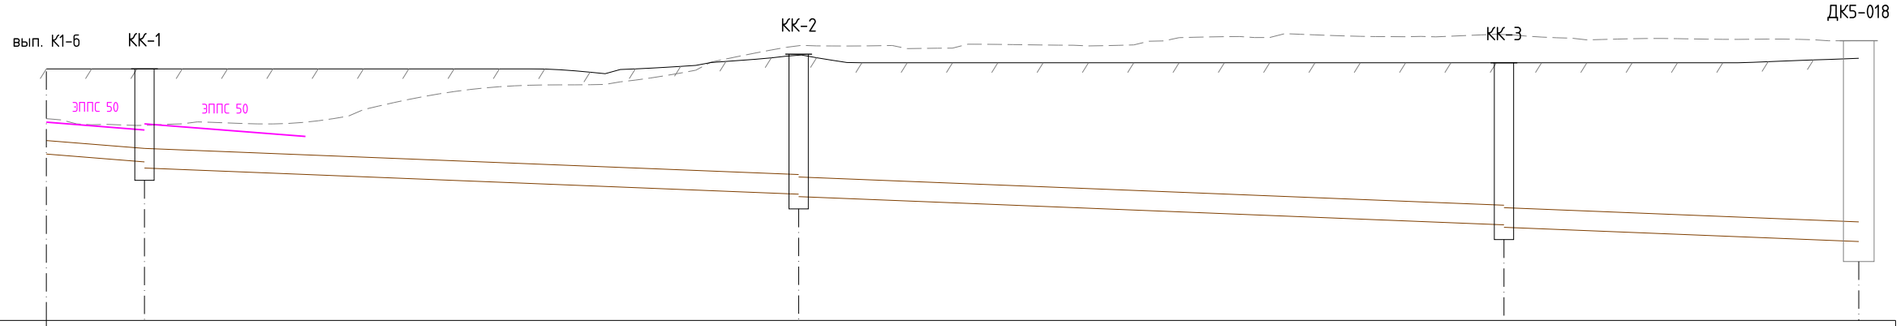

Усл. горизонт 184,50

Материал, диаметр, основание	ПП SN8: Ф110 до КК-1, далее Ф160; песчаное основание 100 мм, обсыпка 300 мм				
Отметка земли проектная	186,55	186,55	186,67	186,60	186,64
Отметка земли фактическая	186,14	186,09	186,74	186,83	186,78
Отметка лотка трубы	185,86	185,79 / 185,74	185,53 / 185,51	185,28 / 185,26	185,14 / 184,98
Глубина заложения лотка	0,69	0,81	1,16	1,34	1,66
Уклон, ‰ / длина, м	20 / 3,20	10 / 21,33	10 / 23,00	10 / 11,57	
Расстояние, м	3,20	21,33	23,00	11,57	
Колодец (точка)	вып. К1-б	КК-1	КК-2	КК-3	ДК5-018

Выпуск дома К1-1 → ДК5-018. Гор. 1:50, верт. 1:50

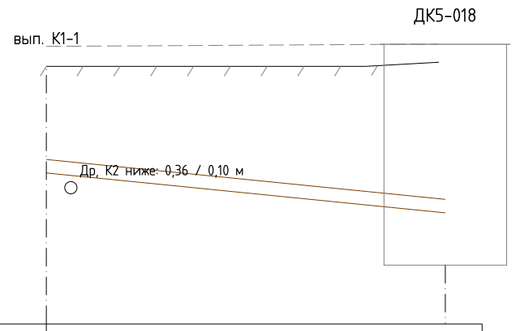

Усл. горизонт 184,50

Материал, диаметр, основание	ПП SN8 Ф110	
Отметка земли проектная	186,60	186,64
Отметка земли фактическая	186,76	186,78
Отметка лотка трубы	185,73	184,98 / 185,41
Глубина заложения лотка	0,87	1,66
Уклон, ‰ / длина, м	100 / 3,25	
Расстояние, м	3,25	
Колодец (точка)	вып. К1-1	ДК5-018

Примечания

1. Отметки – абсолютные (Балтийская система). Земля проектная – планировка у зданий −0,300 (дом 186,60, баня 186,55) с сопряжением на 3 м; фактическая – по топосъемке.
2. Входы в ДК5-018: выпуск дома – с перепадом 0,43 м, сеть бани – 0,16 м (по лотку-водосливу). Врезка в существующий колодец – через герметичные проходы (манжеты), по месту.
3. Колодцы КК-1…КК-3 – полимерные Ф630 с проточным лотком, шахтой и люком; дно – на песчаном основании 200 мм. Участки, где глубина меньше нормы (п. 6.2.4 СП 32.13330.2018), – с утеплением ЭППС 50 мм.
4. До начала работ – шурф у ДК5-018: проверить отметку лотка (184,98 по съемке, 185,019 по ИС).

Согласовано

Взам.инв.№

Подпись и дата


Инв.№ подл.

Изм.	Кол.уч	Лист	№ док	Подп.	Дата	И05.09.26-НВК			
						Двухэтажный индивидуальный жилой дом с баней. Московская область, кадастровый номер участка 50:08:0050209:1600			
Разраб.						Наружные сети водопровода и канализации	Стадия	Лист	Листов
Пров.							Р	4	8
Н.контр.						Профиль сети К1			
ГИП									

Копировал

Формат А3


Профиль Др и К2 дома, ветвь А: Др-1 → Др-2 → Др-3 → КЛ-1 (север и восток). Гор. 1:200, верт. 1:50

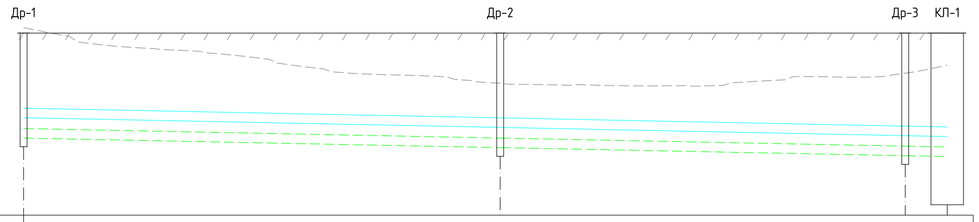

Усл. горизонт 184,50

Материал, диаметр, основание	Др – перфор. Ф110 в геотекстиле в щебне; К2 – ПП SN8 Ф110; общая траншея			
Отметка земли проектная	186,60	186,60	186,60	186,60
Отметка земли фактическая	186,66	186,02	186,14	186,23
Отметка лотка К2	185,52	185,51	185,42	185,41
Отметка лотка Др	185,39	185,28	185,19	185,18
Глубина заложения Др	1,21	1,32	1,41	1,42
Уклон, ‰ / длина, м	5 / 21,98	5 / 18,68	5/94	
Расстояние, м	21,98	18,68	1,94	
Колодец (точка)	Др-1	Др-2	Др-3	КЛ-1

Профиль Др и К2 дома, ветвь Б: Др-1 → Др-4 → Др-3 (запад и юг). Гор. 1:200, верт. 1:50

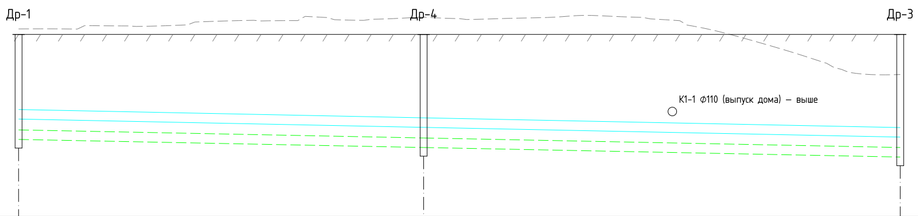

Усл. горизонт 184,50


Материал, диаметр, основание	Др – перфор. Ф110 в геотекстиле в щебне; К2 – ПП SN8 Ф110; общая траншея		
Отметка земли проектная	186,60	186,60	186,60
Отметка земли фактическая	186,66	186,80	186,14
Отметка лотка К2	185,52	185,53	185,42
Отметка лотка Др	185,39	185,30	185,19
Глубина заложения Др	1,21	1,30	1,41
Уклон, ‰ / длина, м	5 / 18,68	5 / 21,98	
Расстояние, м	18,68	21,98	
Колодец (точка)	Др-1	Др-4	Др-3

Примечания

1. Дренаж и К2 – в одной траншее: К2 снаружи и выше дренажа на 0,235 м, у колодцев Др – обход по месту; выходы К2 и Др расходятся по высоте (узел 8).
2. Дренаж – под утепленной отмосткой здания (ЭППС по КР/АР), промерзание не учитывается.
3. Выпуски К2 из стен (стояки внутренних водостоков) – косыми тройниками 45° в кольцо К2 по привязке воронок (выдает Заказчик), узел 9.
4. Колодцы Др – полимерные Ф315 с отстойной частью 0,3 м и крышкой; промывка – через них.


Узел 8. Траншея дренажа Др и ливневой К2 у здания

М 1:20 (разрез поперек трассы)

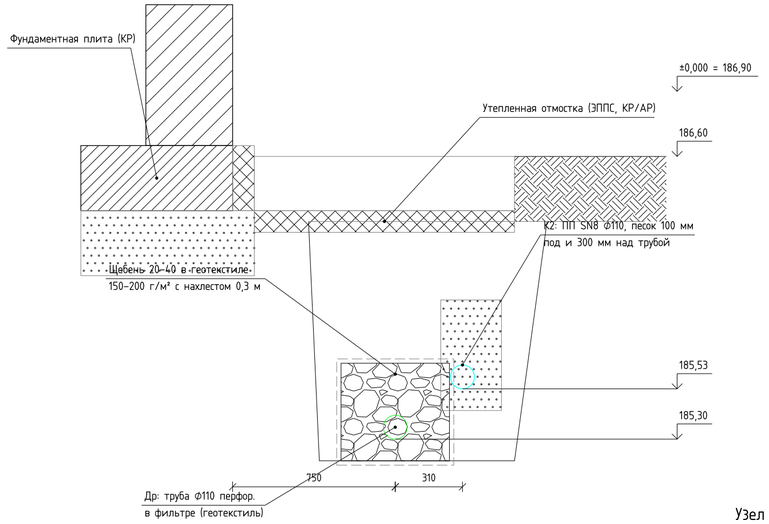

Узел 9. Стояк внутреннего водостока → кольцо К2

М 1:20, схема

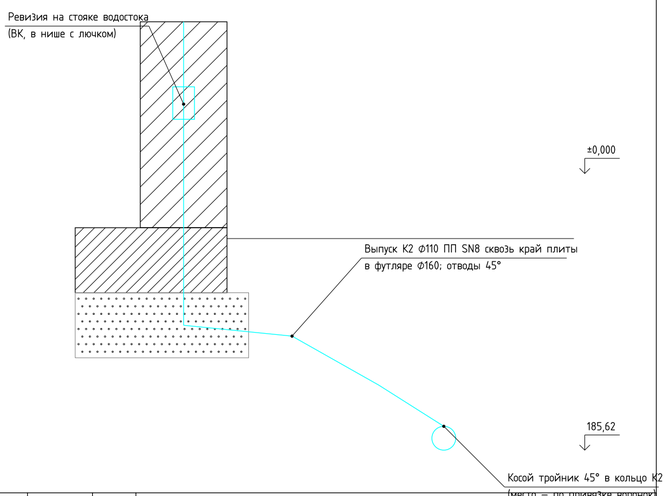

Изм.	Кол.уч	Лист	№ док	Подп.	Дата	И05.09.26-НВК			
						Двухэтажный индивидуальный жилой дом с баней. Московская область, кадастровый номер участка 50:08:0050209:1600			
Разраб.						Наружные сети водопровода и канализации	Стадия	Лист	Листов
Пров.							Р	5	8
Н.контр.						Профили дренажа Др и ливневой сети К2 дома			
ГИП									

Согласовано

Взам.инв.№


Подпись и дата

Инв.№ подл.

Копировал

Формат А2


Профиль Др и К2 бани, ветвь А и транзит: ДрБ-1 → ДрБ-2 → ДрБ-3 → Др-2. Гор. 1:200, верт. 1:50

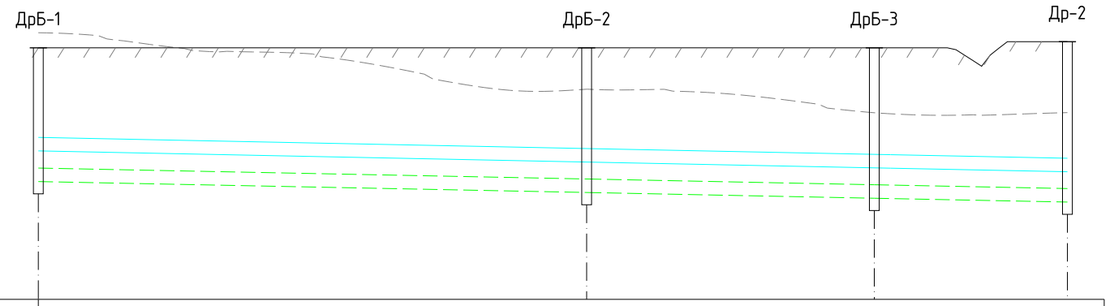

Усл. горизонт 184,50

Материал, диаметр, основание	Др – перфор. Ф110 (транзит – ПП SN8 без перфорации); К2 – ПП SN8 Ф110			
Отметка земли проектная	186,55	186,55	186,55	186,60
Отметка земли фактическая	186,67	186,21	186,02	186,02
Отметка лотка К2	185,71	185,62	185,57	185,54
Отметка лотка Др	185,46	185,37	185,32	185,29
Глубина заложения Др	1,09	1,18	1,23	1,31
Уклон, ‰ / длина, м	5 / 17,88	5 / 9,38	5 / 6,30	
Расстояние, м	17,88	9,38	6,30	
Колодец (точка)	ДрБ-1	ДрБ-2	ДрБ-3	Др-2


Профиль Др и К2 бани, ветвь Б: ДрБ-1 → ДрБ-4 → ДрБ-3. Гор. 1:200, верт. 1:50

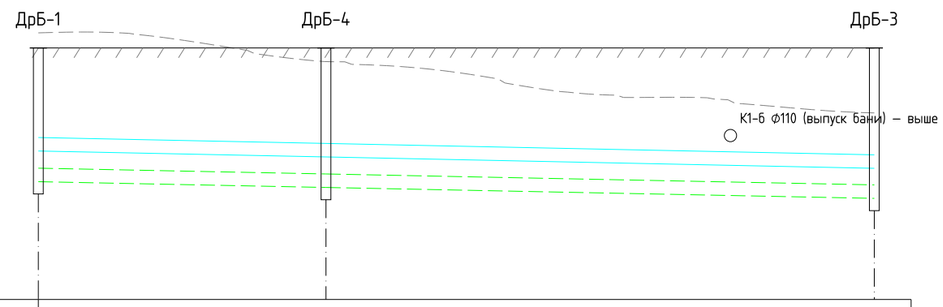

Усл. горизонт 184,50

Материал, диаметр, основание	Др – перфор. Ф110 в геотекстиле в щебне; К2 – ПП SN8 Ф110; общая траншея		
Отметка земли проектная	186,55	186,55	186,55
Отметка земли фактическая	186,67	186,44	186,02
Отметка лотка К2	185,71	185,66	185,57
Отметка лотка Др	185,46	185,41	185,32
Глубина заложения Др	1,09	1,14	1,23
Уклон, ‰ / длина, м	5 / 9,38	5 / 17,88	
Расстояние, м	9,38	17,88	
Колодец (точка)	ДрБ-1	ДрБ-4	ДрБ-3

КЛ-1 → выпуск ЛК Ф63. Гор. 1:50, верт. 1:50

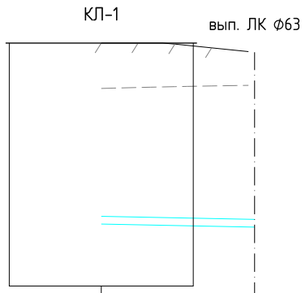

Усл. горизонт 184,50

Материал, диаметр, основание	ПЭ 100 SDR17 63×3,8	
Отметка земли проектная	186,60	186,53
Отметка земли фактическая	186,23	186,26
Отметка лотка трубы	185,12	185,10
Глубина заложения лотка	1,47	1,43
Уклон, ‰ / длина, м	20 / 1,25	
Расстояние, м	1,25	
Колодец (точка)	КЛ-1	вып. ЛК Ф63

Изм.	Кол.уч	Лист	№ док	Подп.	Дата			
Разраб.						И05.09.26-НВК		
Пров.						Двухэтажный индивидуальный жилой дом с баней. Московская область, кадастровый номер участка 50:08:0050209:1600		
Н.контр.						Наружные сети водопровода и канализации	Стадия: Р	Лист: 6 / Листов: 8
ГИП						Профили Др и К2 бани. Выпуск в ливневую сеть		

Согласовано

Взам.инв.№


Подпись и дата

Инв.№ подл.

Копировал

Формат А3


Профиль ввода В1: выпуск ВК ф32 → ЗУ-1 → ввод в 1.6. Гор. 1:100, верт. 1:50

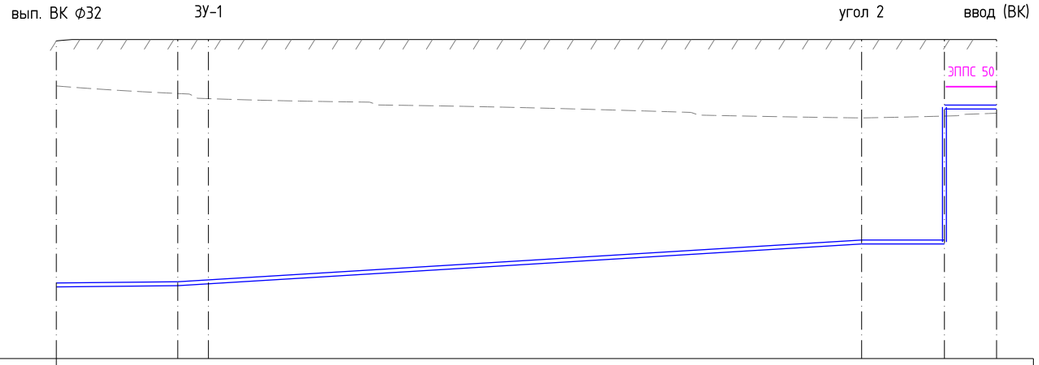

Усл. горизонт 184,00

Материал, диаметр, основание	ПЭ 100 SDR11 32×3,0 питьевая, на песчаном основании 100 мм						
Отметка земли проектная	186,59	186,60	186,60	186,60	186,60	186,60	
Отметка земли фактическая	186,22	186,16	186,12	185,96	185,98	186,00	
Отметка оси трубы	184,60	184,61	184,63	184,95	184,95 / 186,05	186,05	
Глубина до низа трубы	1,99	1,99	1,97	1,65	1,65	0,55	
Уклон, ‰ / длина, м	5 / 1,98	30 / 0,50	30 / 10,65	0 / 1,35	0 / 0,85		
Расстояние, м	1,98	0,50	10,65	1,35	0,85		
Колодец (точка)	вып. ВК ф32	угол 1	ЗУ-1	угол 2	подъем	ввод (ВК)	

Подводка полива КХ-8 → КП-1. Гор. 1:50, верт. 1:50

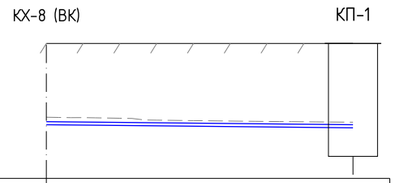

Усл. горизонт 185,50

Материал, диаметр, основание	ПЭ 100 SDR11 25×2,3	
Отметка земли проектная	186,60	186,60
Отметка земли фактическая	186,00	185,96
Отметка оси трубы	185,95	185,93
Глубина до низа трубы	0,65	0,67
Уклон, ‰ / длина, м	10 / 2,50	
Расстояние, м	2,50	
Колодец (точка)	КХ-8 (ВК)	КП-1

Примечания

1. Глубина ввода – не менее 1,60 м до низа трубы (промерзание 1,10 + 0,5 м, п. 11.40 СП 31.13330.2021); у фундамента – подъем к вводу на −0,850 в скорлупе ППУ 40 мм с греющим кабелем 10 Вт/м (лист 8, узел 1).
2. Под крыльцом 1.6 – в футляре ПНД ф110 (L = 2,0 м).
3. Перед засыпкой – гидравлическое испытание 1,5 Рраб, но не менее 1,0 МПа (СП 129.13330.2019), промывка и дезинфекция.
4. Подводка полива КХ-8 – сезонная, с уклоном 0,01 к КП-1; на зиму – перекрыть кран КХ-8 в 1.6 и открыть спускной кран в КП-1.
5. Требуемый напор в точке подключения – 38,1 м (П4); гарантированный напор поселковой сети – по ТУ (запросить у эксплуатирующей организации).

Согласовано

Взам.инв.№

Подпись и дата

Инв.№ подл.


Изм.	Кол.уч	Лист	№ док	Подп.	Дата	И05.09.26-НВК			
						Двухэтажный индивидуальный жилой дом с баней. Московская область, кадастровый номер участка 50:08:0050209:1600			
Разраб.						Наружные сети водопровода и канализации	Стадия	Лист	Листов
Пров.							Р	7	8
Н.контр.						Профиль ввода В1. Подводка полива КХ-8			
ГИП									

Копировал

Формат А3


Узел 1. Ввод В1 у фундамента топочной 1.6

М 1:25

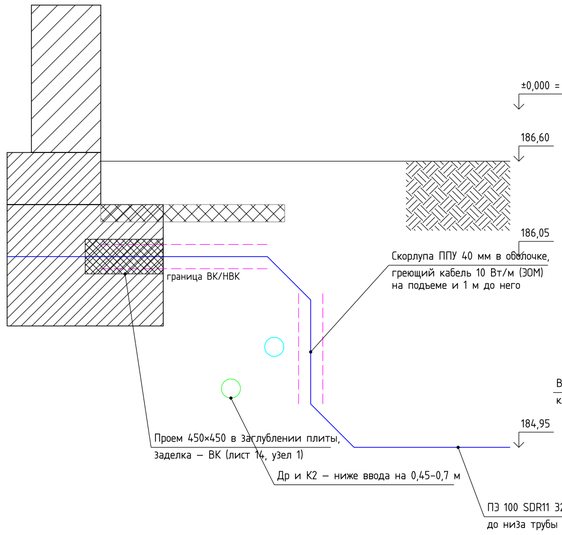


Узел 2. Колодец КЛ-1 (сборный К2 и Др)

М 1:25

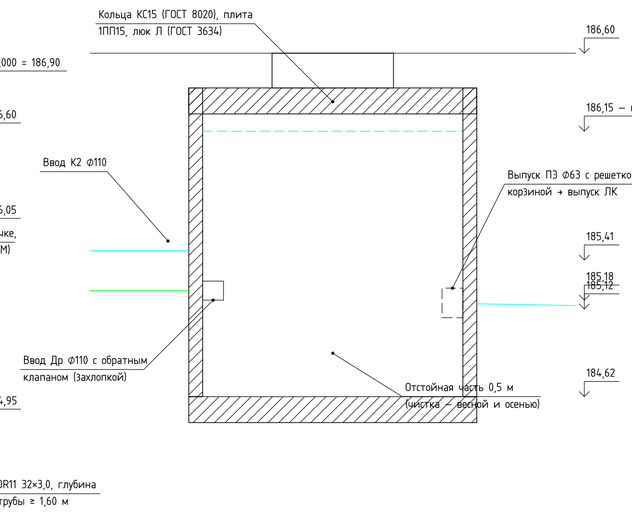


Узел 3. Врезка выпусков в ДК5-018 (сущ.)

М 1:25

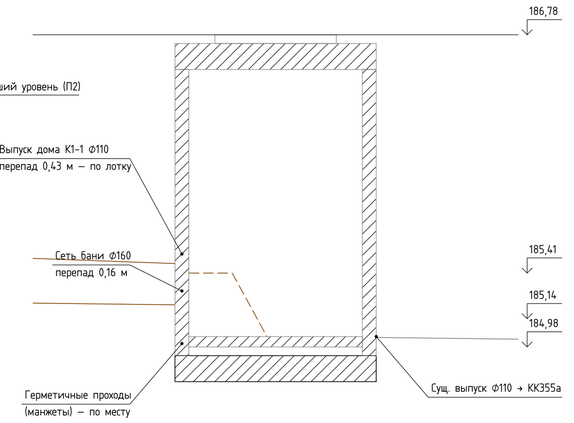


Узел 4. Колодец К1 полимерный Ф630 (КК-1…КК-3)

М 1:20; отметки — КК-2

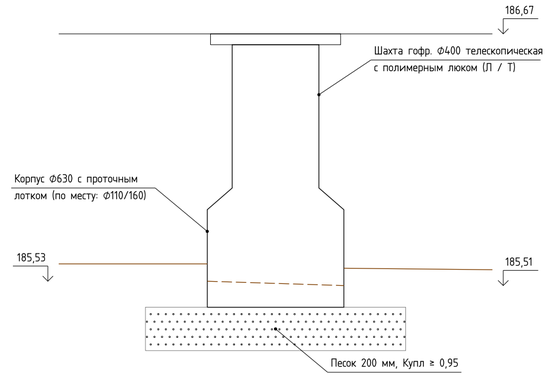


Узел 5. Колодец дренажный Ф315 (Др, ДрБ)

М 1:20; отметки — Др-4

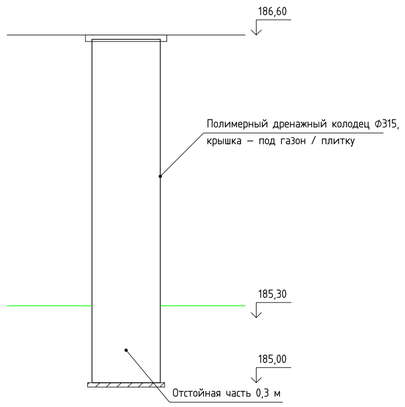


Узел 6. Утепление трубы при малой глубине

М 1:20; К1-6 у КК-1

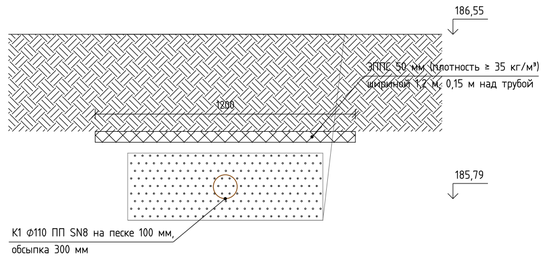

Узел 7. Колодец полива КП-1 (Ф400)

М 1:10

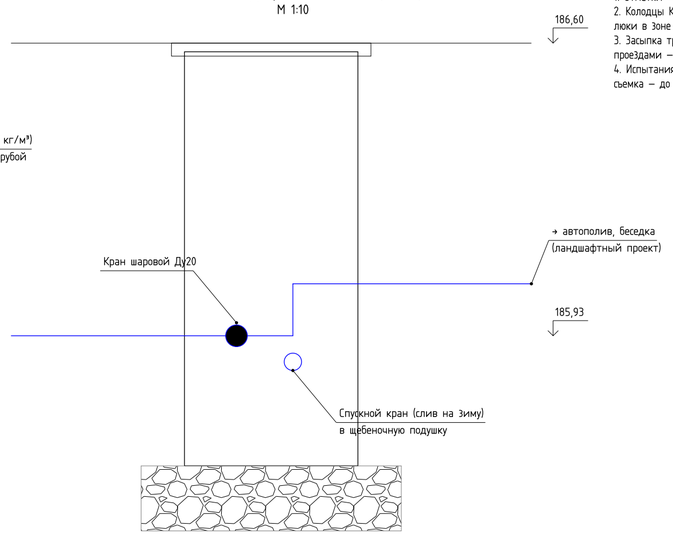

Примечания

1. Отметки — абсолютные (Балтийская система), ±0,000 дома 186,90, бани 186,85 — допущение (лист 1).
2. Колодцы КК, Др, КП — полимерные Заводской готовности; КЛ-1 — из ж/б колец КС15 с наружной гидроизоляцией битумной мастикой; люки в зоне проезда — тяжелые (Т).
3. Засыпка траншей: над трубами — песок 300 мм с ручным уплотнением, выше — местный грунт без камней слоями 0,2–0,3 м; под проездами — песок на всю глубину, Купл ≥ 0,95.
4. Испытания: К1 и К2 — наполнением (п. 7 СП 129.13330.2019), В1 — гидравлически 1,0 МПа, дренаж — проливом; исполнительная съемка — до засыпки.

Согласовано

Взам.инв.№

Подпись и дата

Инв.№ подл.

						И05.09.26-НВК	
						Двухэтажный индивидуальный жилой дом с баней. Московская область, кадастровый номер участка 50:08:0050209:1600	
Изм.	Кол.уч	Лист	№ док	Подп.	Дата		
Разраб.						Наружные сети водопровода и канализации	Стадия: Р; Лист: 8; Листов: 8
Пров.							
Н.контр.						Колодцы. Узлы и детали	
ГИП							

Копировал

Формат А2

Поз.	Наименование и техническая характеристика	Тип, марка, обозначение документа, опросного листа	Код продукции	Поставщик	Ед. измерения	Количество	Масса 1 ед., кг	Примечание
1	2	3	4	5	6	7	8	9
	1. Водопровод В1 (ввод) и подводка полива КХ-8							
1	Труба напорная ПЭ 100 SDR11 32×3,0 питьевая	ГОСТ 18599-2001			м	17		В1-н, ввод от выпуска ВК217 до фундамента 1.6
2	Труба напорная ПЭ 100 SDR11 25×2,3 питьевая	ГОСТ 18599-2001			м	3		КХ-8н, подводка полива до КП-1
3	Муфта электросварная ПЭ 100 SDR11 Ø32	или аналог			шт.	2		стык с выпуском ВК (после шурфа) и с вводом ВК у фундамента
4	Отвод электросварной ПЭ 100 Ø32, 90°	или аналог			шт.	3		подъём к вводу (2), поворот у дома (1); повороты 45° — изгибом трубы, R ≥ 0,8 м
5	Кран шаровой подземный ПЭ 100 Ø32 (Ду 25) под приварку, с телескопическим штоком	или аналог			шт.	1		на вводе у участка (лист 3)
6	Ковер малый с бетонной подушкой — для штока подземного крана	или аналог			шт.	1		
7	Футляр из трубы ПНД Ø110, L = 2,0 м, с центраторами и заглушками торцов	или аналог			шт.	1		В1 под крыльцом 1.6 (лист 7)
8	Скорлупа ППУ 40 мм в защитной оболочке для трубы Ø32	или аналог			м	4		подъём к вводу и 1 м до него (лист 8, узел 1)
9	Кабель нагревательный саморегулирующийся 10 Вт/м с концевой муфтой и холодным концом	или аналог			м	4		под скорлупой ППУ; подключение и терморегулятор — ЭОМ
10	Муфта компрессионная ПЭ 25 × наружная резьба ¾"	или аналог			шт.	2		стык с КХ-8 (ВК) у фундамента, вход в кран КП-1
11	Колодец полимерный Ø400 с крышкой (газонный), H ≈ 0,92 м	или аналог			шт.	1		КП-1 (лист 8, узел 7)
12	Кран шаровой Ду 20 латунный с полусгоном для шланга	или аналог			шт.	1		КП-1: полив, беседка
13	Кран шаровой спускной Ду 15	или аналог			шт.	1		КП-1: слив на зиму
14	Лента сигнальная «Осторожно! Водопровод»	или аналог			м	20		
	2. Канализация бытовая К1							
15	Труба ПП гофрированная двухслойная SN8 Ø110 с раструбом и уплотнительным кольцом	ГОСТ 32413-2013			м	8		выпуски К1-1н, К1-бн
16	Труба ПП гофрированная двухслойная SN8 Ø160 с раструбом и уплотнительным кольцом	ГОСТ 32413-2013			м	62		сеть бани К1-б1…К1-б3
17	Отвод ПП Ø110, 15°	или аналог			шт.	1		стык с выпуском К1-1 (ВК), угол — по месту
18	Колодец канализационный полимерный Ø630 с проточным лотком (приём Ø110, выход Ø160), шахтой гофр. Ø400 телескопической и люком, H = 0,81 м	или аналог			шт.	1		КК-1 (лист 8, узел 4)
19	Колодец канализационный полимерный Ø630 с проточным лотком (проход Ø160, поворот 90°), шахтой гофр. Ø400 телескопической и люком, H = 1,16 м	или аналог			шт.	1		КК-2 (лист 8, узел 4)
20	Колодец канализационный полимерный Ø630 с проточным лотком (проход Ø160, поворот 81°), шахтой гофр. Ø400 телескопической и люком, H = 1,34 м	или аналог			шт.	1		КК-3 (лист 8, узел 4)

Взам.инв№

Подпись и дата

Инв№ подл.

Изм.	Кол.уч	Лист	№ док	Подп.	Дата
Разраб.					
Пров.					
Н.контр.					
ГИП					

И05.09.26-НВК.СО

Двухэтажный индивидуальный жилой дом с баней. Московская область, кадастровый номер участка 50:08:0050209:1600

Наружные сети водопровода и канализации

Стадия	Лист	Листов
Р	1	3

Спецификация оборудования, изделий и материалов

Формат А3

Поз.	Наименование и техническая характеристика	Тип, марка, обозначение документа, опросного листа	Код продукции	Поставщик	Ед. измерения	Количество	Масса 1 ед., кг	Примечание
1	2	3	4	5	6	7	8	9
21	Уплотнитель (манжета) для ввода трубы в стенку ж/б колодца Ø110	или аналог			шт.	1		врезка К1-1н в ДК5-018 (узел 3)
22	Уплотнитель (манжета) для ввода трубы в стенку ж/б колодца Ø160	или аналог			шт.	1		врезка К1-б3 в ДК5-018 (узел 3)
23	Лента сигнальная «Осторожно! Канализация»	или аналог			м	69		
	3. Канализация ливневая К2. Сборный колодец КЛ-1							
24	Труба ПП гофрированная двухслойная SN8 Ø110 с раструбом и уплотнительным кольцом	ГОСТ 32413-2013			м	164		кольца К2 дома и бани, транзит, выпуск лотка гаража
25	Труба напорная ПЭ 100 SDR17 63×3,8	ГОСТ 18599-2001			м	2		выпуск КЛ-1 → выпуск ЛК Ø63
26	Муфта электросварная ПЭ 100 Ø63	или аналог			шт.	1		стык с выпуском ЛК (после шурфа)
27	Отвод ПП Ø110, 45°	или аналог			шт.	36		углы колец (по 2 на угол), транзит, выпуск гаража; выпуски водостоков — по 2
28	Тройник ПП Ø110, 90°	или аналог			шт.	3		слияние полуколец, приём транзита бани
29	Тройник ПП Ø110 косой 45°	или аналог			шт.	9		выпуски водостоков (8, ориентировочно — по привязке воронок) и лотка гаража
30	Футляр (гильза) из трубы ПП Ø160, L = 0,6 м — закладная в край плиты	или аналог			шт.	8		выпуски водостоков (узел 9), ориентировочно; закладка — при бетонировании (КР)
31	Плита днища ПН15	ГОСТ 8020-2016			шт.	1		КЛ-1 (лист 8, узел 2)
32	Кольцо стеновое КС15.9	ГОСТ 8020-2016			шт.	1		КЛ-1
33	Кольцо стеновое КС15.6	ГОСТ 8020-2016			шт.	1		КЛ-1
34	Плита перекрытия 1ПП15-1	ГОСТ 8020-2016			шт.	1		КЛ-1
35	Кольцо стеновое КС7.3 (горловина)	ГОСТ 8020-2016			шт.	1		КЛ-1
36	Люк чугунный лёгкий Л (А15)	ГОСТ 3634-2019			шт.	1		КЛ-1; в зоне проезда — Т (С250)
37	Скобы ходовые	ГОСТ 8020-2016			шт.	4		КЛ-1, шаг 0,3 м
38	Мастика битумная для наружной гидроизоляции колец, 2 слоя	или аналог			м²	13		КЛ-1, наружная поверхность
39	Уплотнитель (манжета) для ввода трубы в стенку ж/б колодца Ø110	или аналог			шт.	2		КЛ-1: К2-К, Др-К
40	Уплотнитель (манжета) для ввода трубы в стенку ж/б колодца Ø63	или аналог			шт.	1		КЛ-1: выпуск
41	Клапан обратный канализационный (захлопка) Ø110	или аналог			шт.	1		КЛ-1: вход дренажа Др-К
42	Решётка-корзина из нержавеющей стали на входе выпуска Ø63	или аналог			шт.	1		КЛ-1
	4. Дренаж Др							
43	Труба дренажная гофрированная перфорированная Ø110 в фильтре из геотекстиля	ГОСТ Р 59249-2020 или ТУ изготовителя			м	150		кольца дренажа дома и бани
44	Труба ПП гофрированная двухслойная SN8 Ø110 (без перфорации)	ГОСТ 32413-2013			м	10		транзит Др-Т, выход Др-К в КЛ-1

Взам.инв.№

Подпись и дата

Инв.№ подл.

Поз.	Наименование и техническая характеристика	Тип, марка, обозначение документа, опросного листа	Код продукции	Поставщик	Ед. измерения	Количество	Масса 1 ед., кг	Примечание
1	2	3	4	5	6	7	8	9
45	Колодец дренажный полимерный: шахта гофр. Ø315, днище, крышка	или аналог			шт.	8		Др-1…Др-4, ДрБ-1…ДрБ-4 (лист 8, узел 5)
46	Труба гофрированная Ø315 для шахт дренажных колодцев	или аналог			м	14		H = 1,39…1,71 м, отстойная часть 0,3 м
47	Уплотнитель резиновый для ввода трубы Ø110 в колодец Ø315	или аналог			шт.	19		
	5. Материалы траншей и утепление							
48	Песок средней крупности для основания и обсыпки труб и колодцев	ГОСТ 8736-2014			м³	56.5		основание 100 мм, обсыпка 300 мм над трубой
49	Щебень гранитный фракции 20–40 мм, промытый	ГОСТ 8267-93			м³	33.0		призма вокруг дренажа (узел 8), основание КЛ-1
50	Геотекстиль иглопробивной 150–200 г/м²	или аналог			м²	360		обёртка щебня, нахлёст 0,3 м
51	Плиты ЭППС 50 мм, плотность не менее 35 кг/м³	или аналог			м²	13		полоса 1,2 м над трубой на мелких участках (узел 6)
	6. Не входит в НВК.СО							
52	Стояки внутренних водостоков в стенах, выпуски К1, ввод В1 и подводка КХ-8 до наружной грани фундамента, лоток гаража ЛГ-1 с пескоуловителем — И05.09.26-ВК.СО							
53	Утеплённая отмостка, утепление торца плиты, футляры в фундаменте — КР/АР							
54	Терморегулятор и питание греющего кабеля — ЭОМ							
55	Автополив участка и водопровод беседки от КП-1 — по ландшафтному проекту							

Примечание — Допускается применение оборудования, изделий и материалов других изготовителей с техническими характеристиками не ниже указанных в настоящей спецификации.

Взам.инв.№

Подпись и дата

Инв.№ подл.

Изм.	Кол.уч	Лист	№ док.	Подп.	Дата	И05.09.26-НВК.СО	Лист 3

Формат А3