
Эскизный проект

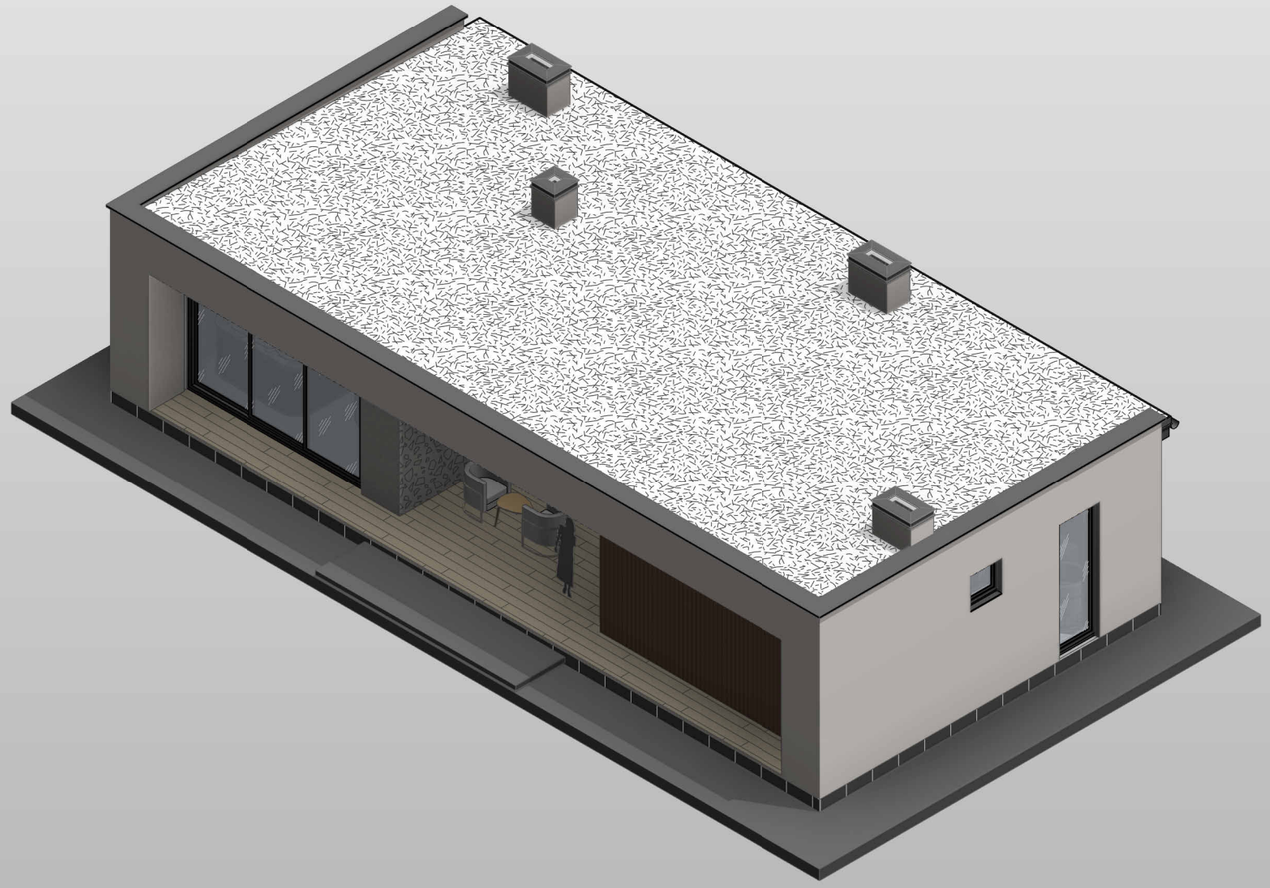

Двухэтажный индивидуальный жилой дом с баней.
Альбом 2. Эскизный проект бани.

Заказчик _____

Подрядчик

Руководитель Иванова Е.С.
Архитектор Харламов П.А.
Архитектор Райтер С.С.

Москва
2026

Ведомость рабочих чертежей1	
Номер листа	Имя листа
1. Альбом	
0	Титульный лист
1	Пояснительная записка
2	Привязка дома и бани на участке
3	Схема благоустройства
4	Баня.Планировочное решение
5	Баня.Планировочное решение. Размеры.
6	Баня. План кровли.
7	Баня. Разрез 1-1, 2-2
8	Баня. Фасад 1-4, 4-1
9	Баня. Фасад А-В, В-А
10	Баня. 3D Вид 1
11	Баня. 3D Вид 2
12	Баня. 3D Вид 3
13	Баня. 3D Вид 4
14	Визуализация
15	Визуализация
16	Визуализация

Экспликация помещений		
№	Наименование	S, м^2
1	Терраса	20,71
2	Прихожая	6,30
3	С/у	4,57
4	Раздевалка	5,49
5	Спальня	12,75
6	Комната отдыха	21,42
7	Помывочная	22,16
8	Парная	8,44
Общая площадь		101,84

Пояснительная записка
Кадастровый номер участка: 50:08:0050209:1600
На участке предполагается расположение двухэтажного дома и бани. Эскизный проект включает в себя два альбома:

Альбом 1 - *Двухэтажный индивидуальный жилой дом с баней.*
Альбом 1. Эскизный проект дома.

Альбом 2 - *Двухэтажный индивидуальный жилой дом с баней.*
Альбом 2. Эскизный проект бани.


Объемно-планировочные решения
Одноэтажная баня запроектирована в стиле современного минимализма с элементами скандинавской архитектуры
В разработанном эскизном проекте бани на 101,84 кв.м. предусмотрены помещения (см. экспликацию помещений на данном листе)

Архитектурно-планировочные решения приняты согластно пожеланиям Заказчика, а именно: баня одноэтажная, высота потолков переменная 2,5-2,75 м, кровля плоская.
Стены дома предварительно штуатурный фасад с декоративными элементами (планкен и декоративный камень). Цокольная часть искуственный или натуральный камень.

Баня запроектирована для II климатического района к В климатическому подрайону
Среднемесячная температура воздуха в январе – от −4 °С до −14 °С.
Среднемесячная температура воздуха в июле – от +12 °С до +21 °С.
Средняя скорость ветра зимой – не превышает 5 м/с.
Относительная влажность воздуха в июле – не более 75%
III снеговой район с расчётным весом снегового покрова 180 кг/м^2.
I ветровой район – 0,23 кПа
Степень огнестойкости II

Основные конструктивные решения и материалы:
- Фундаменты предварительно монолитная плита (уточняется с учетом геологических условий)
- Стены наружные 400мм, внутрениие несущие 200мм, перегородки 150 мм из газобетонных блоков D500.
- Фасады штукатурные с декоративными вставками (планкен и декоративный камень)
- Полы по монолитной плите. Толщина полоа с учетом утепления принята предванительно 250мм
- Кровля плоская из рулонных материалов
- Окна и витражи - алюминиевые и пластиковые двухкамерные стеклопакеты
- Материалы покрытия полов - керамогранитная плитка, паркетная доска, террасная доска ДПК.

	Двухэтажный индивидуальный жилой дом с баней. Альбом 2. Эскизный проект бани.	Архитектор	Харламов П.А.		Пояснительная записка	Лист	Листов
		Архитектор	Райтер С.С.			1	16
		Заказчик	_____				

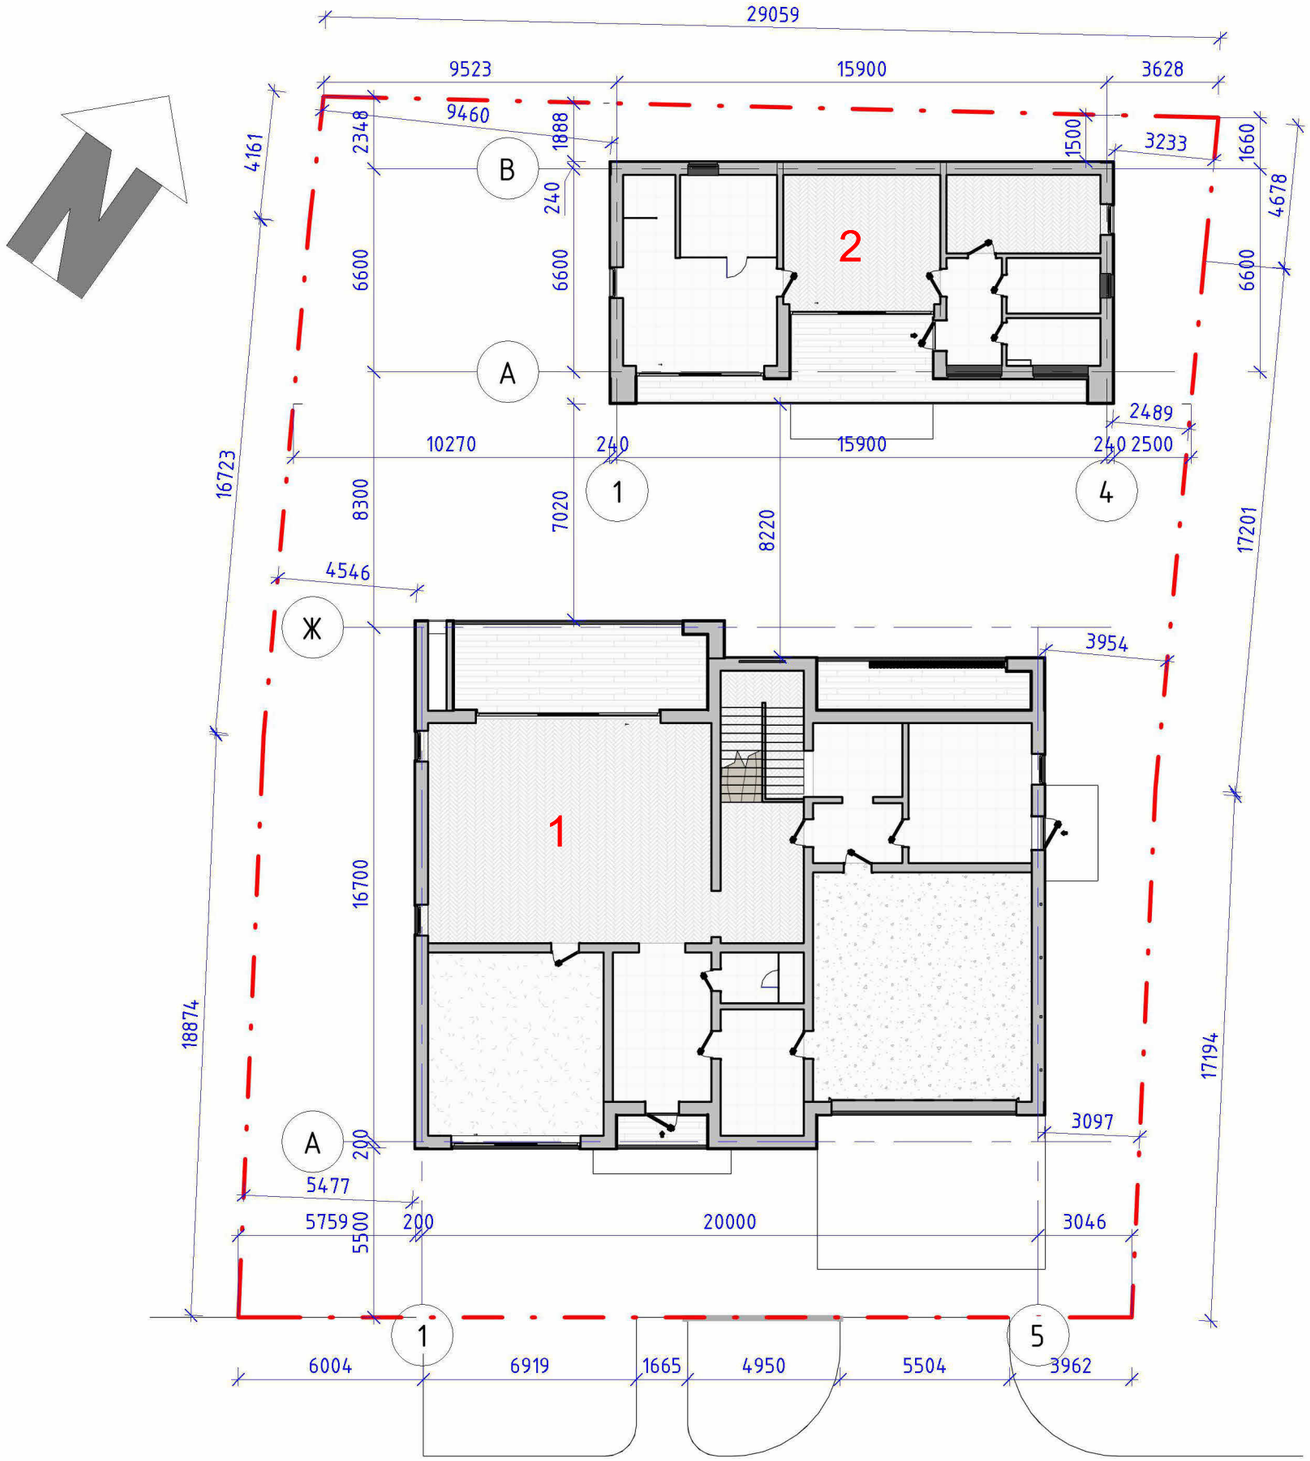


1 – Двухэтажный жилой дом
2 – Баня

Архитектор	Харламов П.А.	
Архитектор	Райтер С.С.	
Заказчик	_____	

Двухэтажный индивидуальный жилой дом с баней.
Альбом 2. Эскизный проект бани.

Привязка дома и бани на участке	Лист	Листов
	2	16

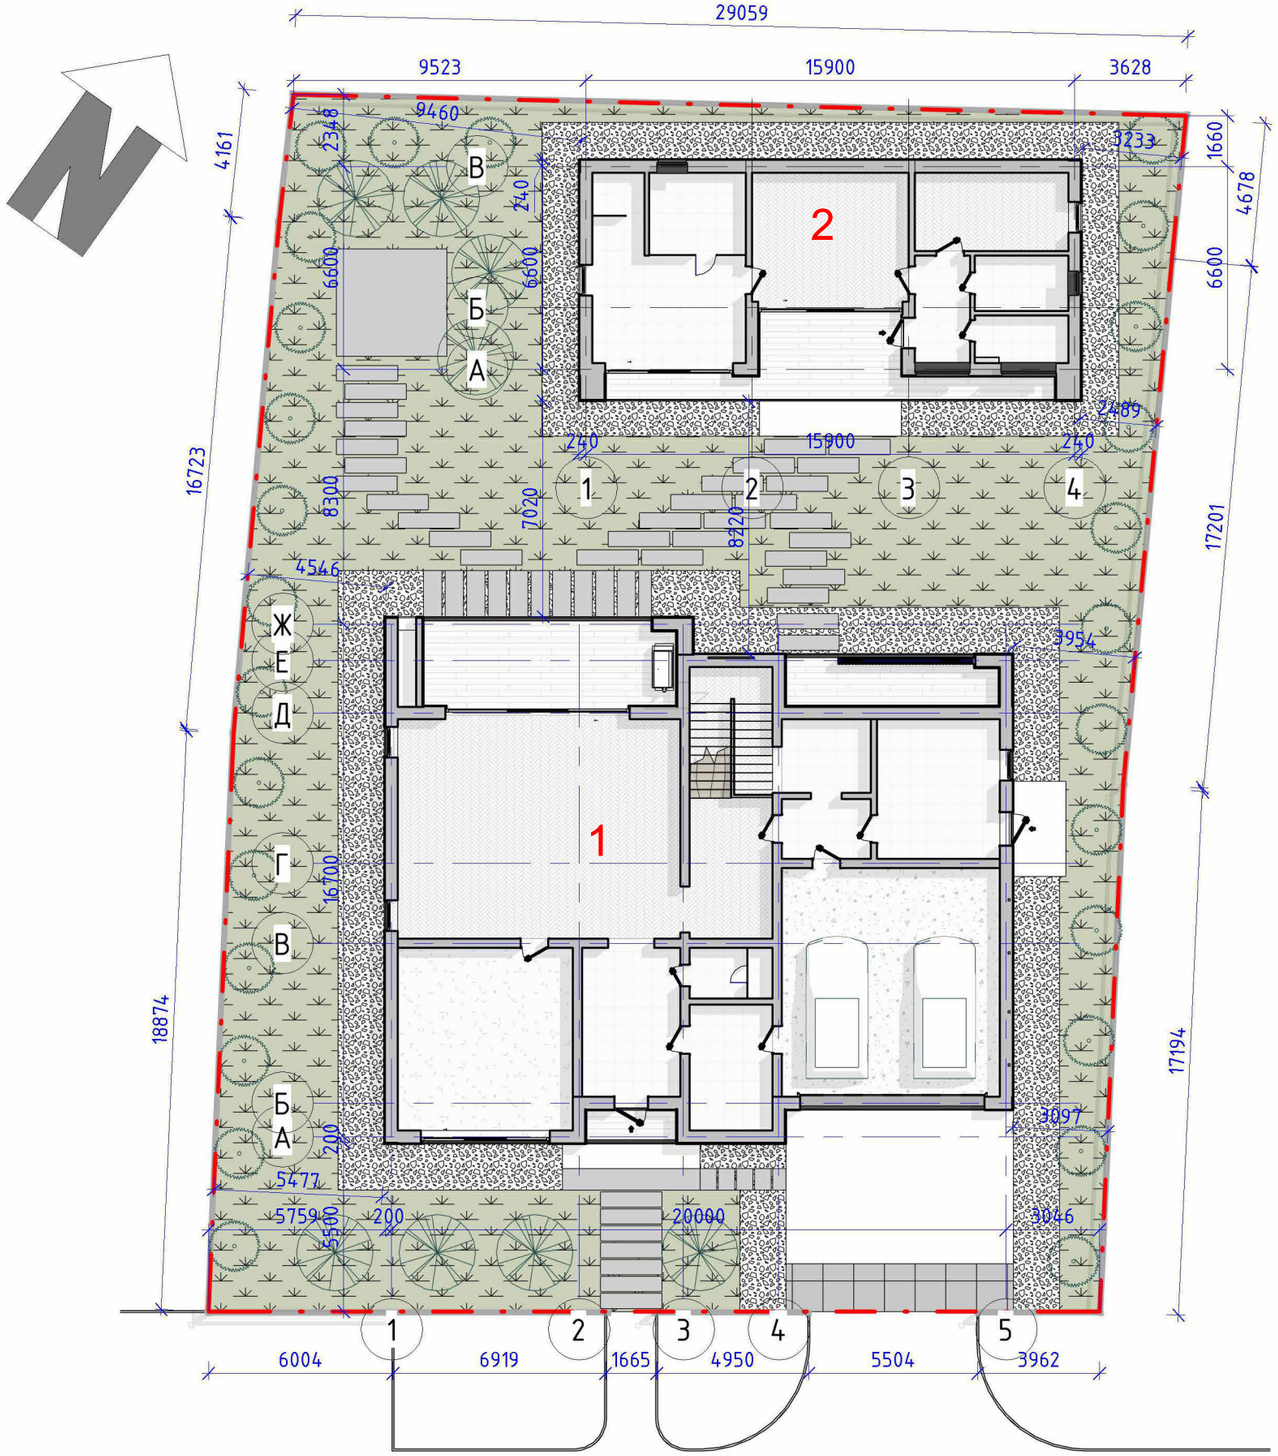


1 – Двухэтажный жилой дом
2 – Баня

Архитектор	Харламов П.А.	
Архитектор	Райтер С.С.	
Заказчик	_____	

Двухэтажный индивидуальный жилой дом с баней.
Альбом 2. Эскизный проект бани.

Схема благоустройства	Лист	Листов
	3	16

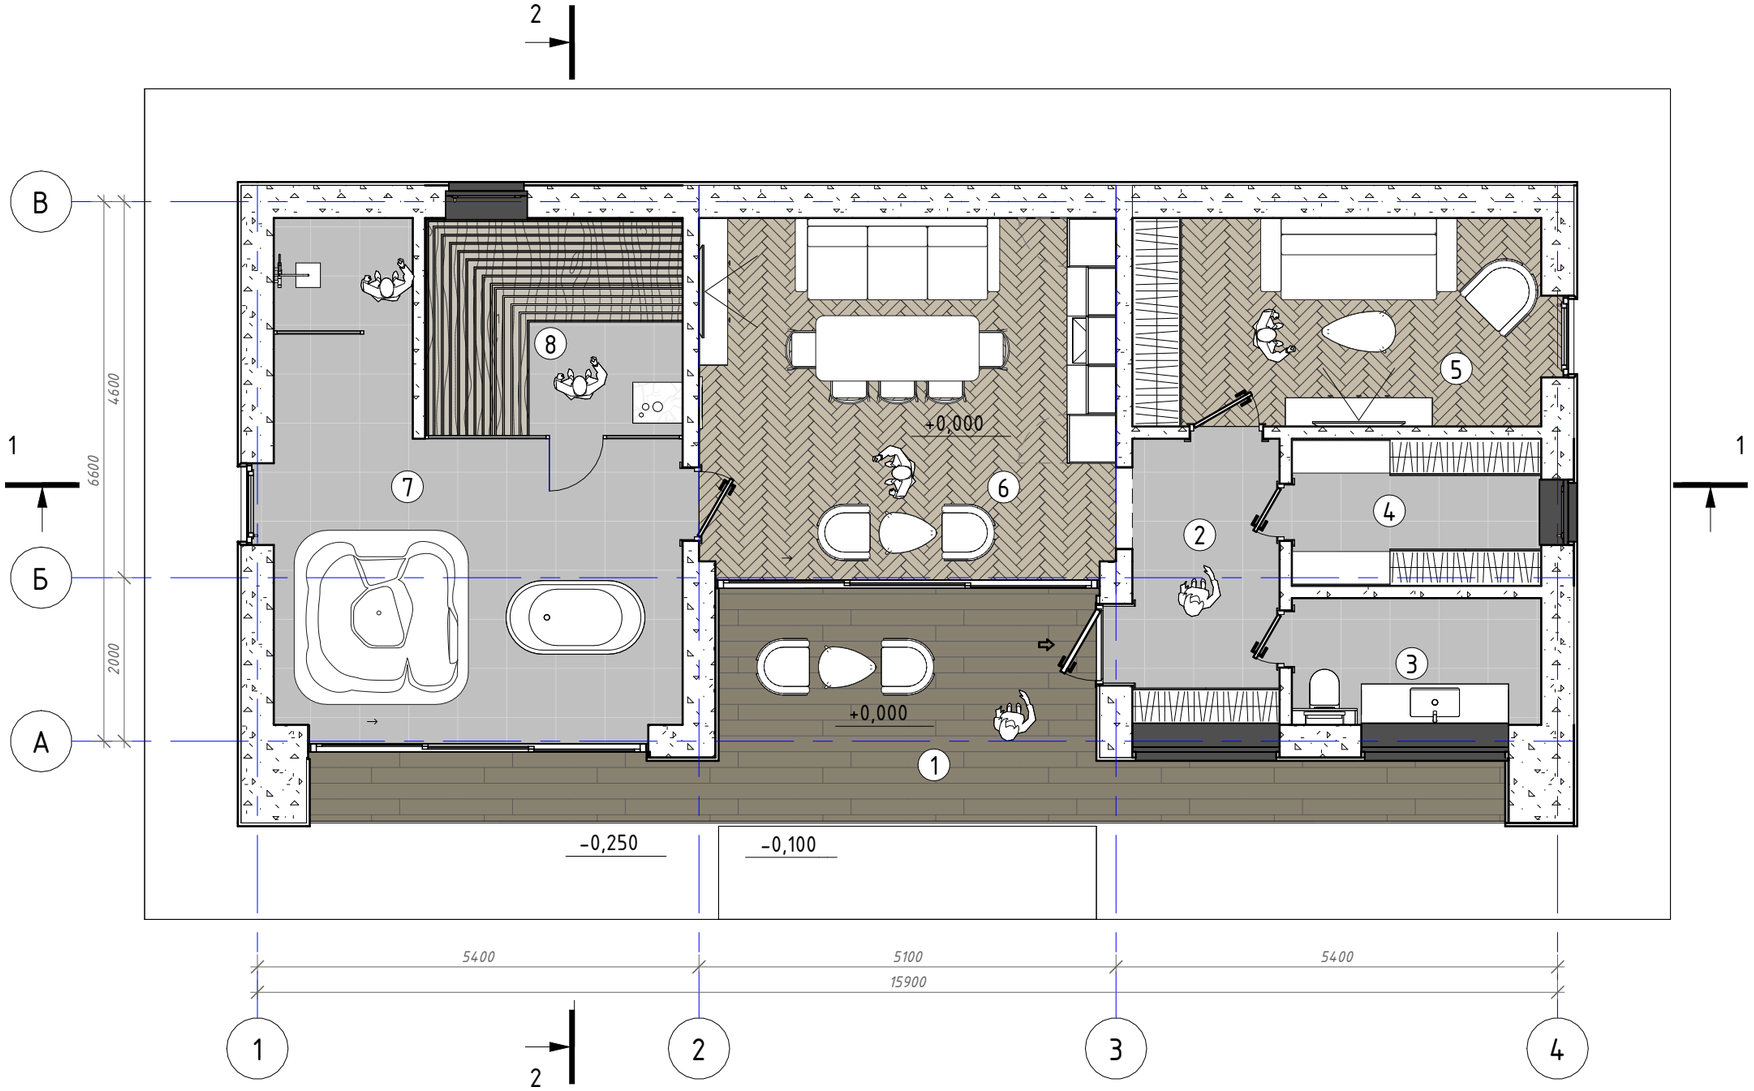


Экспликация помещений		
№	Наименование	S, м²
1	Терраса	20,71
2	Прихожая	6,30
3	С/у	4,57
4	Раздевалка	5,49
5	Спальня	12,75
6	Комната отдыха	21,42
7	Помывочная	22,16
8	Парная	8,44
Общая площадь		101,84

Архитектор	Харламов П.А.	
Архитектор	Райтер С.С.	
Заказчик	_____	

Двухэтажный индивидуальный жилой дом с баней.
Альбом 2. Эскизный проект бани.

Баня.Планировочное решение	Лист	Листов
	4	16

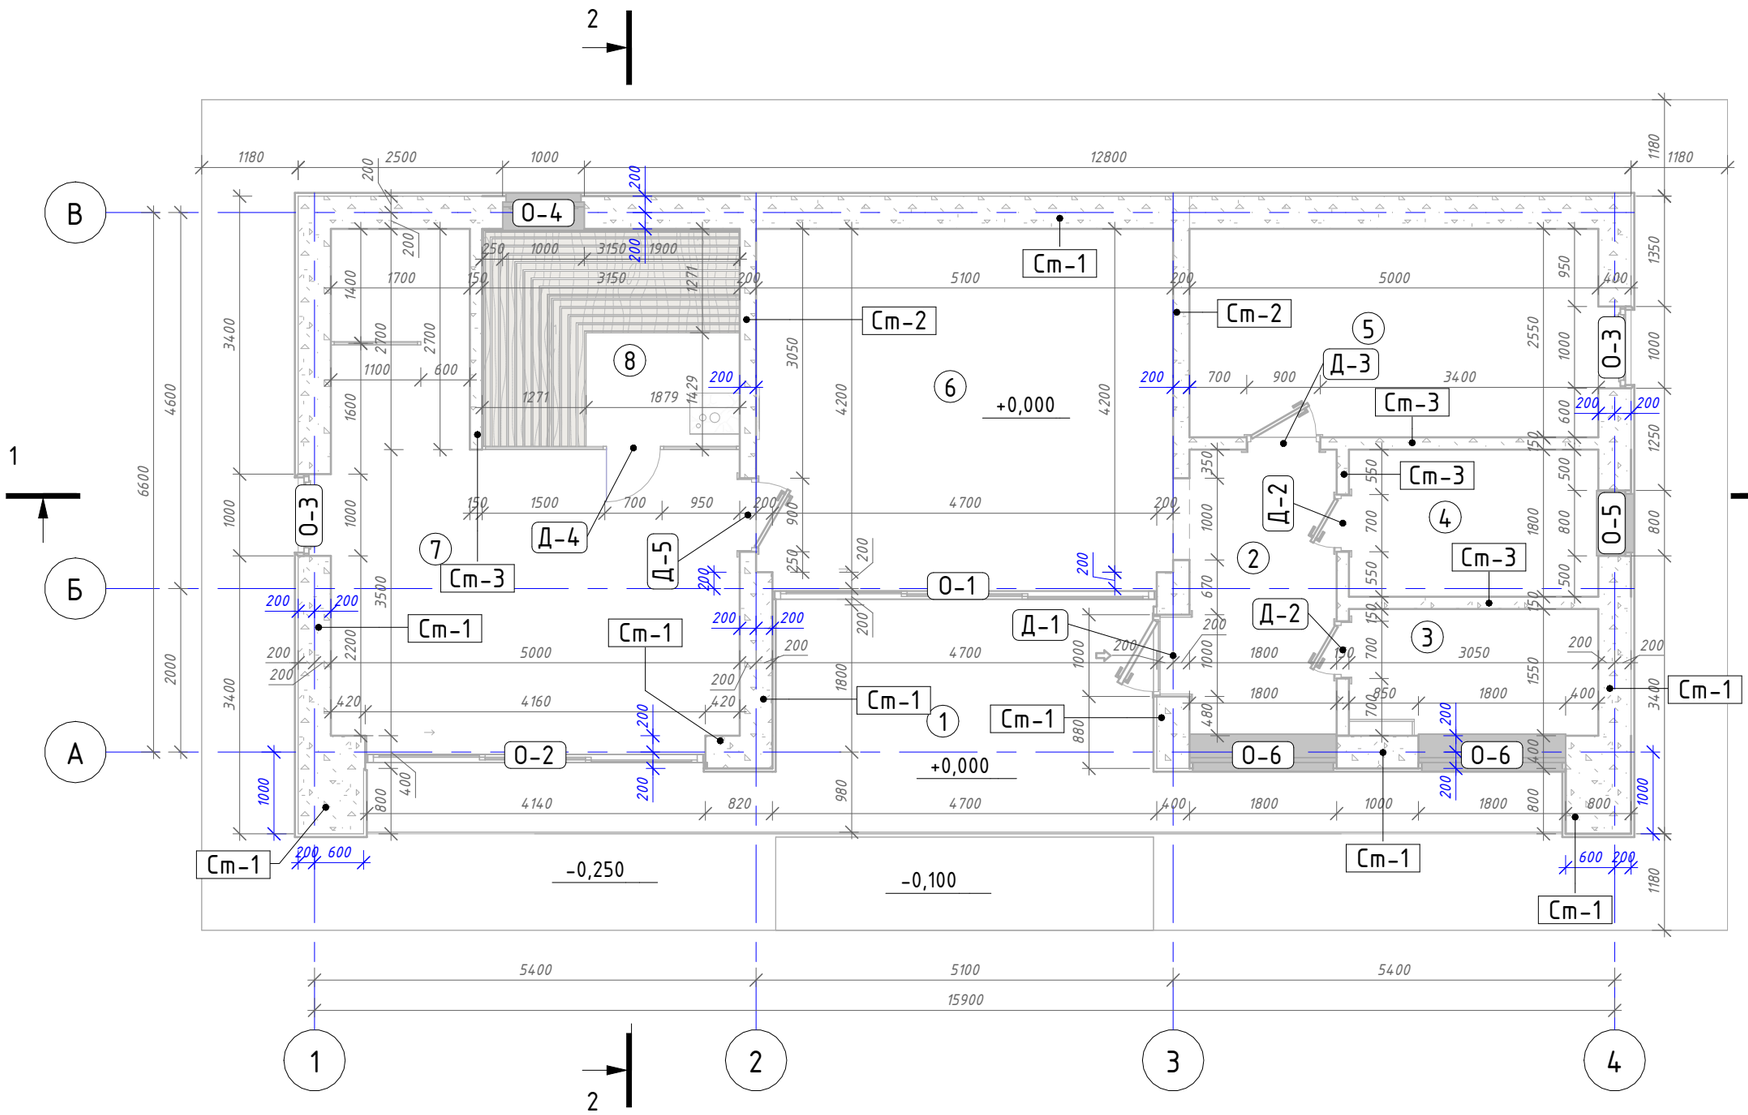

Экспликация помещений		
№	Наименование	S, м²
1	Терраса	20,71
2	Прихожая	6,30
3	С/у	4,57
4	Раздевалка	5,49
5	Спальня	12,75
6	Комната отдыха	21,42
7	Помывочная	22,16
8	Парная	8,44
Общая площадь		101,84

Спецификация стен из газобетона

Марка	Тип	Объем	Площадь
Ст-1	Газобетонный блок D500 t400мм	49,33 м³	124,77 м²
Ст-2	Газобетонный блок D500 t200 мм	6,98 м³	34,91 м²
Ст-3	Газобетонный блок D500 t150мм	5,68 м³	37,90 м²
Общий итог: 23		61,99 м³	197,58 м²

Монолитный фундамент (ребро фундаментной плиты 300мм*850h и плита t=200мм.) V=38куб.м.
Монолитное перекрытие 1 этажа t=200мм. V=26куб.м.

Примечание:
1. Все объемы даны предварительно и уточняются на следующих стадиях проектирования

Спецификация окон

Марка	Высота	Ширина	Описание	Кол-во
О-1	2750	4700	Окно раздвижное 3 створки	1
О-2	2750	4160	Окно раздвижное 3 створки	1
О-3	2750	1000	Поворотно-откидное	2
О-4	500	1000	Поворотно-откидное	1
О-5	750	800	Поворотно-откидное	1
О-6	750	1800	Глухое	2
Общий итог: 8				


Ведомость дверей

Марка	Описание	Габариты проёма, мм	Откр-е	Кол-во
Д-1	Дверь входная одностворчатая с остеклением	1000x2750	Левое Наружу	1
Д-2	Дверь межкомнатная одностворчатая	700x2370	Левое Наружу	2
Д-3	Дверь межкомнатная одностворчатая	900x2370	Правое Наружу	1
Д-4	Дверь сауны одностворчатая	660x1980		1
Д-5	Дверь межкомнатная одностворчатая	900x2370	Левое Наружу	1

Архитектор	Харламов П.А.	
Архитектор	Райтер С.С.	
Заказчик	_____	

Двухэтажный индивидуальный жилой дом с баней.
Альбом 2. Эскизный проект бани.

Баня.Планировочное решение. Размеры.	Лист	Листов
	5	16

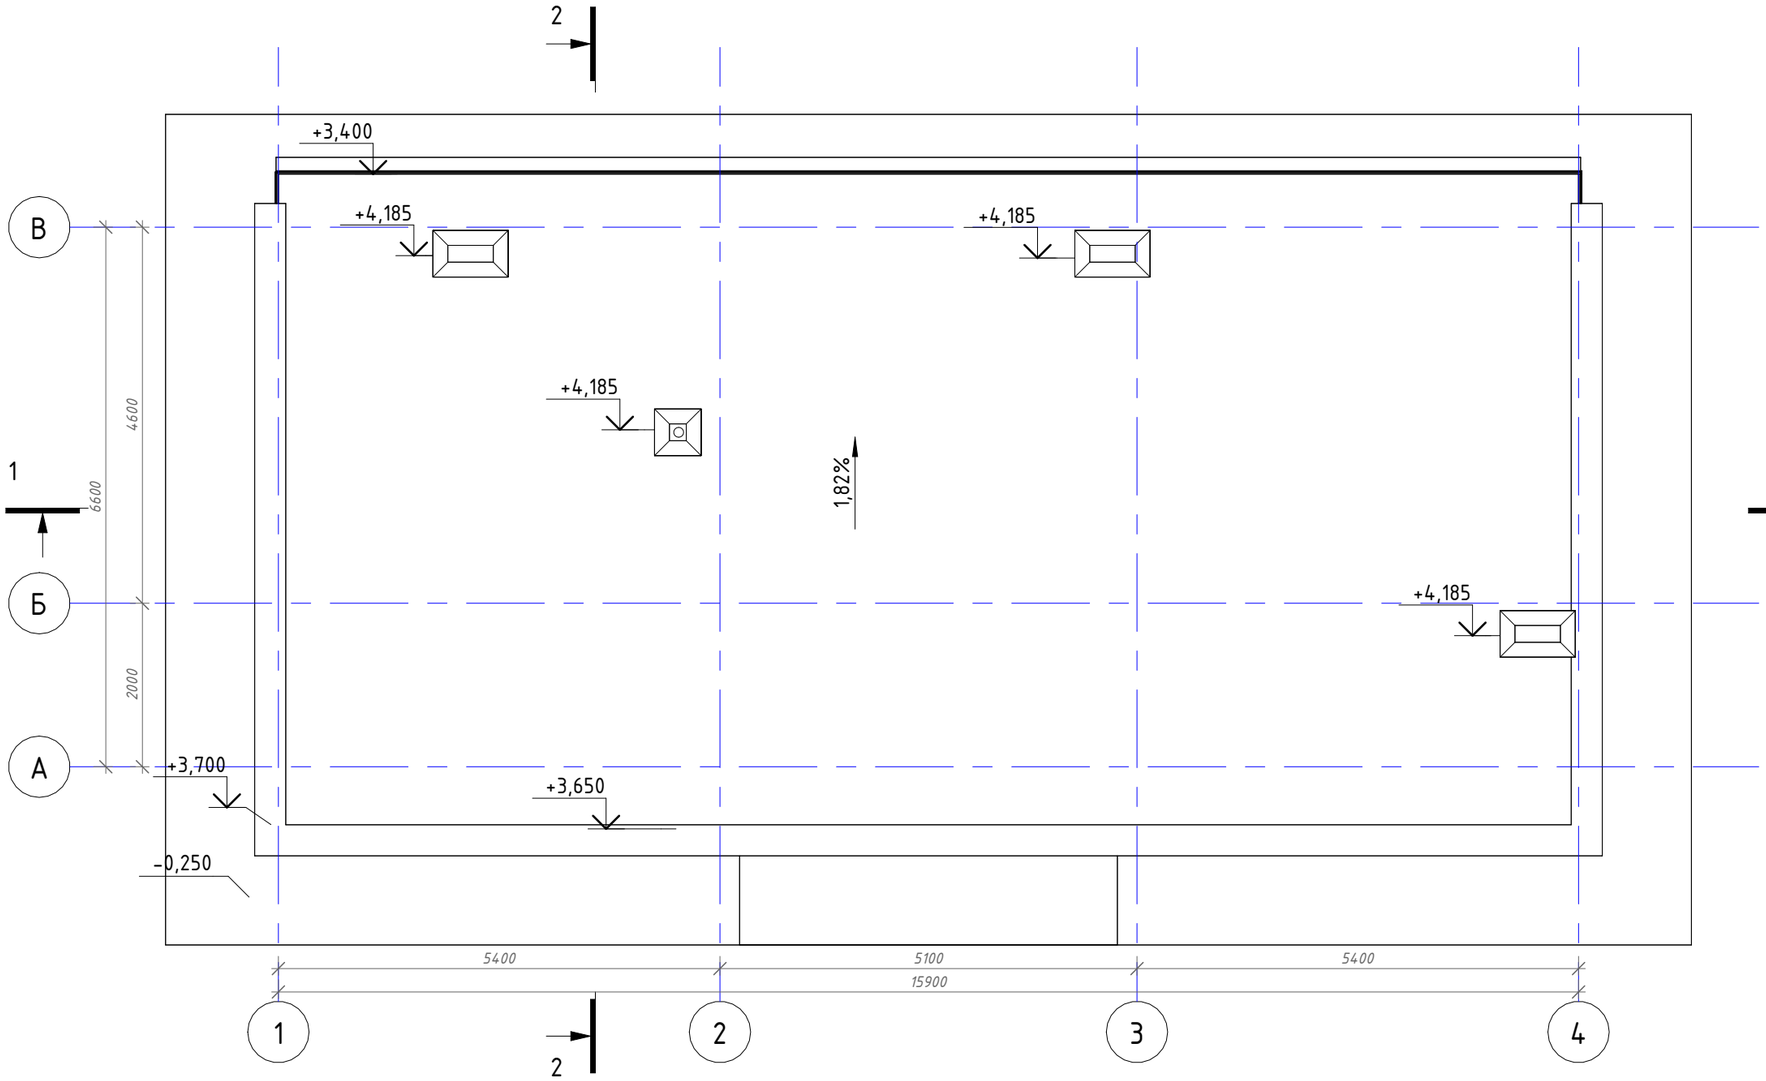

Площадь кровли составляет 131 кв.м.


Архитектор	Харламов П.А.	
Архитектор	Райтер С.С.	
Заказчик	_____	

Двухэтажный индивидуальный жилой дом с баней.


Альбом 2. Эскизный проект бани.

Баня. План кровли.	Лист	Листов
	6	16

Разрез 1-1
1 : 65

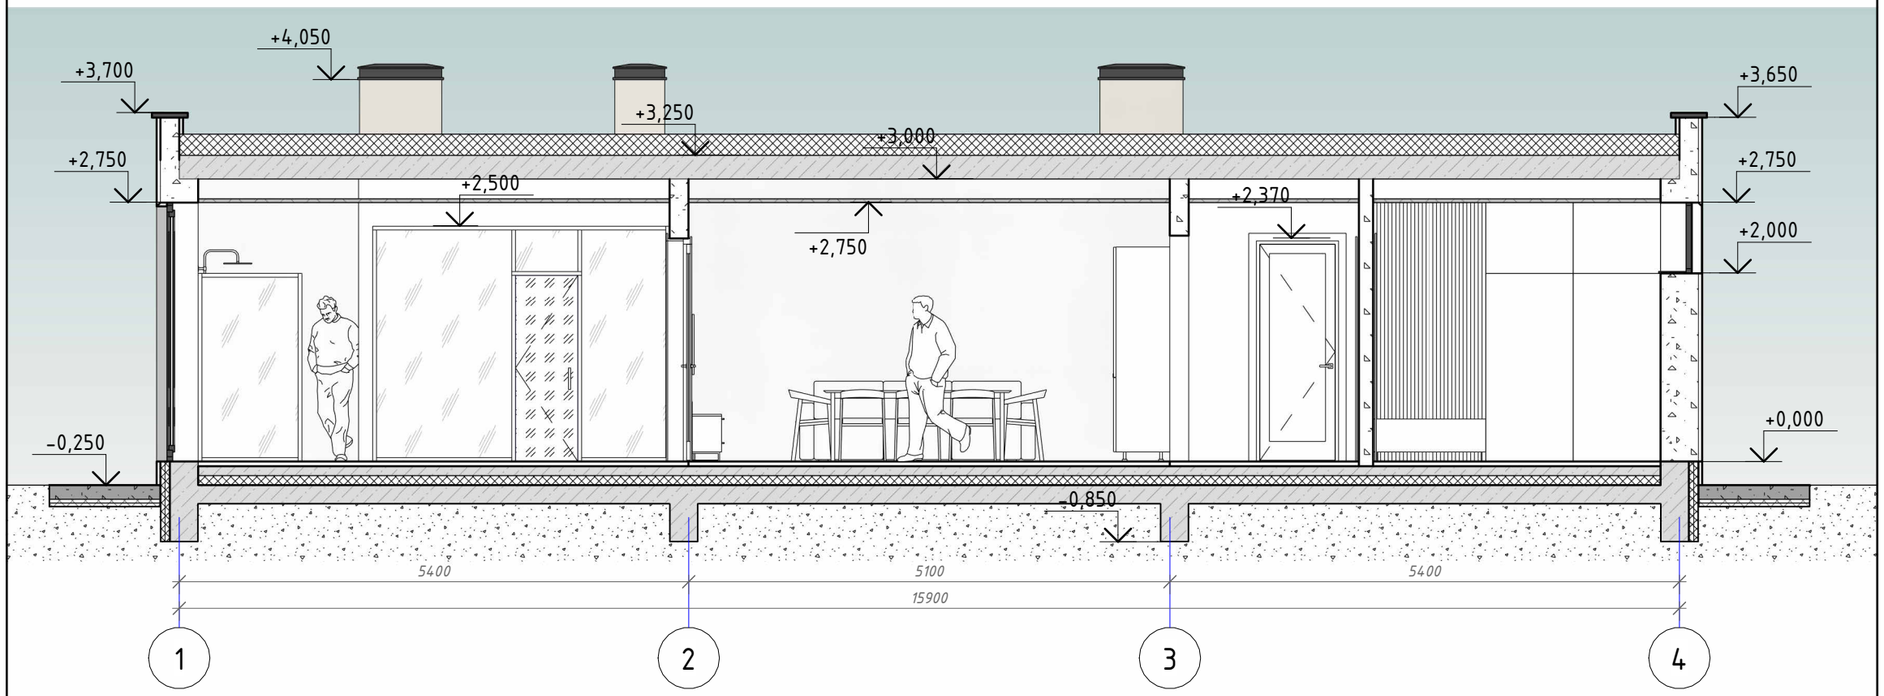

Разрез 2-2
1 : 65

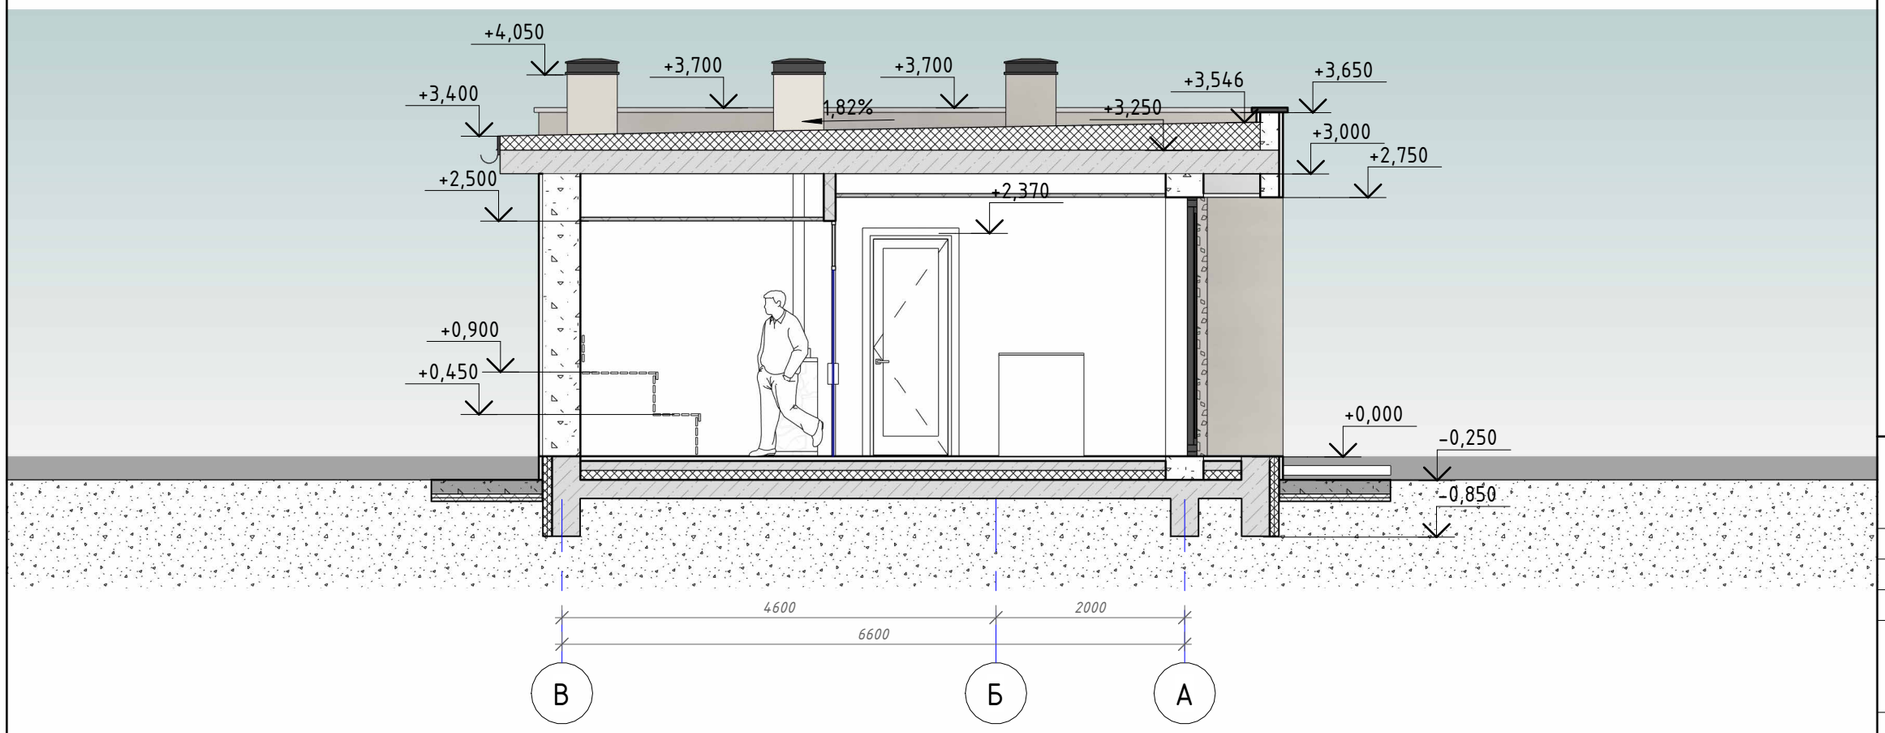


Архитектор	Харламов П.А.	
Архитектор	Райтер С.С.	
Заказчик		

Двухэтажный индивидуальный жилой дом с баней.
Альбом 2. Эскизный проект бани.

Баня. Разрез 1-1, 2-2	Лист	Листов
	7	16



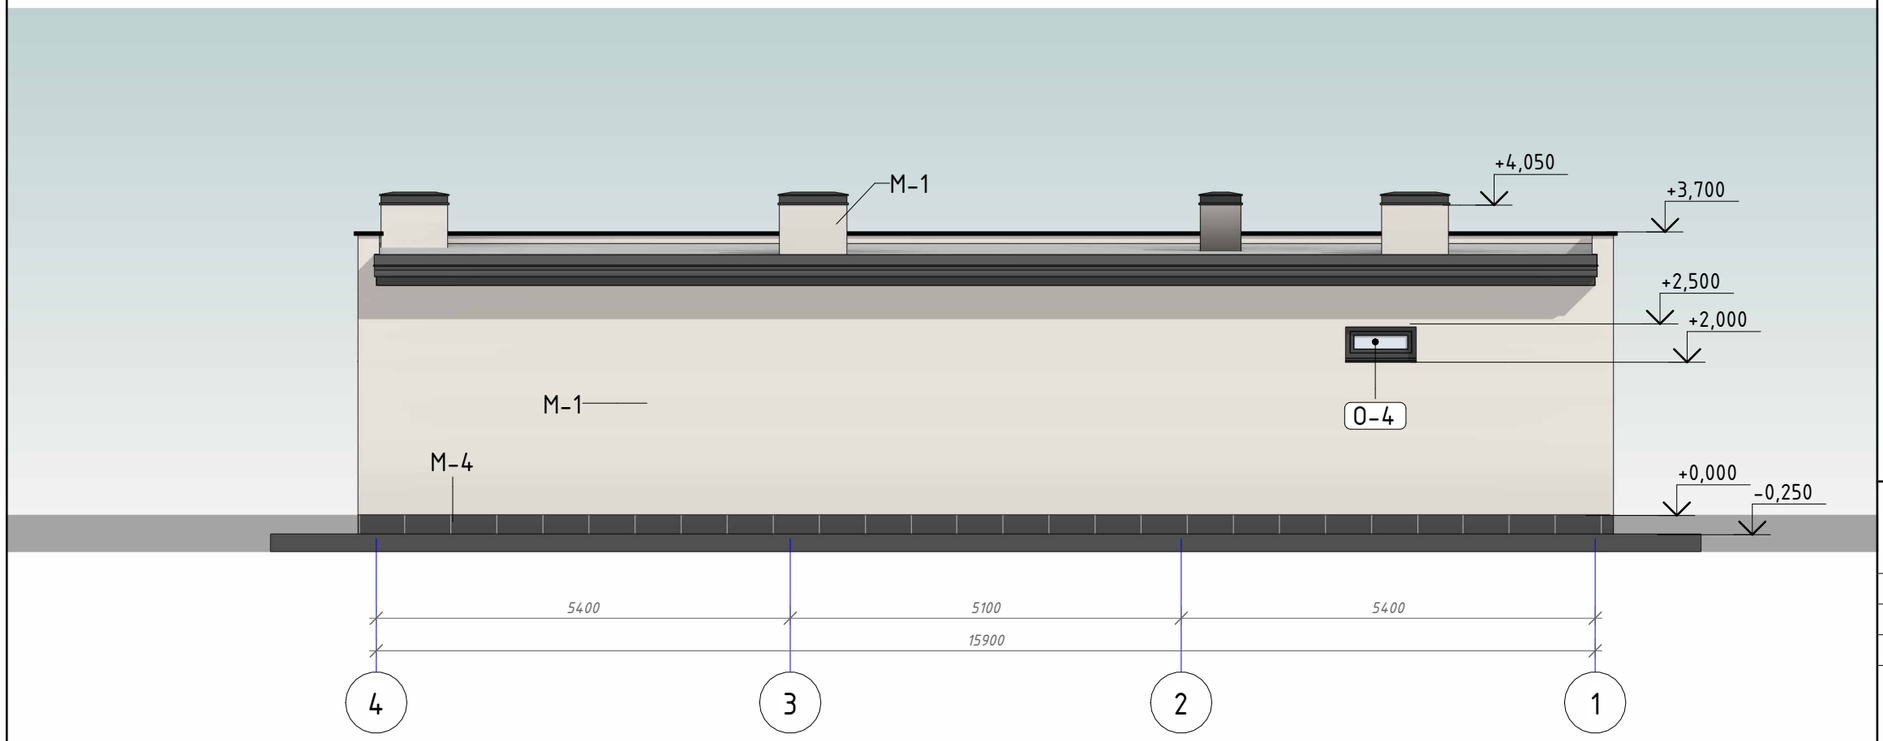

Ведомость материалов фасадов

Марка	Изображение	Площадь	Описание
М-1		137,09 м²	Штукатурка декоративная мраморная Bayramix EcoStone 774
М-2		17,63 м²	Планкен
М-3		8,31 м²	Искусственный камень White Hills Рутланд цвет 603-00
М-4		12,09 м²	Крупноформатный керамогранит Lifebrick Mountain Black new
		175,11 м²	


Рамы окон, наружных дверей, ворот и декоративных элементов Ral7024


Архитектор	Харламов П.А.	
Архитектор	Райтер С.С.	
Заказчик	_____	

Двухэтажный индивидуальный жилой дом с баней.
Альбом 2. Эскизный проект бани.

Баня. Фасад 1-4, 4-1

Лист	Листов
8	16

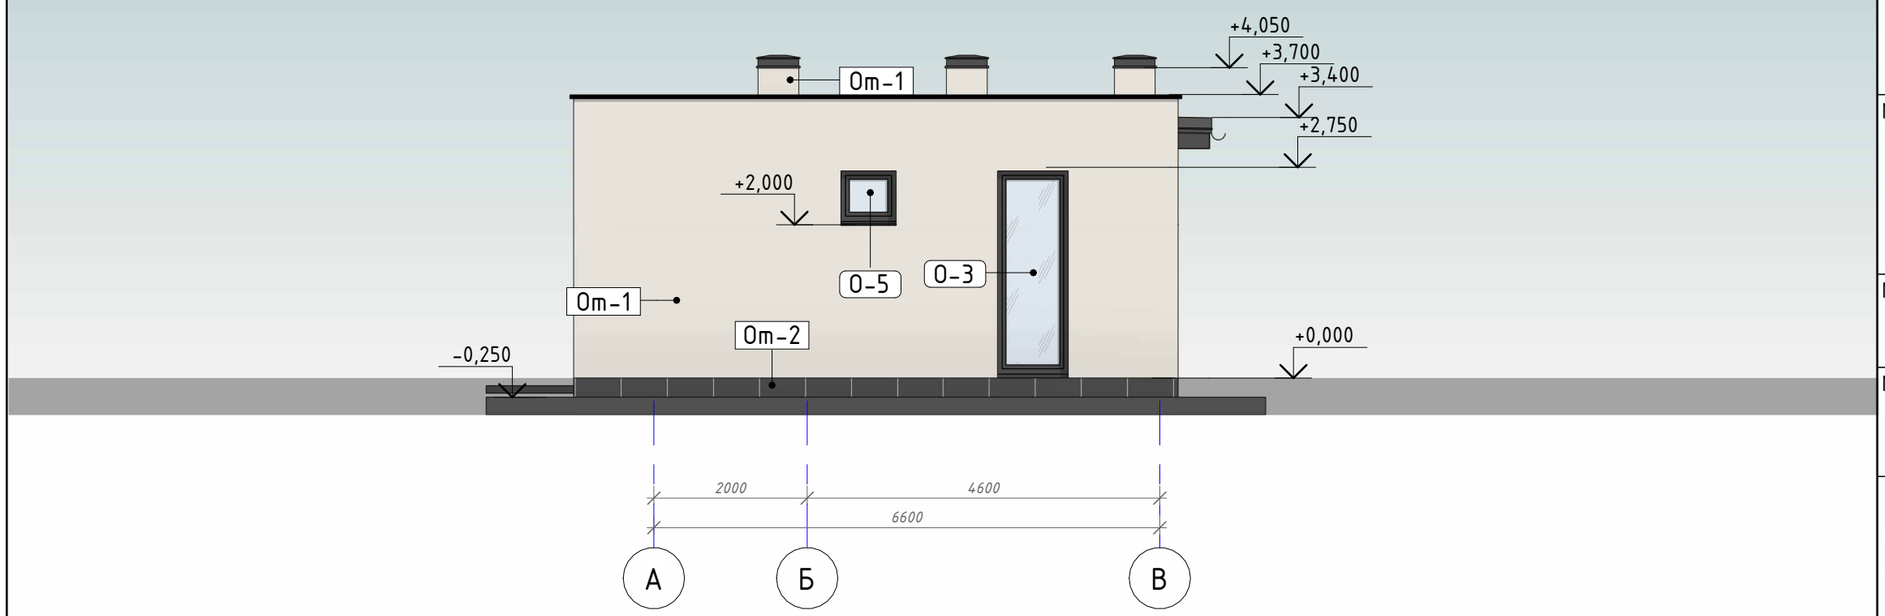

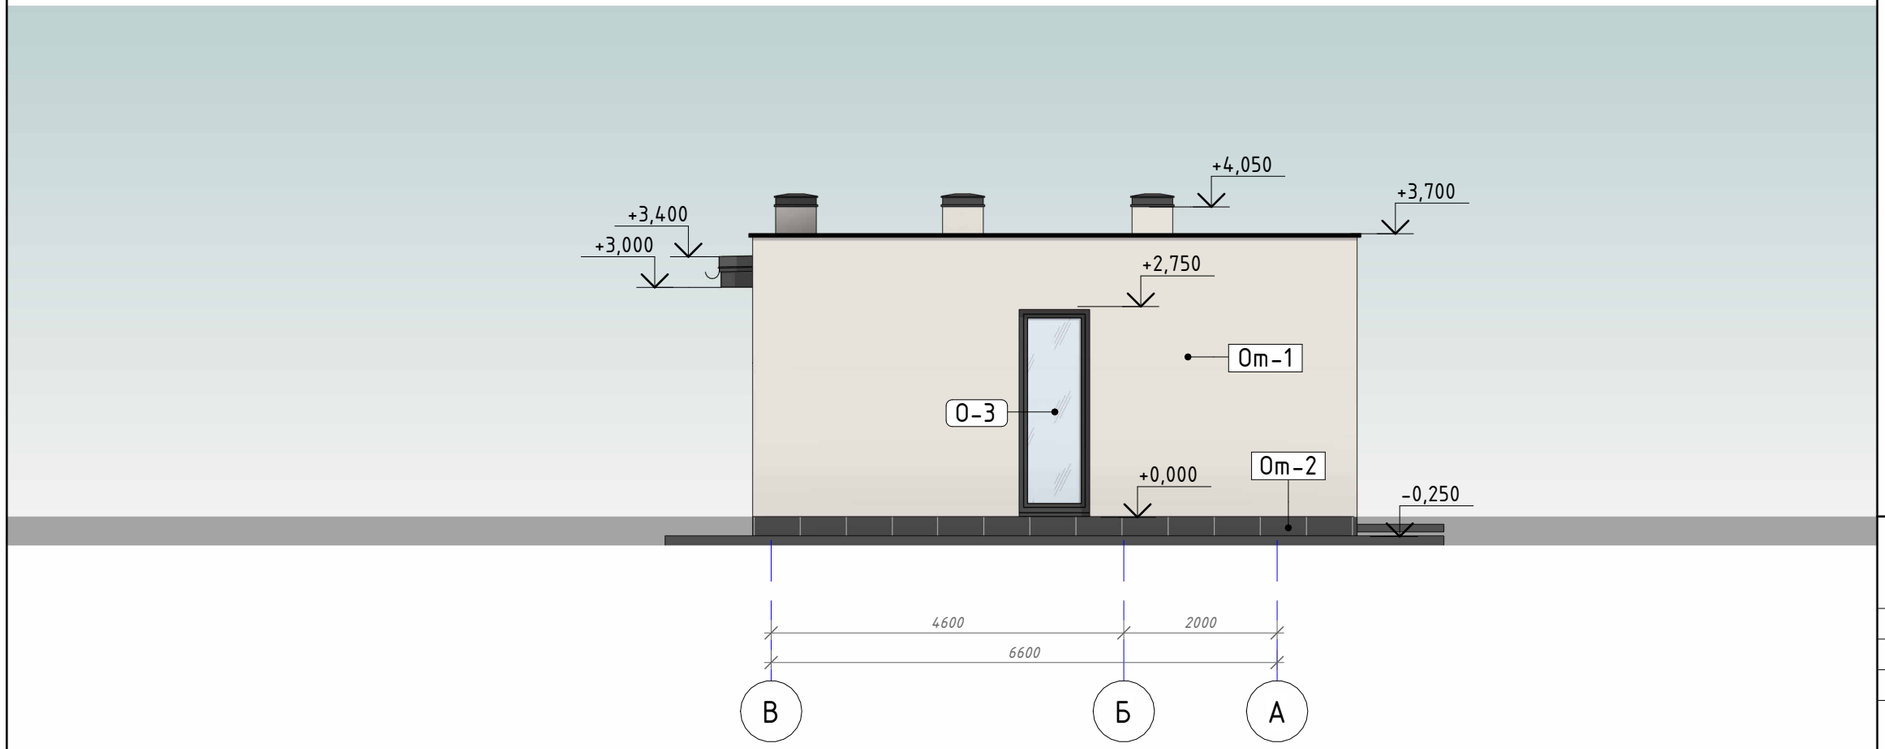

Ведомость материалов фасадов

Марка	Изображение	Площадь	Описание
М-1		137,09 м²	Штукатурка декоративная мраморная Bayramix EcoStone 774
М-2		17,63 м²	Планкен
М-3		8,31 м²	Искусственный камень White Hills Рутланд цвет 603-00
М-4		12,09 м²	Крупноформатный керамогранит Lifebrick Mountain Black new
		175,11 м²	

Рамы окон, наружных дверей, ворот и декоративных элементов Ral7024

Архитектор	Харламов П.А.	
Архитектор	Райтер С.С.	
Заказчик	_____	

Двухэтажный индивидуальный жилой дом с баней.
Альбом 2. Эскизный проект бани.

	Лист	Листов
Баня. Фасад А-В, В-А	9	16



Архитектор	Харламов П.А.	
Архитектор	Райтер С.С.	
Заказчик	_____	

Двухэтажный индивидуальный жилой дом с баней.

Альбом 2. Эскизный проект бани.

Баня. 3D Вид 1	Лист	Листов
	10	16




Архитектор	Харламов П.А.	
Архитектор	Райтер С.С.	
Заказчик	_____	

Двухэтажный индивидуальный жилой дом с баней.
Альбом 2. Эскизный проект бани.

Баня. 3D Вид 2

Лист	Листов
11	16

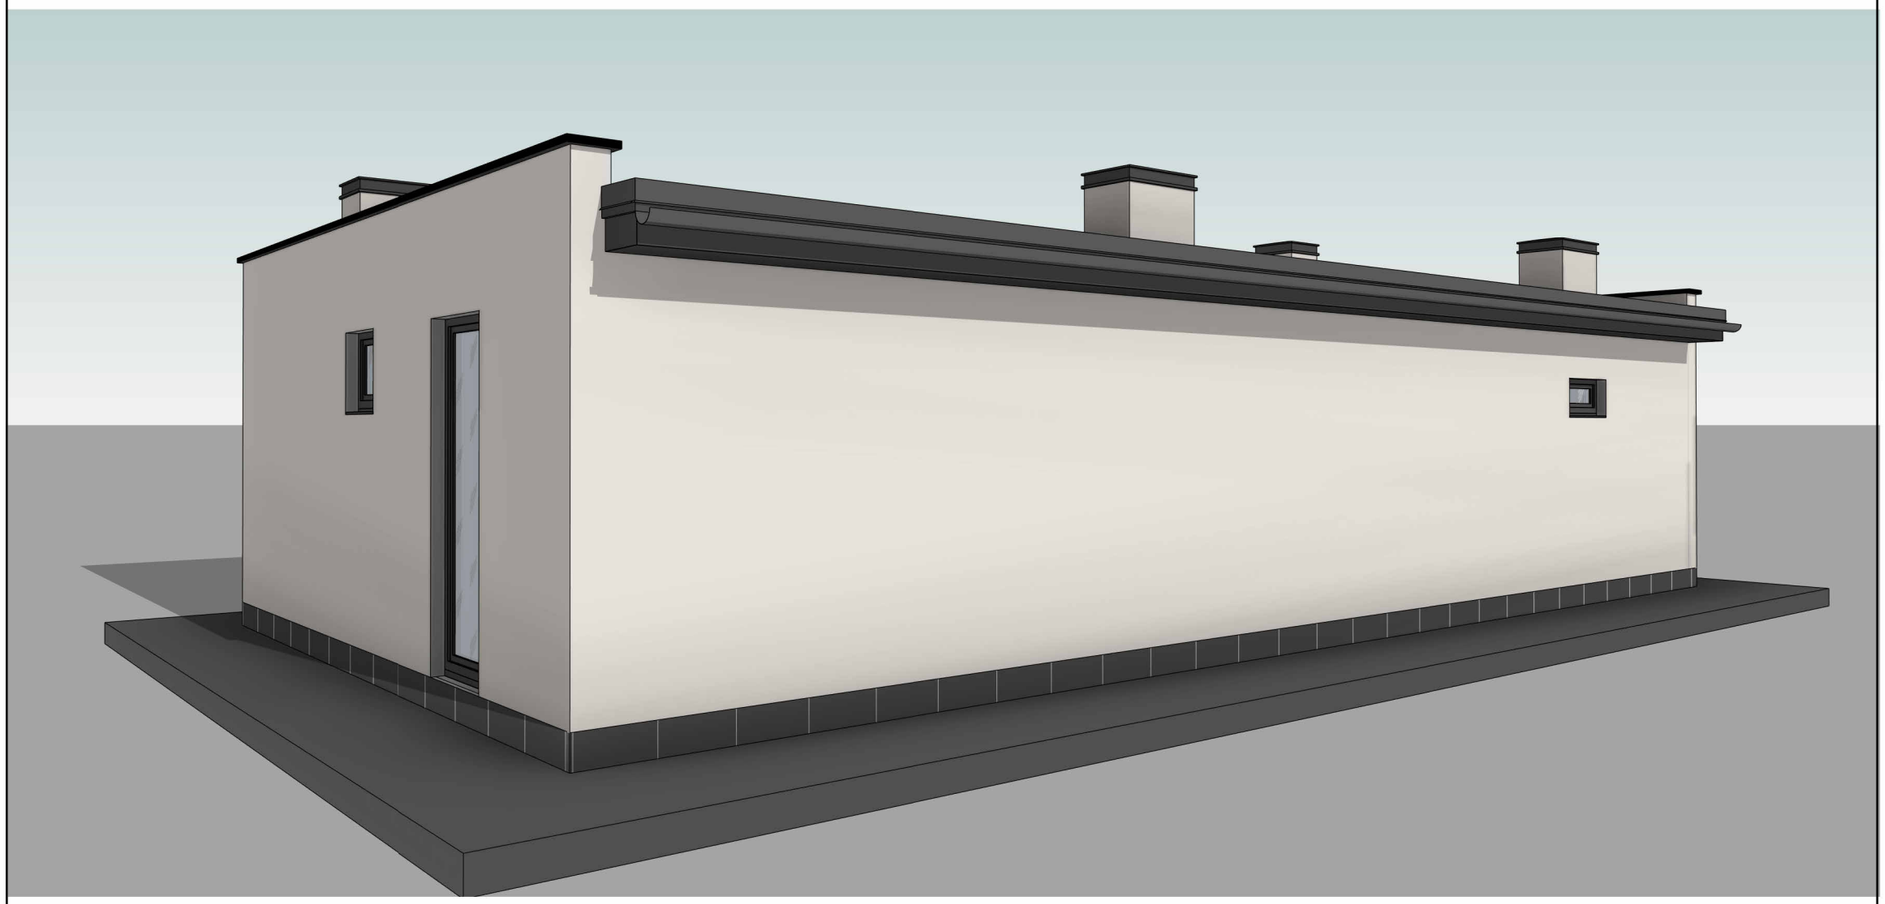


Архитектор	Харламов П.А.	
Архитектор	Райтер С.С.	
Заказчик	_____	

Двухэтажный индивидуальный жилой дом с баней.

Альбом 2. Эскизный проект бани.

Баня. 3D Вид 3

Лист	Листов
12	16

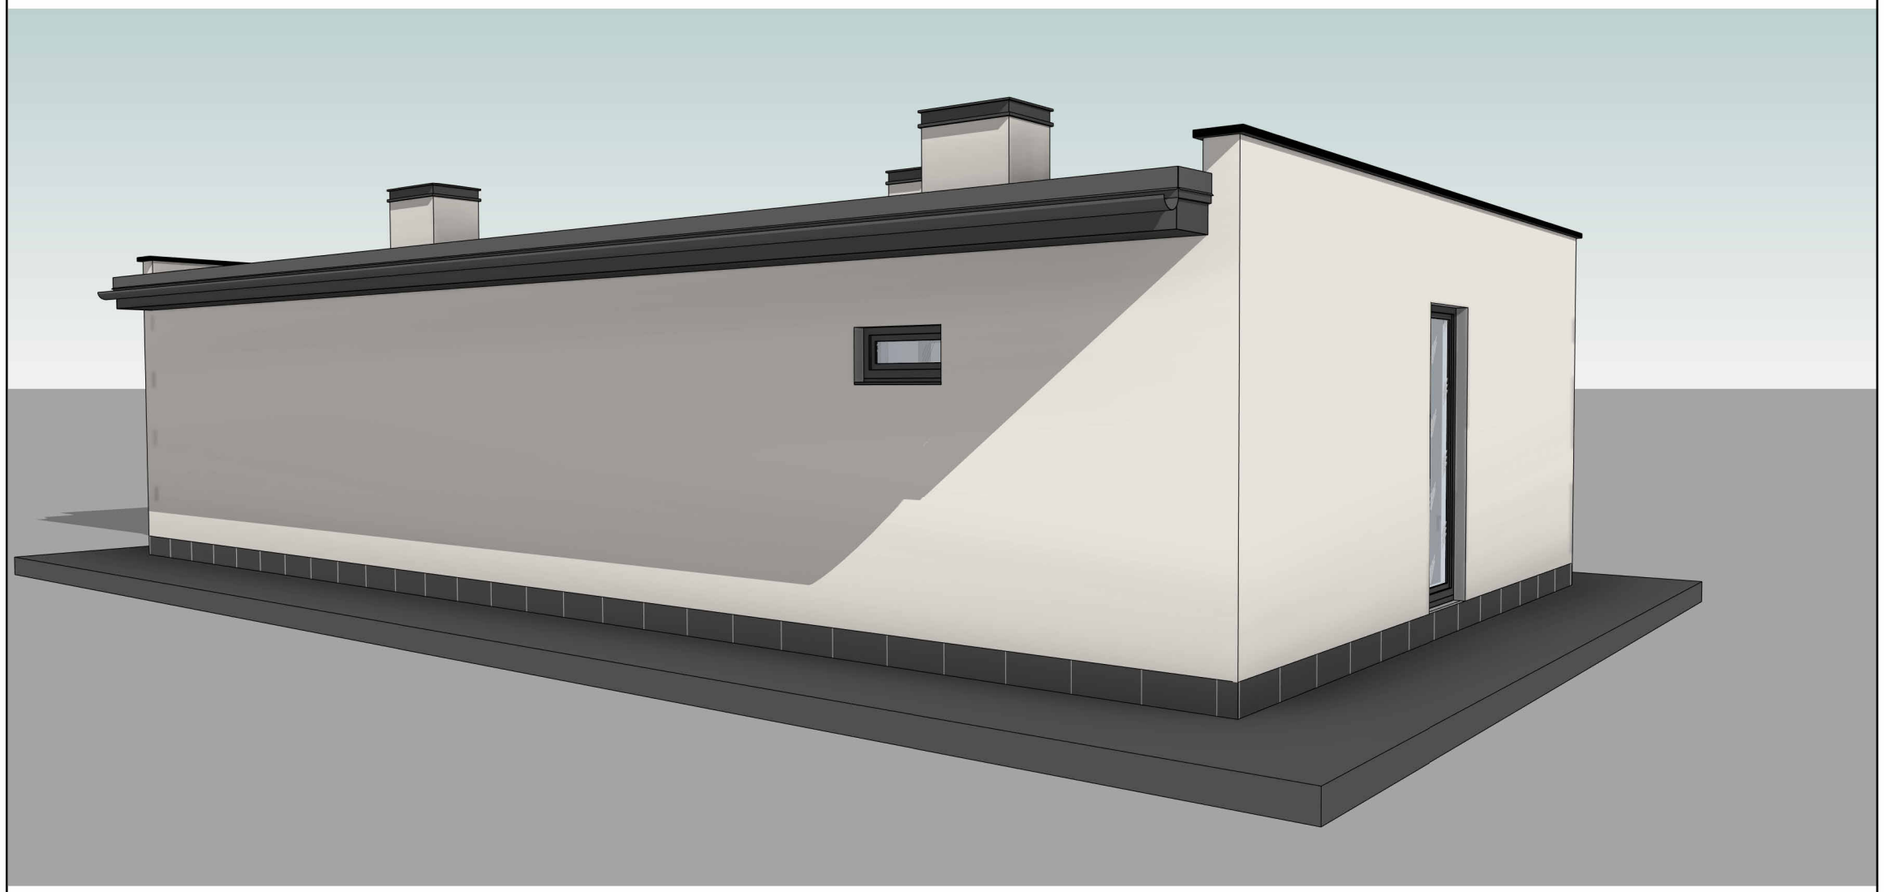

Архитектор	Харламов П.А.	
Архитектор	Райтер С.С.	
Заказчик	_____	

Двухэтажный индивидуальный жилой дом с баней.

Альбом 2. Эскизный проект бани.

Баня. 3D Вид 4	Лист	Листов
	13	16



Архитектор	Харламов П.А.	
Архитектор	Райтер С.С.	
Заказчик	_____	

Двухэтажный индивидуальный жилой дом с баней.
Альбом 2. Эскизный проект бани.

	Лист	Листов
Визуализация	14	16



Архитектор	Харламов П.А.	
Архитектор	Райтер С.С.	
Заказчик	_____	

Двухэтажный индивидуальный жилой дом с баней.
Альбом 2. Эскизный проект бани.

Визуализация	Лист	Листов
	15	16



Архитектор	Харламов П.А.	
Архитектор	Райтер С.С.	
Заказчик	_____	

Двухэтажный индивидуальный жилой дом с баней.

Альбом 2. Эскизный проект бани.

	Лист	Листов
Визуализация	16	16