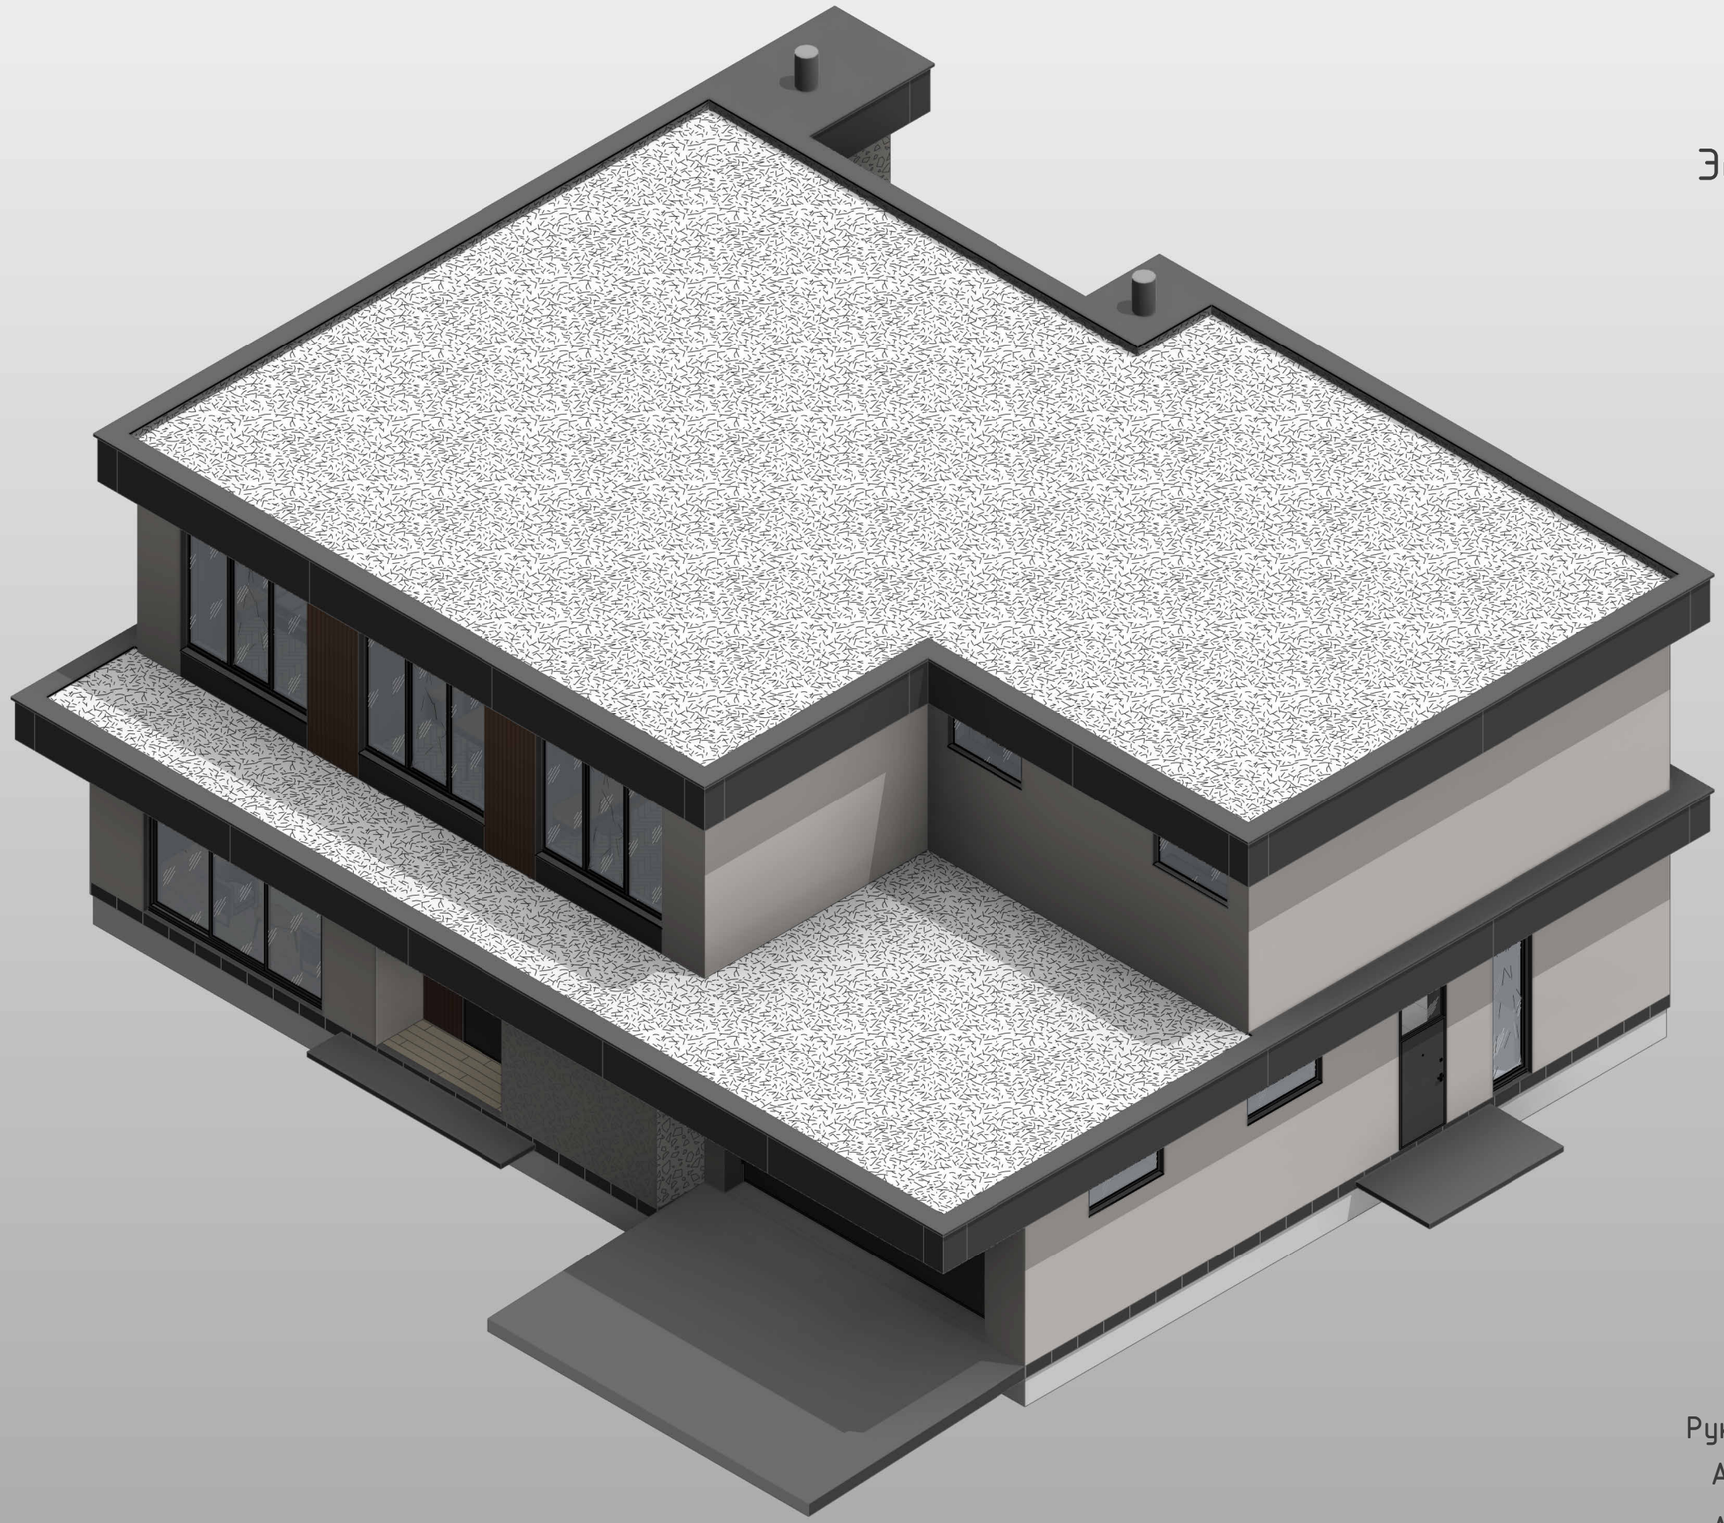


Эскизный проект

Двухэтажный индивидуальный жилой дом с баней.

Альбом 2. Эскизный проект дома.

Заказчик _____

Подрядчик

Руководитель Иванова Е.С.

Архитектор Харламов П.А.

Архитектор Райтер С.С.

Москва
2026

Ведомость рабочих чертежей1	
Номер листа	Имя листа
1. Альбом	
0	Титульный лист
1	Пояснительная записка
2	Привязка дома и бани на участке
3	Схема благоустройства
4	Дом.Планировочное решение. 1 этаж.
5	Дом.Планировочное решение. 1 этаж. Размеры.
6	Дом.Планировочное решение. 2 этаж.
7	Дом.Планировочное решение. 2 этаж. Размеры.
8	Дом. План кровли.
9	Дом. Разрез 1-1, 2-2
10	Дом. Фасад 1-5, 5-1
11	Дом. Фасад А-Ж, Ж-А
12	Дом. 3D Вид 1
13	Дом. 3D Вид 2
14	Дом. 3D Вид 3
15	Дом. 3D Вид 4
16	Визуализация.
17	Визуализация.
18	Визуализация.
19	Визуализация.
20	Визуализация.
21	Визуализация.

Пояснительная записка
Кадастровый номер участка: 50:08:0050209:1600
На участке предполагается расположение двухэтажного дома и бани. Эскизный проект включает в себя два альбома:

Альбом 1 - *Двухэтажный индивидуальный жилой дом с баней.*
Альбом 1. Эскизный проект дома.

Альбом 2 - *Двухэтажный индивидуальный жилой дом с баней.*
Альбом 2. Эскизный проект бани.

Объемно-планировочные решения
Двухэтажный жилой дом запроектирован в стиле современного минимализма с элементами скандинавской архитектуры
В разработанном эскизном проекте бани на 440,13 кв.м. предусмотрены помещения (см. экспликацию помещений на данном листе).

Архитектурно-планировочные решения приняты согластно пожеланиям Заказчика, а именно: дом двухэтажный, высота потолков первого этажа 3,3м, высота потолков 2 этажа 3м, кровля плоская.
Отделка фасадов дома предварительно штукатурный фасад с декоративными элементами (планкен и декоративный камень).
Цокольная часть искуственный или натуральный камень.


Индивидуальный жилой дом запроектирован для II климатического района к В климатическому подрайону
Среднемесячная температура воздуха в январе – от −4 °С до −14 °С.
Среднемесячная температура воздуха в июле – от +12 °С до +21 °С.
Средняя скорость ветра зимой – не превышает 5 м/с.
Относительная влажность воздуха в июле – не более 75%
III снеговой район с расчётным весом снегового покрова 180 кг/м².
I ветровой район – 0,23 кПа
Степень огнестойкости II

Экспликация помещений		
№	Наименование	S, м²
1 этаж		
1.1	Крыльцо	3,10
1.2	Прихожая	15,52
1.3	Тамбур	11,07
1.4	С/у	4,46
1.5	Гараж	52,90
1.6	Топочная	18,20
1.7	Тамбур	5,66
1.8	Кладовая	6,96
1.9	Лестница-холл	23,90
1.10	Кухня-гостиная	65,78
1.11	Бильярдная	33,92
1.12	Терраса	23,16
1.13	Хозблок	10,10
		274,70

Экспликация помещений		
№	Наименование	S, м²
2 этаж		
2.1	Лестница-холл	25,11
2.2	Балкон	13,34
2.3	Спальня	19,40
2.4	Кабинет	18,43
2.5	Спальня	19,40
2.6	Гардеробная	13,20
2.7	Спальня	18,20
2.8	С/у	9,20
2.9	С/у	6,67
2.10	Балкон	11,01
		153,96
Общая площадь		428,66

Основные конструктивные решения и материалы:
- Фундаменты предварительно монолитная плита (уточняется с учетом геологических условий)
- Тип каркаса дома решается на следующих этапах проектирования. Предварительно несущие стены из газобетона D500 толщиной 400мм, 300мм. Перегородки 200мм, 150 мм из газобетонных блоков D400.
- Фасады предварительно штукатурные с декоративными вставками (планкен и декоративный камень)
- Полы по монолитной плите. Толщина полоов с учетом утепления принята предванительно 250мм
- Кровля плоская
- Окна - алюминиевые и пластиковые двухкамерные стеклопакеты
- Материалы покрытия полов - керамогранитная плитка, паркетная доска, террасная доска ДПК.

	Двухэтажный индивидуальный жилой дом с баней. Альбом 2. Эскизный проект дома.	Архитектор	Харламов П.А.		Пояснительная записка	Лист 1 / Листов 21
		Архитектор	Райтер С.С.			
		Заказчик	_____			

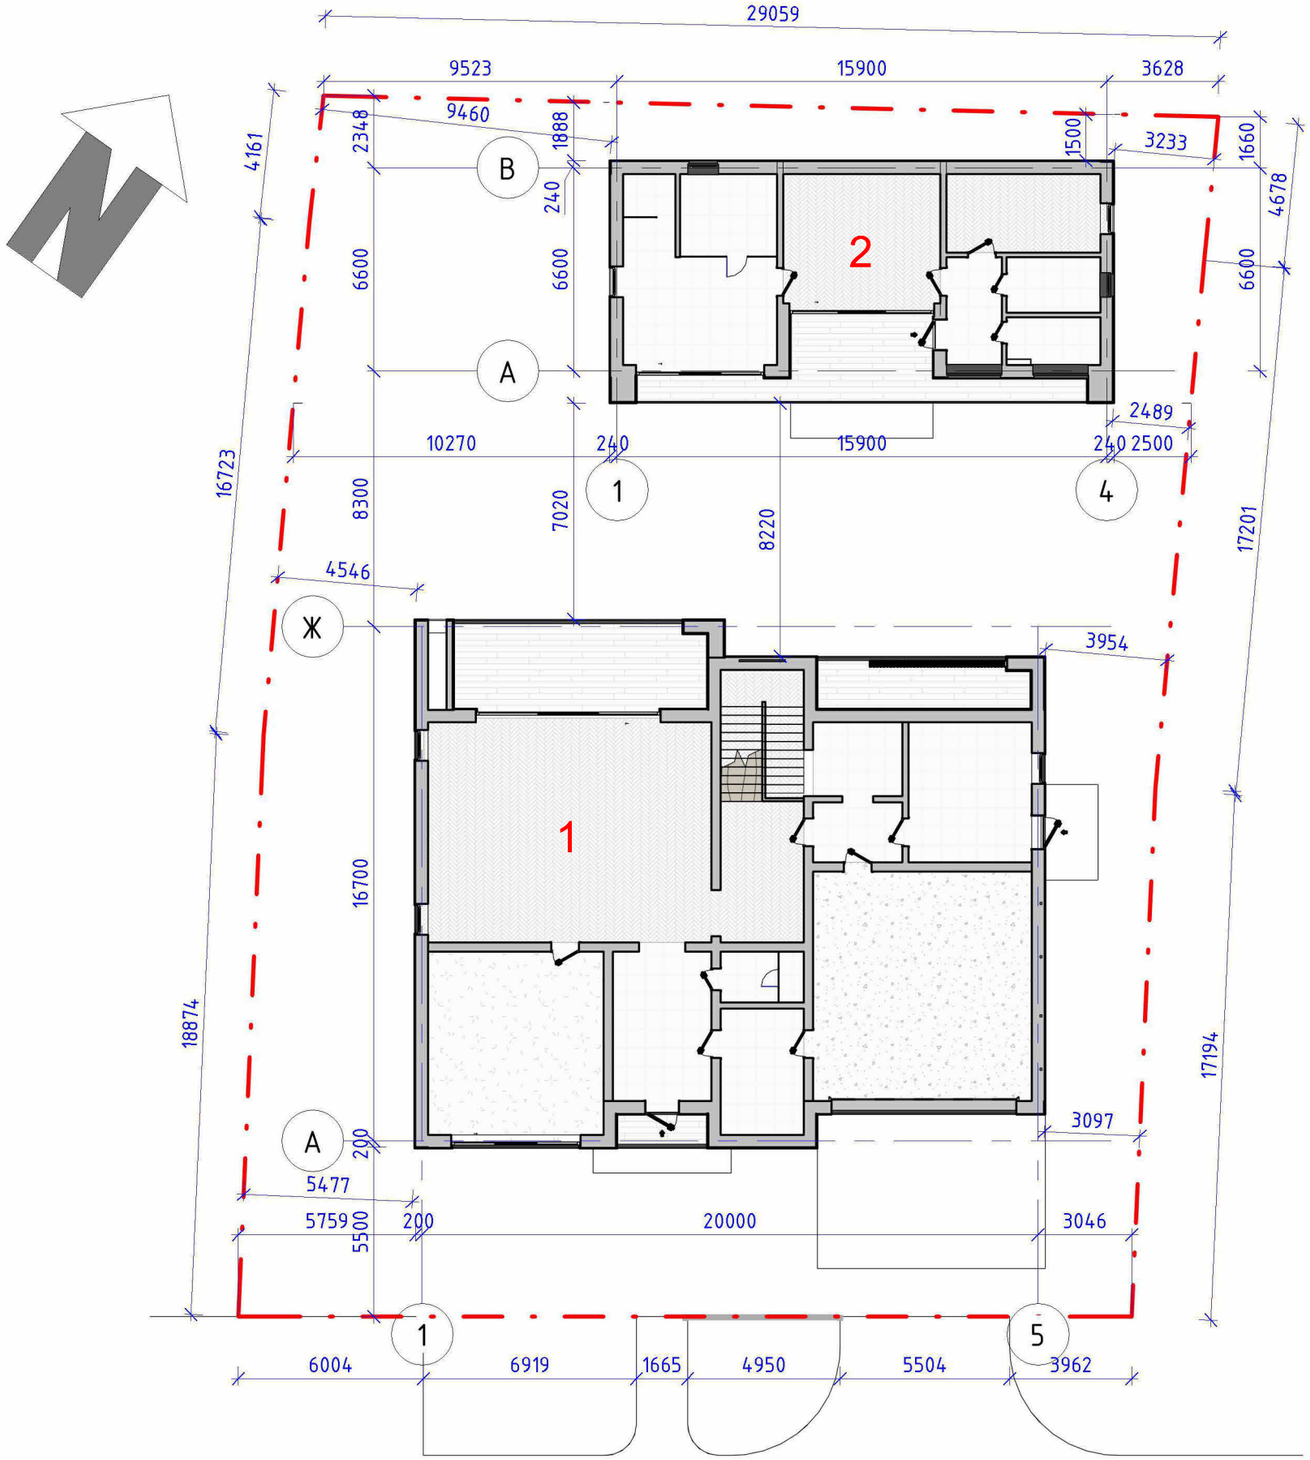


1 – Двухэтажный жилой дом
2 – Баня

Архитектор	Харламов П.А.	
Архитектор	Райтер С.С.	
Заказчик	_____	

Двухэтажный индивидуальный жилой дом с баней.
Альбом 2. Эскизный проект дома.

Привязка дома и бани на участке	Лист	Листов
	2	21

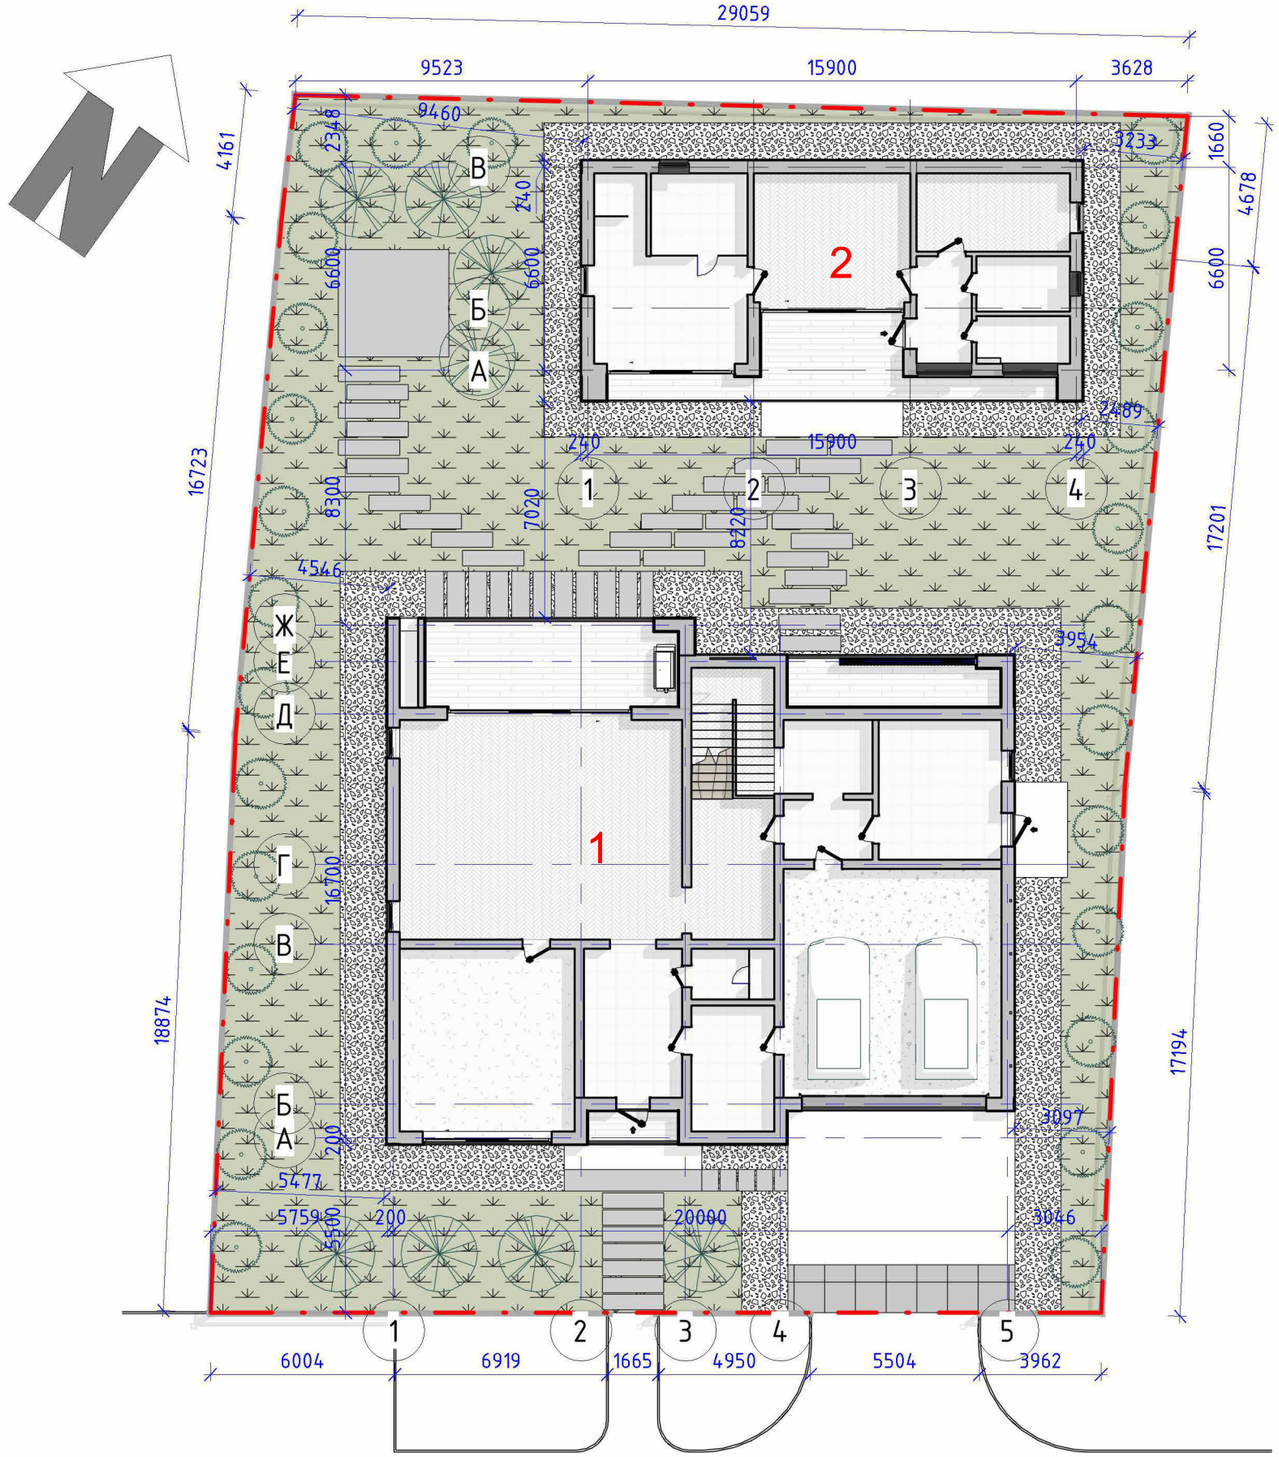


1 – Двухэтажный жилой дом
2 – Баня

Архитектор	Харламов П.А.	
Архитектор	Райтер С.С.	
Заказчик	_____	

Двухэтажный индивидуальный жилой дом с баней.
Альбом 2. Эскизный проект дома.

Схема благоустройства	Лист	Листов
	3	21

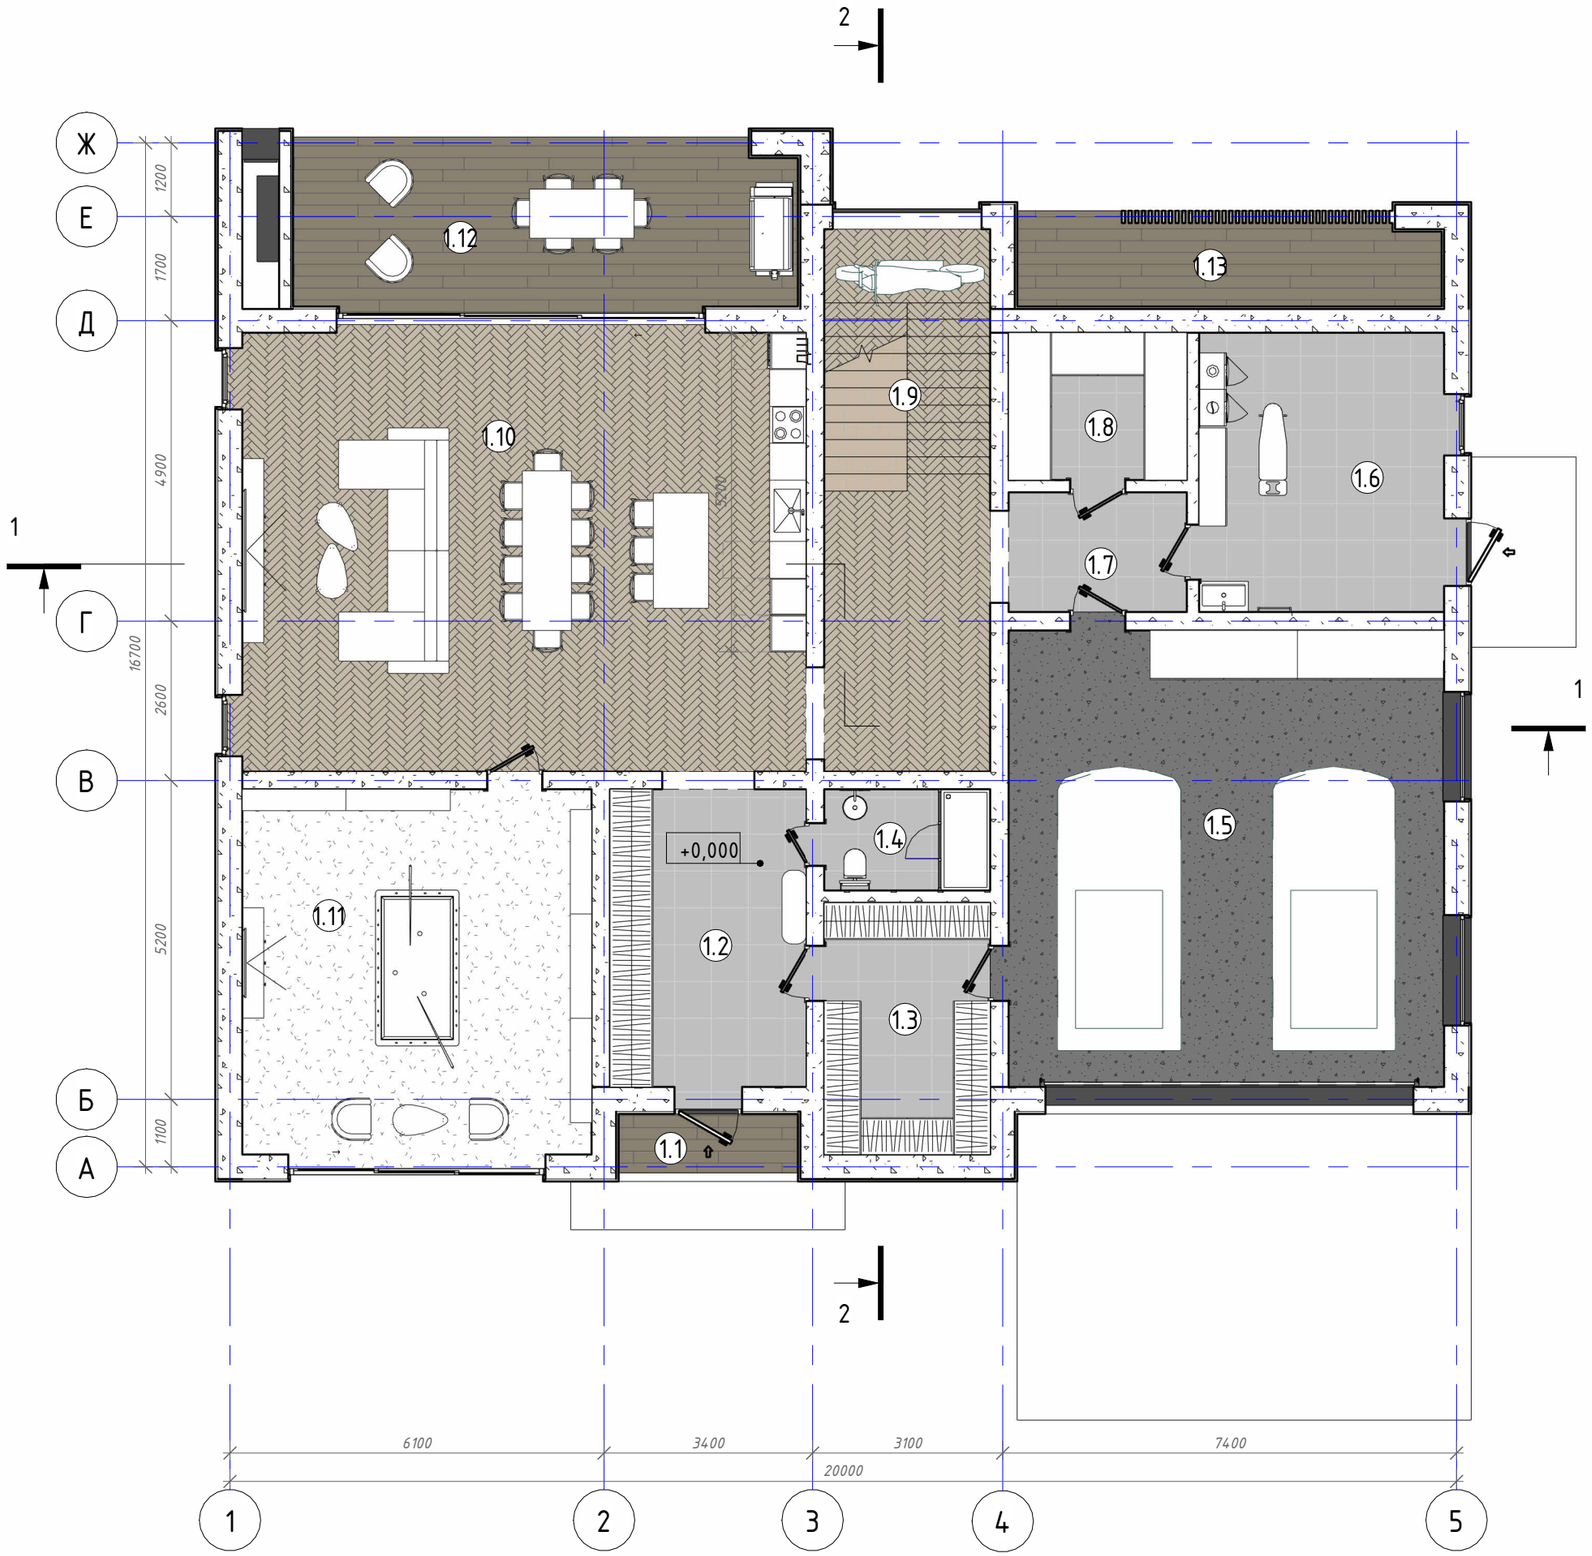


Экспликация помещений		
№	Наименование	S, м²
1 этаж		
1.1	Крыльцо	3,10
1.2	Прихожая	15,52
1.3	Тамбур	11,07
1.4	С/у	4,46
1.5	Гараж	52,90
1.6	Топочная	18,20
1.7	Тамбур	5,66
1.8	Кладовая	6,96
1.9	Лестница-холл	23,90
1.10	Кухня-гостиная	65,78
1.11	Бильярдная	33,92
1.12	Терраса	23,16
1.13	Хозблок	10,10
		274,70
2 этаж		
2.1	Лестница-холл	25,11
2.2	Балкон	13,34
2.3	Спальня	19,40
2.4	Кабинет	18,43
2.5	Спальня	19,40
2.6	Гардеробная	13,20
2.7	Спальня	18,20
2.8	С/у	9,20
2.9	С/у	6,67
2.10	Балкон	11,01
		153,96
Общая площадь		428,66

Архитектор	Харламов П.А.	
Архитектор	Райтер С.С.	
Заказчик	_____	

Двухэтажный индивидуальный жилой дом с баней.
Альбом 2. Эскизный проект дома.

Дом.Планировочное решение. 1 этаж.	Лист	Листов
	4	21

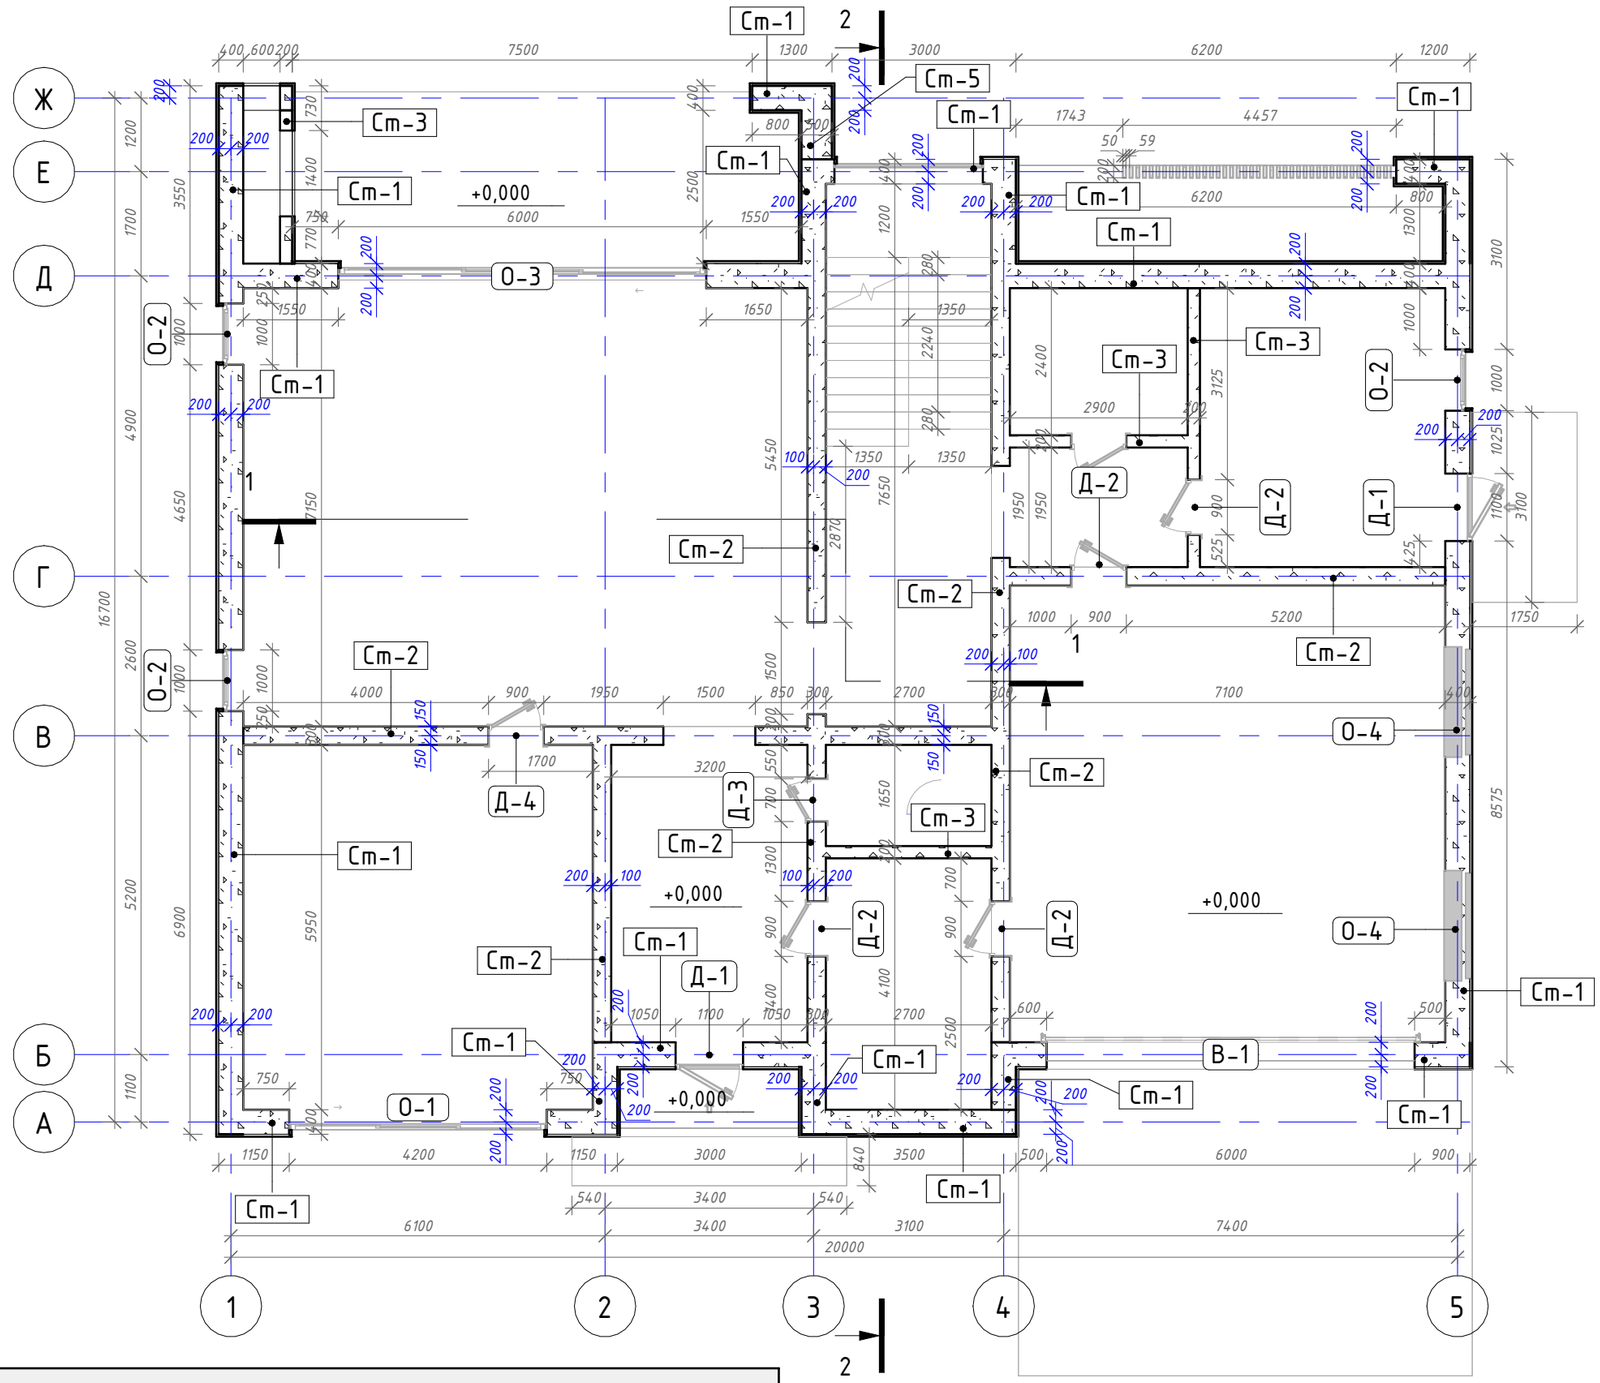

Экспликация помещений 1 этажа		
№	Наименование	S, м²
1 этаж		
1.1	Крыльцо	3,10
1.2	Прихожая	15,52
1.3	Тамбур	11,07
1.4	С/у	4,46
1.5	Гараж	52,90
1.6	Топочная	18,20
1.7	Тамбур	5,66
1.8	Кладовая	6,96
1.9	Лестница-холл	23,90
1.10	Кухня-гостиная	65,78
1.11	Бильярдная	33,92
1.12	Терраса	23,16
1.13	Хозблок	10,10
		274,70
Общая площадь		274,70

Спецификация стен из газобетона

Марка	Тип	Объем	Площадь
Ст-1	Газобетонный блок D500 t400мм	169,32 м³	424,48 м²
Ст-2	Газобетонный блок D500 t300мм	74,72 м³	249,07 м²
Ст-3	Газобетонный блок D500 t200 мм	23,81 м³	119,06 м²
Ст-5	Газобетонный блок D500 t500мм	1,38 м³	2,76 м²
Общий итог: 53		269,24 м³	795,37 м²

Монолитный фундамент (ребро фундаментной плиты 300мм*850h и плита t=200мм.) V=85куб.м.
Монолитное перекрытие 1 этажа t=200мм. V=69,5куб.м.
Монолитное перекрытие 2 этажа t=200мм. V=57 куб.м.

Примечание:
1. Все объемы даны предварительно и уточняются на следующих стадиях проектирования

Спецификация окон

Марка	Высота	Ширина	Описание	Количество
О-1	3000	4200	Окно раздвижное 3 створки	1
О-2	3000	1000	Поворотно-откидное	3
О-3	3000	6000	Окно раздвижное 3 створки	1
О-4	750	1800	Откидное	4
О-6	2500	3000	Окно прямоугольное трёхстворчатое	3
О-8	3000	3000	Окно раздвижное 3 створки	1
О-9	3000	1000	Поворотно-откидное	3
О-10	3000	6000	Окно прямоугольное трёхстворчатое	1
О-13	3000	2420	Окно глухое	2
Общий итог: 19				


Ведомость дверей

Марка	Описание	Габариты проёма, мм	Откр-е	Кол-во
В-1	Ворота	6000x3000		1
Д-1	Дверь входная одностворчатая с остеклением сверху	1100x3000	Левое Наружу	2
Д-2	Дверь межкомнатная одностворчатая	900x2370	Левое Наружу	4
Д-3	Дверь межкомнатная одностворчатая	700x2370	Правое Наружу	1
Д-4	Дверь межкомнатная одностворчатая	900x2370	Правое Наружу	2

Архитектор	Харламов П.А.	
Архитектор	Райтер С.С.	
Заказчик	_____	

Двухэтажный индивидуальный жилой дом с баней.
Альбом 2. Эскизный проект дома.

Дом.Планировочное решение. 1 этаж. Размеры.	Лист	Листов
	5	21

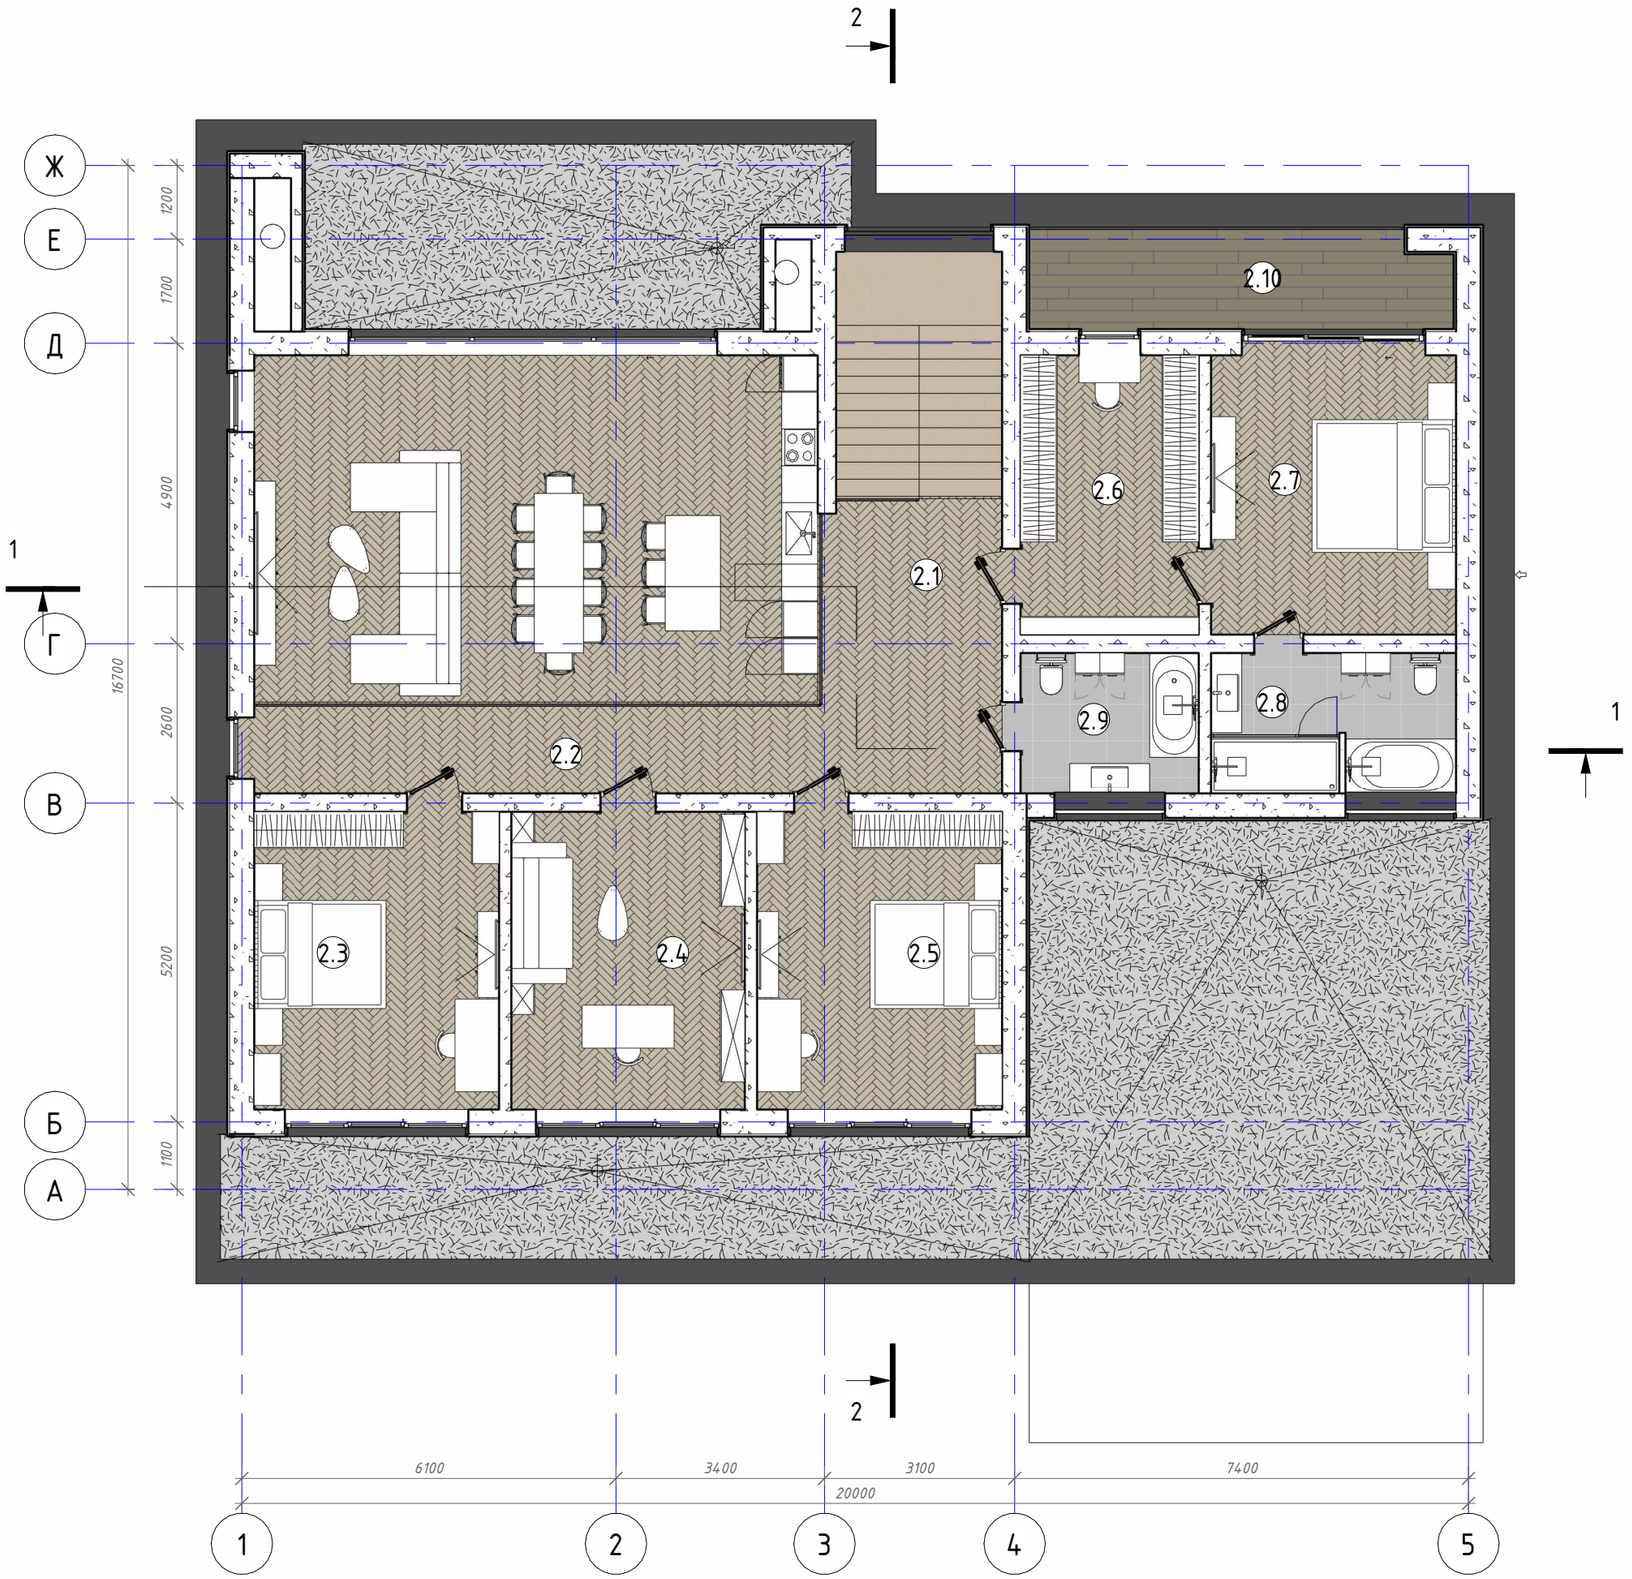


Экспликация помещений		
№	Наименование	S, м²
1 этаж		
1.1	Крыльцо	3,10
1.2	Прихожая	15,52
1.3	Тамбур	11,07
1.4	С/у	4,46
1.5	Гараж	52,90
1.6	Топочная	18,20
1.7	Тамбур	5,66
1.8	Кладовая	6,96
1.9	Лестница-холл	23,90
1.10	Кухня-гостиная	65,78
1.11	Бильярдная	33,92
1.12	Терраса	23,16
1.13	Хозблок	10,10
		274,70
2 этаж		
2.1	Лестница-холл	25,11
2.2	Балкон	13,34
2.3	Спальня	19,40
2.4	Кабинет	18,43
2.5	Спальня	19,40
2.6	Гардеробная	13,20
2.7	Спальня	18,20
2.8	С/у	9,20
2.9	С/у	6,67
2.10	Балкон	11,01
		153,96
Общая площадь		428,66

Архитектор	Харламов П.А.	
Архитектор	Райтер С.С.	
Заказчик	_____	

Двухэтажный индивидуальный жилой дом с баней.
Альбом 2. Эскизный проект дома.

Дом.Планировочное решение. 2 этаж.	Лист	Листов
	6	21

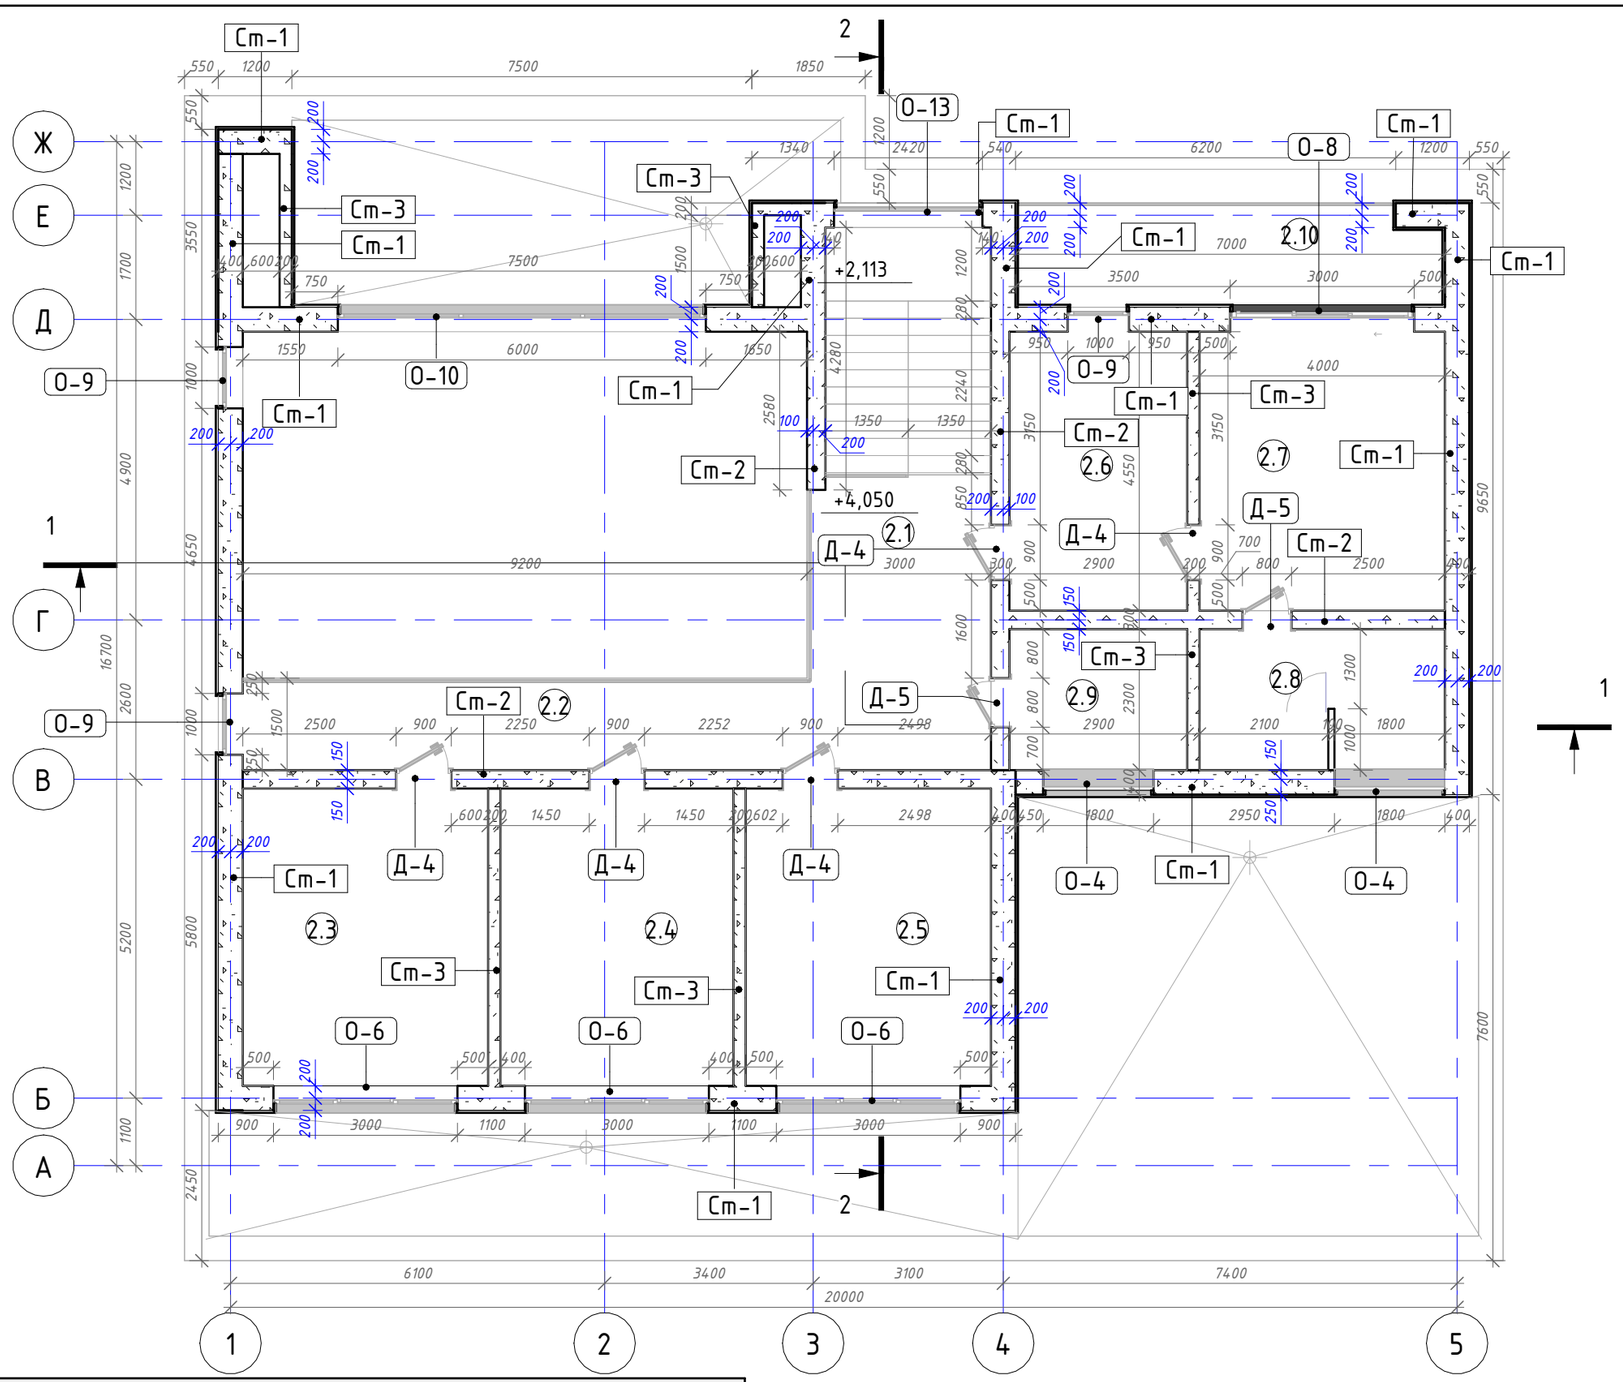

Экспликация помещений 2 этажа		
№	Наименование	S, м²
2 этаж		
2.1	Лестница-холл	25,11
2.2	Балкон	13,34
2.3	Спальня	19,40
2.4	Кабинет	18,43
2.5	Спальня	19,40
2.6	Гардеробная	13,20
2.7	Спальня	18,20
2.8	С/у	9,20
2.9	С/у	6,67
2.10	Балкон	11,01
		153,96
Общая площадь		153,96

Спецификация стен из газобетона

Марка	Тип	Объем	Площадь
Ст-1	Газобетонный блок D500 t400мм	169,32 м³	424,48 м²
Ст-2	Газобетонный блок D500 t300мм	74,72 м³	249,07 м²
Ст-3	Газобетонный блок D500 t200 мм	23,81 м³	119,06 м²
Ст-5	Газобетонный блок D500 t500мм	1,38 м³	2,76 м²
Общий итог: 53		269,24 м³	795,37 м²

Монолитный фундамент (ребро фундаментной плиты 300мм*850h и плита t=200мм.) V=85куб.м.
Монолитное перекрытие 1 этажа t=200мм. V=69,5куб.м.
Монолитное перекрытие 2 этажа t=200мм. V=57 куб.м.

Примечание:
1. Все объемы даны предварительно и уточняются на следующих стадиях проектирования

Спецификация окон

Марка	Высота	Ширина	Описание	Количество
О-1	3000	4200	Окно раздвижное 3 створки	1
О-2	3000	1000	Поворотно-откидное	3
О-3	3000	6000	Окно раздвижное 3 створки	1
О-4	750	1800	Откидное	4
О-6	2500	3000	Окно прямоугольное трёхстворчатое	3
О-8	3000	3000	Окно раздвижное 3 створки	1
О-9	3000	1000	Поворотно-откидное	3
О-10	3000	6000	Окно прямоугольное трёхстворчатое	1
О-13	3000	2420	Окно глухое	2
Общий итог: 19				


Ведомость дверей

Марка	Описание	Габариты проёма, мм	Откр-е	Кол-во
В-1	Ворота	6000x3000		1
Д-1	Дверь входная одностворчатая с остеклением сверху	1100x3000	Левое Наружу	2
Д-2	Дверь межкомнатная одностворчатая	900x2370	Левое Наружу	4
Д-3	Дверь межкомнатная одностворчатая	700x2370	Правое Наружу	1
Д-4	Дверь межкомнатная одностворчатая	900x2370	Правое Наружу	2

Архитектор	Харламов П.А.	
Архитектор	Райтер С.С.	
Заказчик	_____	

Двухэтажный индивидуальный жилой дом с баней.
Альбом 2. Эскизный проект дома.

Дом.Планировочное решение. 2 этаж. Размеры.	Лист	Листов
	7	21

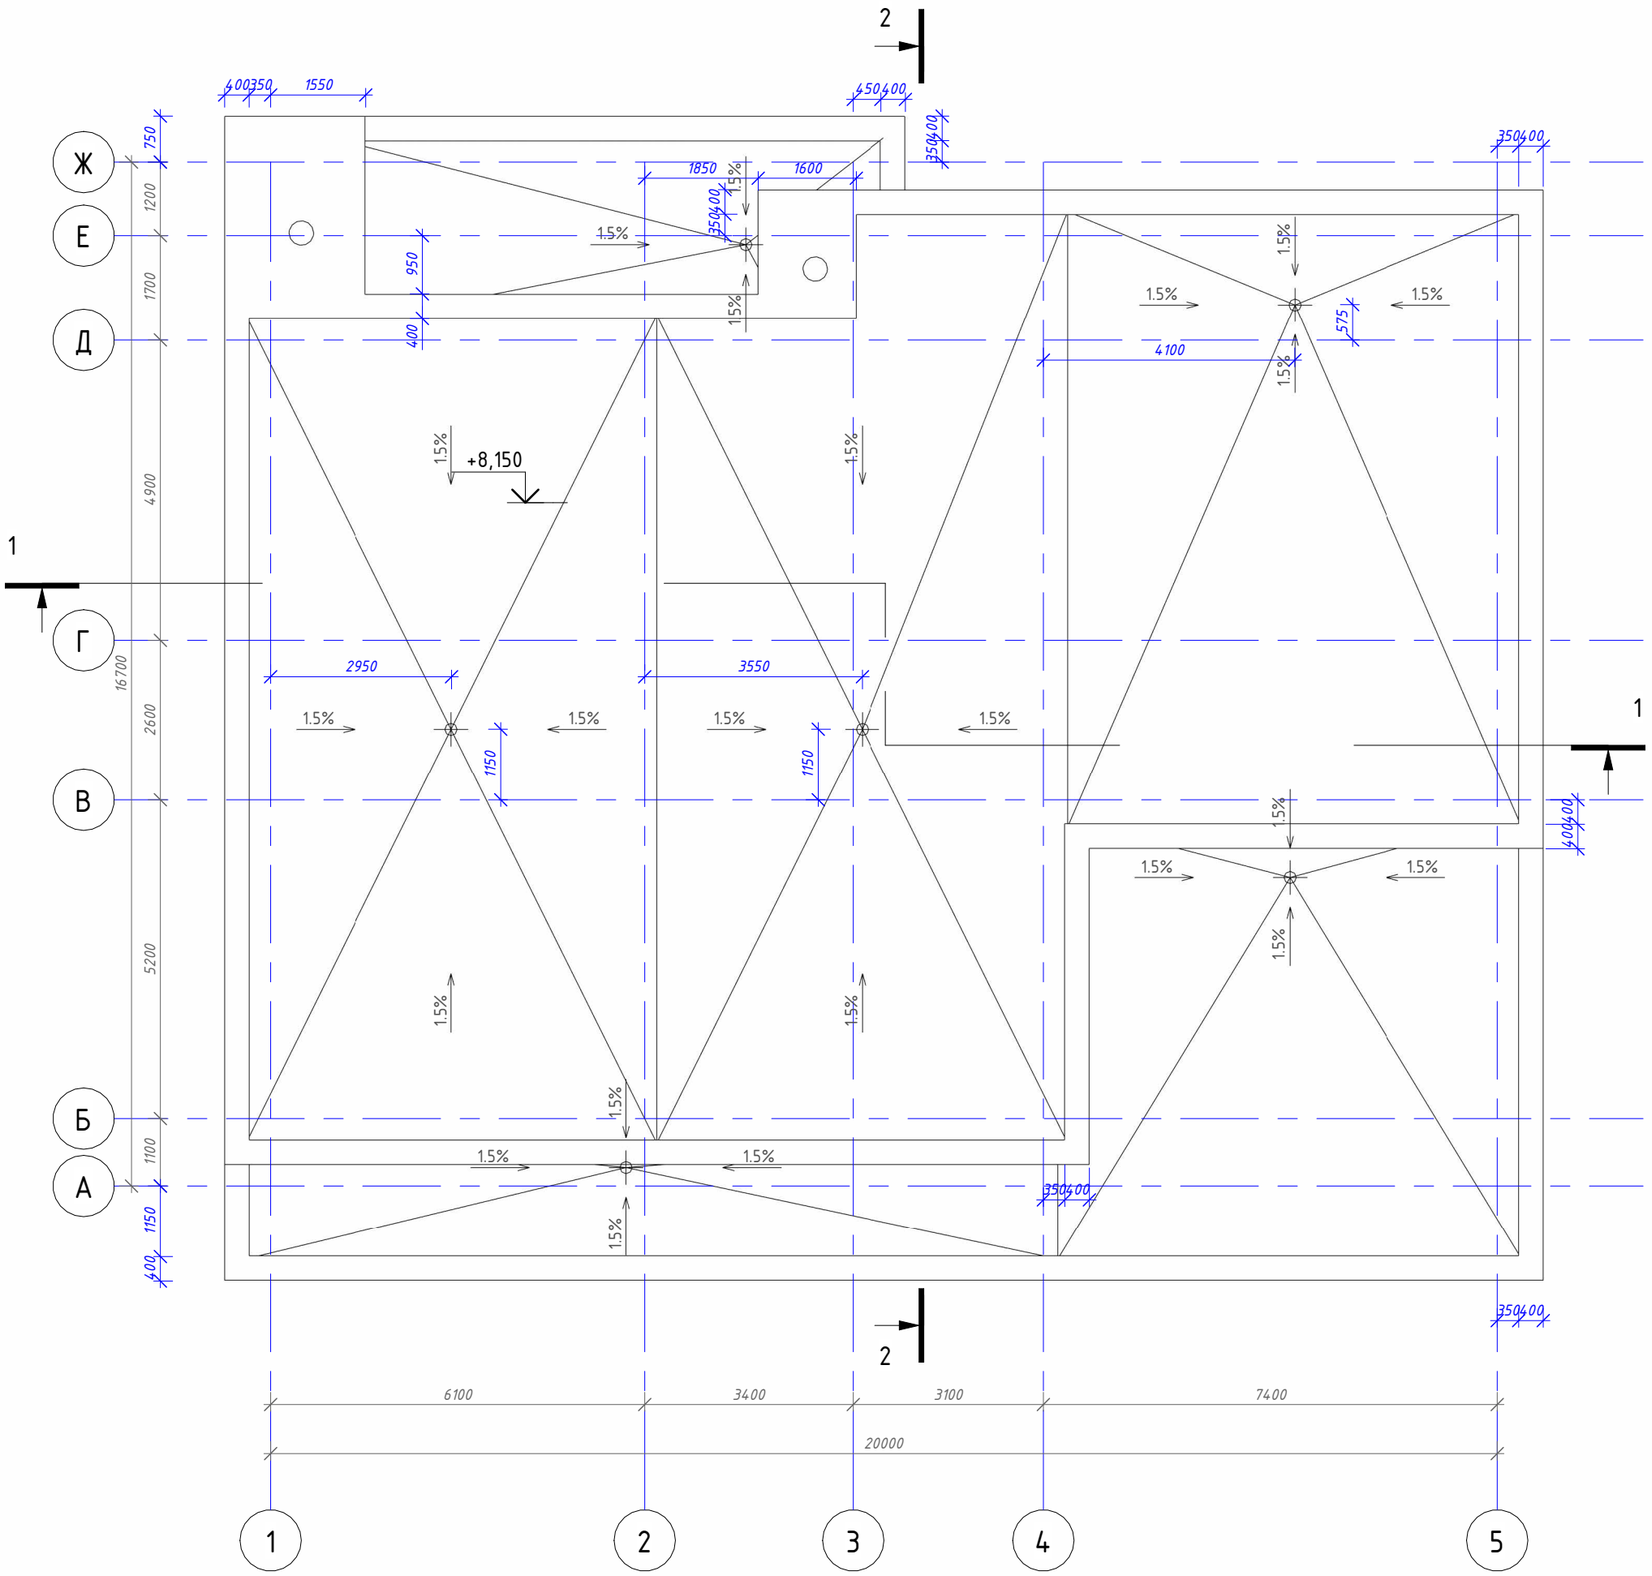

Площадь кровли составляет 371кв.м.


Архитектор	Харламов П.А.	
Архитектор	Райтер С.С.	
Заказчик	_____	

Двухэтажный индивидуальный жилой дом с баней.
Альбом 2. Эскизный проект дома.

Дом. План кровли.	Лист	Листов
	8	21


Разрез 1-1

1 : 100

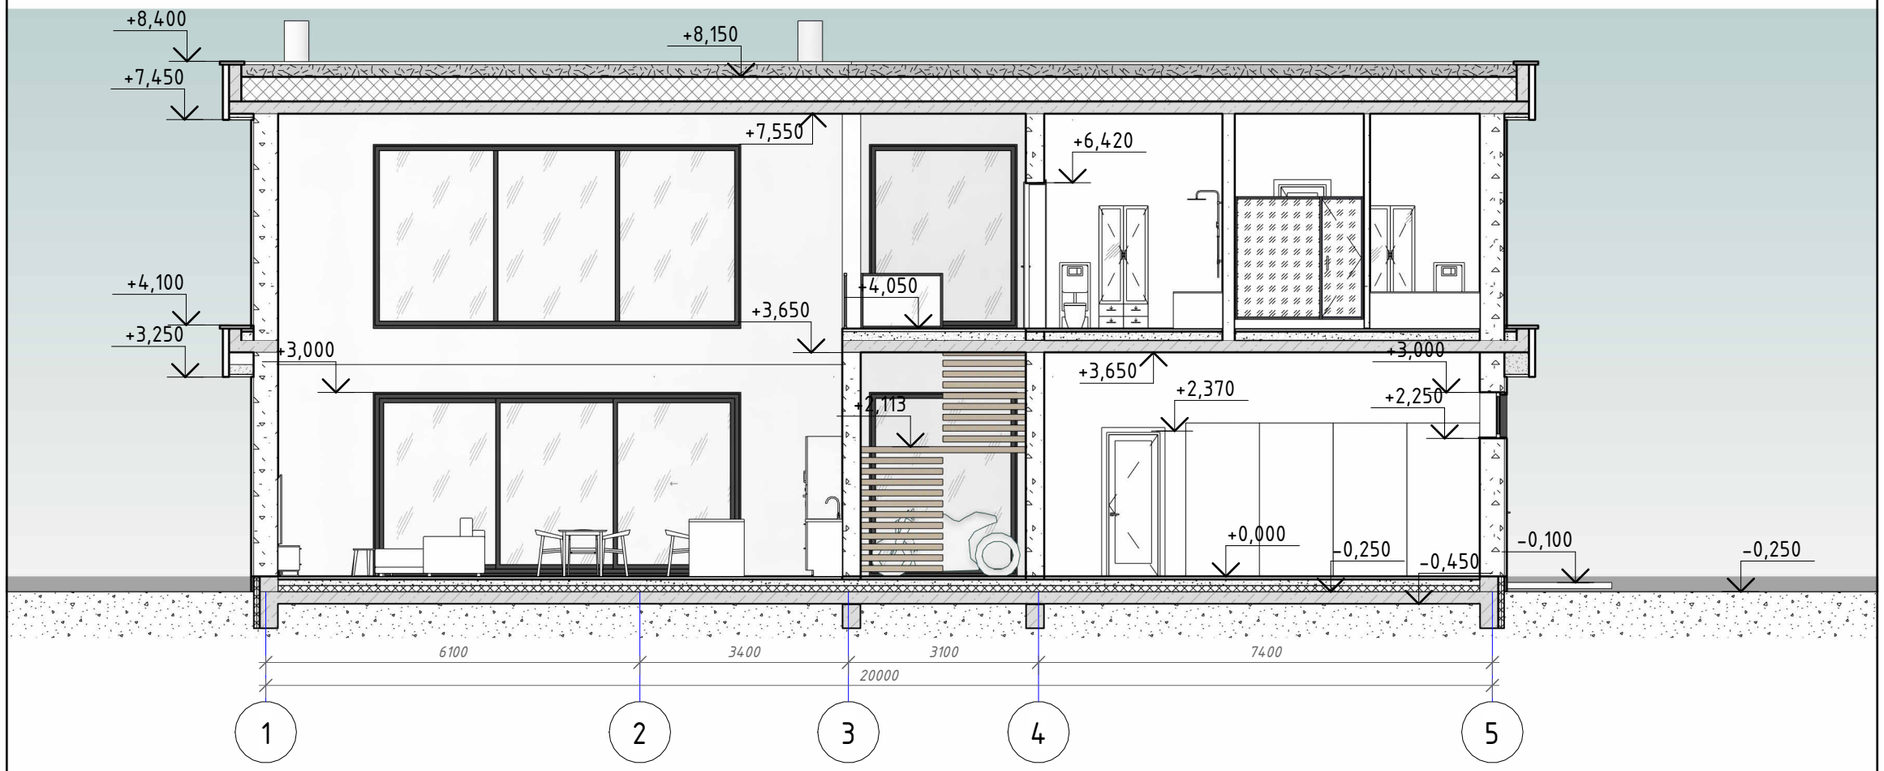

Разрез 2-2

1 : 100

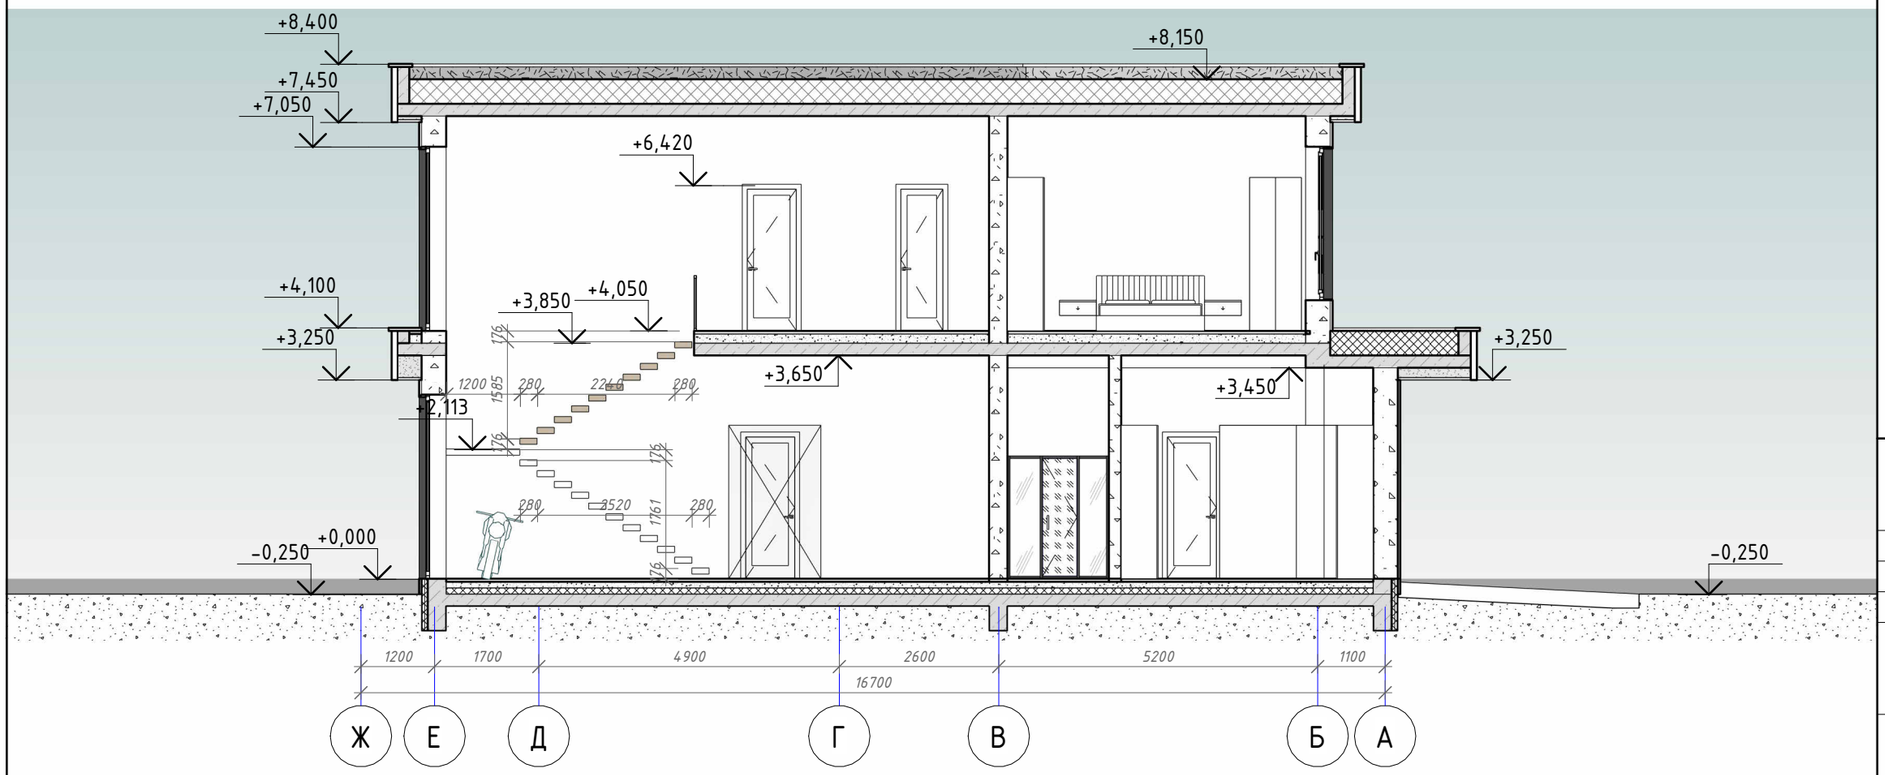

Архитектор	Харламов П.А.	
Архитектор	Райтер С.С.	
Заказчик	_____	

Двухэтажный индивидуальный жилой дом с баней.

Альбом 2. Эскизный проект дома.

Дом. Разрез 1-1, 2-2

Лист	Листов
9	21





Ведомость материалов фасадов

Марка	Изображение	Площадь	Описание
М-1		319,79 м²	Штукатурка декоративная мраморная Bayramix EcoStone 774
М-1.1	RAL7024 GRAPHITE GREY	21,63 м²	Штукатурка декоративная мраморная Bayramix EcoStone Ral7024
М-2		80,83 м²	Планкен
М-3		68,51 м²	Искусственный камень White Hills Рутланд цвет 603-00
М-4	RAL7024 GRAPHITE GREY	135,79 м²	Отделка карниза Ral7024
М-5		18,79 м²	Крупноформатный керамогранит Lifebrick Mountain Black new
		645,34 м²	


Рамы окон, наружных дверей, ворот и декоративных элементов Ral7024


Архитектор	Харламов П.А.	
Архитектор	Райтер С.С.	
Заказчик		

Двухэтажный индивидуальный жилой дом с баней.
Альбом 2. Эскизный проект дома.

Дом. Фасад 1-5, 5-1

Лист	Листов
10	21

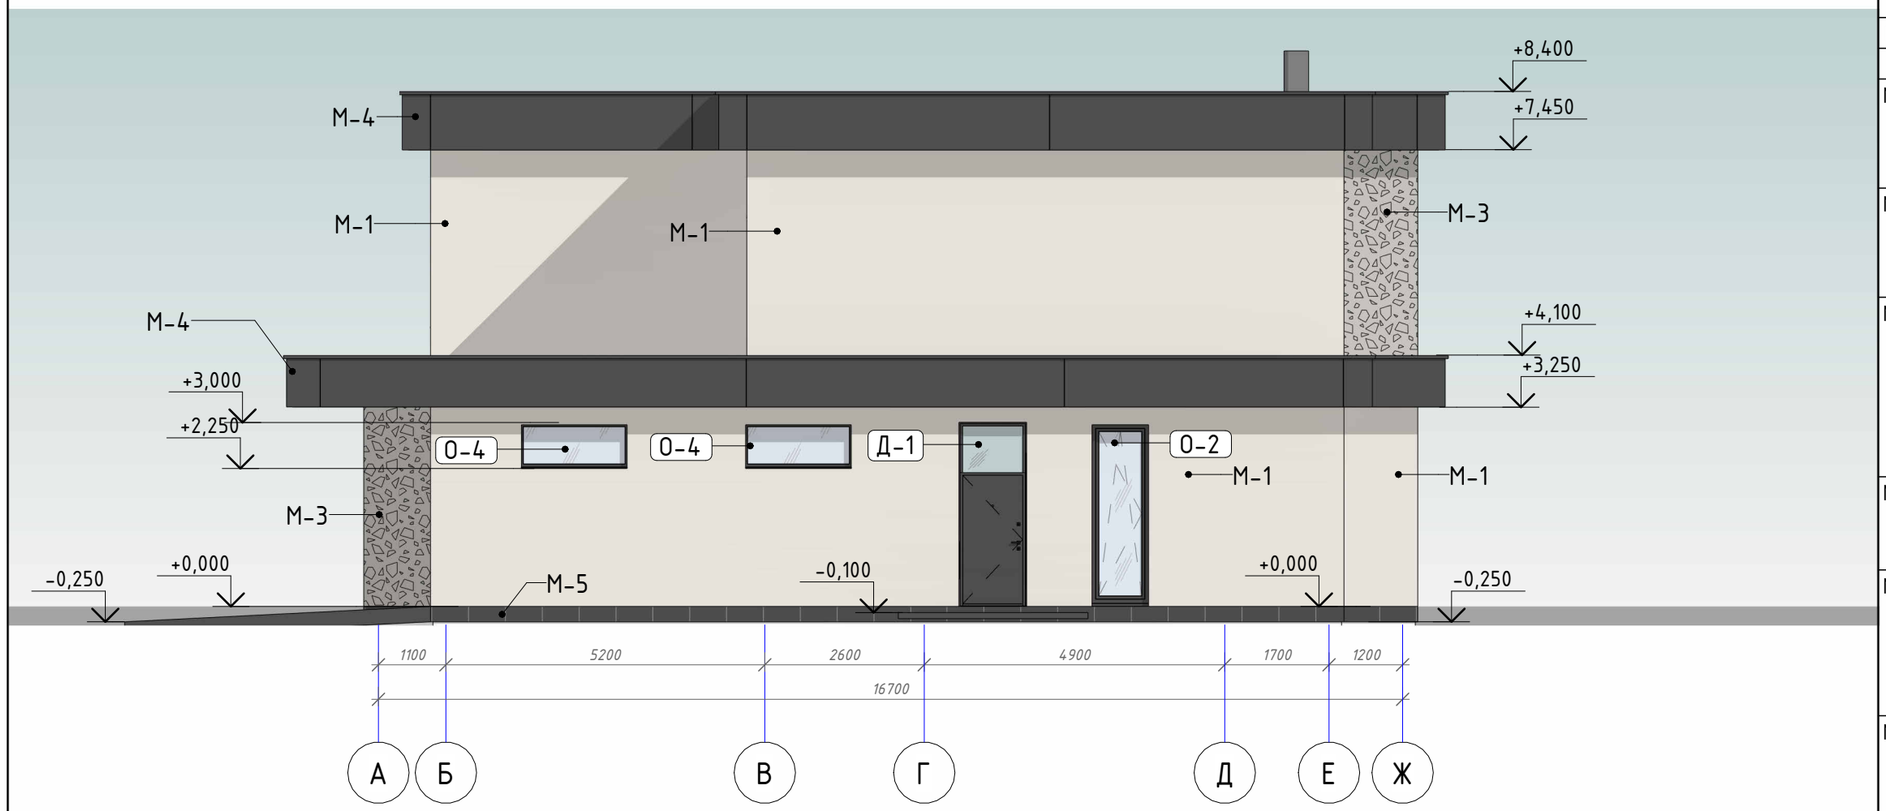

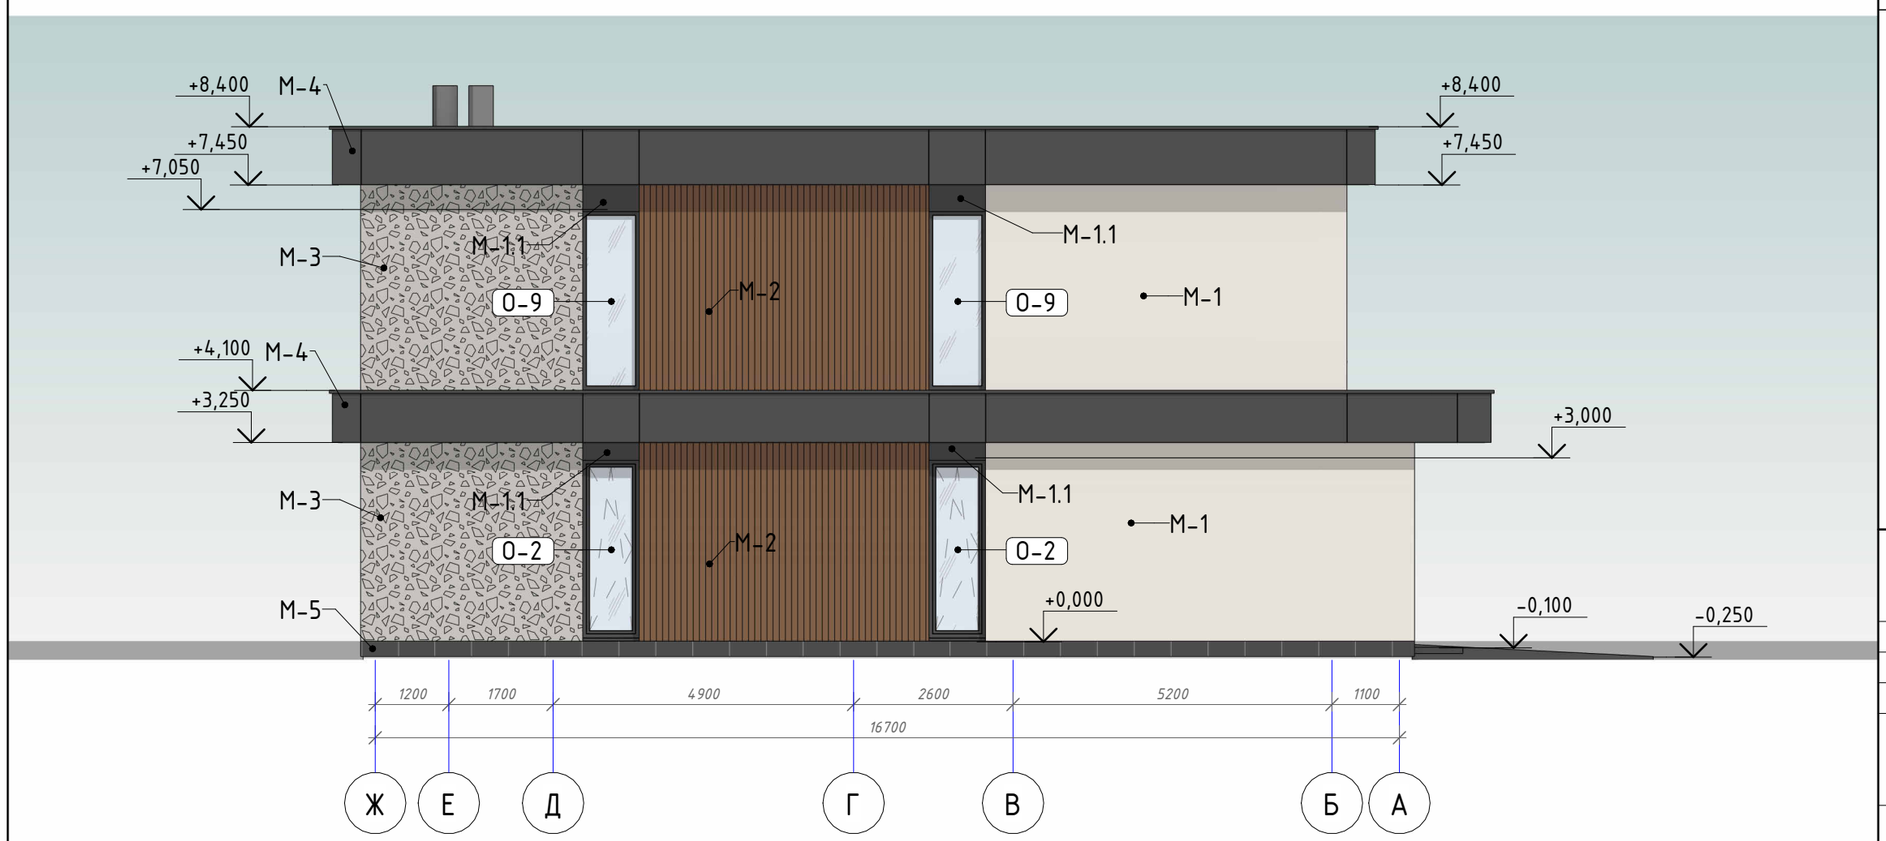

Ведомость материалов фасадов

Марка	Изображение	Площадь	Описание
М-1		319,79 м²	Штукатурка декоративная мраморная Bayramix EcoStone 774
М-1.1	RAL7024 GRAPHITE GREY	21,63 м²	Штукатурка декоративная мраморная Bayramix EcoStone Ral7024
М-2		80,83 м²	Планкен
М-3		68,51 м²	Искусственный камень White Hills Рутланд цвет 603-00
М-4	RAL7024 GRAPHITE GREY	135,79 м²	Отделка карниза Ral7024
М-5		18,79 м²	Крупноформатный керамогранит Lifebrick Mountain Black new
		645,34 м²	

Рамы окон, наружных дверей, ворот и декоративных элементов Ral7024

Архитектор	Харламов П.А.	
Архитектор	Райтер С.С.	
Заказчик	_____	

Двухэтажный индивидуальный жилой дом с баней.
Альбом 2. Эскизный проект дома.

Дом. Фасад А-Ж, Ж-А

Лист	Листов
11	21



Архитектор	Харламов П.А.	
Архитектор	Райтер С.С.	
Заказчик	_____	

Двухэтажный индивидуальный жилой дом с баней.

Альбом 2. Эскизный проект дома.

Дом. 3D Вид 1

Лист	Листов
12	21



Архитектор	Харламов П.А.	
Архитектор	Райтер С.С.	
Заказчик	_____	

Двухэтажный индивидуальный жилой дом с баней.
Альбом 2. Эскизный проект дома.

	Лист	Листов
Дом. 3D Вид 2	13	21



Архитектор	Харламов П.А.	
Архитектор	Райтер С.С.	
Заказчик	_____	

Двухэтажный индивидуальный жилой дом с баней.

Альбом 2. Эскизный проект дома.

	Лист	Листов
Дом. 3D Вид 3	14	21



Архитектор	Харламов П.А.	
Архитектор	Райтер С.С.	
Заказчик	_____	

Двухэтажный индивидуальный жилой дом с баней.
Альбом 2. Эскизный проект дома.

	Лист	Листов
Дом. 3D Вид 4	15	21