

## Топочная 1.6. План. М 1:50

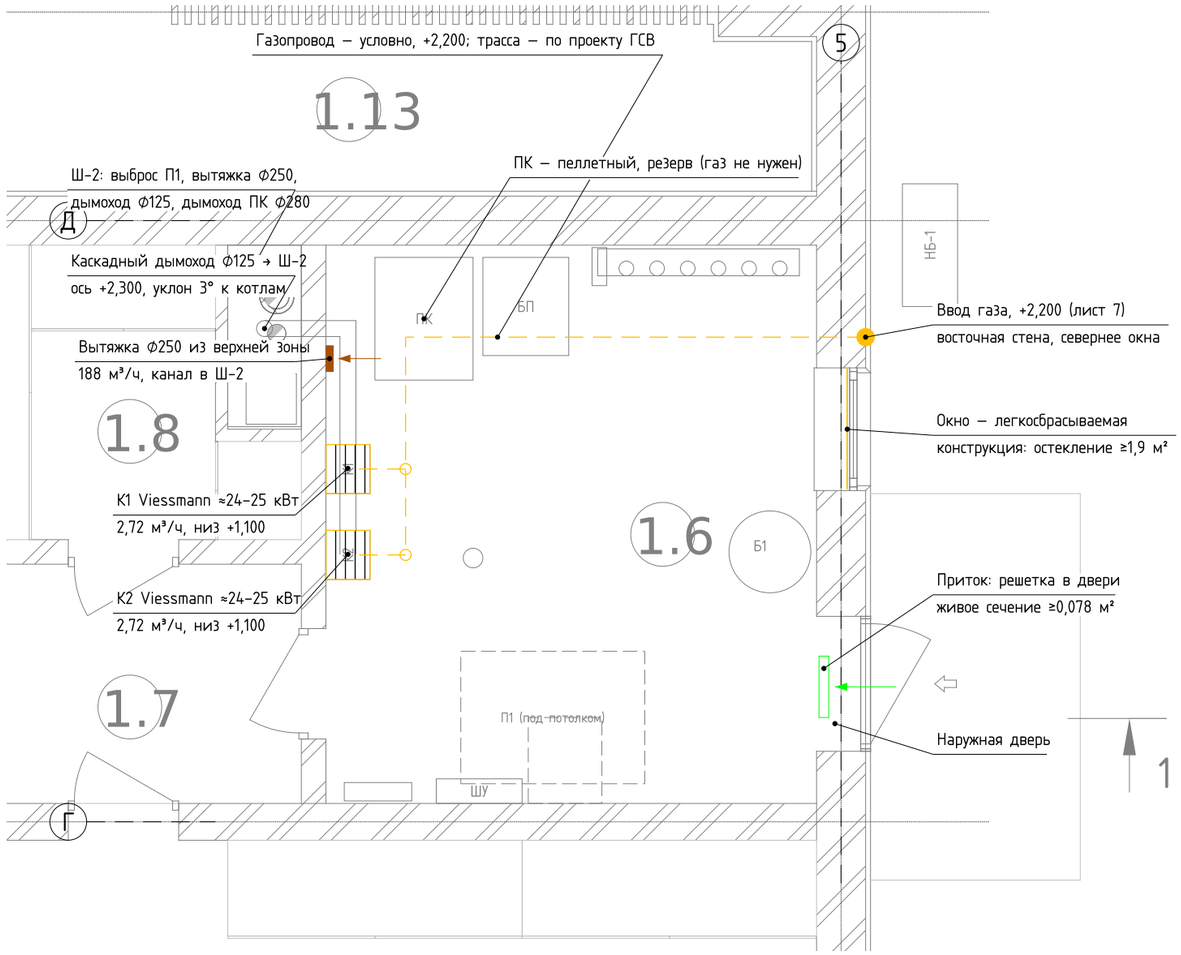


## Развертка по западной стене (вид А). М 1:50

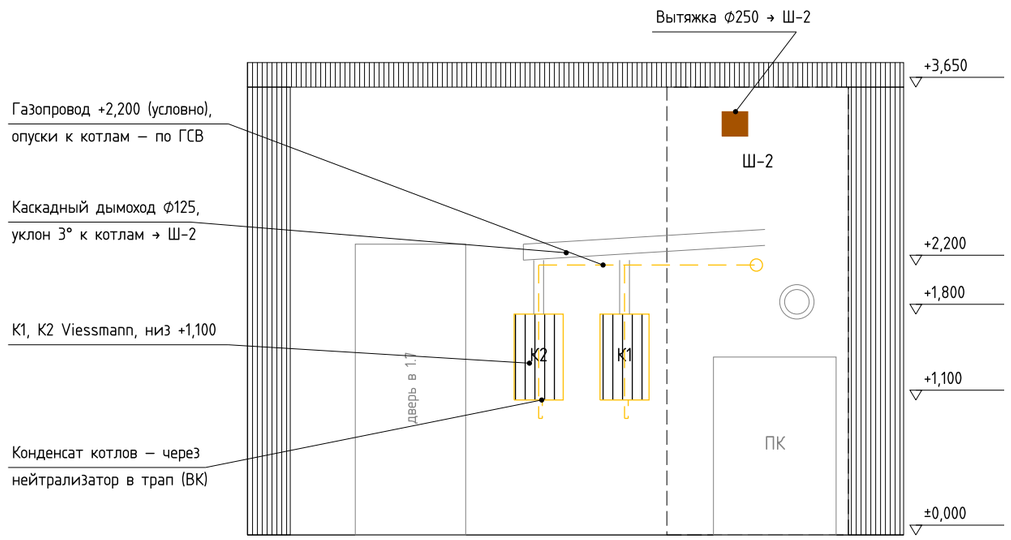


## Потребители газа

| Поз. | Марка | Потребитель газа | Ном. мощность, кВт | Расход газа, м³/ч | Примечание |
|---|---|---|---|---|---|
| 1 | K1 | Котел газовый настенный конденсационный одноконтурный Viessmann (напр. Vitodens 200-W), каскадное управление | 24–25 | 2,72 | уточняется по паспорту типоразмера |
| 2 | K2 | То же | 24–25 | 2,72 | то же |
| | | Итого: каскад K1 + K2, одновременная работа | 48 | 5,43 | уточняется по паспорту |

## Примечания

1. Задание разделу ГСВ на газоснабжение котлов отопления и ГВС по И05.09.26-ОВ. Газ природный; расход — при низшей теплоте сгорания 33,5 МДж/м³ (9,3 кВт·ч/м³) и КПД 95 %: 5,43 м³/ч при 2×24 кВт — уточняется по паспорту выбранного типоразмера Viessmann (решение Заказчика).
2. Ввод газопровода — в восточной стене топочной севернее окна, на отметке +2,200 (лист 7 ОВ). Разводка внутри показана условно (по модели котельной И05.09.26-ТМ): открыто на +2,200 от ввода на запад и вдоль котлов в 0,65 м от западной стены, опуски к котлам до +0,950 с подключением снизу. Трасса, отключающие устройства на вводе и перед котлами, счетчик газа и его место — по проекту ГСВ и ТУ.
3. Сигнализатор загазованности с клапаном-отсекателем на вводе — по проекту ГСВ; электропитание — ТЗ-2 (ЭОМ), поз. 18.
4. Воздух на горение — из помещения топочной (67 м³/ч при работе каскада). Приток наружного воздуха — решетка в нижней части наружной двери, живое сечение не менее 0,078 м², 282 м³/ч (вытяжка 188 м³/ч + воздух на горение).
5. Вытяжка — естественная, из верхней зоны топочной каналом Ф250 в шахте Ш-2, 188 м³/ч (3 обмена в час).
6. Отвод продуктов сгорания — общий каскадный дымоход Ф125 системы производителя котлов: коллектор на +2,300 с уклоном 3° к котлам, ввод в канал шахты Ш-2 (вместо двух Ф150 по модели АР), выход выше кровли — по АР. Подбор и расчет — по паспорту котлов Viessmann. Конденсат — через нейтрализатор в трап (ТЗ-3, ВК).
7. Топочная 1.6: объем ≈63 м³, до низа плиты перекрытия 3,65 м, выход наружу через дверь в восточной стене. Легкосбрасываемая конструкция — окно в восточной стене: площадь остекления не менее 0,03 м² на 1 м³ объема (≈1,9 м²) — проверить разделом АР.
8. В топочной также установлен пеллетный котел ПК ≈50 кВт (резерв, газом не питается) с отдельным дымоходом Ф280 в шахте Ш-2 — учесть в проекте ГСВ.
9. Отметки — от ±0,000 (чистый пол 1 этажа). Подложка — АР03 (выгрузка из Revit 19.10.2026); оборудование — по листам 7, 8 И05.09.26-ОВ.

## Топочная 1.6 — исходные данные для ГСВ

| Показатель | Значение |
|---|---|
| Объем топочной 1.6 / высота до низа плиты | ≈63 м³ / 3,65 м |
| Газовые котлы: число, мощность | 2 × 24 кВт (каскад, 48 кВт) |
| Расход газа (уточнить по паспорту) | 5,43 м³/ч |
| Воздух на горение газа (из помещения) | 67 м³/ч |
| Вытяжка естественная, канал Ф250 в Ш-2 | 188 м³/ч |
| Приток: решетка в наружной двери | 282 м³/ч, ≥0,078 м² |
| Дымоход котлов | каскадный Ф125, канал в Ш-2 |
| Ввод газа | восточная стена, +2,200 |
| Остекление окна (ЛСК), требуется | ≥1,9 м² — проверить АР |
| Выход наружу | дверь в восточной стене |

| Изм. | Кол.уч | Лист | № док | Подп. | Дата | И05.09.26-ОВ.ТЗ-4 | | | |
|---|---|---|---|---|---|---|---|---|---|
| | | | | | | Двухэтажный индивидуальный жилой дом с баней. Московская область, кадастровый номер участка 50:08:0050209:1600 | | | |
| Разраб. | | | | | | Отопление, вентиляция и кондиционирование | Стадия | Лист | Листов |
| Пров. | | | | | | | Р | 1 | 1 |
| Н.контр. | | | | | | Задание на газоснабжение (ГСВ). Топочная 1.6 | | | |
| ГИП | | | | | | | | | |

Согласовано | Взам.инв.№ | Подпись и дата | Инв.№ подл.

Копировал | Формат А3