


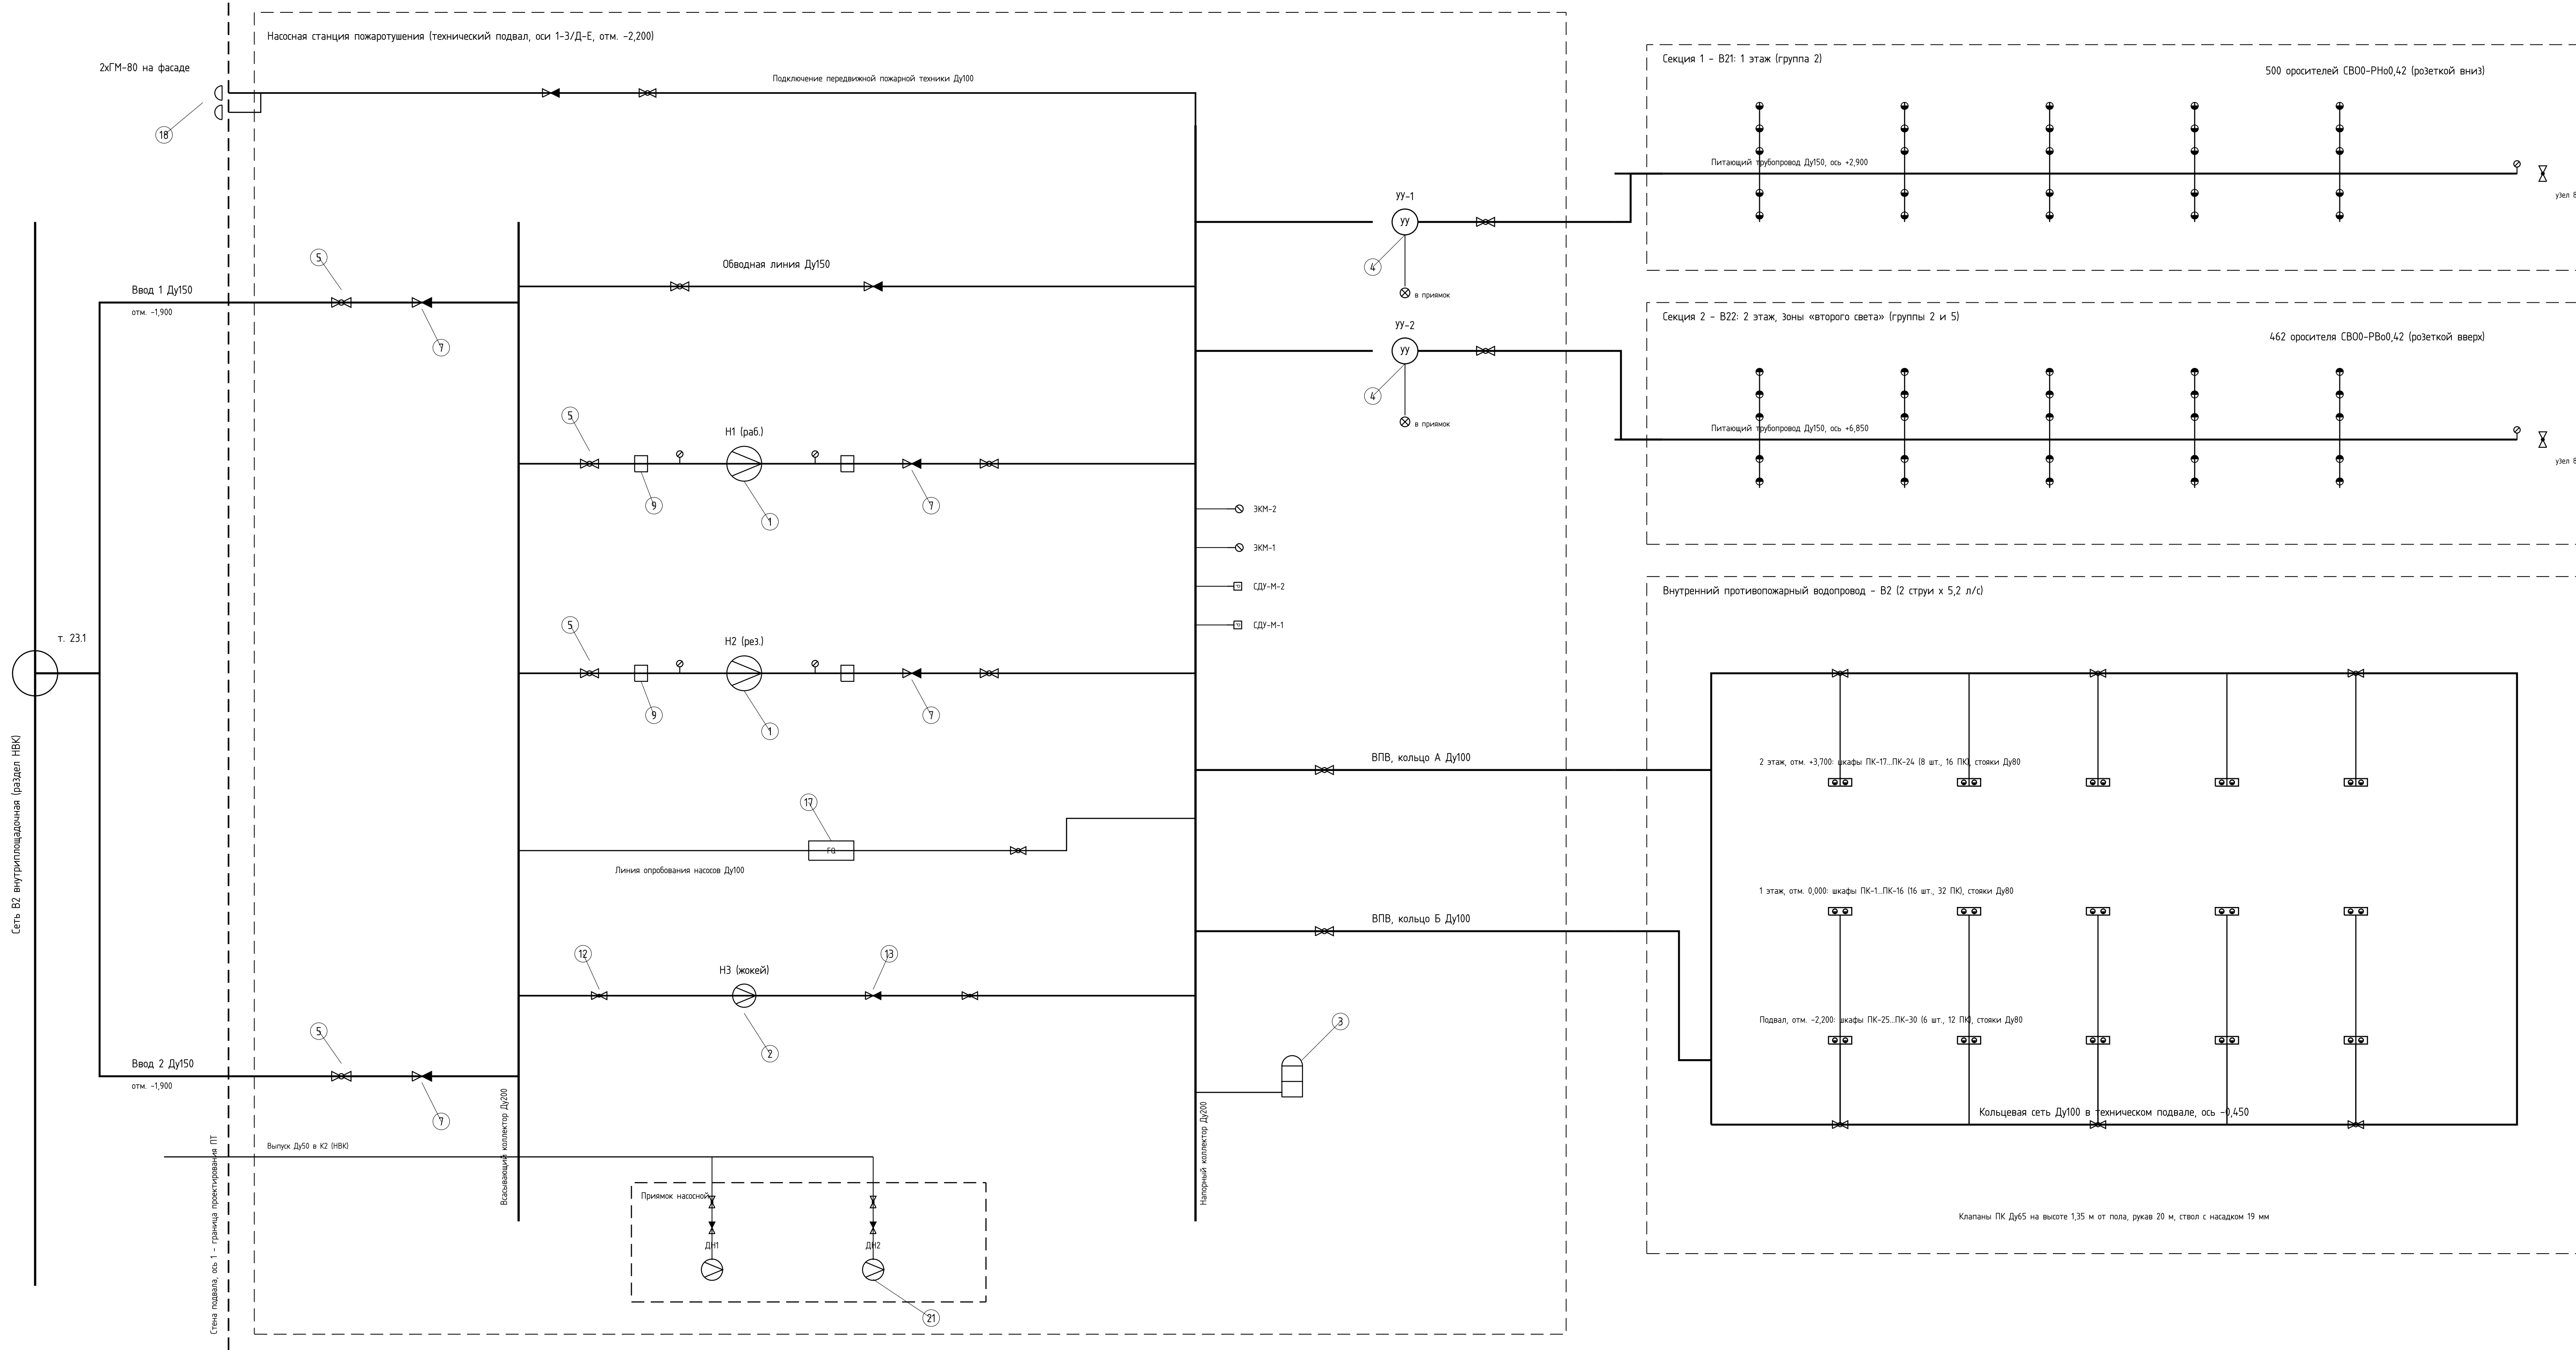


Показатель	Значение
Расчётный расход АУПТ (табл. 6.1 СП 485, гр. 2)	30,0 л/с
Расход ВРВ (2 струи)	10,4 л/с
Расход на вводе	40,4 л/с (145 м³/ч)
Требуемый напор на выходе насосной	37,1 м
Давление на вводе 23.1 по ТУ (при 40 л/с)	0,20 МПа
Напор насосов Н1/Н2	21 м
Выделенный расход по ТУ	40 л/с
Продолжительность работы	60 мин
Объём воды на пожаротушение	145,4 м³


- Применения
- Позиции оборудования - по спецификации ПТ.С.
 - Отметки: ось насосов и коллекторов -1,750, выход УУ -0,600, питающие B21 +2,900, B22 +6,850, кольцо B2 -0,450, вводы -1,900.
 - Затворы на вводах, после УУ, на отводе к кольцу ВРВ, на обводной линии и линии опробования - с контролем положения (сигнал на ППК/П «Сириус», пом. 03).
 - Пуск основного насоса - по падению давления в напорном коллекторе (СДУ-М, ЭКМ), от СДУ узлов управления, от кнопок «Пуск насосов» в шкафах ПК; резервный - при невыходе основного на режим. Алгоритм - лист 14.
 - Напор насосов подобран по ТУ от 08.10.2026: 0,20 МПа на вводе 23.1. Расчётный расход 40,4 л/с больше выделенных 40 л/с на 0,4 л/с - требуется корректировка ТУ (п. 4.1 ТУ).

						ОПР-01/24/2024-ДП1-ПТ			
						«Современный коммерческий оптово-продуктовый рынок (ОПР) по адресу: Донецкая область, г. Макеевка, Горняцкий район»			
Изм.	Кол-во	Лист	№ док.	Подп.	Дата	Док-павильон №23, №23.2 Рыба-Мясо. Пожаротушение (ВРВ, АУПТ, АУПП ВРУ)	Стация	Лист	Листов
Разраб.							Р	3	15
Пров.						Схема принципиальная систем B2, B21, B22	000 «Технология»		
Н.контр.									
Гип									


План насосной станции пожаротушения на отм. -2,200 М 1:25

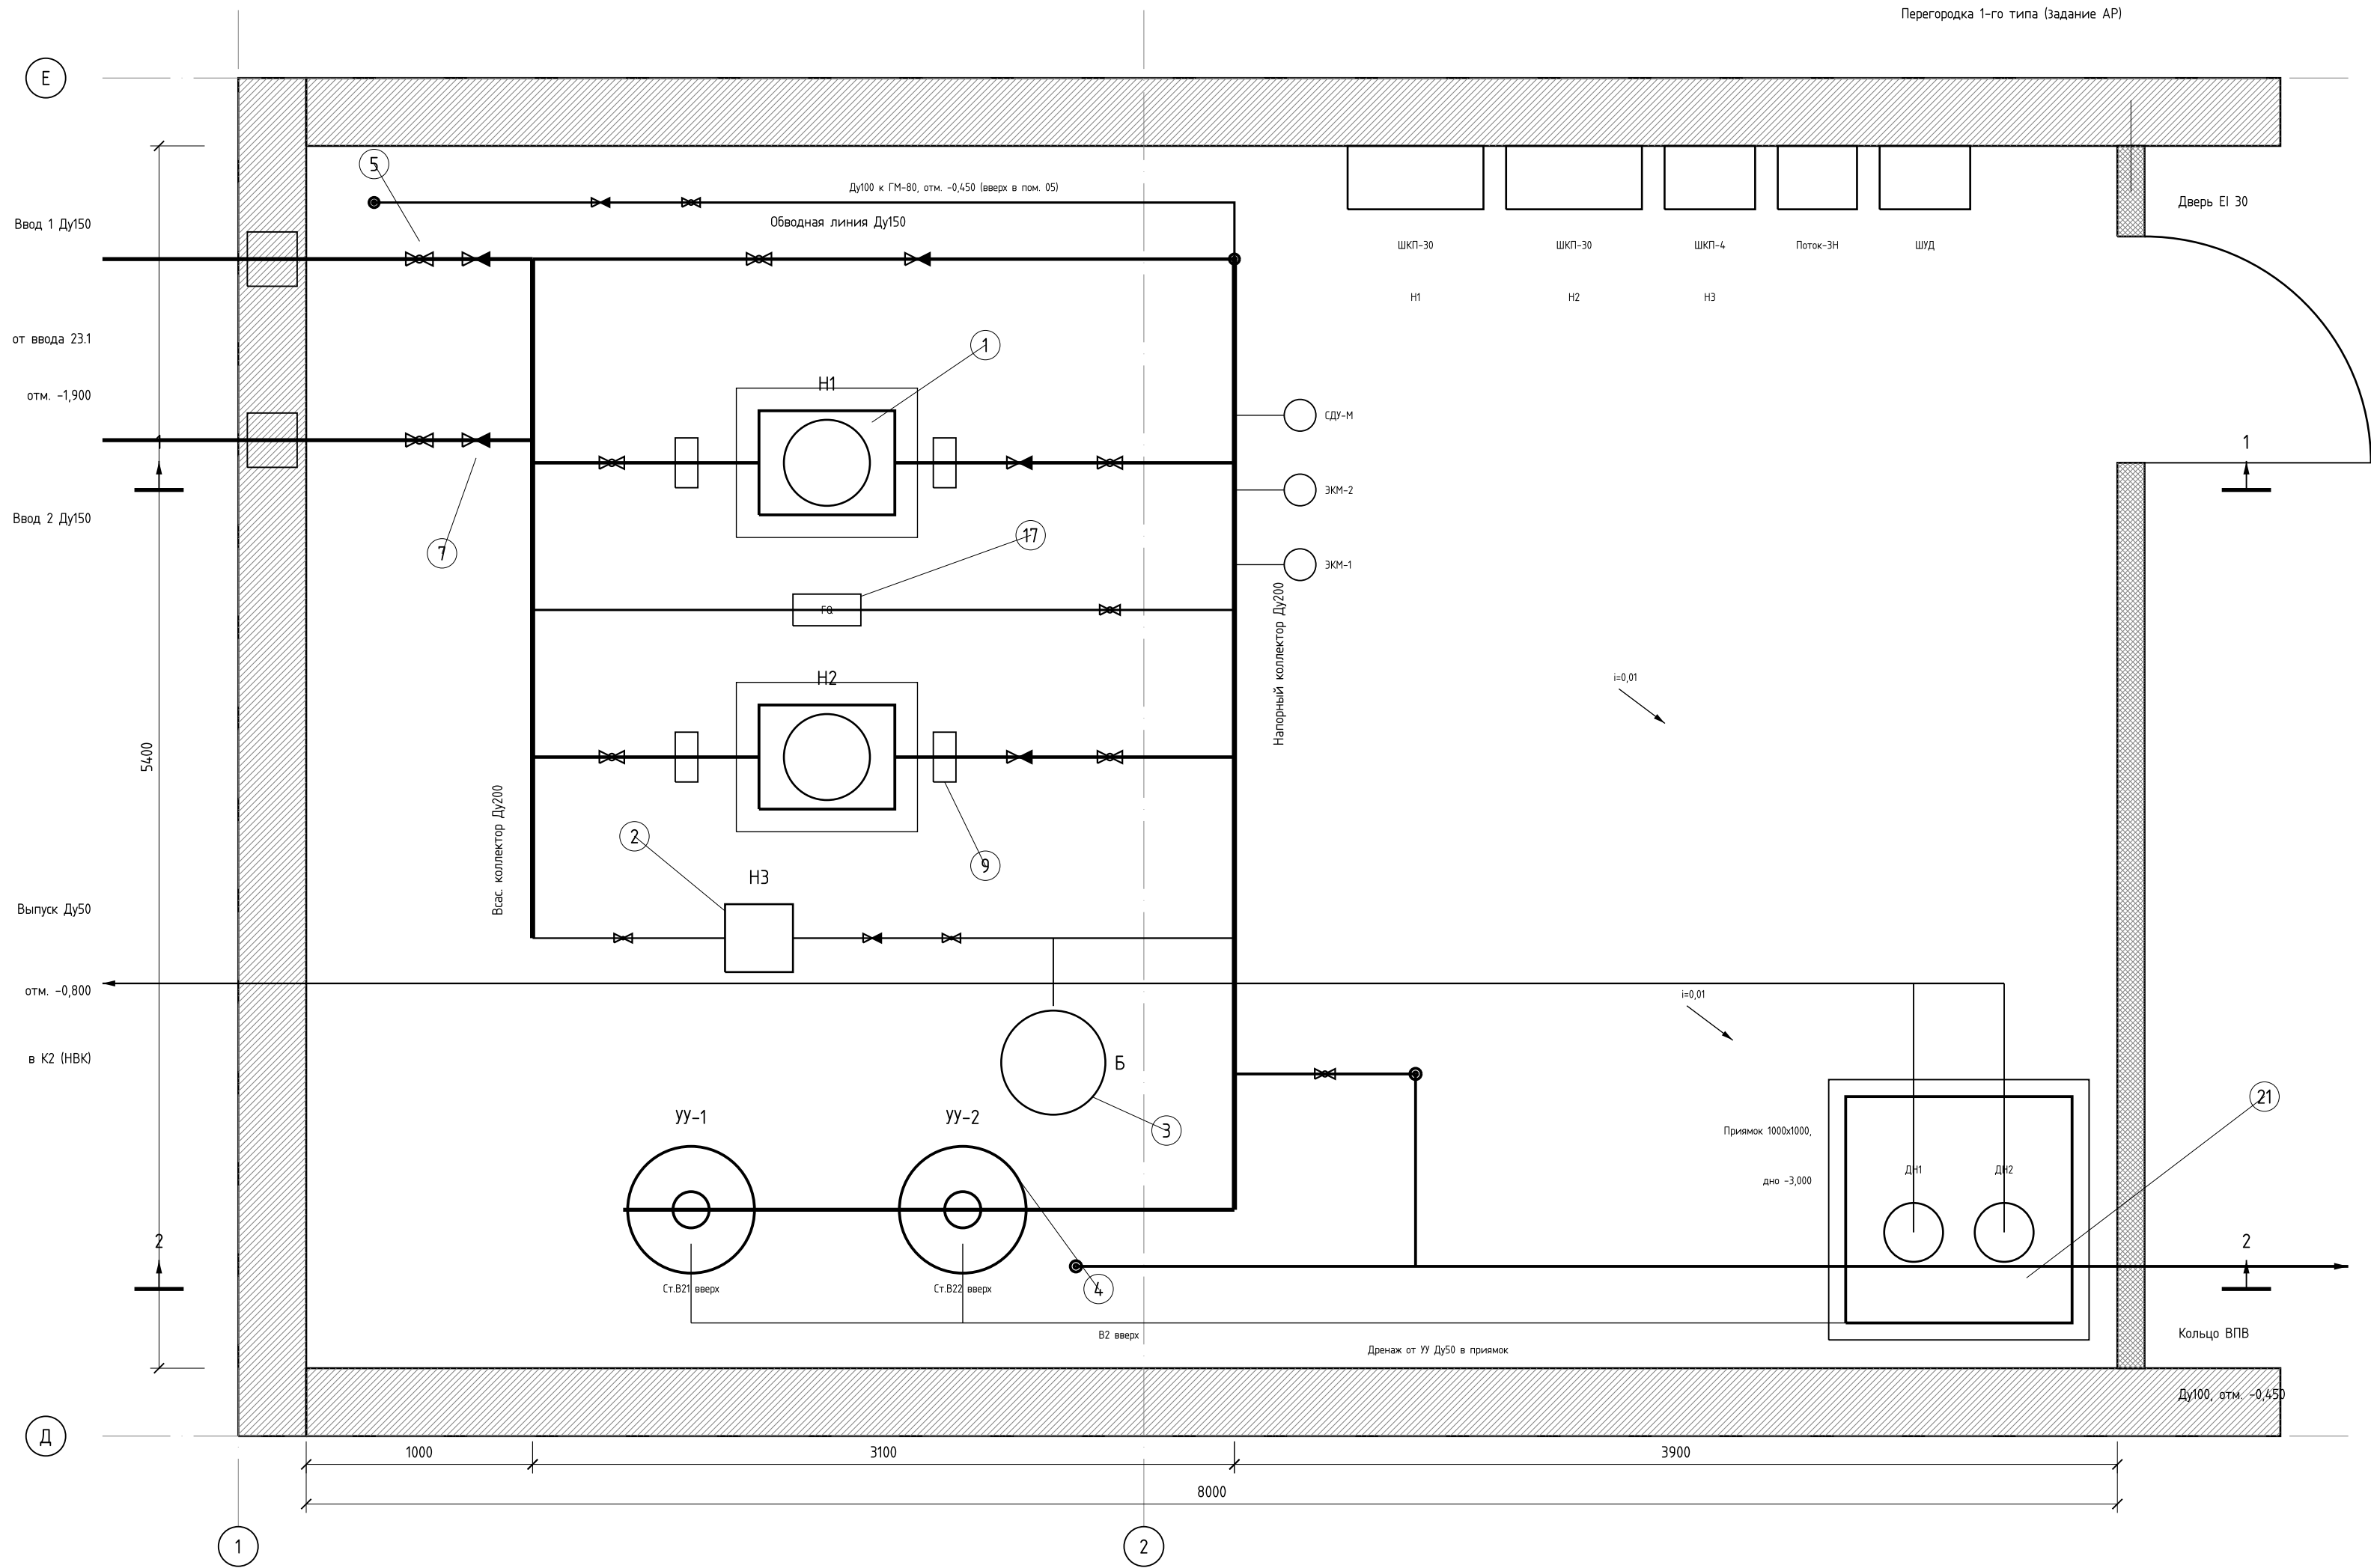

Разрез 1-1 (по линии Н1) М 1:25

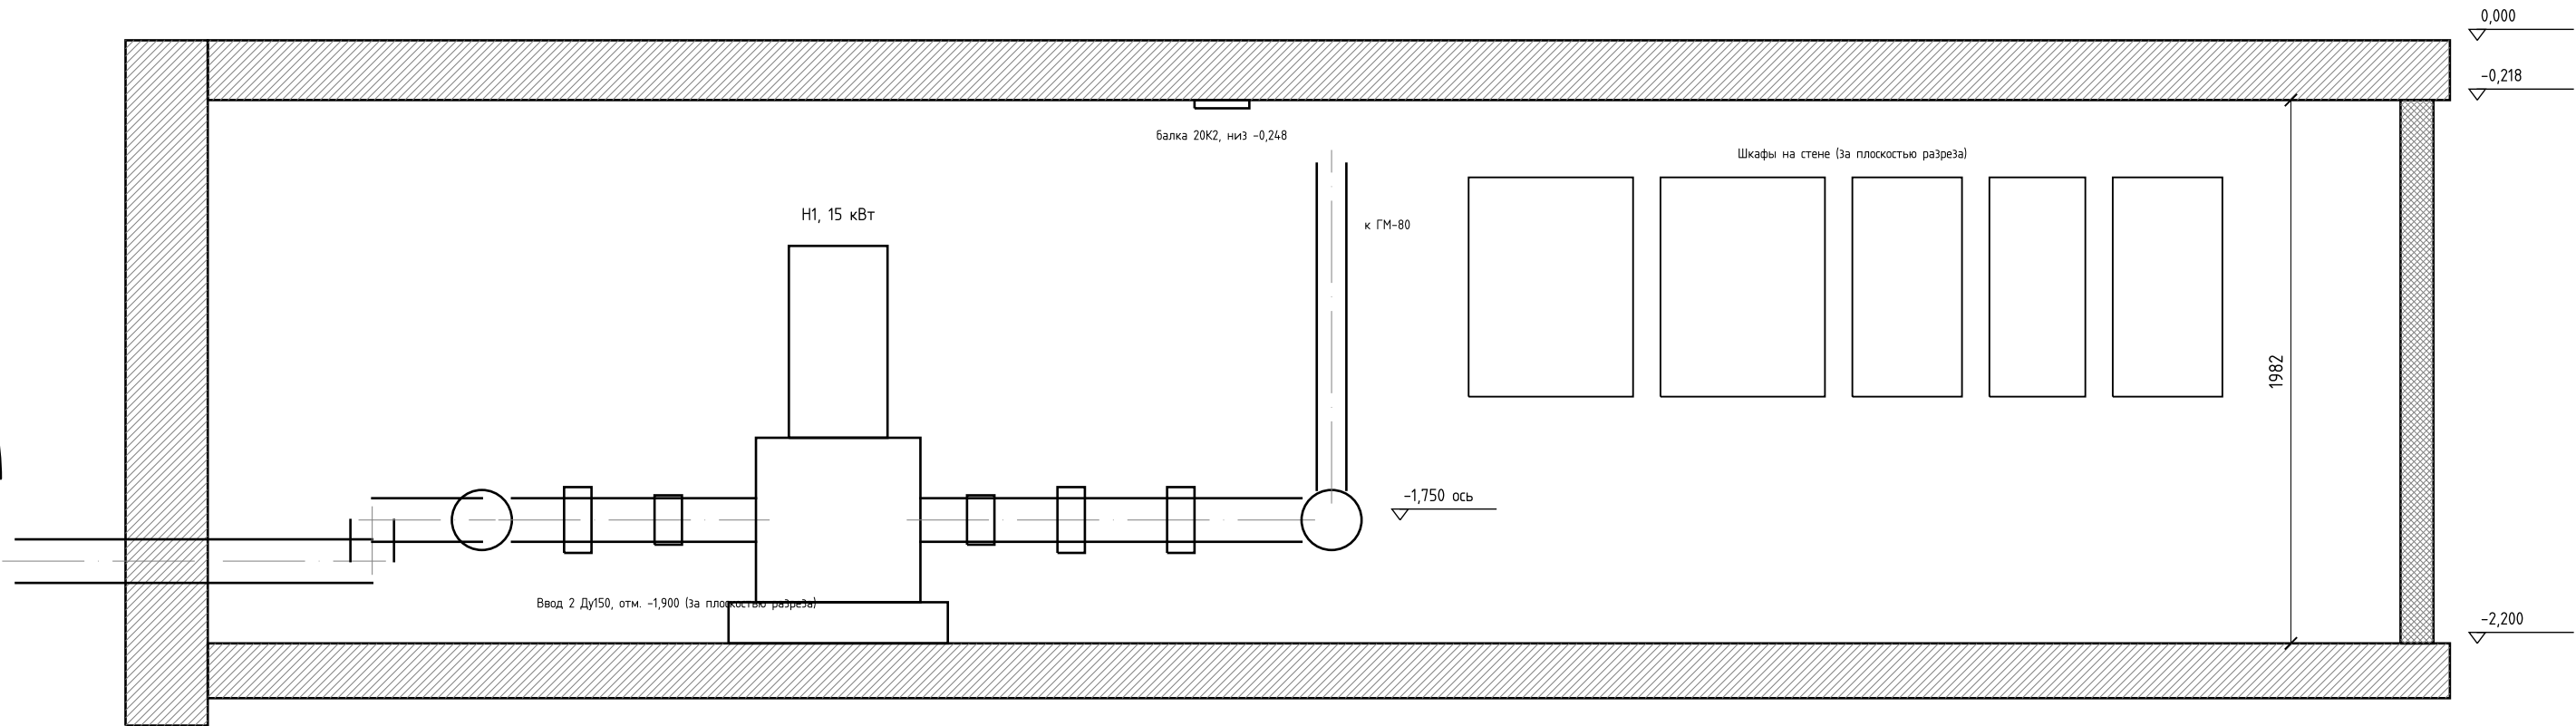

Разрез 2-2 (по узлам управления и приямку) М 1:25

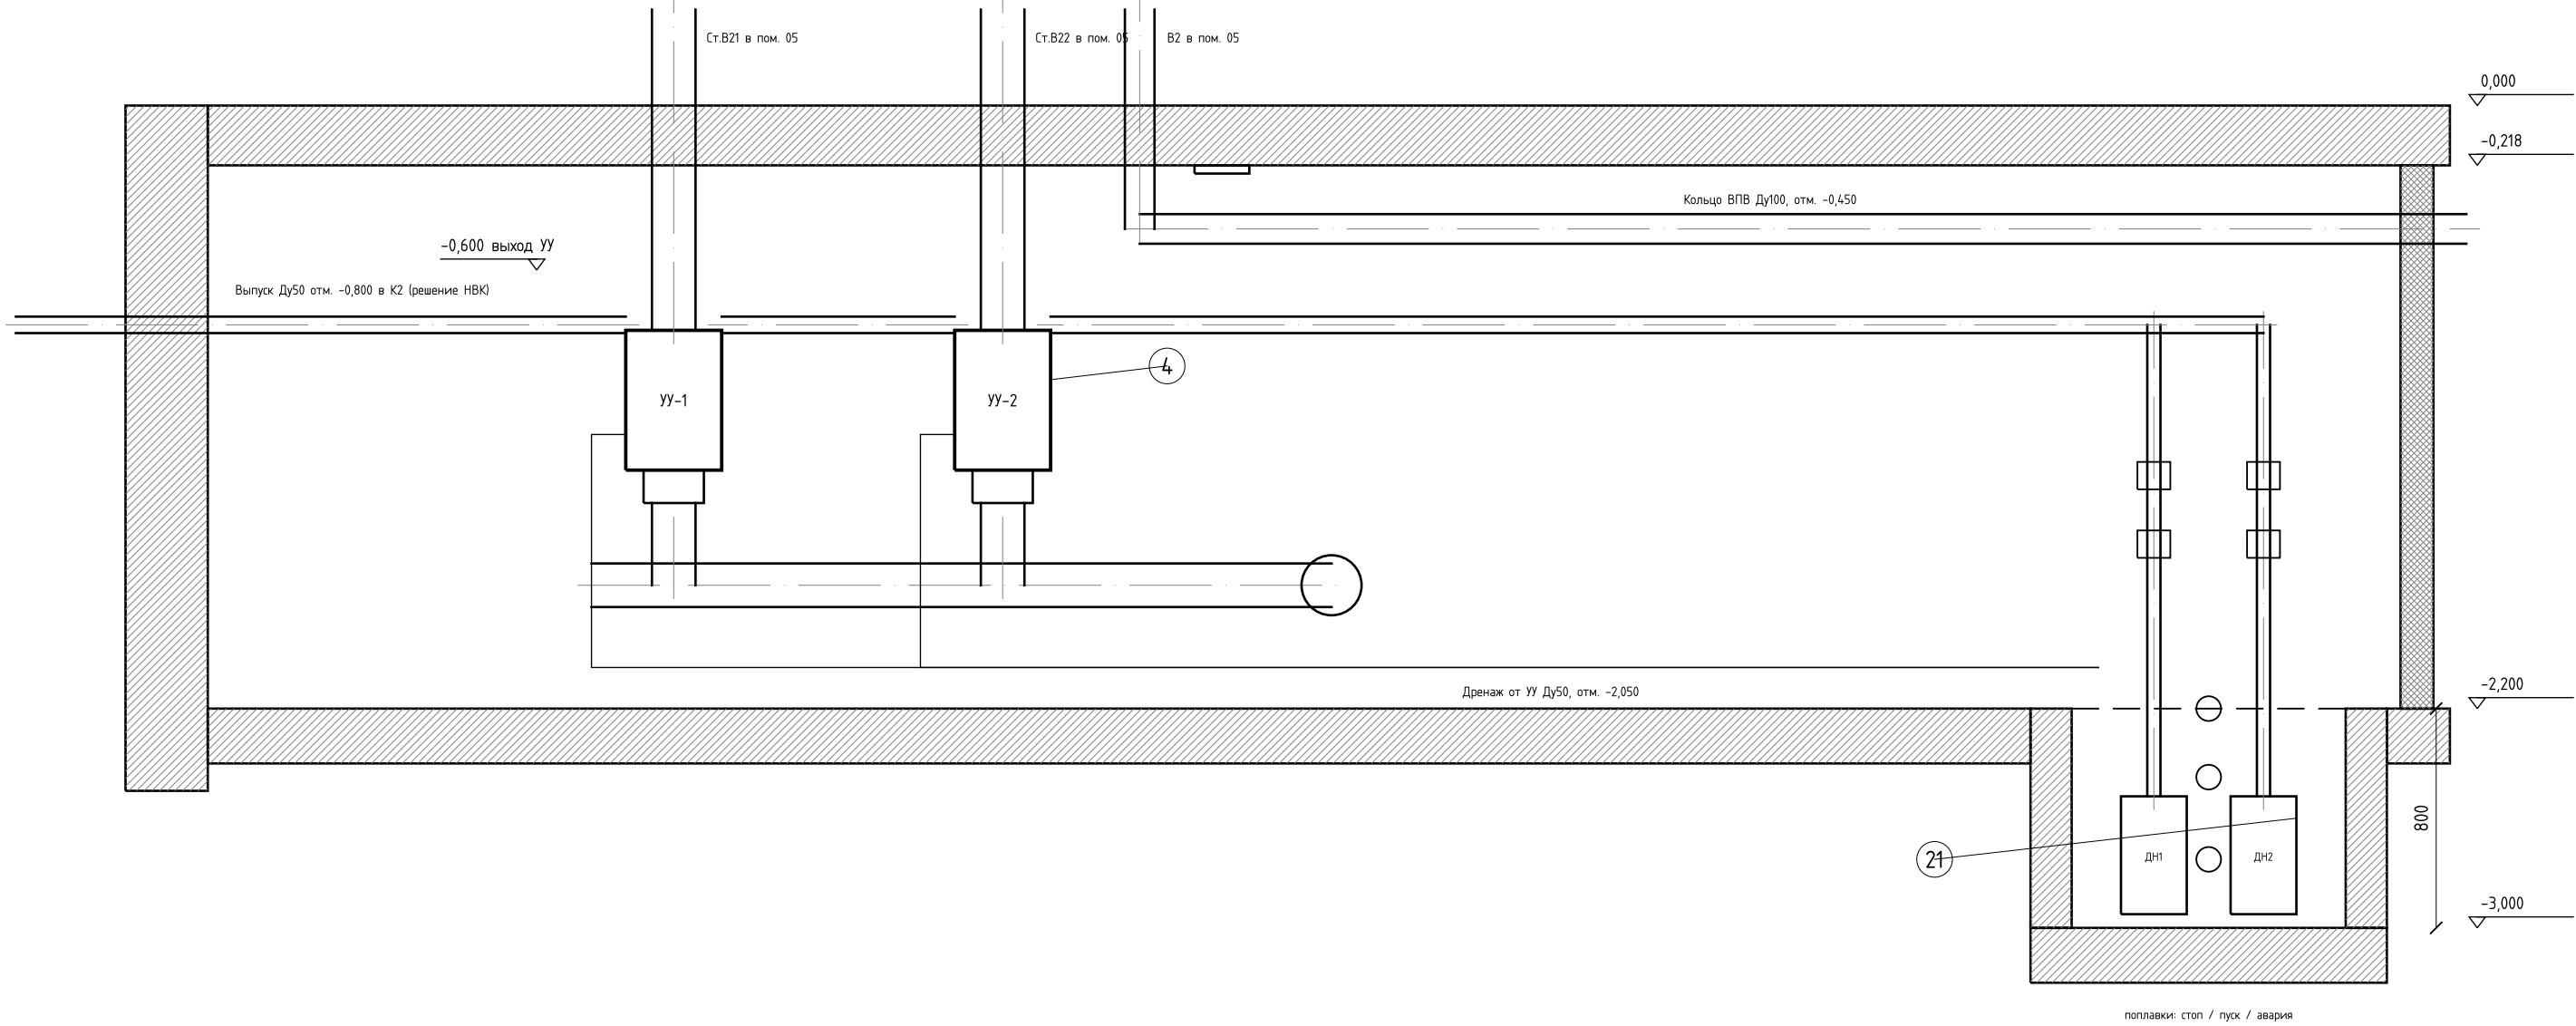


Экспликация оборудования

Обозн.	Наименование	Кол.	Поз.
Н1, Н2	Насос пожарный in-line Q=145 м³/ч, Н=21 м, 15 кВт (1 раб. + 1 рез.)	2	1
Н3	Жокей-насос Q=1,5 м³/ч, Н=30 м, 0,55 кВт	1	2
Б	Бак мембранный 100 л	1	3
УУ-1, УУ-2	Узел управления спринклерный Ду150	2	4
ДН1, ДН2	Насос дренажный погружной Q=10 м³/ч, Н=10 м, 0,75 кВт	2	21
ШКП	Шкафы контрольно-пусковые ШКП-30 (Н1, Н2), ШКП-4 (Н3)	3	180, 181
ША	Поток-ЭН, С2000-КДП-2И, РИП-24 в шкафу автоматики	1	179, 182, 184
ШУД	Шкаф управления дренажными насосами	1	22
РQ	Расходомер на линии опробования Ду100	1	17

- Примечания
- Насосная станция размещена в западном конце технического коридора 1 (оси 1-3/Д-Е), у места ввода водопровода. Помещение отделяется от коридора противопожарной перегородкой 1-го типа с дверью Е1 30 (Задание АР). Путь от двери насосной до выхода - по коридору 1 к лестнице в осях 9-10; решение подтвердить в разделе АР и ПБ. Температура воздуха - не ниже +5 °С.
 - Вводы 2хДу150 - от ввода 23.1 на границе здания (ТУ от 08.10.2026). Граница проектирования ПТ - наружная грань стены подвала. Отметки, материал труб и привязку вводов согласовать с разделом НВК.
 - Насосы - на бетонных основаниях h=150 мм с виброизоляторами, присоединение - через виброкомпенсаторы.
 - Станки С1-Б21 и С1-Б22 проходит в пом. 05 1 этажа, затворы после УУ - в пом. 05 на отм. +1,000. Перемычка кольца ВПВ и линии к патрубкам ГН-80 - также через пом. 05.
 - Примык 1000х1000, глубина 800 мм (Задание КР), пол насосной - с уклоном 0,01 к приямку. Дренажные насосы ДН1, ДН2 работают поочередно, резервный включается по второму поплавку. Сигнал «Аварийный уровень» - на ППКУП «Сириус». Выпуск - в сеть К2 по решению раздела НВК, с обратным клапаном и краном.
 - Электроприводы насосной - I категория надежности, питание от панели ППУ (раздел ЭМ). Рабочее и аварийное освещение, телефонная связь с помещением дежурного персонала - по смежным разделам.
 - Трубопроводы обвязки - сталь электрокоррозионная ГОСТ 10704-91, соединения сварные и фланцевые РN16. Балки перекрытия подвала (20К2, низ -0,248) обшить сниту.
 - У ввода в насосную - световое табло «Насосная станция пожаротушения» (раздел СПС/30).

Схема расположения насосной станции М 1:500

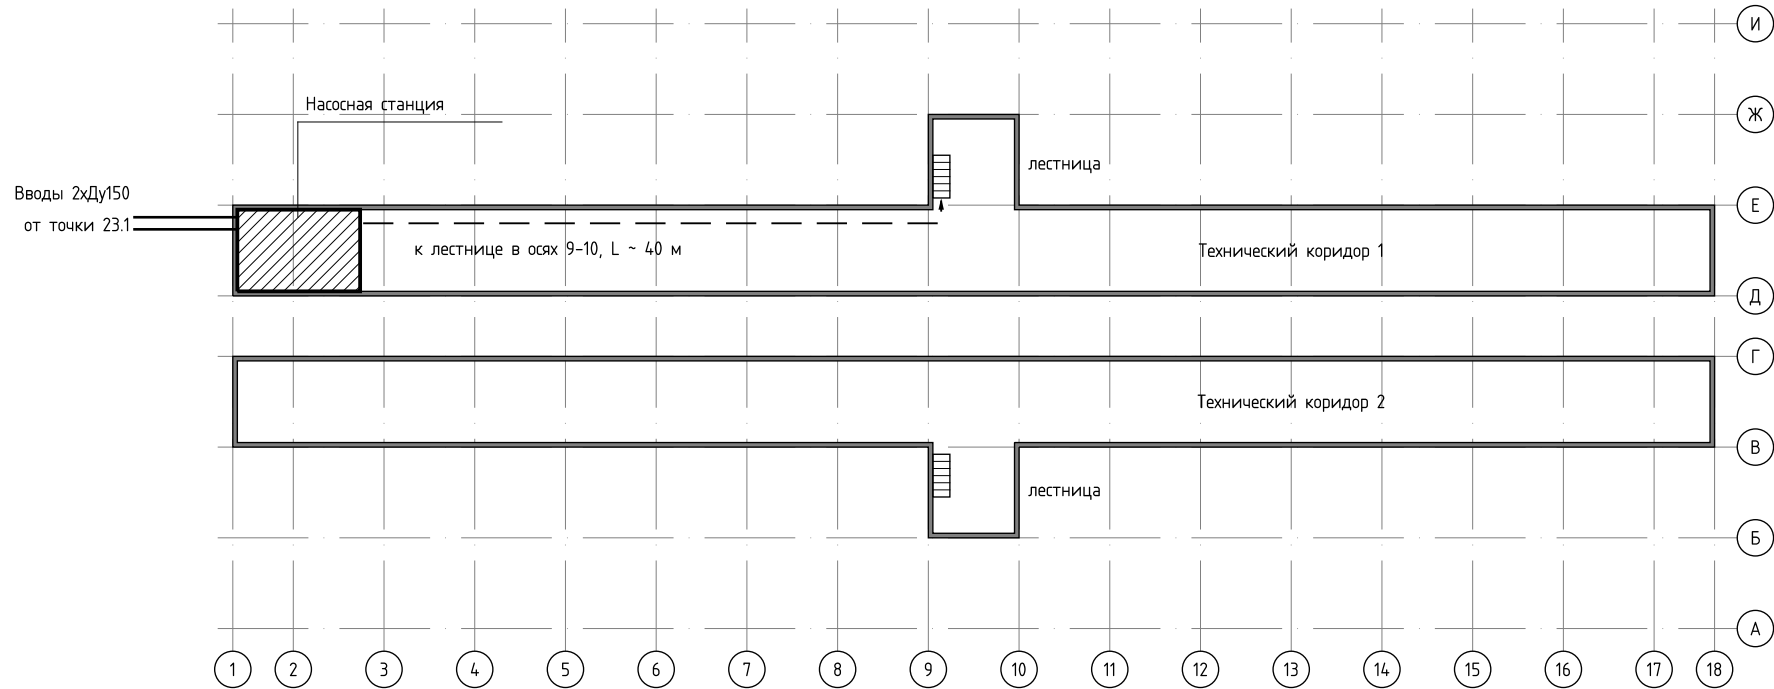

						ОПР-01/24/2024-ДП1-ПТ		
						«Современный коммерческий опто-продуктовый рынок (ОПР) по адресу: Донецкая область, г. Макеевка, Горняцкий район»		
Изм.	Колуч.	Лист	№ док.	Подп.	Дата	Док-павильон №23, №23.2 Рыба-Мясо. Пожаротушение (ВПВ, АУПТ, АУПВ ВРУ)	Стация	Лист
Разраб.							Р	10
Пров.								15
Нконтр.						Насосная станция пожаротушения. План, разрезы 1-1, 2-2. Схема расположения	000 «Технология»	
Гип								