Исаково дом.rvt

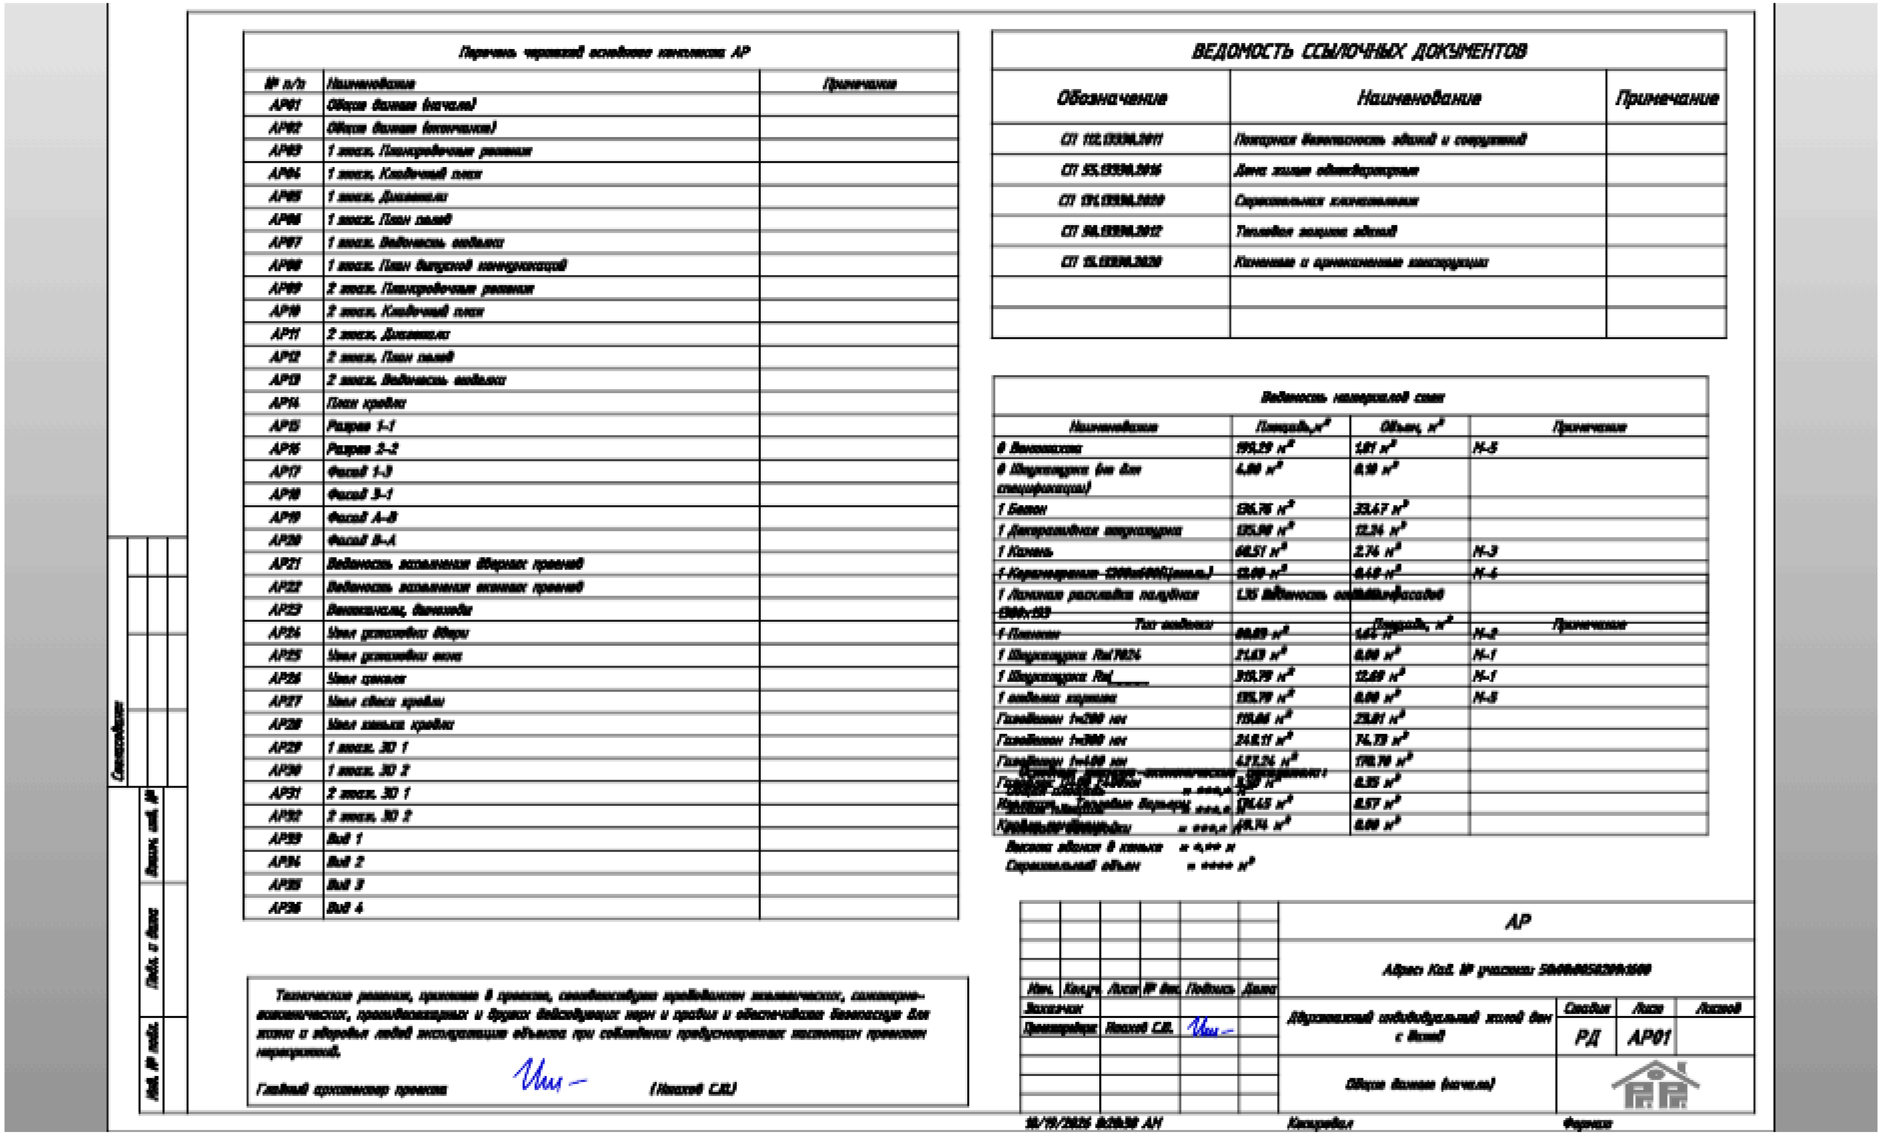

Перечень чертежей основного комплекта АР

№ п/п	Наименование	Примечание
АР01	Общие данные (начало)	
АР02	Общие данные (окончание)	
АР03	1 этаж. Планировочные решения	
АР04	1 этаж. Кладочный план	
АР05	1 этаж. [illegible]	
АР06	1 этаж. План полов	
АР07	1 этаж. Ведомость отделки	
АР08	1 этаж. План выпусков коммуникаций	
АР09	2 этаж. Планировочные решения	
АР10	2 этаж. Кладочный план	
АР11	2 этаж. [illegible]	
АР12	2 этаж. План полов	
АР13	2 этаж. Ведомость отделки	
АР14	План кровли	
АР15	Разрез 1-1	
АР16	Разрез 2-2	
АР17	Фасад 1-3	
АР18	Фасад 3-1	
АР19	Фасад А-В	
АР20	Фасад В-А	
АР21	Ведомость заполнения дверных проемов	
АР22	Ведомость заполнения оконных проемов	
АР23	Вентканалы, дымоходы	
АР24	Узел установки двери	
АР25	Узел установки окна	
АР26	Узел цоколя	
АР27	Узел свеса кровли	
АР28	Узел конька кровли	
АР29	1 этаж. 3D 1	
АР30	1 этаж. 3D 2	
АР31	2 этаж. 3D 1	
АР32	2 этаж. 3D 2	
АР33	Вид 1	
АР34	Вид 2	
АР35	Вид 3	
АР36	Вид 4	

ВЕДОМОСТЬ ССЫЛОЧНЫХ ДОКУМЕНТОВ

Обозначение	Наименование	Примечание
СП 112.13330.2011	Пожарная безопасность зданий и сооружений	
СП 55.13330.2016	Дома жилые одноквартирные	
СП 131.13330.2020	Строительная климатология	
СП 50.13330.2012	Тепловая защита зданий	
СП 15.13330.2020	Каменные и армокаменные конструкции	

Ведомость материалов стен

Наименование	Площадь, м²	Объем, м³	Примечание
0 [illegible]	199.29 м²	1.81 м³	М-5
0 Штукатурка (не для спецификации)	4.80 м²	0.19 м³	
1 Бетон	136.76 м²	33.47 м³	
1 Декоративная штукатурка	135.98 м²	13.34 м³	
1 Камень	68.51 м²	2.74 м³	М-3
1 Керамогранит 1200х600([illegible])	13.00 м²	0.48 м³	М-4
1 Ламинат раскладка полубная 1300х133	1.36 Ведомость отделки фасадов		
Тип отделки		Площадь, м²	Примечание
1 Панели	86.89 м²	1.64 м³	М-2
1 Штукатурка Ral7024	21.43 м²	0.00 м³	М-1
1 Штукатурка Ral____	319.79 м²	12.69 м³	М-1
1 отделка карниза	135.79 м²	0.00 м³	М-5
Газобетон t=200 мм	119.86 м²	23.81 м³	
Газобетон t=300 мм	248.11 м²	74.73 м³	
Газобетон t=400 мм	473.24 м²	170.76 м³	
[illegible]	5.39 м²	0.35 м³	
[illegible]	136.45 м²	0.57 м³	
[illegible]	49.74 м²	0.00 м³	

Основные технико-экономические показатели:
Общая площадь = ***,* м²
Площадь застройки = ***,* м²
Количество этажей = ***,*
Высота здания в коньке = *,** м
Строительный объем = **** м³

Технические решения, принятые в проекте, соответствуют требованиям экологических, санитарно-гигиенических, противопожарных и других действующих норм и правил и обеспечивают безопасную для жизни и здоровья людей эксплуатацию объекта при соблюдении предусмотренных чертежами проекта мероприятий.

Главный архитектор проекта Иш– (Исаков С.В.)

Согласовано
Взам. инв. №
Подп. и дата
Инв. № подл.

Изм.	Кол.уч.	Лист	№ док.	Подпись	Дата	
Заказчик						
Проектировщик	Исаков С.В.			Иш–		

АР

Адрес: Кад. № участка: [illegible]

Двухэтажный индивидуальный жилой дом с баней

Стадия	Лист	Листов
РД	АР01	

Общие данные (начало)

10/19/2026 8:28:58 AM Копировал Формат

AUTODESK Viewer

AUTODESK