

Общество с ограниченной ответственностью "Технология"


«Современный коммерческий оптово-продовольственный рынок (ОПР) по адресу:
Донецкая область, г. Макеевка, Горняцкий район»

Док павильон рыба-мясо № 23

Проектная документация

Автоматическая установка пожарной сигнализации. Система оповещения и
управления эвакуацией.

ОПР-01/24/2024-КДЗ-АПСиСОУЭ

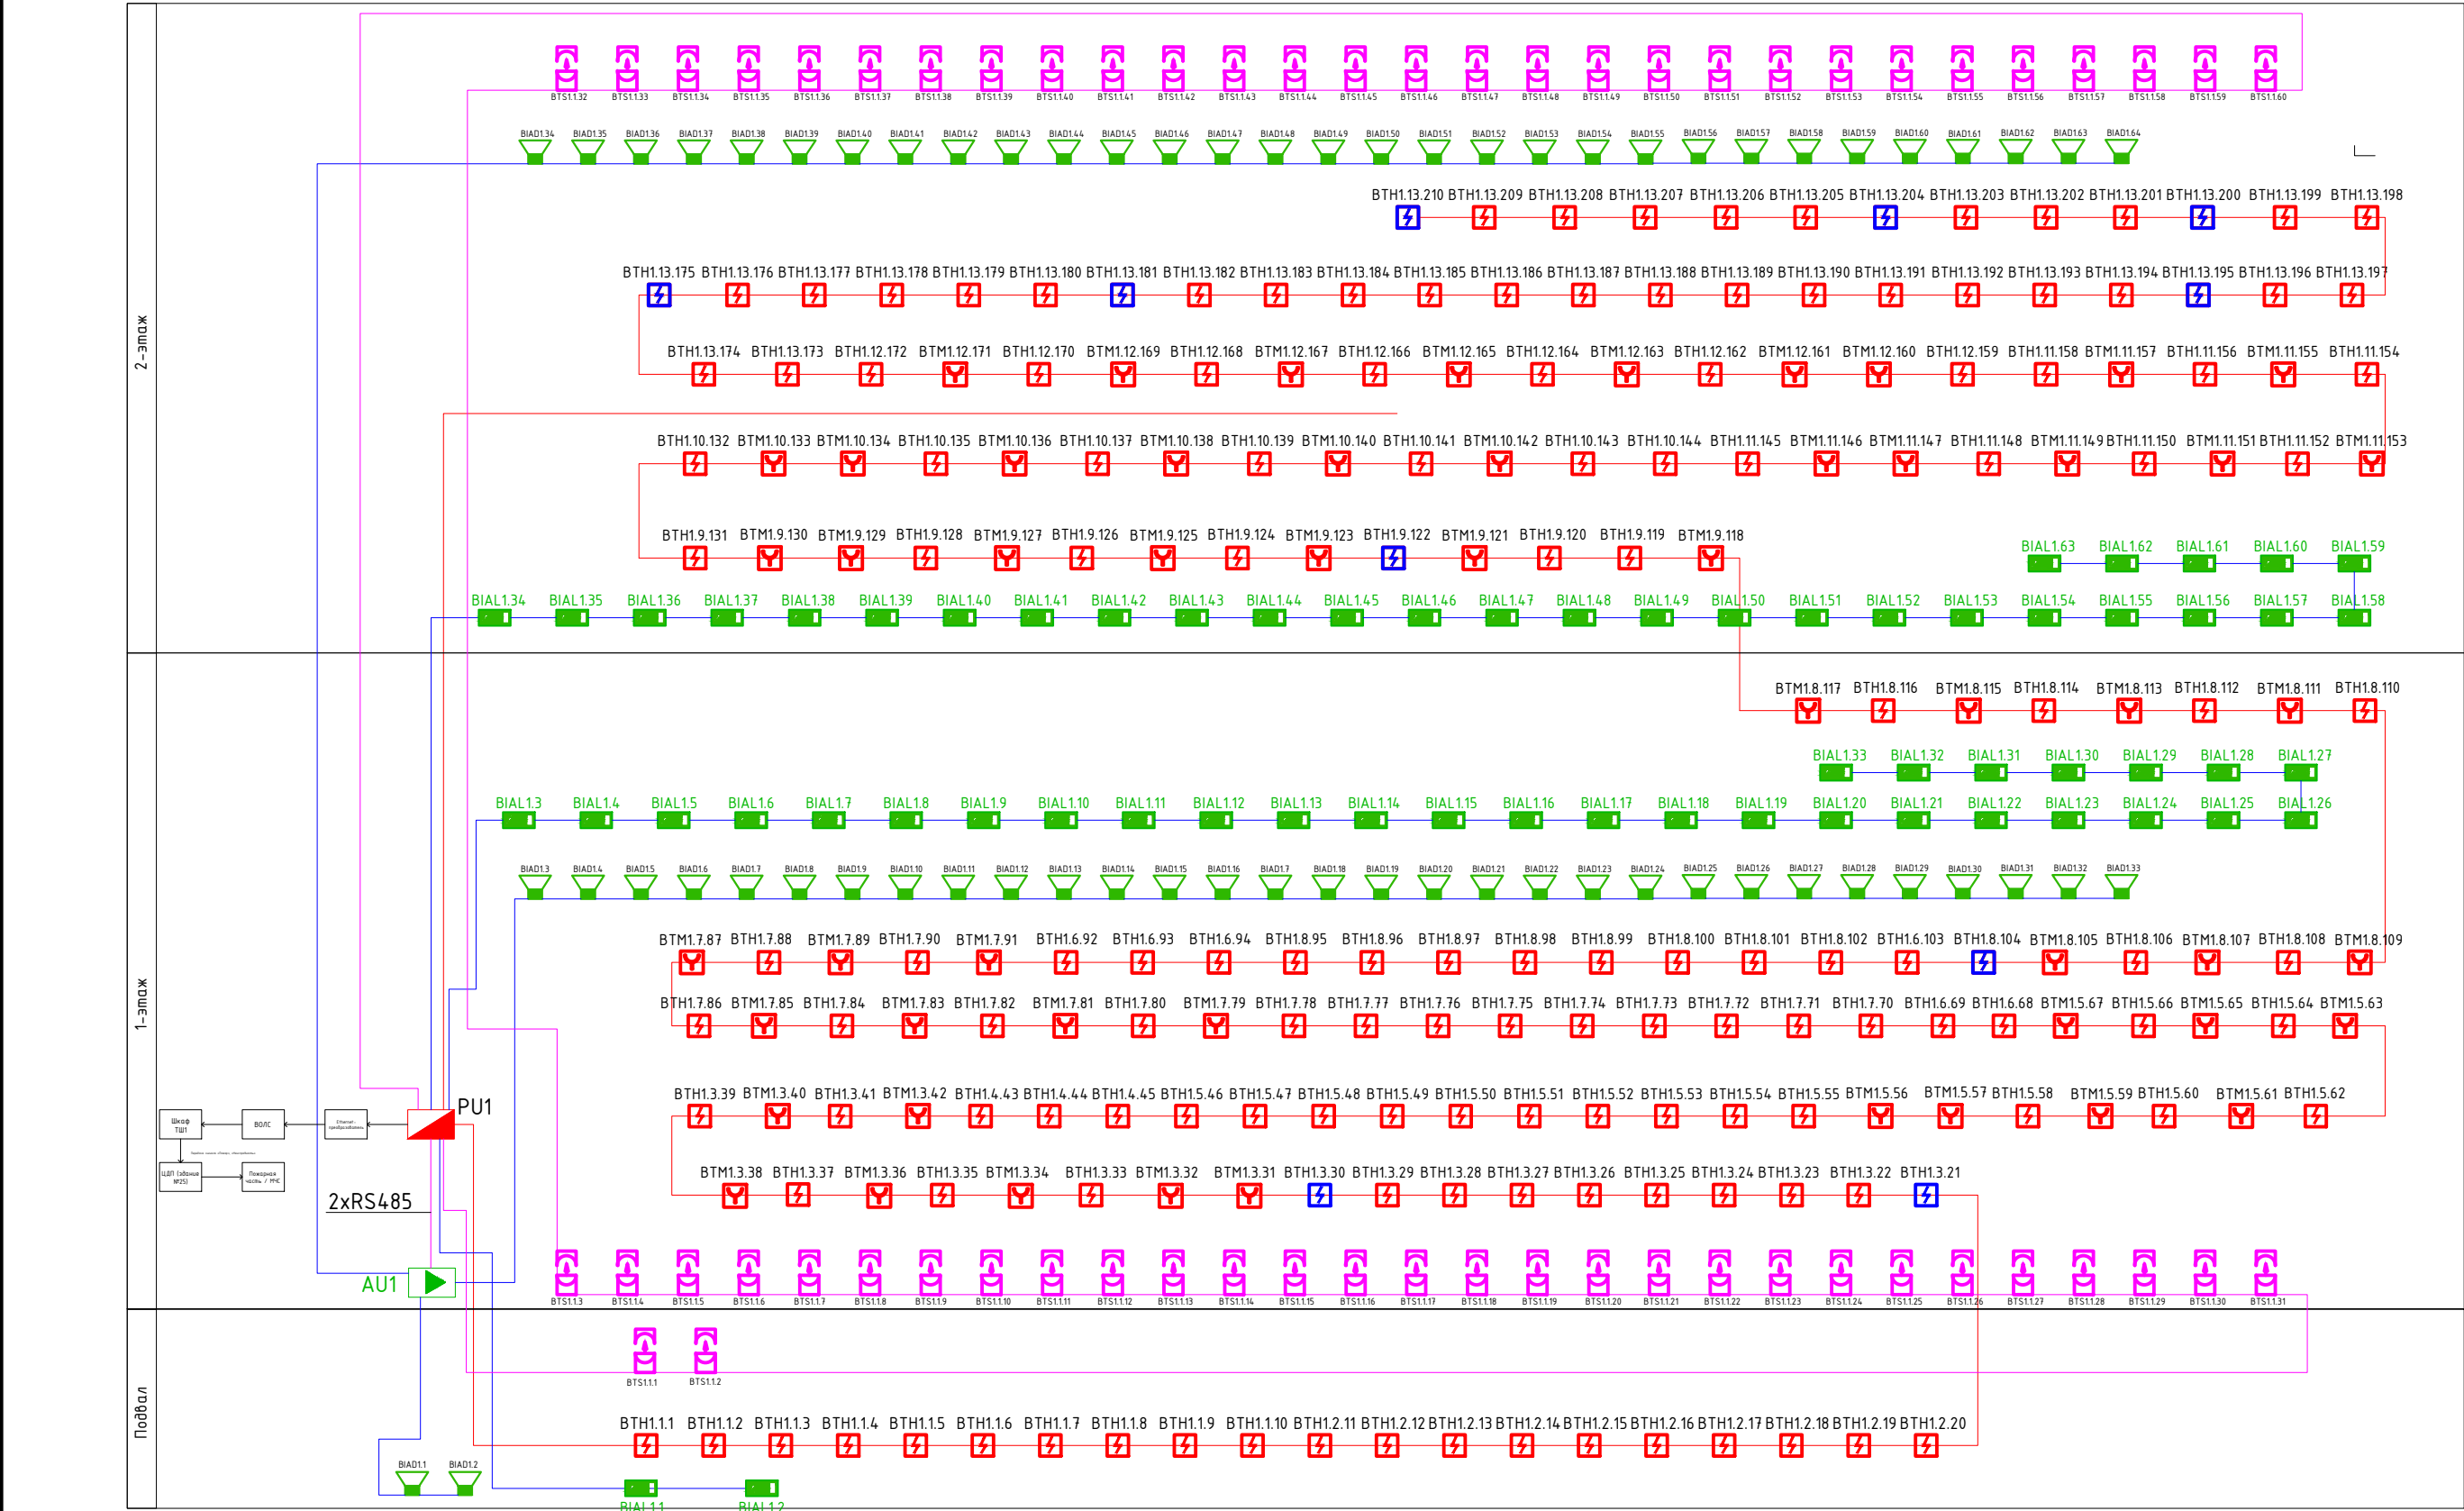


Условные графические обозначения оборудования					
Поз. обозначение	Наименование	Примечание	Символ	Обозначение	Описание
	PUx			BIALx.y	Оповещатели световые "Молния 24"
	AUx	Блок речевого оповещения "РУПОР-300"		BTSx.y.z	Извещатель пожарный дымовой оптико-электронный линейный "С2000-ИПДЛ"
	BTHx.y	Извещатель пожарный дымовой оптико-электронный адресно-аналоговый "ДИП-34А-03"		BRIZx.y.z	Блок разветвительно-изолирующий "БРИЗ"
	BTMx.y	Извещатель пожарный ручной адресный "ИПР 513-ЗАМ-С"		SP4x.y.z	Блок сигнально-пусковой адресный "С2000-СП4/220"
	BTMx.y.z	Устройство дистанционного пуска (Пуск дымоудаления) "УДП 513-ЗАМ"	Условные графические обозначения кабельных линий		
	BTHx.y	Извещатель пожарный дымовой оптико-электронный адресно-аналоговый со встроенным ИКЗ "ДИП-34А-04"	Марка кабеля	Назначение	Граф. обозначение
	BIAOx.y	Оповещатель речевой настенный "ОПР-С103.1"	КПСЭн2(А)-FRHF 1x2x0,5	Шлейф пожарной сигнализации	
	ZCx.y	Адресный модуль контроля оповещения "Рупор-300-МК"	КПСЭн2(А)-FRHF 1x2x0,5	Линия светового оповещения	
			КПСЭн2(А)-FRHF 1x2x0,5	Линия звукового оповещения	

Примечание - в перечне условных обозначений: x - порядковый номер прибора, y - порядковый номер z - порядковый номер устройства/линии. ЗКПС,

						ОПР-01/24/2024-КДЗ-АПСuCOУЭ			
						«Современный коммерческий оптово-продовольственный рынок (ОПР) по адресу: Донецкая область, г. Макеевка, Горняцкий район»			
						Док-павильон Рыба-мясо №23			
Изм.	Колуч	Лист	N док	Погнись	Дата	Автоматическая установка пожарной сигнализации. Система оповещения и управления эвакуацией.	Стадия	Лист	Листов
ГИП							Р	4	17
Разработал						Структурная схема	ООО "Технология"		
Н.контроль									

План расположения зон ЗКПС в подвале

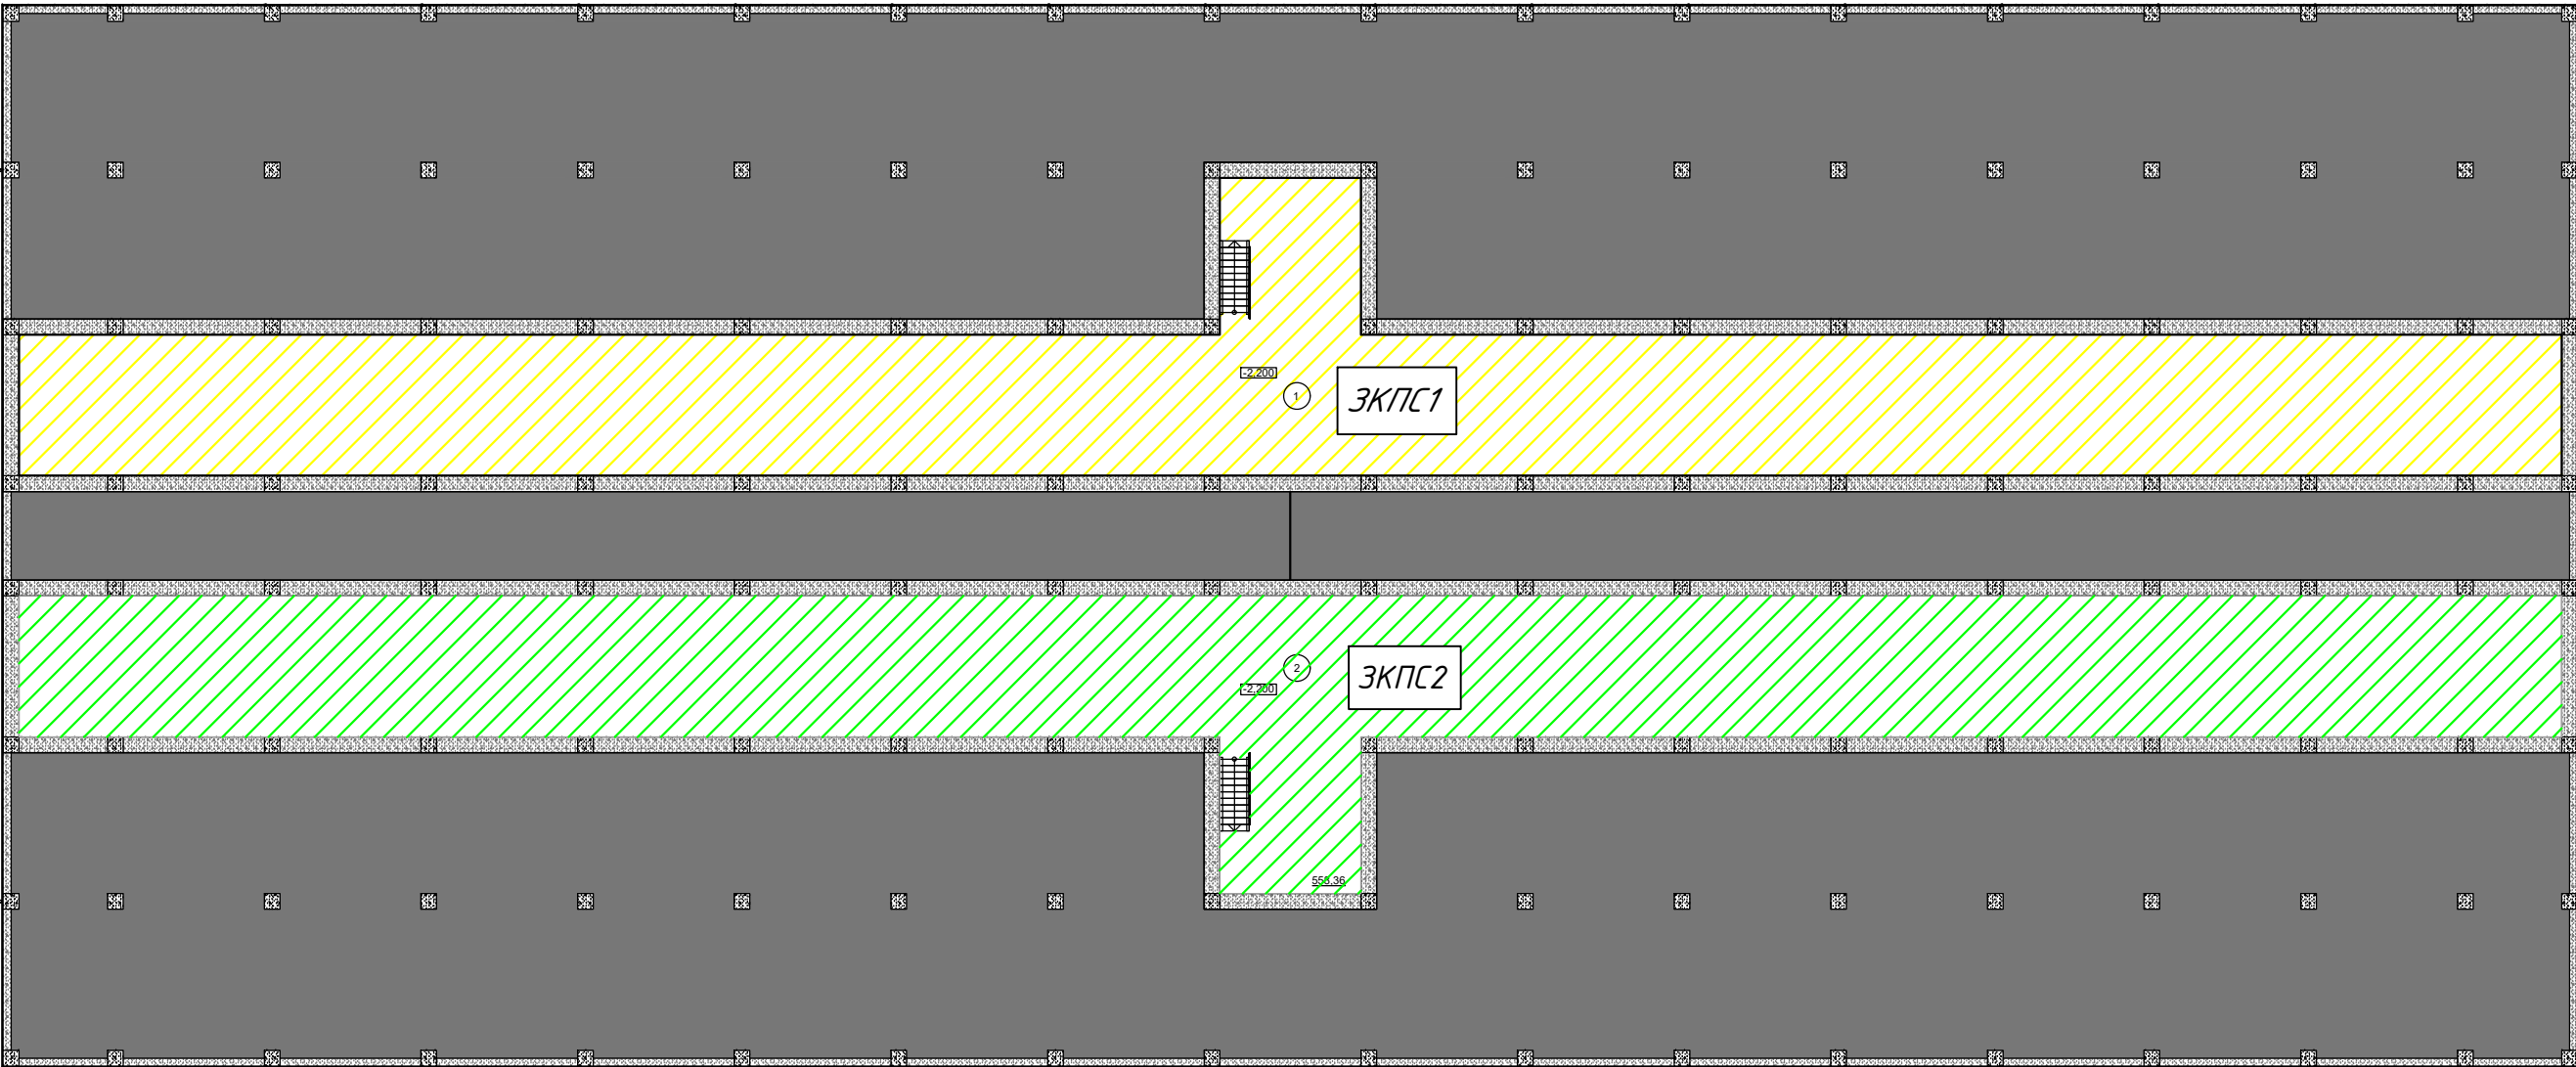


Номер помещения	Наименование	Площадь, м2	Кат. помещения
1	Технический коридор	558,36	-
2	Технический коридор	558,36	-
		1 116,72 м²	

						ОПР-01/24/2024-КДЗ-АПСuCOУЭ		
						«Современный коммерческий оптово-продовольственный рынок (ОПР) по адресу: Донецкая область, г. Макеевка, Горняцкий район»		
						Док-павильон Рыба-мясо №23		
Изм.	Кол.уч	Лист	N док	Подпись	Дата	Автоматическая установка пожарной сигнализации. Система оповещения и управления эвакуацией.	Стадия	Лист
ГИП							Р	5
Разработал						План расположения зон ЗКПС в подвале		17
Н.контроль							ООО "Технология"	


План расположения зон ЗКПС на 1-м этаже

Номер пояс сечения	Наименование	Площадь, м2	Кат. пози- ция
01	Тамбур	11,41	-
02	Тамбур	11,41	-
03	Тамбур	11,41	-
04	Тамбур	11,41	-
05	Коридор уборочного инвентаря	25,08	Б-3
06	ИТП	12,33	Б-3
07	Электрощитовая	12,33	Б-3
08	Разрушенный тамбур	107,83	-
09	Разрушенный тамбур	70,33	-
10	Разрушенный тамбур	70,33	-
21	Разрушенный тамбур	107,83	-
22	Разрушенный тамбур	107,83	-
23	Разрушенный тамбур	70,19	-
24	Разрушенный тамбур	70,19	-
25	Разрушенный тамбур	70,21	-
26	Разрушенный тамбур	70,19	-
27	Разрушенный тамбур	70,21	-
28	Разрушенный тамбур	72,28	-
29	Разрушенный тамбур	72,28	-
31	Разрушенный тамбур	70,19	-
32	Разрушенный тамбур	70,21	-
33	Разрушенный тамбур	70,19	-
34	Разрушенный тамбур	70,21	-
35	Разрушенный тамбур	107,60	-
36	Зона подготовки товара	22,04	-
37	Зона подготовки товара	22,72	-
38	Зона подготовки товара	22,72	-
39	Зона подготовки товара	22,72	-
40	Зона подготовки товара	22,72	-
41	Зона подготовки товара	22,72	-
42	Зона подготовки товара	22,72	-
43	Зона подготовки товара	23,39	-
44	Зона подготовки товара	22,72	-
45	Зона подготовки товара	22,72	-
46	Зона подготовки товара	22,72	-
47	Зона подготовки товара	22,72	-
48	Зона подготовки товара	22,72	-
49	Зона подготовки товара	22,04	-
50	Зона подготовки товара	22,04	-
51	Зона подготовки товара	22,72	-
52	Зона подготовки товара	22,72	-
53	Зона подготовки товара	22,72	-
54	Зона подготовки товара	22,72	-
55	Зона подготовки товара	22,72	-
56	Зона подготовки товара	23,39	-
57	Зона подготовки товара	22,72	-
58	Зона подготовки товара	22,72	-
59	Зона подготовки товара	22,72	-
60	Зона подготовки товара	22,72	-
61	Зона подготовки товара	22,72	-
62	Зона подготовки товара	22,72	-
63	Зона подготовки товара	22,04	-
64	Выставочная зона	13,17	-
65	Выставочная зона	13,17	-
66	Выставочная зона	13,17	-
67	Выставочная зона	13,17	-
68	Выставочная зона	13,17	-
69	Выставочная зона	13,17	-
70	Выставочная зона	13,17	-
71	Выставочная зона	13,17	-
72	Выставочная зона	13,17	-
73	Выставочная зона	13,17	-
74	Выставочная зона	13,17	-
75	Выставочная зона	13,17	-
76	Выставочная зона	13,17	-
77	Выставочная зона	13,17	-
78	Выставочная зона	13,17	-
79	Выставочная зона	13,17	-
80	Выставочная зона	13,17	-
81	Выставочная зона	13,17	-
82	Выставочная зона	13,17	-
83	Выставочная зона	13,17	-
84	Выставочная зона	13,17	-
85	Выставочная зона	13,17	-
86	Выставочная зона	13,17	-
87	Выставочная зона	13,17	-
88	Выставочная зона	13,17	-
89	Выставочная зона	13,17	-
90	Выставочная зона	13,17	-
91	Выставочная зона	13,17	-
92	Тамбур	18,06	-
93	Тамбур	18,06	-
94	Тамбур-шлюз	62,36	-
95	Тамбур-шлюз	62,36	-
96	Торговый зал	96,19	-
97	Торговый зал	107,13	-
98	Торговый зал	107,13	-
99	СУ М	24,75	-
100	СУ Ж	24,75	-
		3 848,29 м²	

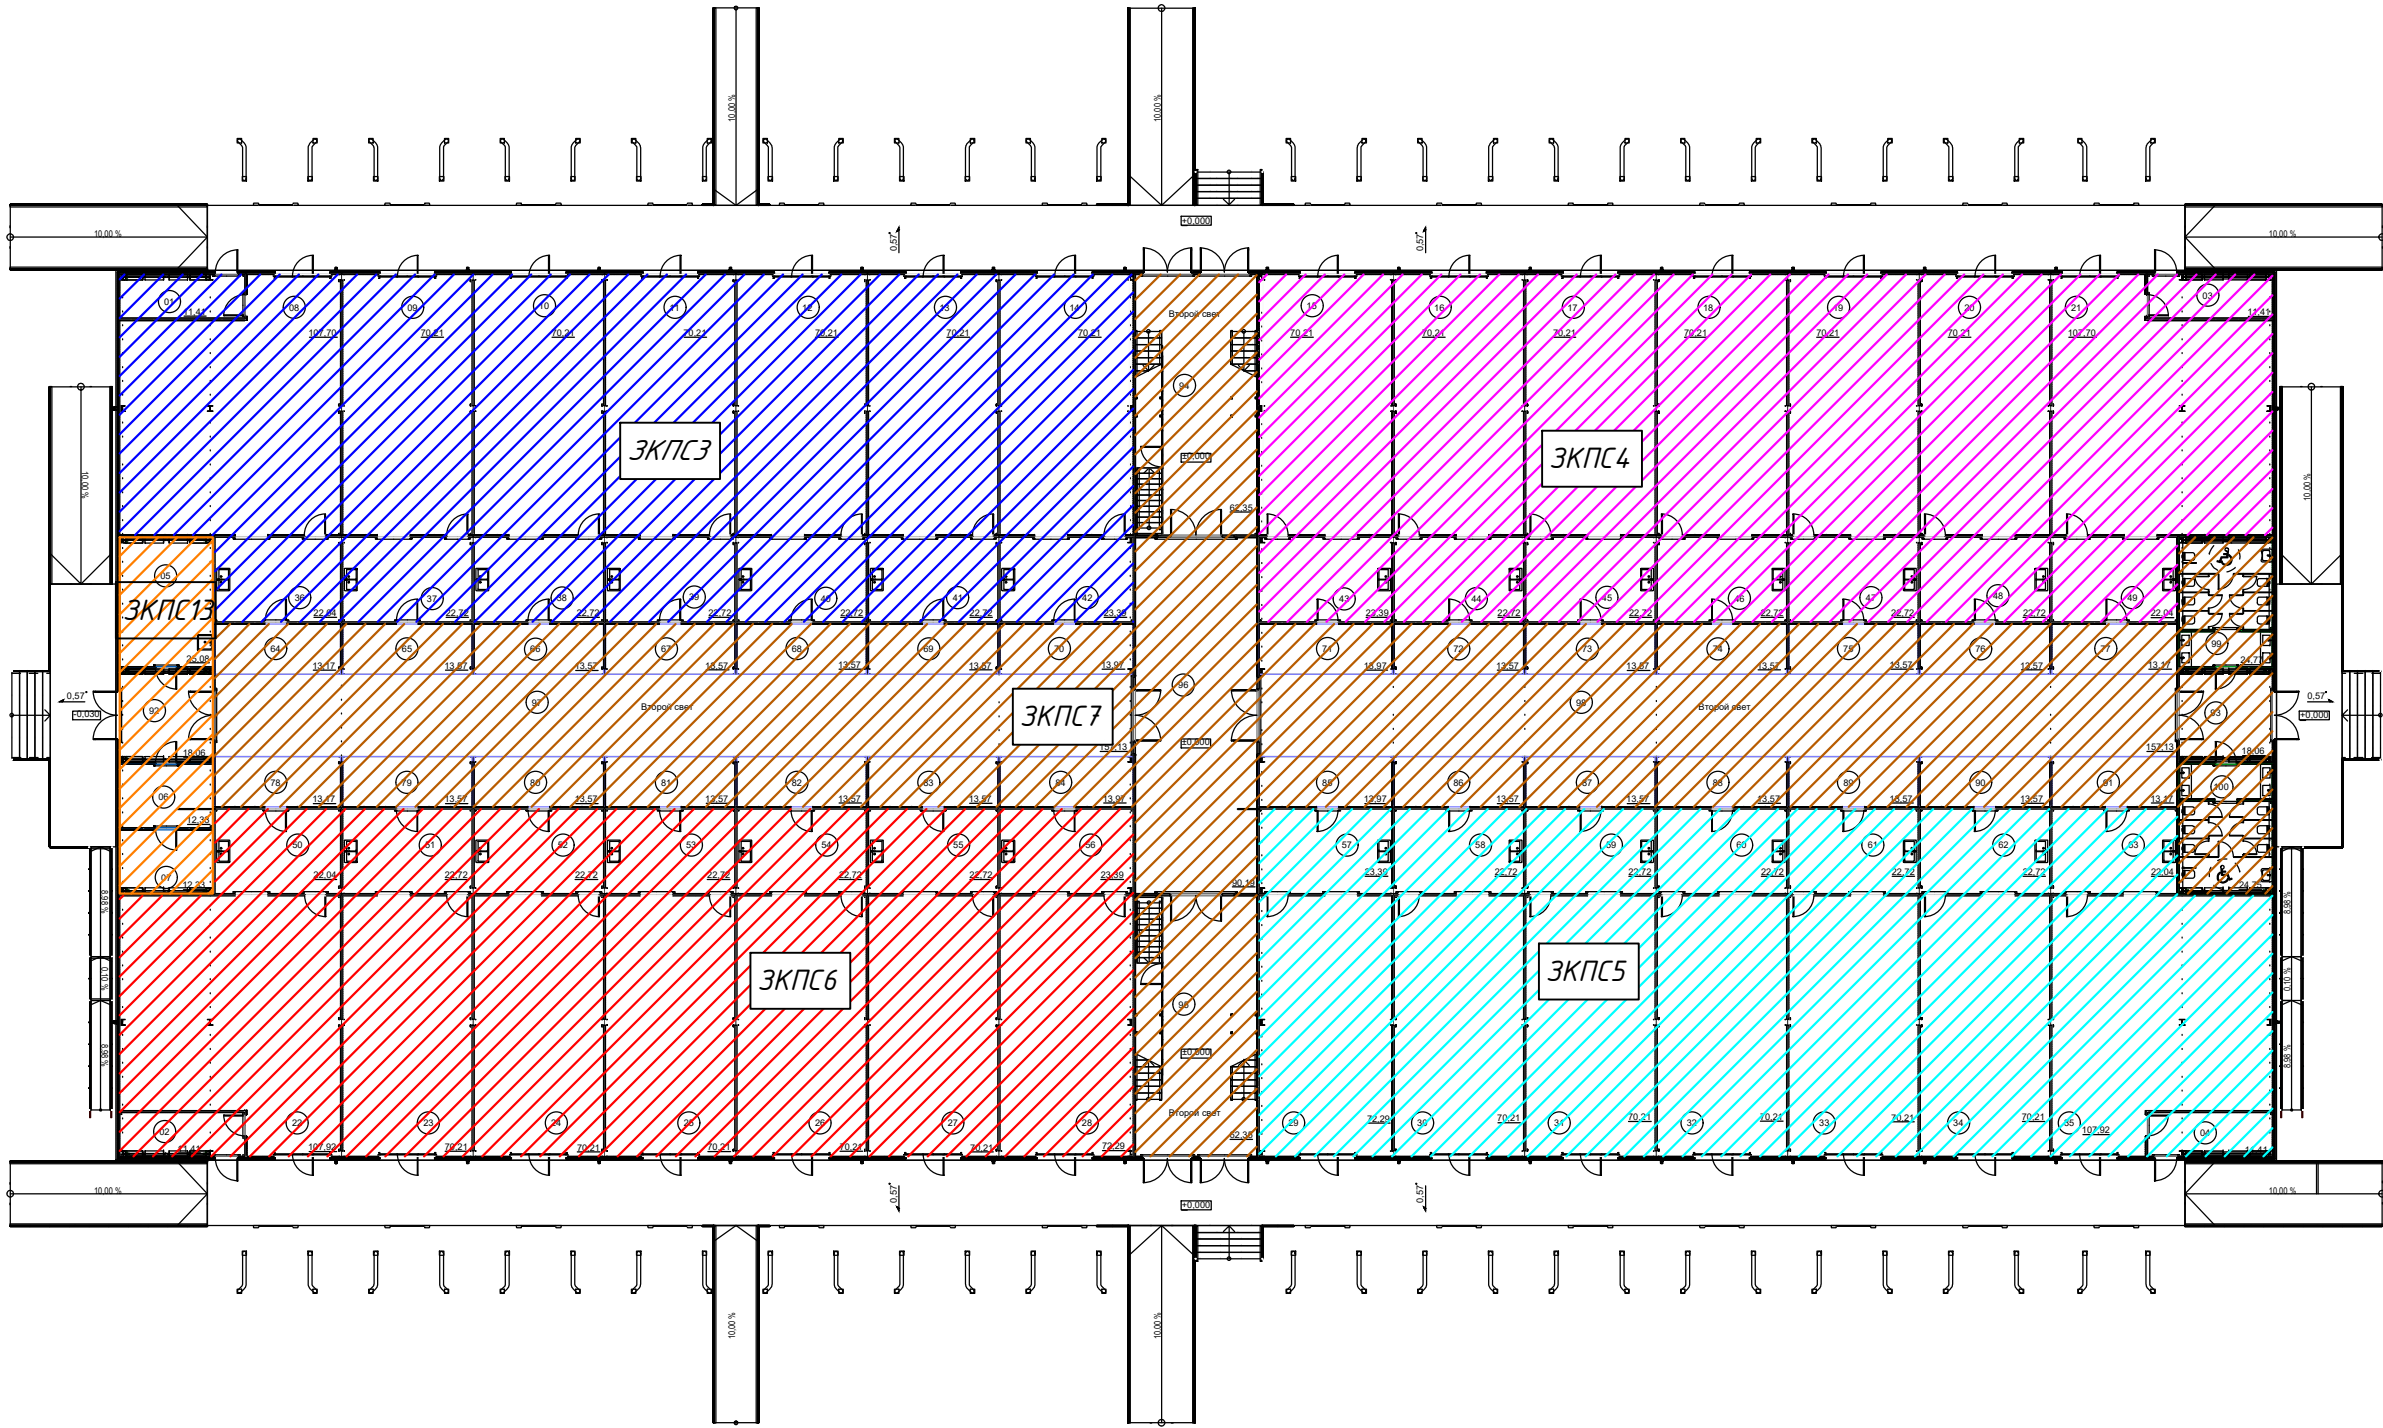

						ОПР-01/24/2024–КДЗ–АПСиСОУЭ			
						«Современный коммерческий оптово-продовольственный рынок (ОПР) по адресу: Донецкая область, г. Макеевка, Горняцкий район» Док-павильон Рыба-мясо №23			
Изм.	Колуч	Лист	N док	Подпись	Дата	Автоматическая установка пожарной сигнализации. Система оповещения и управления эвакуацией.	Страница	Лист	Листов
ГИП							Р	6	17
Разработал									
Н.контроль						План расположения зон ЭКПС на 1-м этаже	ООО "Технология"		


План расположения зон ЗКПС на 2-м этаже

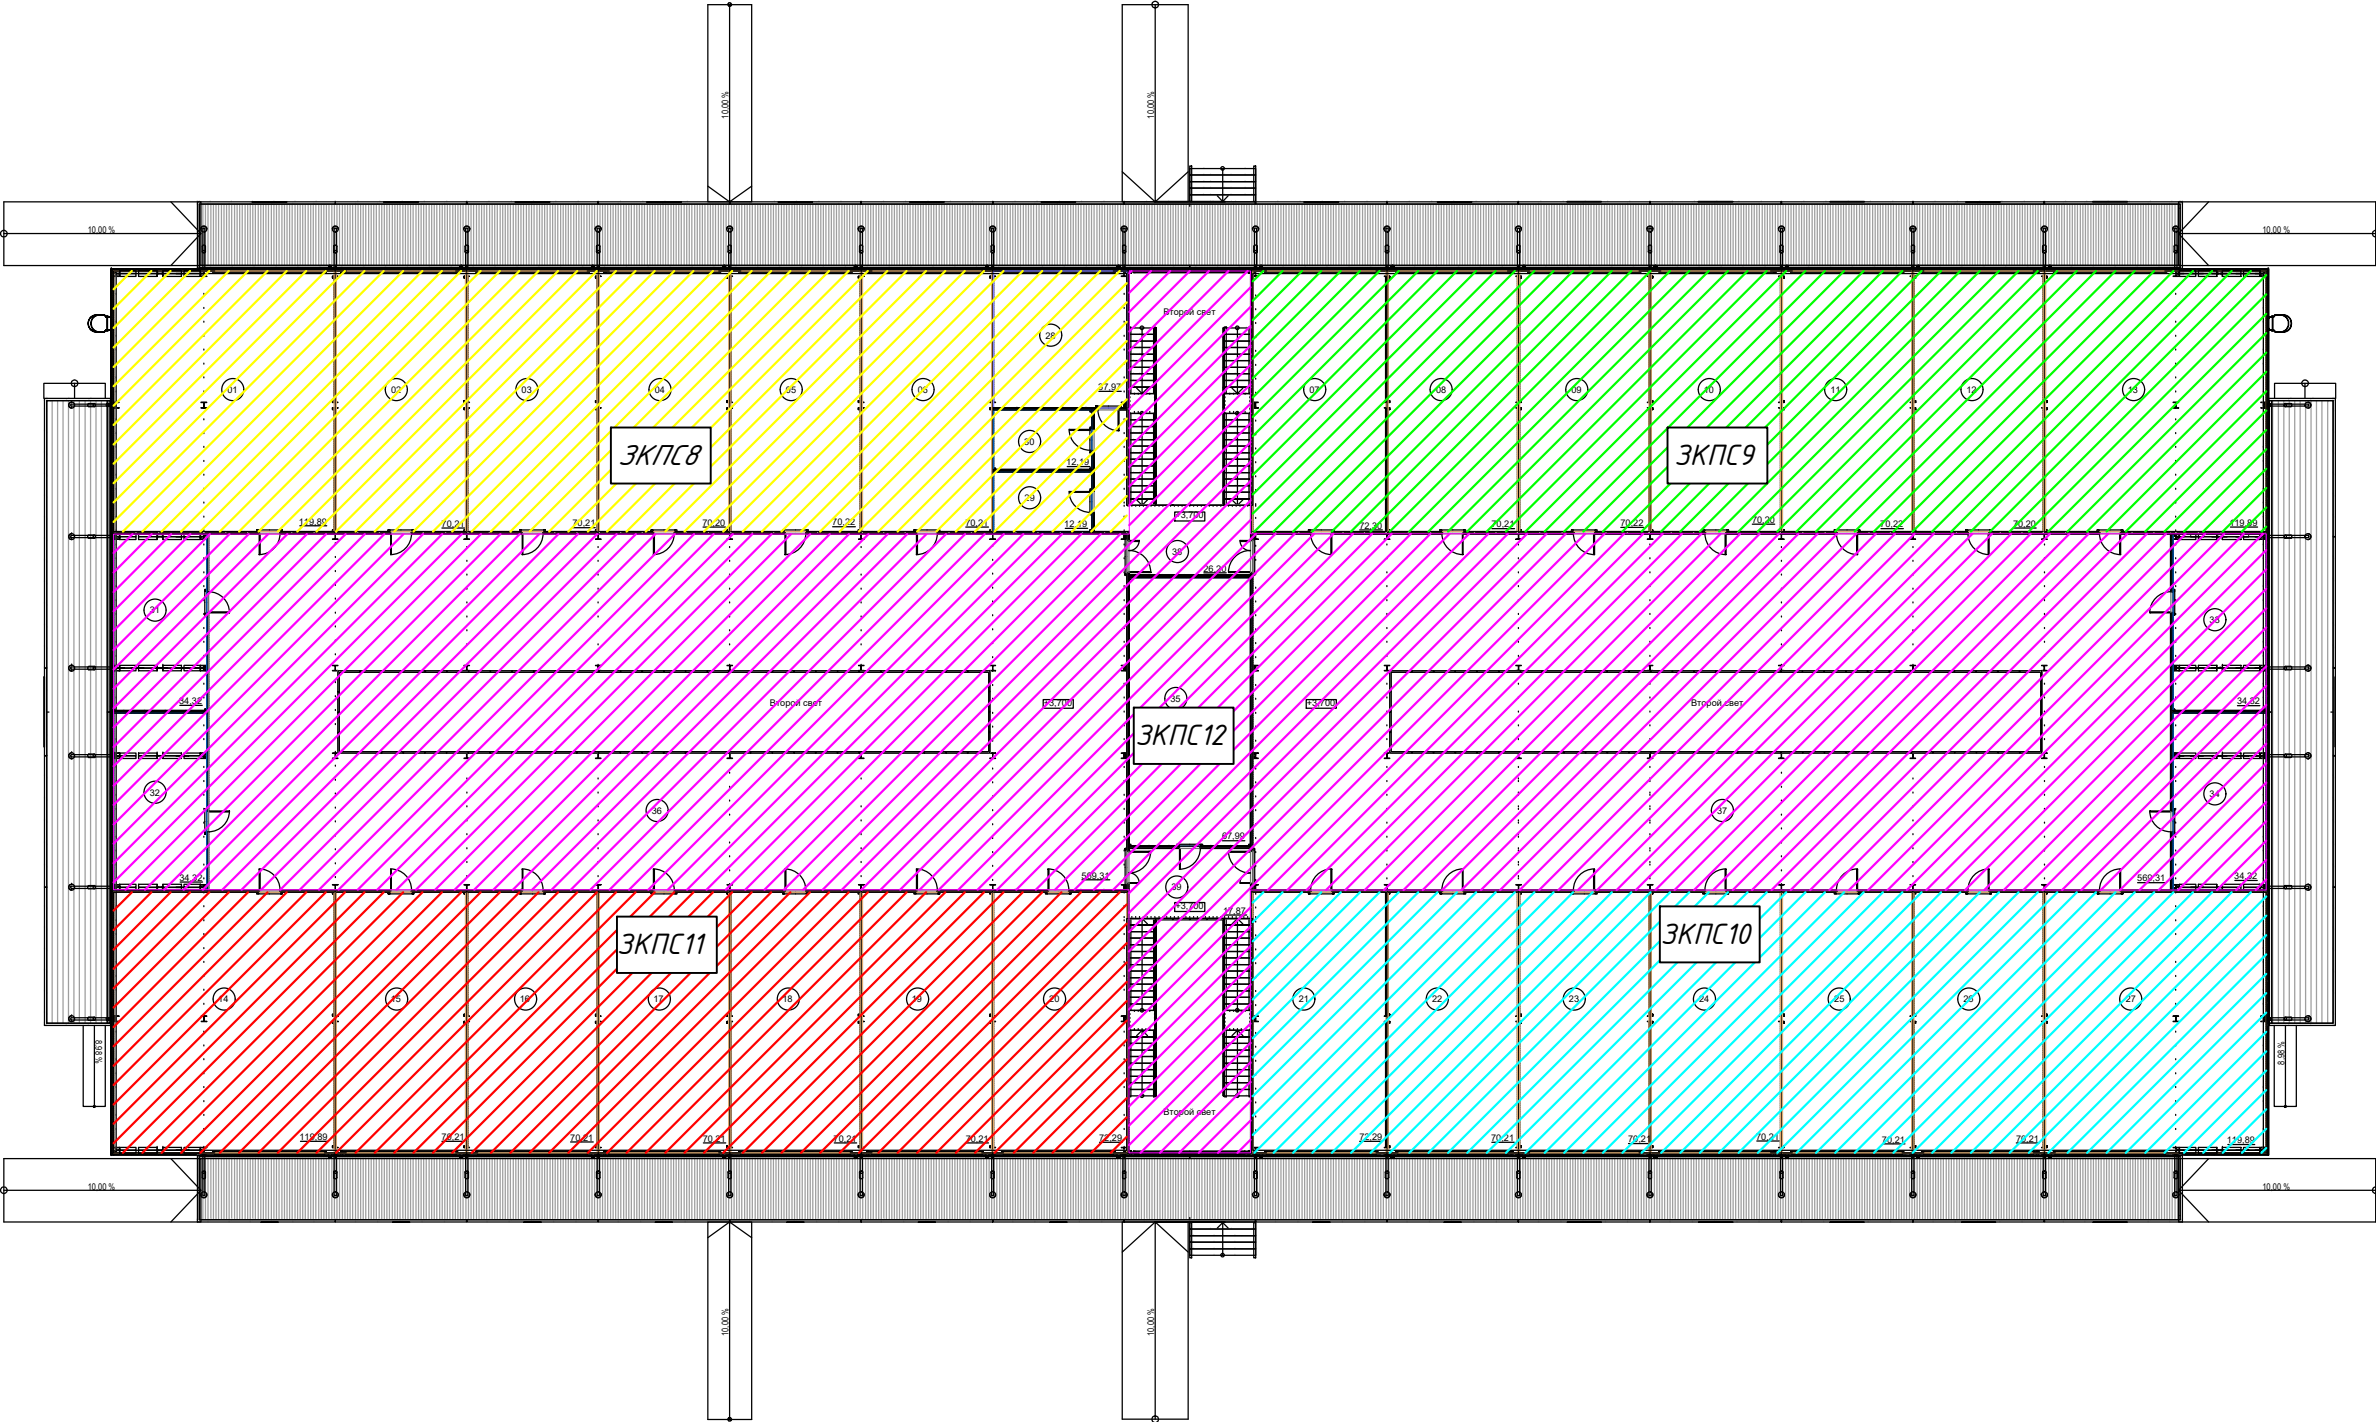

Номер помещения	Наименование	Площадь, м2	Кат. помещения
01	Кладовая	119,89	В-3
02	Кладовая	70,21	В-3
03	Кладовая	70,21	В-3
04	Кладовая	70,2	В-3
05	Кладовая	70,22	В-3
06	Кладовая	70,21	В-3
07	Кладовая	72,3	В-3
08	Кладовая	70,21	В-3
09	Кладовая	70,22	В-3
10	Кладовая	70,2	В-3
11	Кладовая	70,22	В-3
12	Кладовая	70,2	В-3
13	Кладовая	119,89	В-3
14	Кладовая	119,89	В-3
15	Кладовая	70,21	В-3
16	Кладовая	70,21	В-3
17	Кладовая	70,21	В-3
18	Кладовая	70,21	В-3
19	Кладовая	70,21	В-3
20	Кладовая	72,29	В-3
21	Кладовая	72,29	В-3
22	Кладовая	70,21	В-3
23	Кладовая	70,21	В-3
24	Кладовая	70,21	В-3
25	Кладовая	70,21	В-3
26	Кладовая	70,21	В-3
27	Кладовая	119,89	В-3
28	Рабочий кабинет	37,97	-
29	Кладовая уборочного инвентаря	12,19	В-3
30	Техническое помещение	12,19	В-3
31	Техническое помещение	34,32	В-3
32	Техническое помещение	34,32	В-3
33	Техническое помещение	34,32	В-3
34	Техническое помещение	34,32	В-3
35	Вент-камера	67,99	В-3
36	Холл	569,31	-
37	Холл	569,31	-
38	Лестничная площадка	26,2	-
39	Лестничная площадка	17,87	-
		3 550,95 м²	

						ОПР-01/24/2024-КДЗ-АПСиСУЭ		
						«Современный коммерческий оптово-продовольственный рынок (ОПР) по адресу: Донецкая область, г. Макеевка, Горняцкий район» Док-павильон Рыба-мясо №23		
Изм.	Колуч	Лист	№ док	Подпись	Дата	Автоматическая установка пожарной сигнализации. Система оповещения и управления эвакуацией.	Стадия	Лист
ГИП							Р	7
Разработал								17
Н.контроль						ППлан расположения зон ЗКПС на 2-м этаже	000 "Технология"	

План расположения оборудования и кабельных трасс в подвале

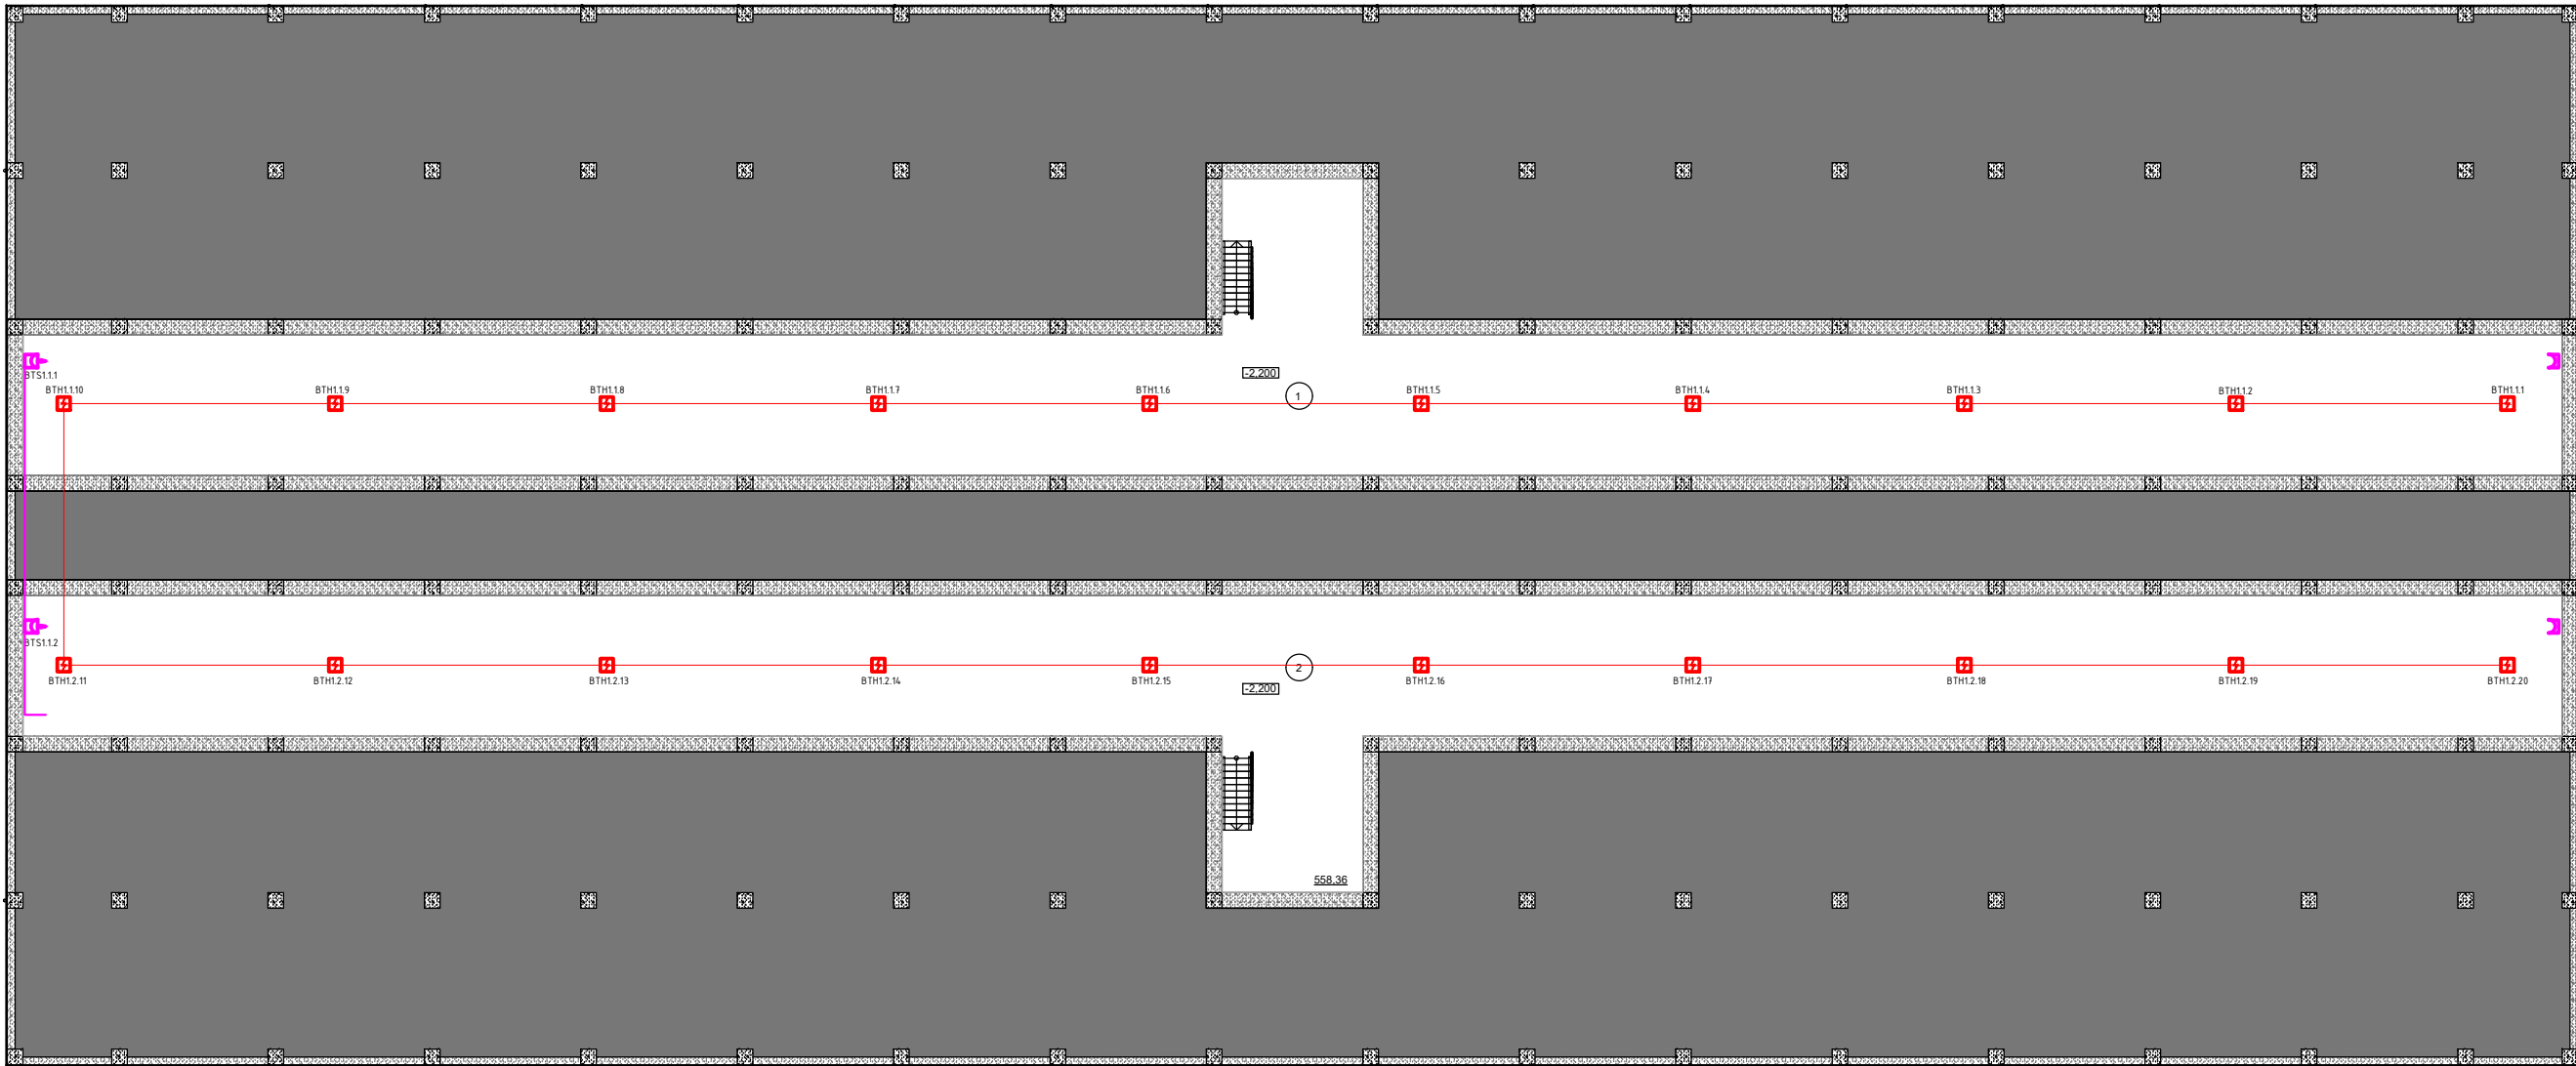


Номер помеще-ния	Наименование	Площадь, м2	Кат. поме-щ е-ния
1	Технический коридор	558,36	-
2	Технический коридор	558,36	-
		1 116,72 м²	

						ОПР-01/24/2024-КДЗ-АПСuCOУЭ		
						«Современный коммерческий оптово-продовольственный рынок (ОПР) по адресу: Донецкая область, г. Макеевка, Горняцкий район»		
						Док-павильон Рыба-мясо №23		
Изм.	Кол.уч	Лист	N док	Подпись	Дата	Автоматическая установка пожарной сигнализации. Система оповещения и управления эвакуацией.	Стадия	Лист
ГИП							Р	8
Разработал						План расположения оборудования и кабельных трасс в подвале		17
Н.контроль							ООО "Технология"	

План расположения оборудования и кабельных трасс на 1-м этаже

Номер по плану	Наименование	Площадь, м2	Кат. помещ.
01	Тамбур	11,41	-
02	Тамбур	11,41	-
03	Тамбур	11,41	-
04	Тамбур	11,41	-
05	Кладовая уборочного инвентаря	25,08	Б-3
06	ИТП	12,33	Б-3
07	Электрощитовая	12,33	Б-3
08	Разгрузочный тамбур	107,83	-
09	Разгрузочный тамбур	70,33	-
10	Разгрузочный тамбур	70,33	-
11	Разгрузочный тамбур	70,33	-
12	Разгрузочный тамбур	70,33	-
13	Разгрузочный тамбур	70,33	-
14	Разгрузочный тамбур	70,33	-
15	Разгрузочный тамбур	70,33	-
16	Разгрузочный тамбур	70,33	-
17	Разгрузочный тамбур	70,33	-
18	Разгрузочный тамбур	70,33	-
19	Разгрузочный тамбур	70,33	-
20	Разгрузочный тамбур	70,33	-
21	Разгрузочный тамбур	107,83	-
22	Разгрузочный тамбур	107,82	-
23	Разгрузочный тамбур	70,21	-
24	Разгрузочный тамбур	70,19	-
25	Разгрузочный тамбур	70,21	-
26	Разгрузочный тамбур	70,19	-
27	Разгрузочный тамбур	70,21	-
28	Разгрузочный тамбур	72,28	-
29	Разгрузочный тамбур	72,28	-
30	Разгрузочный тамбур	70,21	-
31	Разгрузочный тамбур	70,19	-
32	Разгрузочный тамбур	70,21	-
33	Разгрузочный тамбур	70,19	-
34	Разгрузочный тамбур	70,21	-
35	Разгрузочный тамбур	107,82	-
36	Зона подготовки товара	22,04	-
37	Зона подготовки товара	22,72	-
38	Зона подготовки товара	22,72	-
39	Зона подготовки товара	22,72	-
40	Зона подготовки товара	22,72	-
41	Зона подготовки товара	22,72	-
42	Зона подготовки товара	23,39	-
43	Зона подготовки товара	23,39	-
44	Зона подготовки товара	22,72	-
45	Зона подготовки товара	22,72	-
46	Зона подготовки товара	22,72	-
47	Зона подготовки товара	22,72	-
48	Зона подготовки товара	22,72	-
49	Зона подготовки товара	22,04	-
50	Зона подготовки товара	22,04	-
51	Зона подготовки товара	22,72	-
52	Зона подготовки товара	22,72	-
53	Зона подготовки товара	22,72	-
54	Зона подготовки товара	22,72	-
55	Зона подготовки товара	22,72	-
56	Зона подготовки товара	23,39	-
57	Зона подготовки товара	23,39	-
58	Зона подготовки товара	22,72	-
59	Зона подготовки товара	22,72	-
60	Зона подготовки товара	22,72	-
61	Зона подготовки товара	22,72	-
62	Зона подготовки товара	22,72	-
63	Зона подготовки товара	22,04	-
64	Выставочная зона	13,17	-
65	Выставочная зона	13,57	-
66	Выставочная зона	13,57	-
67	Выставочная зона	13,57	-
68	Выставочная зона	13,57	-
69	Выставочная зона	13,57	-
70	Выставочная зона	13,57	-
71	Выставочная зона	13,97	-
72	Выставочная зона	13,57	-
73	Выставочная зона	13,57	-
74	Выставочная зона	13,57	-
75	Выставочная зона	13,57	-
76	Выставочная зона	13,57	-
77	Выставочная зона	13,17	-
78	Выставочная зона	13,17	-
79	Выставочная зона	13,57	-
80	Выставочная зона	13,57	-
81	Выставочная зона	13,57	-
82	Выставочная зона	13,57	-
83	Выставочная зона	13,57	-
84	Выставочная зона	13,97	-
85	Выставочная зона	13,57	-
86	Выставочная зона	13,57	-
87	Выставочная зона	13,57	-
88	Выставочная зона	13,57	-
89	Выставочная зона	13,57	-
90	Выставочная зона	13,57	-
91	Выставочная зона	13,17	-
92	Тамбур	18,06	-
93	Тамбур	18,06	-
94	Тамбур-шлюз	62,35	-
95	Тамбур-шлюз	62,35	-
96	Торговый зал	95,19	-
97	Торговый зал	157,13	-
98	Торговый зал	157,13	-
99	СУ М	24,77	-
100	СУ Ж	24,75	-
		3 848,29 м²	

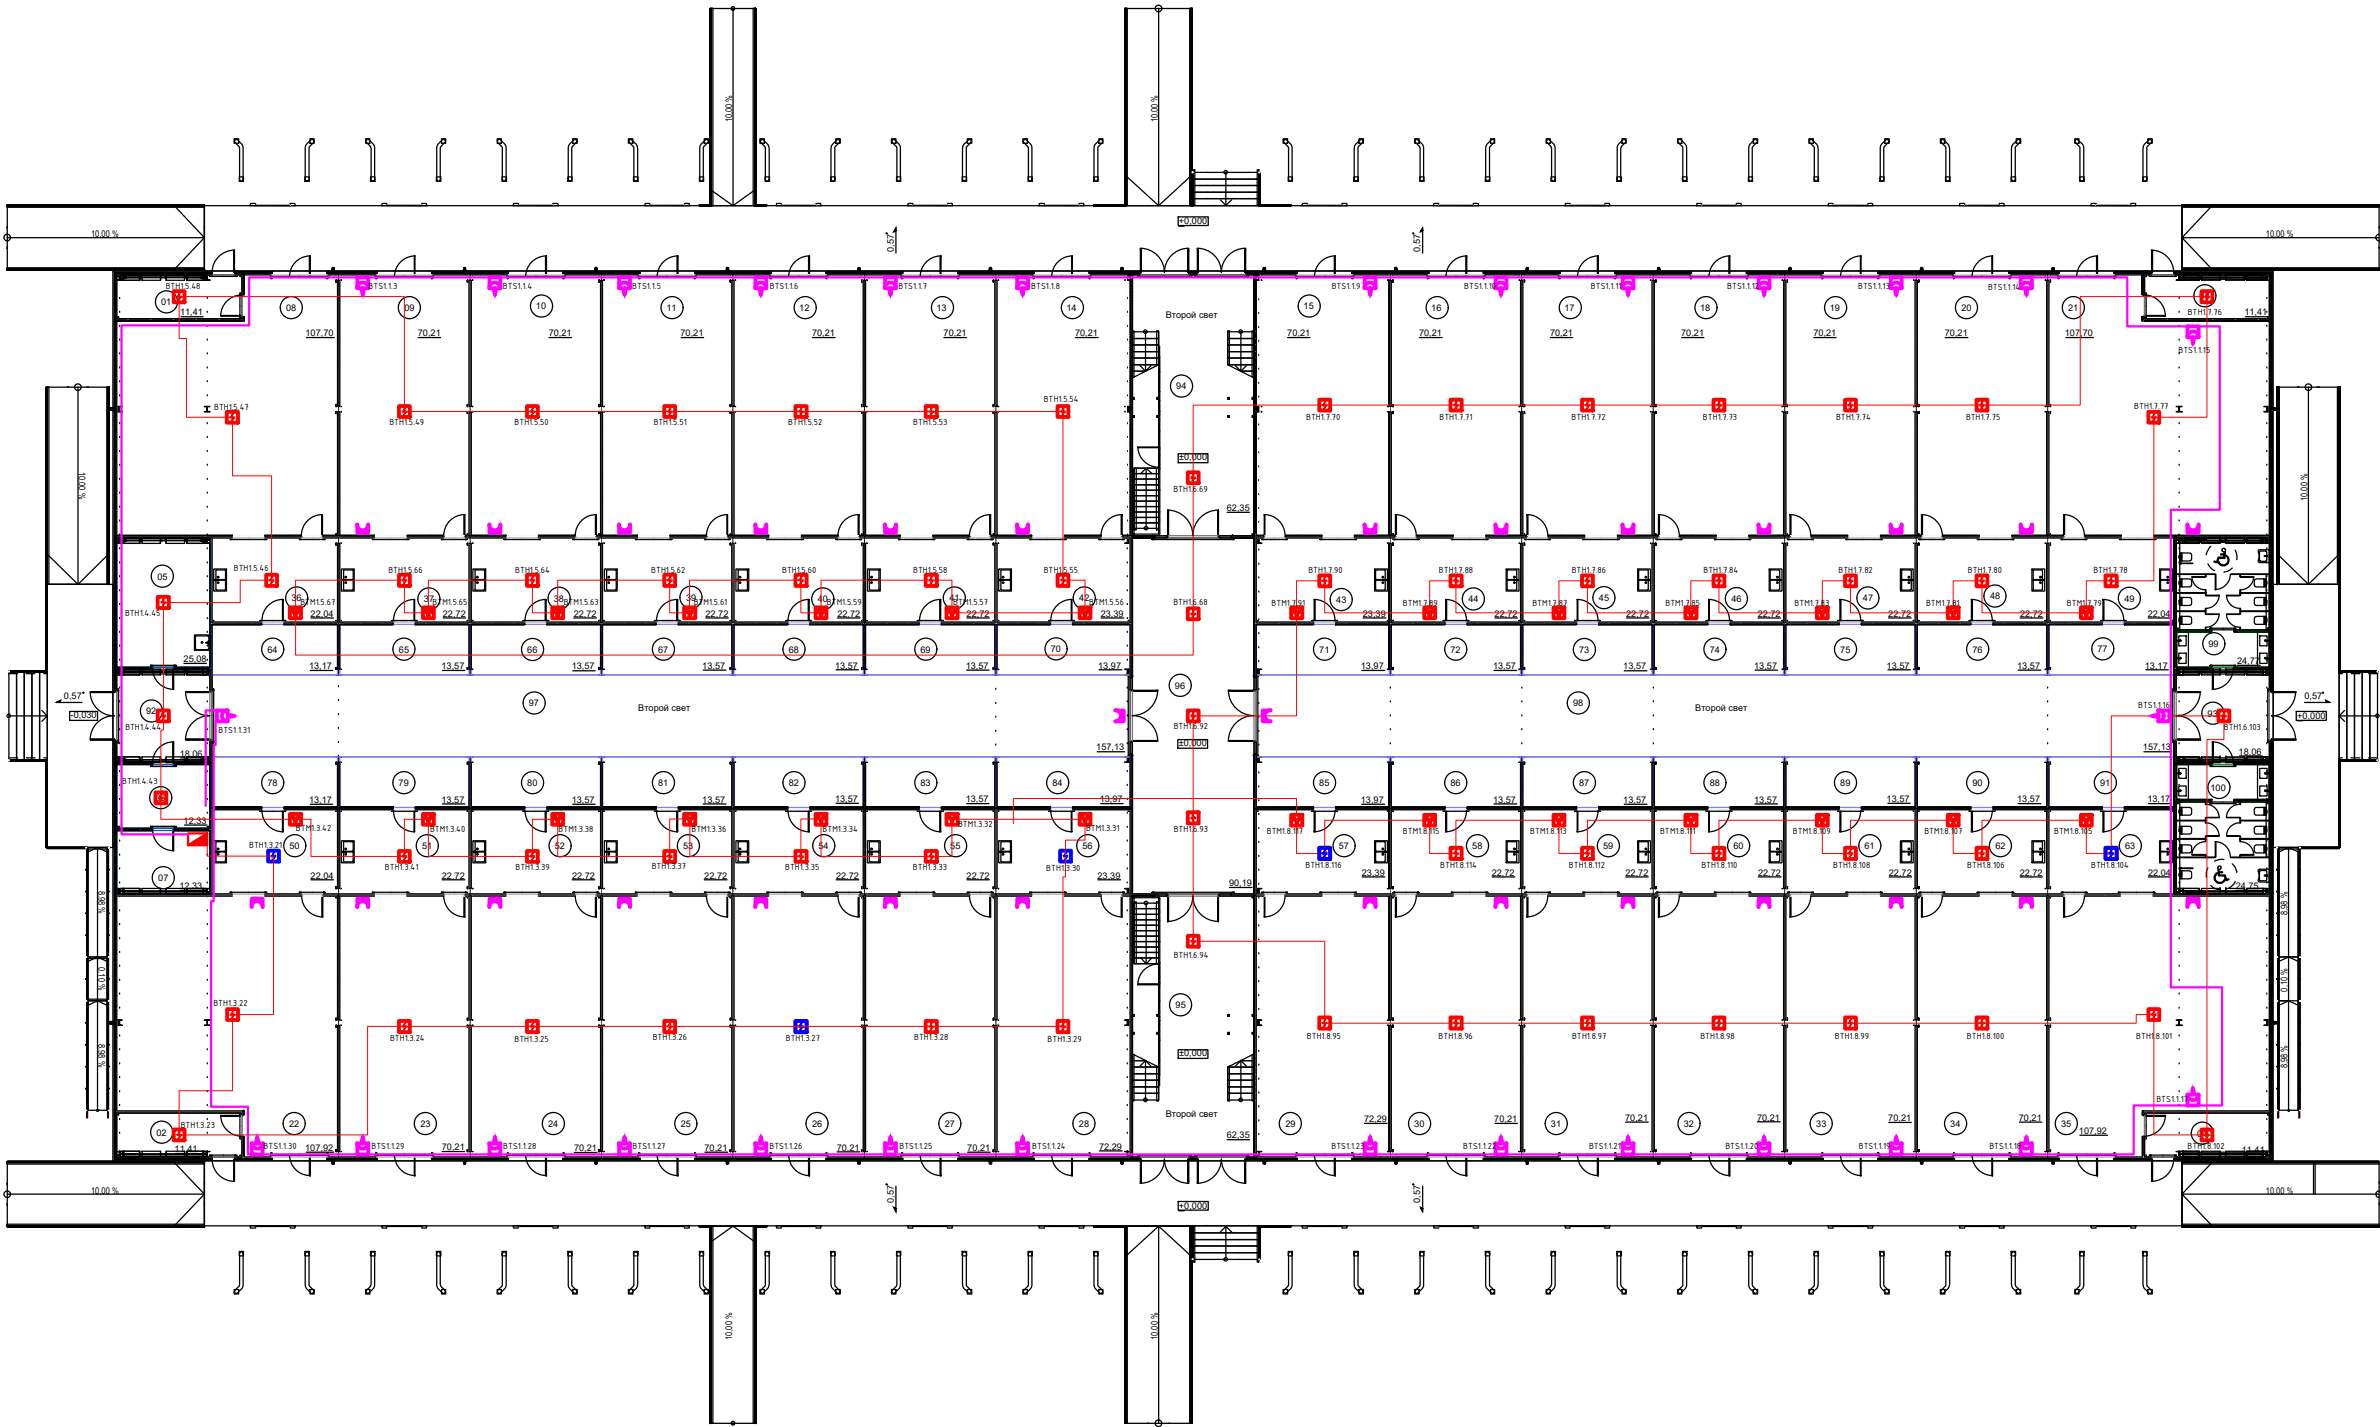

						ОПР-01/24/2024-КДЗ-АПСиСОУЗ		
						«Современный коммерческий оптово-продуктовый рынок (ОПР) по адресу: Донецкая область, г. Макеевка, Горняцкий район» Док-павильон Рыба-мясо №23		
Изм.	Кол.уч.	Лист	N док.	Погнись	Дата	Автоматическая установка пожарной сигнализации. Система оповещения и управления эвакуацией.	Страница	Листов
ГИП							Р	17
Разработал						План расположения оборудования и кабельных трасс на 1-м этаже	000 "Технология"	
Н.контроль								


План расположения оборудования и кабельных трасс на 2-м этаже

Номер помещения	Наименование	Площадь, м2	Кат. помещения
01	Кладовая	119,89	В-3
02	Кладовая	70,21	В-3
03	Кладовая	70,21	В-3
04	Кладовая	70,2	В-3
05	Кладовая	70,22	В-3
06	Кладовая	70,21	В-3
07	Кладовая	72,3	В-3
08	Кладовая	70,21	В-3
09	Кладовая	70,22	В-3
10	Кладовая	70,2	В-3
11	Кладовая	70,22	В-3
12	Кладовая	70,2	В-3
13	Кладовая	119,89	В-3
14	Кладовая	119,89	В-3
15	Кладовая	70,21	В-3
16	Кладовая	70,21	В-3
17	Кладовая	70,21	В-3
18	Кладовая	70,21	В-3
19	Кладовая	70,21	В-3
20	Кладовая	72,29	В-3
21	Кладовая	72,29	В-3
22	Кладовая	70,21	В-3
23	Кладовая	70,21	В-3
24	Кладовая	70,21	В-3
25	Кладовая	70,21	В-3
26	Кладовая	70,21	В-3
27	Кладовая	119,89	В-3
28	Рабочий кабинет	37,97	-
29	Кладовая уборочного инвентаря	12,19	В-3
30	Техническое помещение	12,19	В-3
31	Техническое помещение	34,32	В-3
32	Техническое помещение	34,32	В-3
33	Техническое помещение	34,32	В-3
34	Техническое помещение	34,32	В-3
35	Вент-камера	67,99	В-3
36	Холл	569,31	-
37	Холл	569,31	-
38	Лестничная площадка	26,2	-
39	Лестничная площадка	17,87	-
		3 550,95 м²	



						ОПР-01/24/2024–КДЗ–АПСыСОУЗ			
						«Современный коммерческий оптово-продовольственный рынок (ОПР) по адресу: Донецкая область, г. Макеевка, Горняцкий район» Док-павильон Рыба-мясо №23			
Изм.	Кол.уч	Лист	№ док	Подпись	Дата	Автоматическая установка пожарной сигнализации. Система оповещения и управления эвакуацией.	Страница	Лист	Листов
ГИП							Р	10	17
Разработал									
Н.контроль						План расположения оборудования и кабельных трасс на 2-м этаже	000 “Технология”		

План расположения оборудования и кабельных трасс системы светового оповещения в подвале

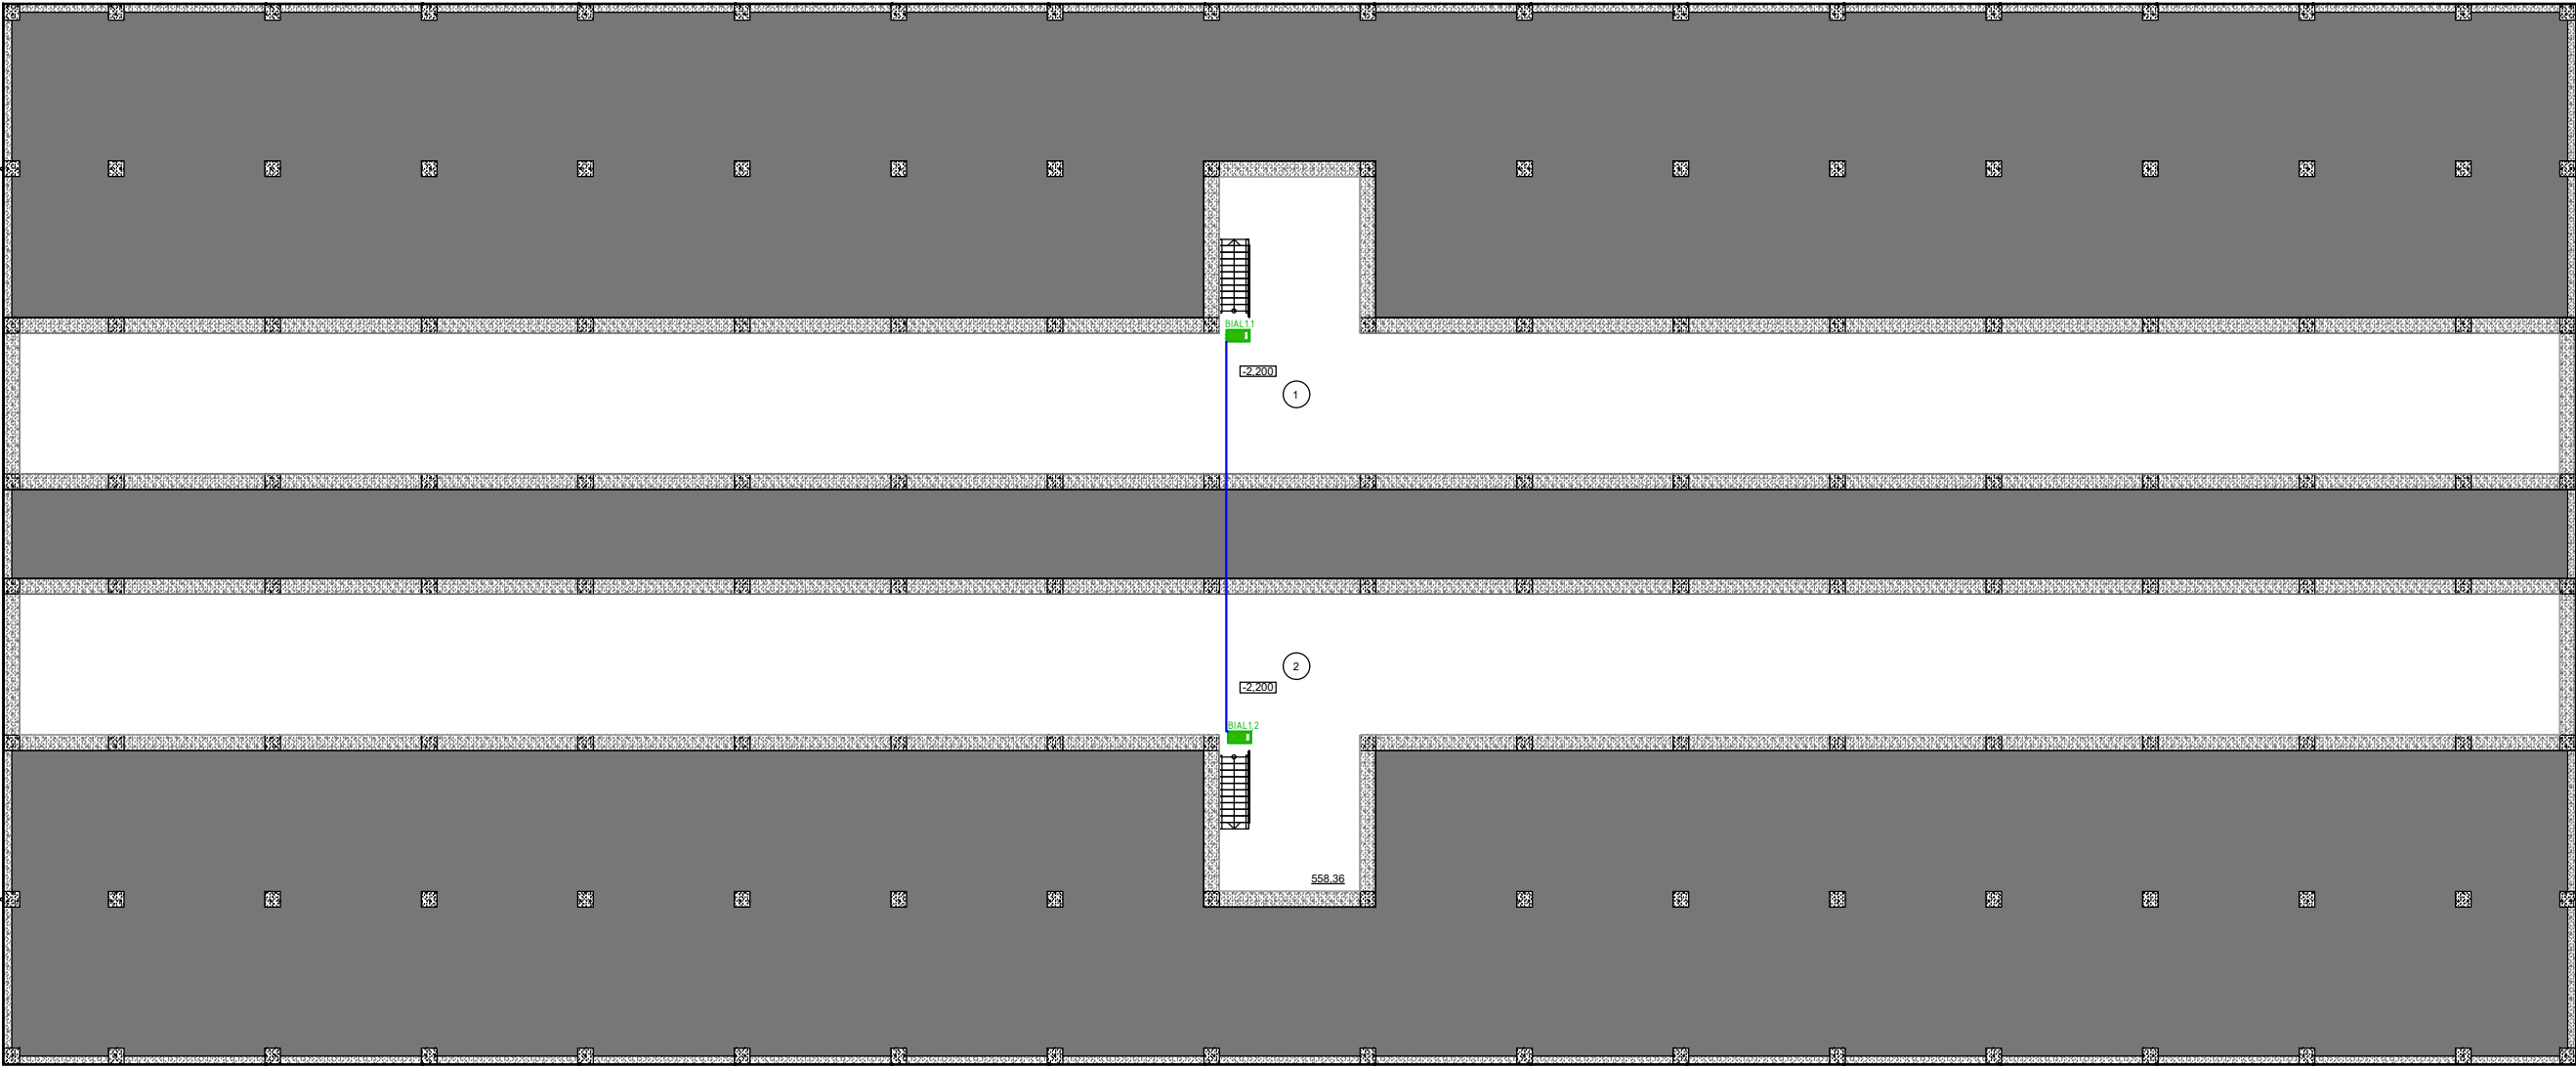


Номер помеще-ния	Наименование	Площадь, м2	Кат. поме-щ е-ния
1	Технический коридор	558,36	-
2	Технический коридор	558,36	-
		1 116,72 м²	

						ОПР-01/24/2024-КДЗ-АПСuCOУЭ		
						«Современный коммерческий оптово-продовольственный рынок (ОПР) по адресу: Донецкая область, г. Макеевка, Горняцкий район»		
						Док-павильон Рыба-мясо №23		
Изм.	Кол.уч	Лист	N док	Подпись	Дата	Автоматическая установка пожарной сигнализации. Система оповещения и управления эвакуацией.	Стадия	Лист
ГИП							Р	11
Разработал						План расположения оборудования и кабельных трасс системы светового оповещения в подвале		17
Н.контроль							ООО "Технология"	

План расположения оборудования и кабельных трасс системы светового оповещения 1-м этаже


Номер пояса цифры	Наименование	Площадь, м2	Кат. помеще- ния
01	Тамбур	11,41	-
02	Тамбур	11,41	-
03	Тамбур	11,41	-
04	Тамбур	11,41	-
05	Кладовая уборочного инвентаря	25,08	В-3
06	АТП	12,33	В-3
07	Электрощитовая	12,33	В-3
08	Разгрузочный тамбур	107,83	-
09	Разгрузочный тамбур	70,33	-
10	Разгрузочный тамбур	70,33	-
11	Разгрузочный тамбур	70,33	-
12	Разгрузочный тамбур	70,33	-
13	Разгрузочный тамбур	70,33	-
14	Разгрузочный тамбур	70,33	-
15	Разгрузочный тамбур	70,33	-
16	Разгрузочный тамбур	70,33	-
17	Разгрузочный тамбур	70,33	-
18	Разгрузочный тамбур	70,33	-
19	Разгрузочный тамбур	70,33	-
20	Разгрузочный тамбур	70,33	-
21	Разгрузочный тамбур	107,83	-
22	Разгрузочный тамбур	107,82	-
23	Разгрузочный тамбур	70,21	-
24	Разгрузочный тамбур	70,18	-
25	Разгрузочный тамбур	70,21	-
26	Разгрузочный тамбур	70,18	-
27	Разгрузочный тамбур	70,21	-
28	Разгрузочный тамбур	72,28	-
29	Разгрузочный тамбур	72,28	-
30	Разгрузочный тамбур	70,21	-
31	Разгрузочный тамбур	70,18	-
32	Разгрузочный тамбур	70,21	-
33	Разгрузочный тамбур	70,18	-
34	Разгрузочный тамбур	70,21	-
35	Разгрузочный тамбур	107,82	-
36	Зона подготовки товара	22,04	-
37	Зона подготовки товара	22,72	-
38	Зона подготовки товара	22,72	-
39	Зона подготовки товара	22,72	-
40	Зона подготовки товара	22,72	-
41	Зона подготовки товара	22,72	-
42	Зона подготовки товара	23,38	-
43	Зона подготовки товара	23,38	-
44	Зона подготовки товара	22,72	-
45	Зона подготовки товара	22,72	-
46	Зона подготовки товара	22,72	-
47	Зона подготовки товара	22,72	-
48	Зона подготовки товара	22,72	-
49	Зона подготовки товара	22,04	-
50	Зона подготовки товара	22,04	-
51	Зона подготовки товара	22,72	-
52	Зона подготовки товара	22,72	-
53	Зона подготовки товара	22,72	-
54	Зона подготовки товара	22,72	-
55	Зона подготовки товара	22,72	-
56	Зона подготовки товара	22,72	-
57	Зона подготовки товара	23,38	-
58	Зона подготовки товара	23,38	-
59	Зона подготовки товара	22,72	-
60	Зона подготовки товара	22,72	-
61	Зона подготовки товара	22,72	-
62	Зона подготовки товара	22,72	-
63	Зона подготовки товара	22,04	-
64	Выставочная зона	13,17	-
65	Выставочная зона	13,57	-
66	Выставочная зона	13,57	-
67	Выставочная зона	13,57	-
68	Выставочная зона	13,57	-
69	Выставочная зона	13,57	-
70	Выставочная зона	13,97	-
71	Выставочная зона	13,97	-
72	Выставочная зона	13,57	-
73	Выставочная зона	13,57	-
74	Выставочная зона	13,57	-
75	Выставочная зона	13,57	-
76	Выставочная зона	13,57	-
77	Выставочная зона	13,17	-
78	Выставочная зона	13,17	-
79	Выставочная зона	13,57	-
80	Выставочная зона	13,57	-
81	Выставочная зона	13,57	-
82	Выставочная зона	13,57	-
83	Выставочная зона	13,57	-
84	Выставочная зона	13,97	-
85	Выставочная зона	13,97	-
86	Выставочная зона	13,57	-
87	Выставочная зона	13,57	-
88	Выставочная зона	13,57	-
89	Выставочная зона	13,57	-
90	Выставочная зона	13,57	-
91	Выставочная зона	13,17	-
92	Тамбур	18,06	-
93	Тамбур	18,06	-
94	Тамбур-ширма	62,36	-
95	Тамбур-ширма	62,36	-
96	Торговый зал	90,19	-
97	Торговый зал	197,13	-
98	Торговый зал	197,13	-
99	СУ Ж	24,77	-
100	СУ Ж	24,75	-
		3 648,29	

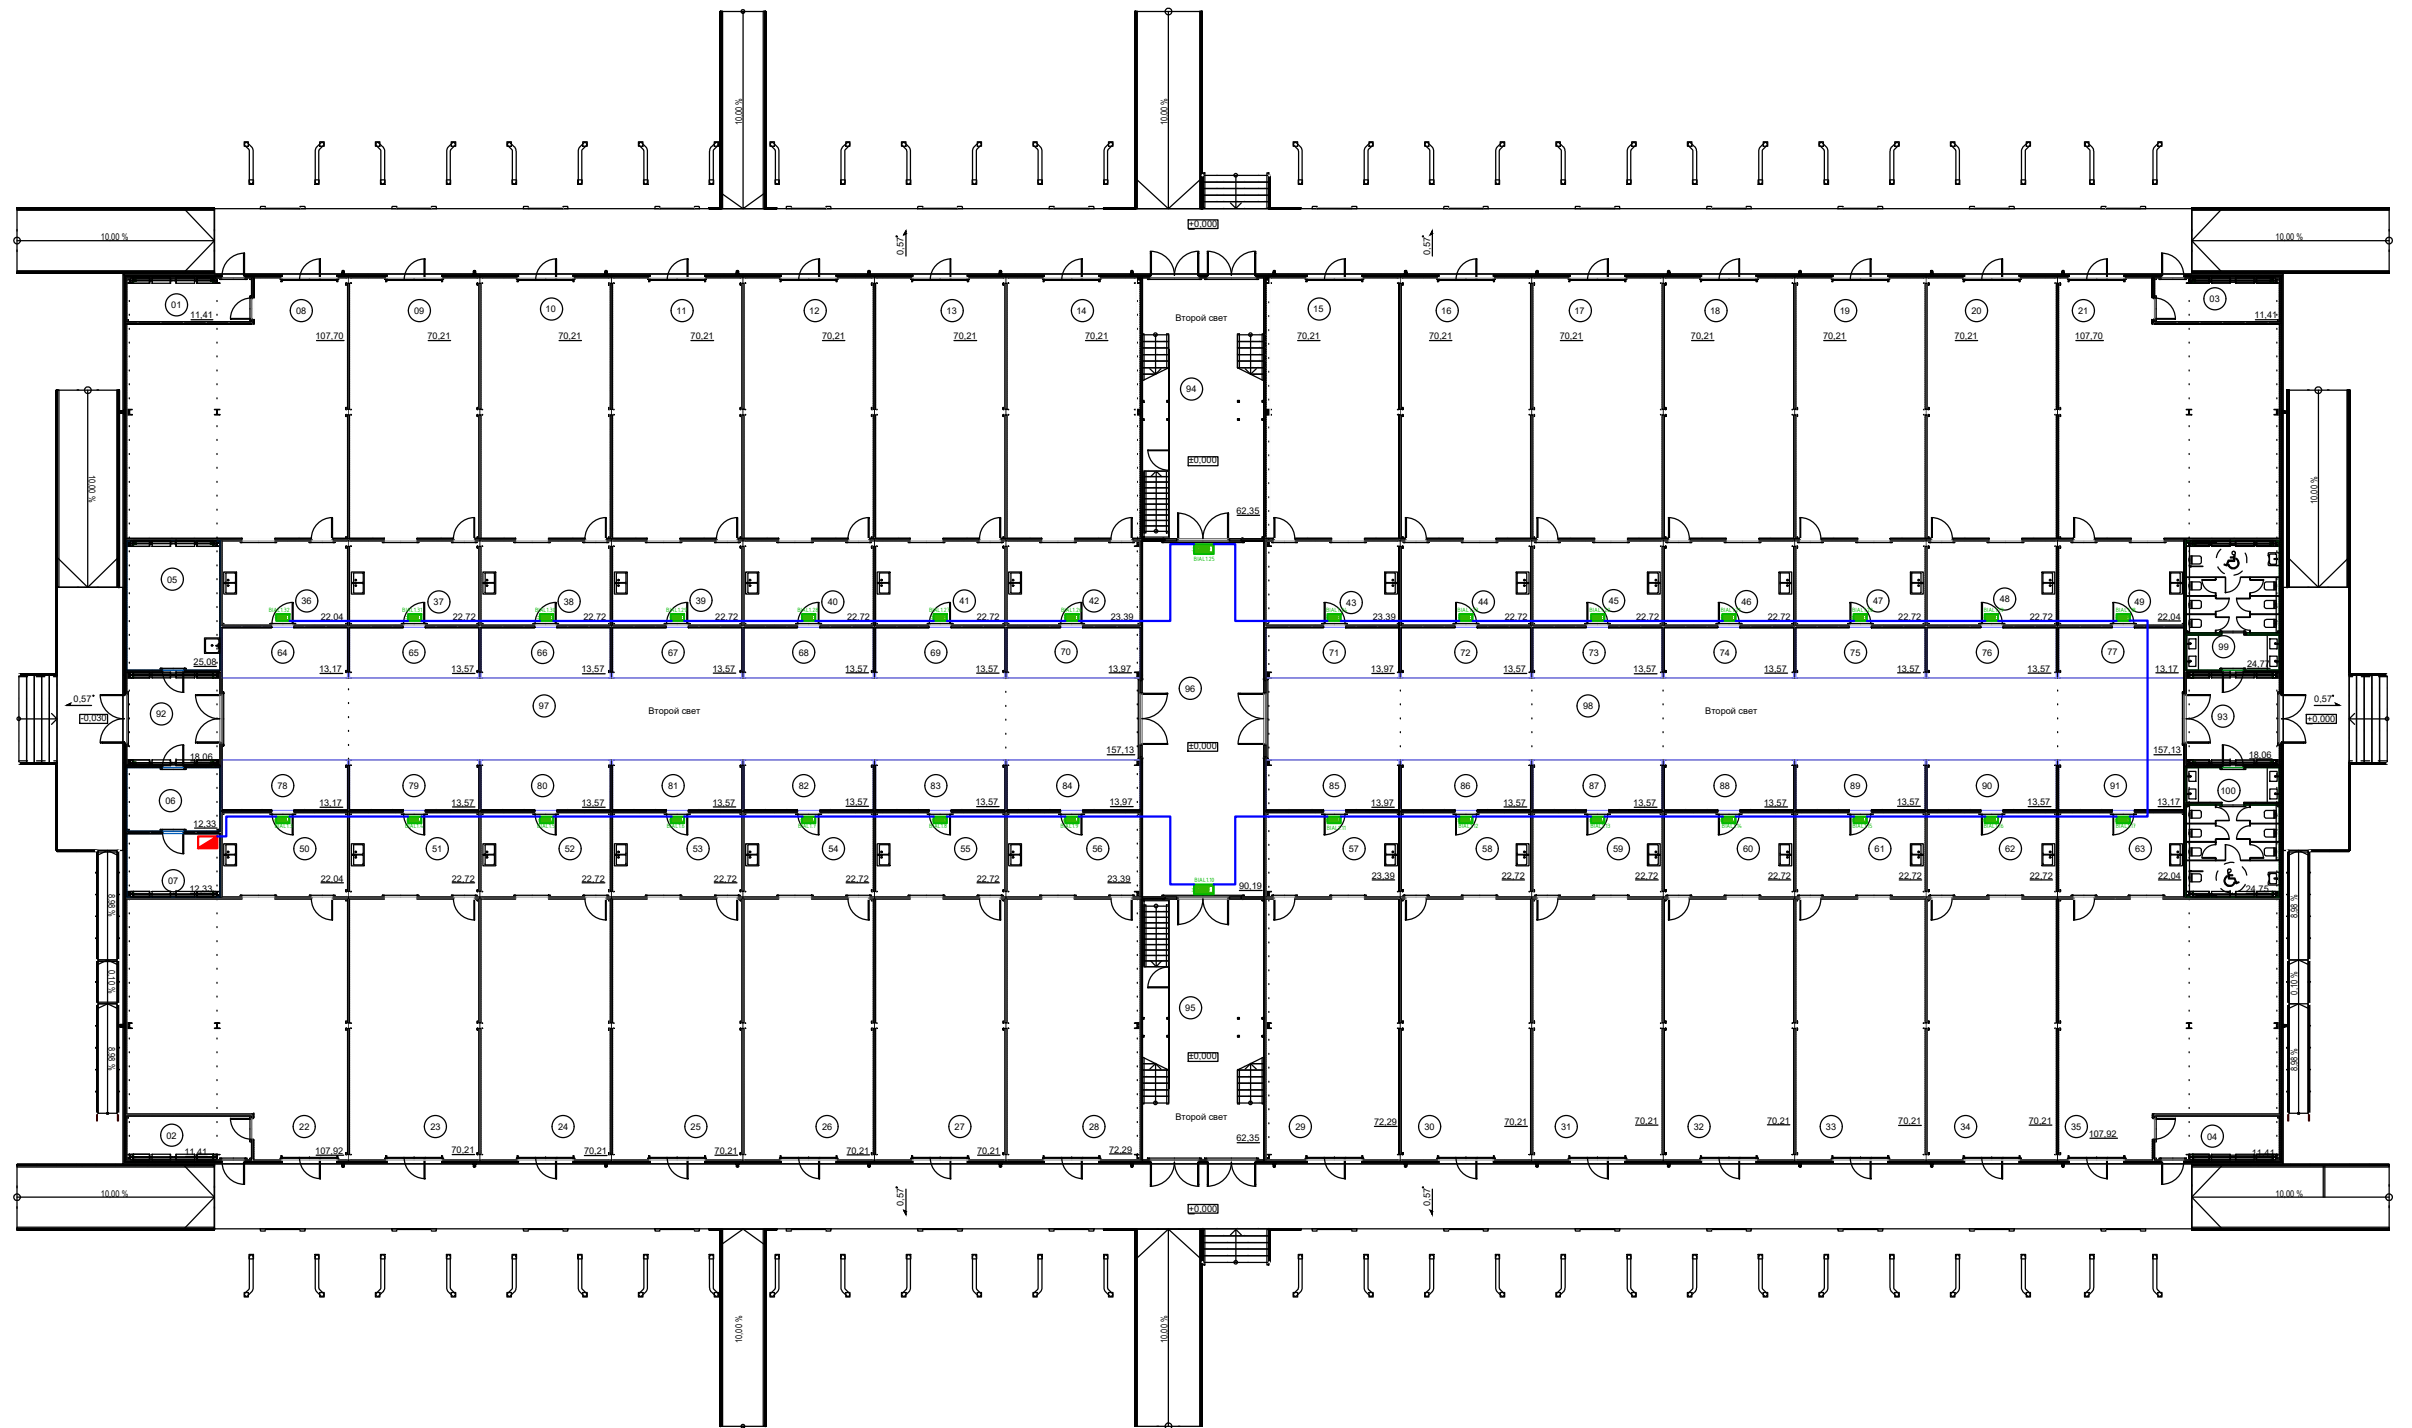

						ОПР-01/24/2024-КДЗ-АПСсСОУЭ					
						«Современный коммерческий оптово-продовольственный рынок (ОПР) по адресу: Донецкая область, г. Макеевка, Горняцкий район» Док-павильон Рыба-мясо №23					
Изм.	Колуч	Лист	№ док	Подпись	Дата				Статус	Лист	Листов
ГИП						Автоматическая установка пожарной сигнализации. Система оповещения и управления эвакуацией.			П	12	17
Разработал											
Н. контроль						План расположения оборудования и кабельных трасс системы светового оповещения 1-м этаже			ООО "Технология"		


План расположения оборудования и кабельных трасс системы светового оповещения 2-м этаже

Номер помещения	Наименование	Площадь, м2	Кат. помещения
01	Кладовая	119,89	В-3
02	Кладовая	70,21	В-3
03	Кладовая	70,21	В-3
04	Кладовая	70,2	В-3
05	Кладовая	70,22	В-3
06	Кладовая	70,21	В-3
07	Кладовая	72,3	В-3
08	Кладовая	70,21	В-3
09	Кладовая	70,22	В-3
10	Кладовая	70,2	В-3
11	Кладовая	70,22	В-3
12	Кладовая	70,2	В-3
13	Кладовая	119,89	В-3
14	Кладовая	119,89	В-3
15	Кладовая	70,21	В-3
16	Кладовая	70,21	В-3
17	Кладовая	70,21	В-3
18	Кладовая	70,21	В-3
19	Кладовая	70,21	В-3
20	Кладовая	72,29	В-3
21	Кладовая	72,29	В-3
22	Кладовая	70,21	В-3
23	Кладовая	70,21	В-3
24	Кладовая	70,21	В-3
25	Кладовая	70,21	В-3
26	Кладовая	70,21	В-3
27	Кладовая	119,89	В-3
28	Рабочий кабинет	37,97	-
29	Кладовая уборочного инвентаря	12,19	В-3
30	Техническое помещение	12,19	В-3
31	Техническое помещение	34,32	В-3
32	Техническое помещение	34,32	В-3
33	Техническое помещение	34,32	В-3
34	Техническое помещение	34,32	В-3
35	Вент-камера	67,99	В-3
36	Холл	569,31	-
37	Холл	569,31	-
38	Лестничная площадка	26,2	-
39	Лестничная площадка	17,87	-
		3 550,95 м²	

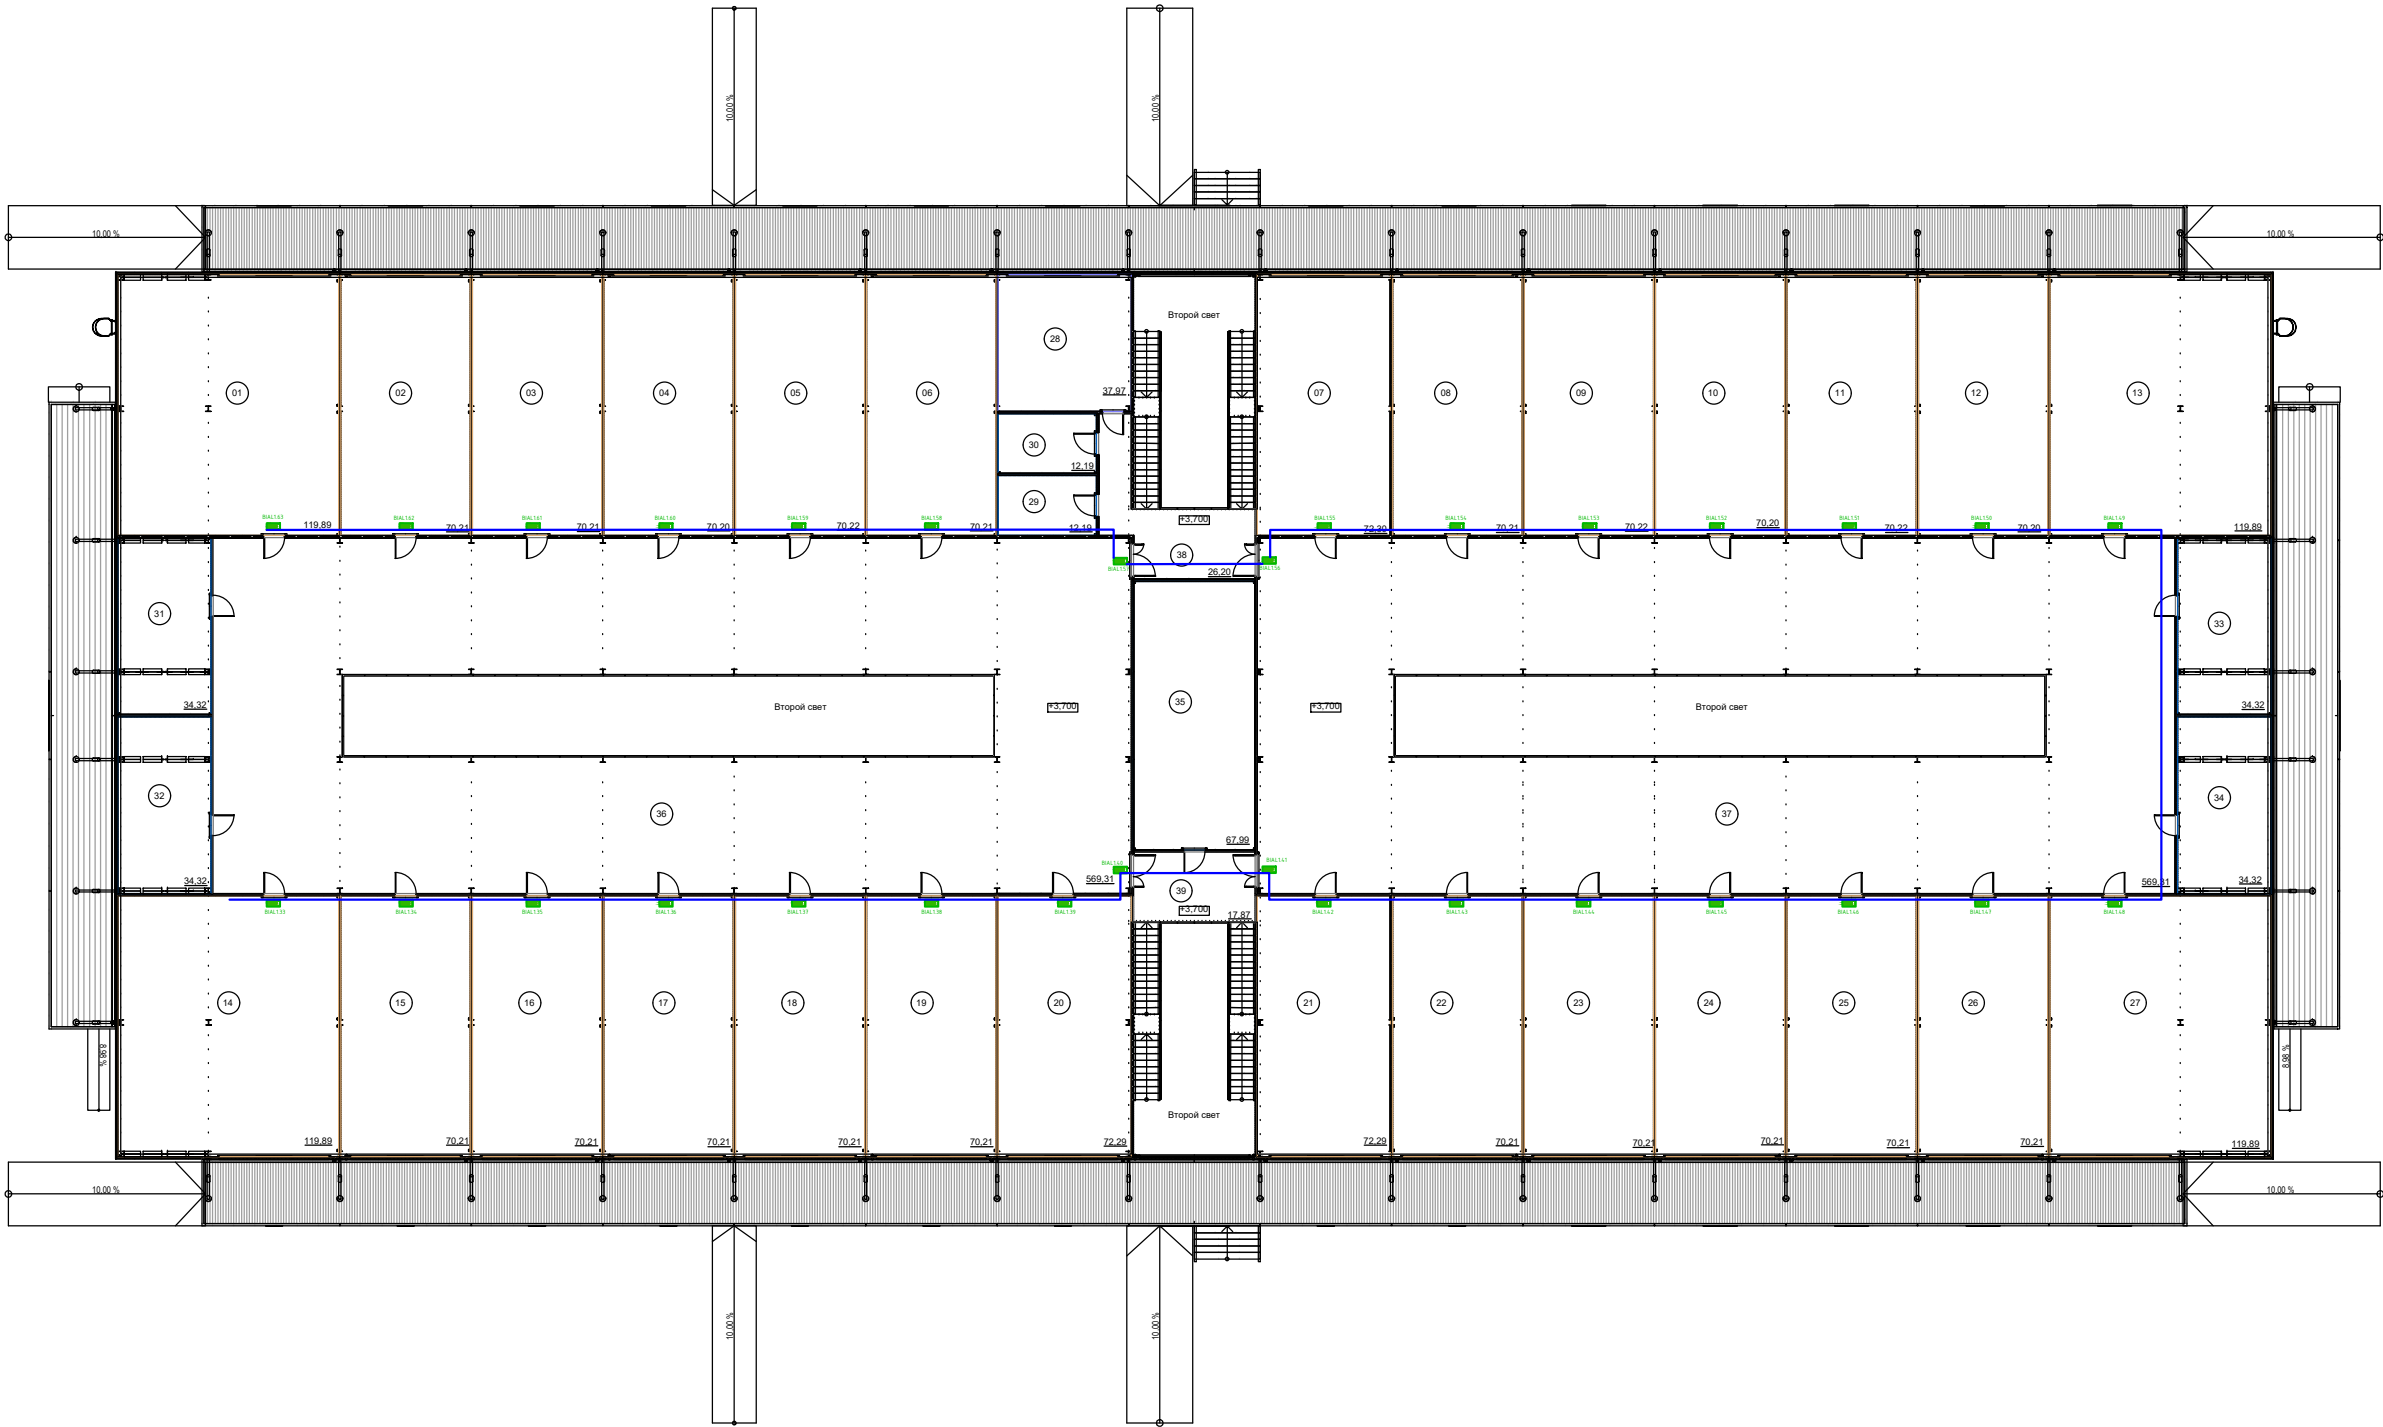

						ОПР-01/24/2024-КДЗ-АПСиСОУЭ		
						«Современный коммерческий оптово-продуктовый рынок (ОПР) по адресу: Донецкая область, г. Макеевка, Горняцкий район» Док-павильон Рыба-мясо №23		
Изм.	Кол.уч.	Лист	N док.	Погнись	Дата	Автоматическая установка пожарной сигнализации. Система оповещения и управления эвакуацией.	Стадия	Лист
ГИП							Р	13
Разработал						План расположения оборудования и кабельных трасс системы светового оповещения 2-м этаже		17
Н.контроль							000 "Технология"	

План расположения оборудования и кабельных трасс системы речевого оповещения в подвале

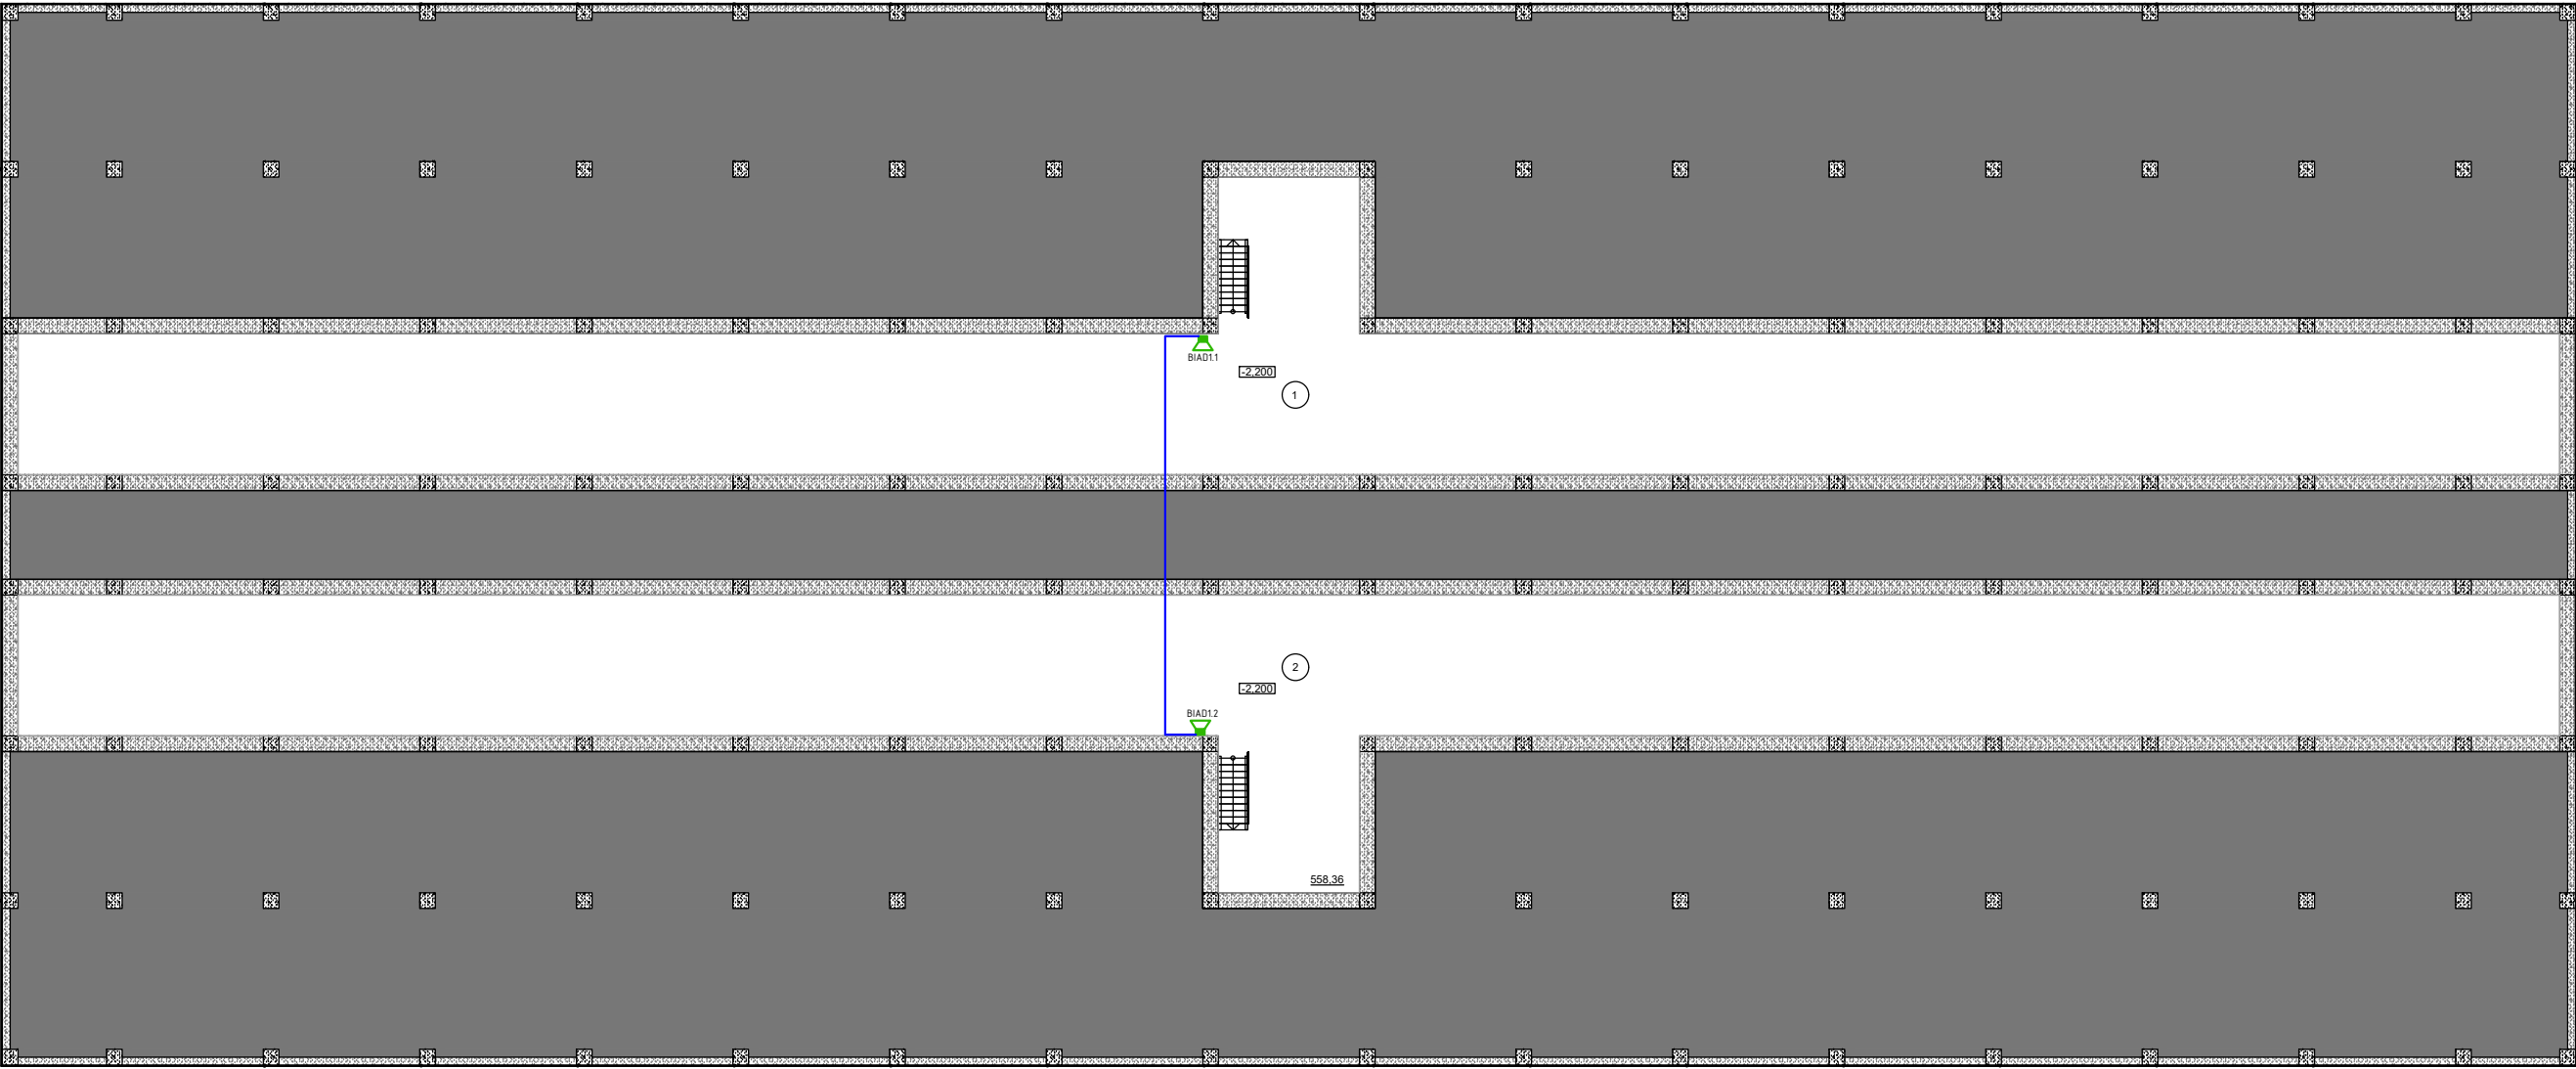


Номер помеще-ния	Наименование	Площадь, м2	Кат. поме-щ е-ния
1	Технический коридор	558,36	-
2	Технический коридор	558,36	-
		1 116,72 м²	

						ОПР-01/24/2024-КДЗ-АПСuCOУЭ		
						«Современный коммерческий оптово-продовольственный рынок (ОПР) по адресу: Донецкая область, г. Макеевка, Горняцкий район»		
						Док-павильон Рыба-мясо №23		
Изм.	Кол.уч	Лист	N док.	Подпись	Дата	Автоматическая установка пожарной сигнализации. Система оповещения и управления эвакуацией.	Стадия	Лист
ГИП							Р	14
Разработал						План расположения оборудования и кабельных трасс системы речевого оповещения в подвале		17
Н.контроль							ООО "Технология"	

План расположения оборудования и кабельных трасс системы речевого оповещения на 1-м этажа


Номер по инвентарю	Наименование	Группы, м2	Кап- пом- щ. Рязань
01	Тамбур	11,41	-
02	Тамбур	11,41	-
03	Тамбур	11,41	-
04	Тамбур	11,41	-
05	Коридор уборочного инвентаря	21,08	8-8
06	ИТП	12,23	8-3
07	Электрощитовая	12,23	8-3
08	Разруженный тамбур	107,83	-
09	Разруженный тамбур	70,33	-
10	Разруженный тамбур	70,33	-
11	Разруженный тамбур	70,33	-
12	Разруженный тамбур	70,33	-
13	Разруженный тамбур	70,33	-
14	Разруженный тамбур	70,33	-
15	Разруженный тамбур	70,33	-
16	Разруженный тамбур	70,33	-
17	Разруженный тамбур	70,33	-
18	Разруженный тамбур	70,33	-
19	Разруженный тамбур	70,33	-
20	Разруженный тамбур	70,33	-
21	Разруженный тамбур	107,83	-
22	Разруженный тамбур	107,83	-
23	Разруженный тамбур	70,21	-
24	Разруженный тамбур	70,19	-
25	Разруженный тамбур	70,21	-
26	Разруженный тамбур	70,19	-
27	Разруженный тамбур	70,21	-
28	Разруженный тамбур	72,28	-
29	Разруженный тамбур	72,28	-
30	Разруженный тамбур	70,21	-
31	Разруженный тамбур	70,19	-
32	Разруженный тамбур	70,21	-
33	Разруженный тамбур	70,19	-
34	Разруженный тамбур	70,21	-
35	Разруженный тамбур	107,82	-
36	Зона подпотоки товара	22,04	-
37	Зона подпотоки товара	22,72	-
38	Зона подпотоки товара	22,72	-
39	Зона подпотоки товара	22,72	-
40	Зона подпотоки товара	22,72	-
41	Зона подпотоки товара	22,72	-
42	Зона подпотоки товара	23,39	-
43	Зона подпотоки товара	23,39	-
44	Зона подпотоки товара	22,72	-
45	Зона подпотоки товара	22,72	-
46	Зона подпотоки товара	22,72	-
47	Зона подпотоки товара	22,72	-
48	Зона подпотоки товара	22,72	-
49	Зона подпотоки товара	22,04	-
50	Зона подпотоки товара	22,04	-
51	Зона подпотоки товара	22,72	-
52	Зона подпотоки товара	22,72	-
53	Зона подпотоки товара	22,72	-
54	Зона подпотоки товара	22,72	-
55	Зона подпотоки товара	22,72	-
56	Зона подпотоки товара	23,39	-
57	Зона подпотоки товара	23,39	-
58	Зона подпотоки товара	22,72	-
59	Зона подпотоки товара	22,72	-
60	Зона подпотоки товара	22,72	-
61	Зона подпотоки товара	22,72	-
62	Зона подпотоки товара	22,72	-
63	Зона подпотоки товара	22,04	-
64	Выстывание зона	13,17	-
65	Выстывание зона	13,17	-
66	Выстывание зона	13,17	-
67	Выстывание зона	13,17	-
68	Выстывание зона	13,17	-
69	Выстывание зона	13,17	-
70	Выстывание зона	13,17	-
71	Выстывание зона	13,17	-
72	Выстывание зона	13,17	-
73	Выстывание зона	13,17	-
74	Выстывание зона	13,17	-
75	Выстывание зона	13,17	-
76	Выстывание зона	13,17	-
77	Выстывание зона	13,17	-
78	Выстывание зона	13,17	-
79	Выстывание зона	13,17	-
80	Выстывание зона	13,17	-
81	Выстывание зона	13,17	-
82	Выстывание зона	13,17	-
83	Выстывание зона	13,17	-
84	Выстывание зона	13,17	-
85	Выстывание зона	13,17	-
86	Выстывание зона	13,17	-
87	Выстывание зона	13,17	-
88	Выстывание зона	13,17	-
89	Выстывание зона	13,17	-
90	Выстывание зона	13,17	-
91	Выстывание зона	13,17	-
92	Тамбур	18,06	-
93	Тамбур	18,06	-
94	Тамбур-шлюз	62,36	-
95	Тамбур-шлюз	62,36	-
96	Горючий зал	80,19	-
97	Горючий зал	197,13	-
98	Горючий зал	24,77	-
99	СУ Ч	24,75	-
100	СУ Ч	24,75	-
		3 848,29 м²	

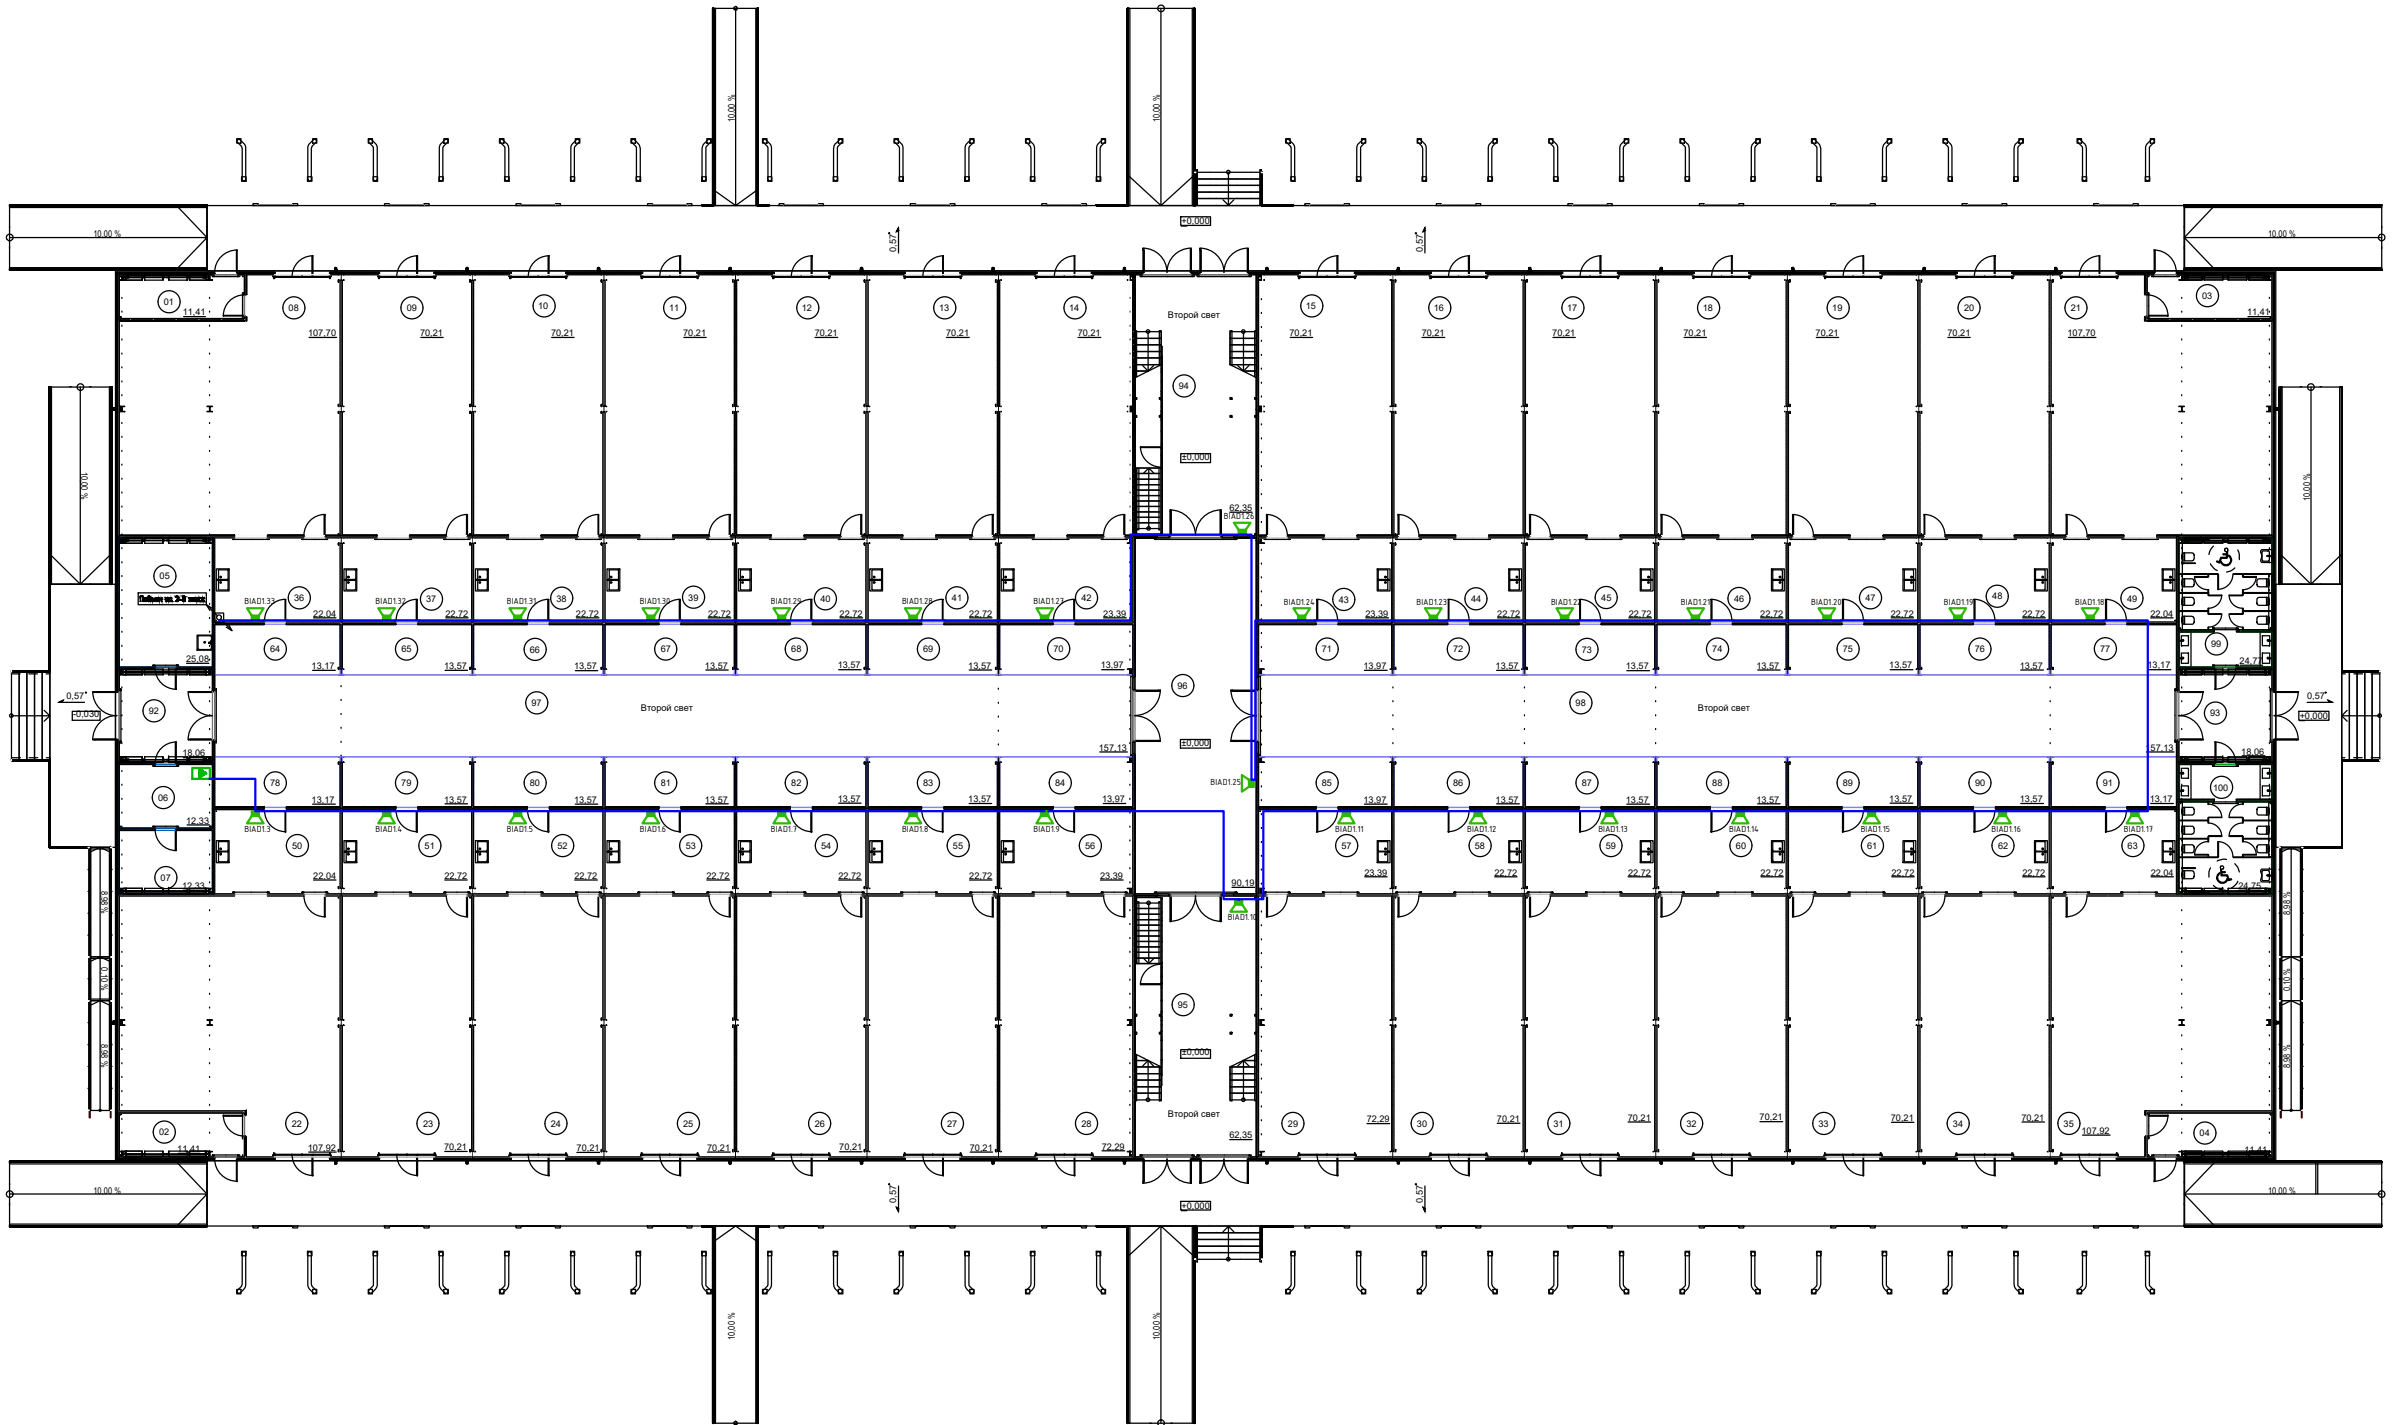

						ОПР-01/24/2024–КДЗ–АПСиСОУЗ			
						«Современный коммерческий оптово-продовольственный рынок (ОПР) по адресу: Донецкая область, г. Макеевка, Горняцкий район» Док-павильон Рыба-мясо №23			
Изм.	Код уч.	Лист	№ док.	Подпись	Дата	Автоматическая установка пожарной сигнализации. Система оповещения и управления эвакуацией.	Страница	Лист	Листов
ГИП							Р	15	17
Разработал									
Н.контроль									
						План расположения оборудования и кабельных трасс системы речевого оповещения на 1-м этаже	000 "Технология"		



План расположения оборудования и кабельных трасс системы речевого оповещения на 2-м этажа

Номер помеще-ния	Наименование	Площадь, м2	Кат. пом е-ще -ния
01	Кладовая	119,89	В-3
02	Кладовая	70,21	В-3
03	Кладовая	70,21	В-3
04	Кладовая	70,2	В-3
05	Кладовая	70,22	В-3
06	Кладовая	70,21	В-3
07	Кладовая	72,3	В-3
08	Кладовая	70,21	В-3
09	Кладовая	70,22	В-3
10	Кладовая	70,2	В-3
11	Кладовая	70,22	В-3
12	Кладовая	70,2	В-3
13	Кладовая	119,89	В-3
14	Кладовая	119,89	В-3
15	Кладовая	70,21	В-3
16	Кладовая	70,21	В-3
17	Кладовая	70,21	В-3
18	Кладовая	70,21	В-3
19	Кладовая	70,21	В-3
20	Кладовая	72,29	В-3
21	Кладовая	72,29	В-3
22	Кладовая	70,21	В-3
23	Кладовая	70,21	В-3
24	Кладовая	70,21	В-3
25	Кладовая	70,21	В-3
26	Кладовая	70,21	В-3
27	Кладовая	119,89	В-3
28	Рабочий кабинет	37,97	-
29	Кладовая уборочного инвентаря	12,19	В-3
30	Техническое помещение	12,19	В-3
31	Техническое помещение	34,32	В-3
32	Техническое помещение	34,32	В-3
33	Техническое помещение	34,32	В-3
34	Техническое помещение	34,32	В-3
35	Вент-камера	67,99	В-3
36	Холл	569,31	-
37	Холл	569,31	-
38	Лестничная площадка	26,2	-
39	Лестничная площадка	17,87	-
		3 550,95 м²	

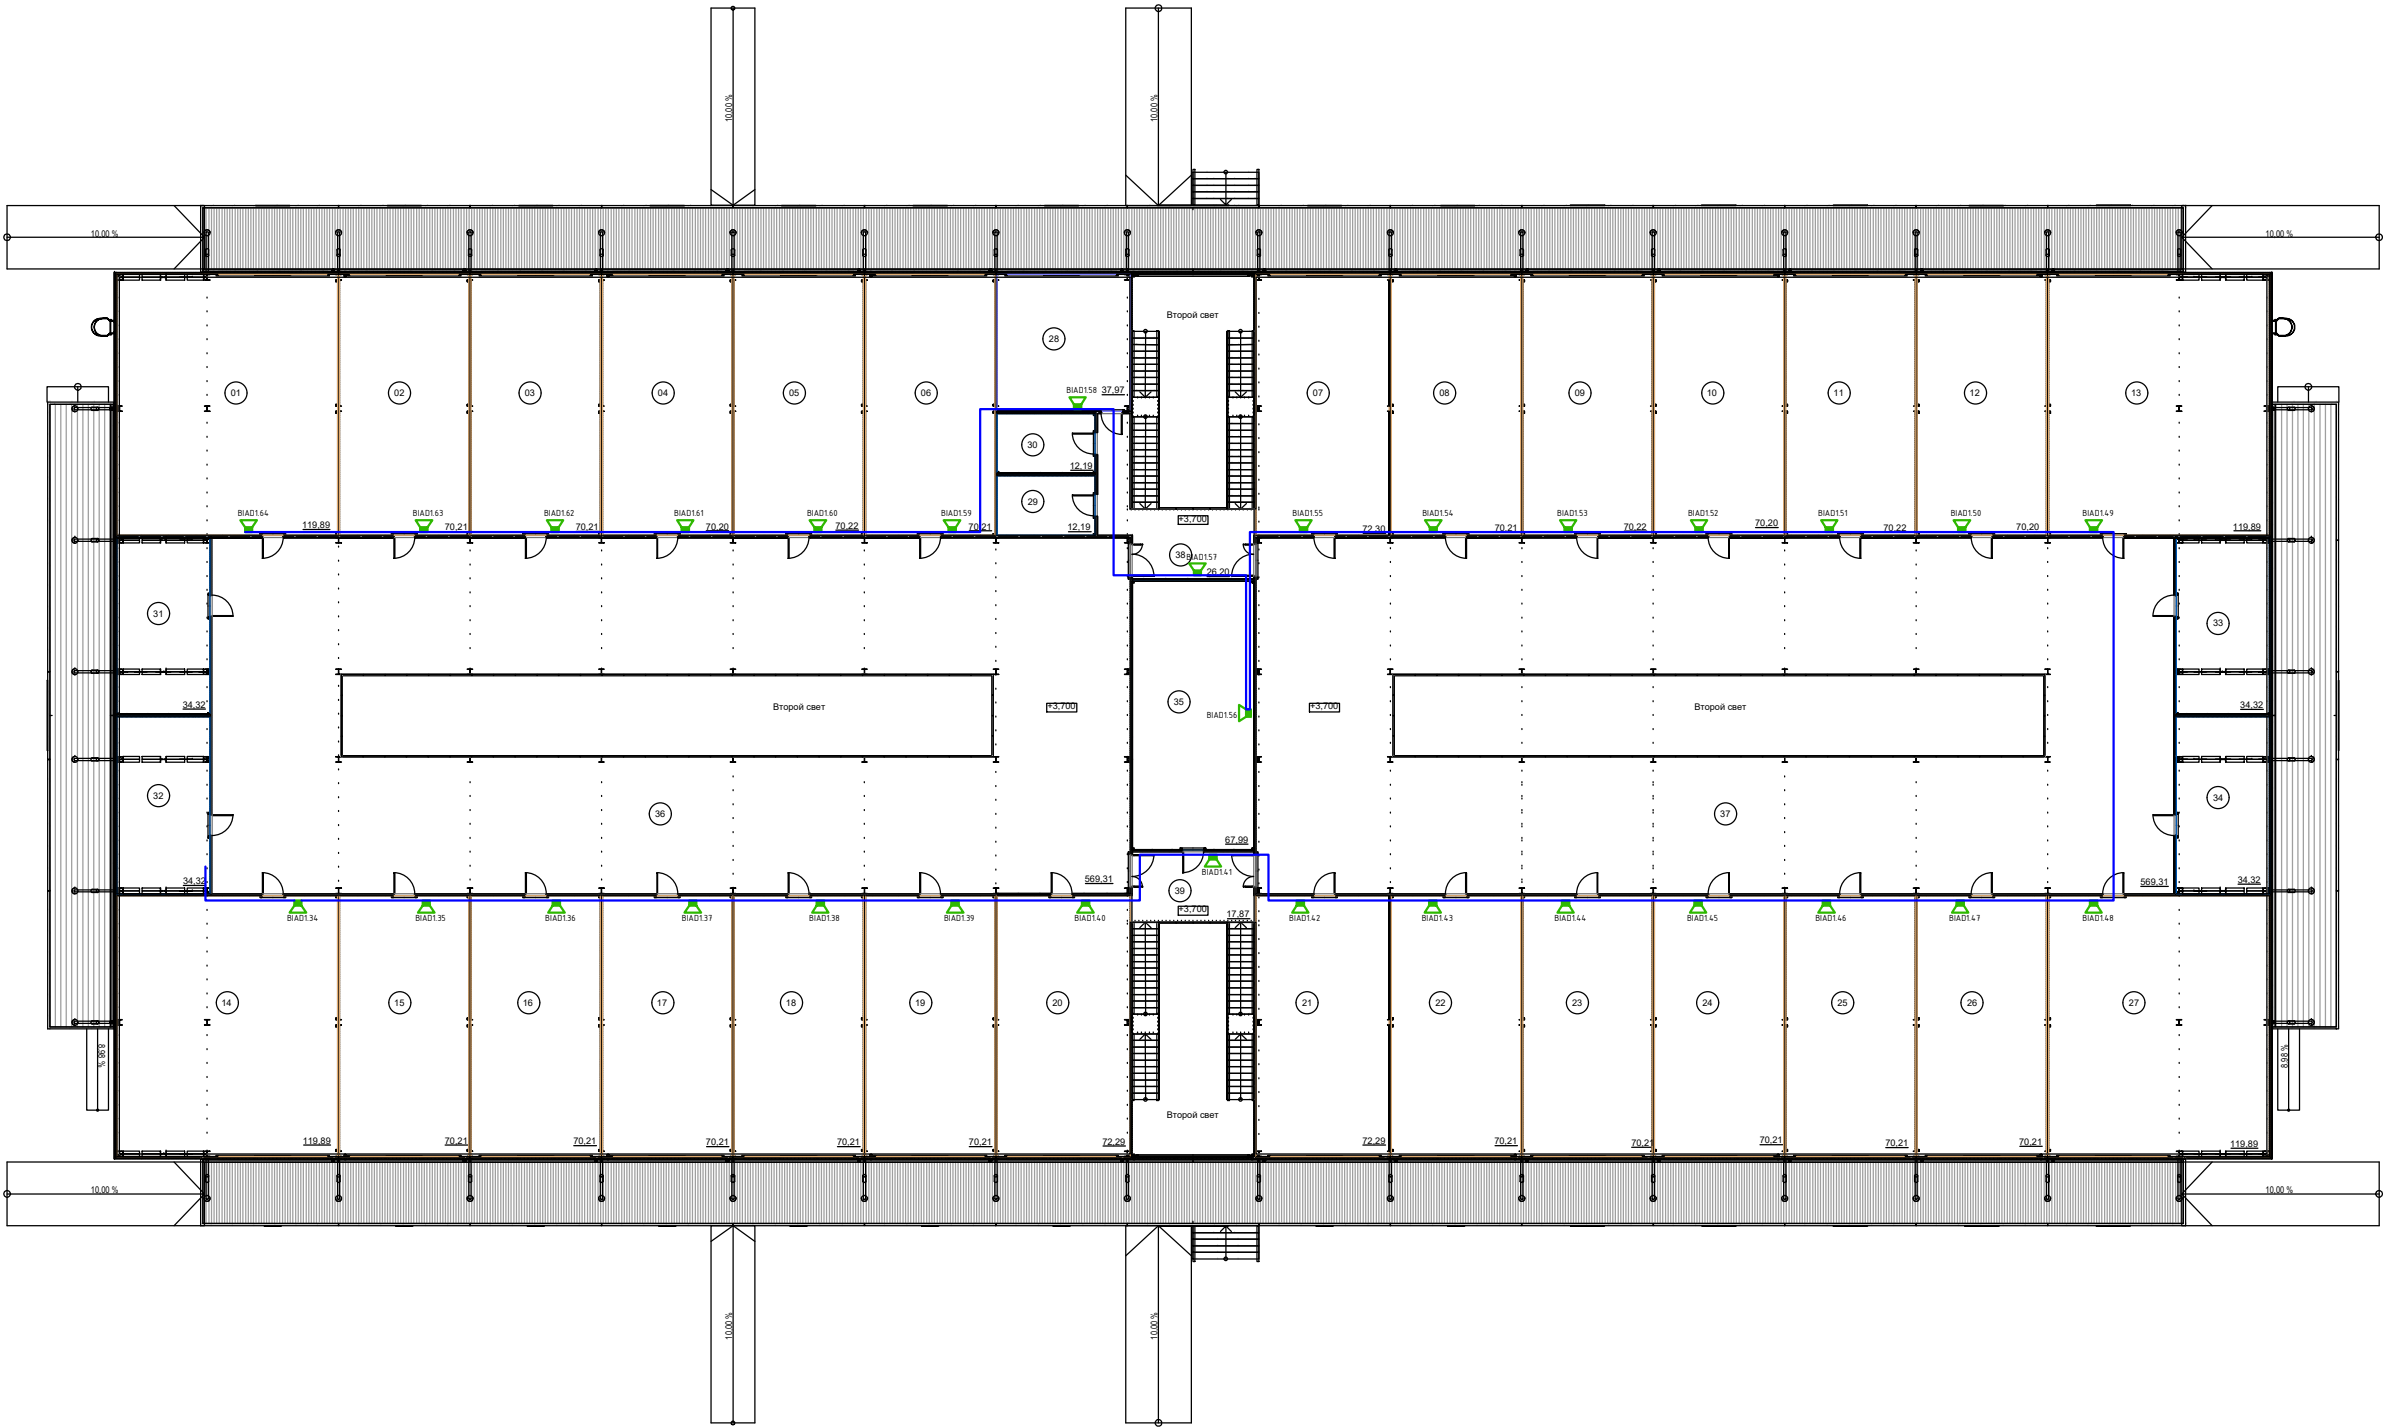

						ОПР-01/24/2024-КДЗ-АПСиСОУЭ			
						«Современный коммерческий оптово-продовольственный рынок (ОПР) по адресу: Донецкая область, г. Макеевка, Горняцкий район» Док-павильон Рыба-мясо №23			
Изм.	Кол.уч	Лист	N док	Погнись	Дата	Автоматическая установка пожарной сигнализации. Система оповещения и управления эвакуацией.	Стадия	Лист	Листов
ГИП							Р	16	17
Разработал						План расположения оборудования и кабельных трасс системы речевого оповещения на 2-м этажа	ООО "Технология"		
Н.контроль									

Инв. №	Подп.	Взам. инв. №	Согласовано	
			Гл. спец.	

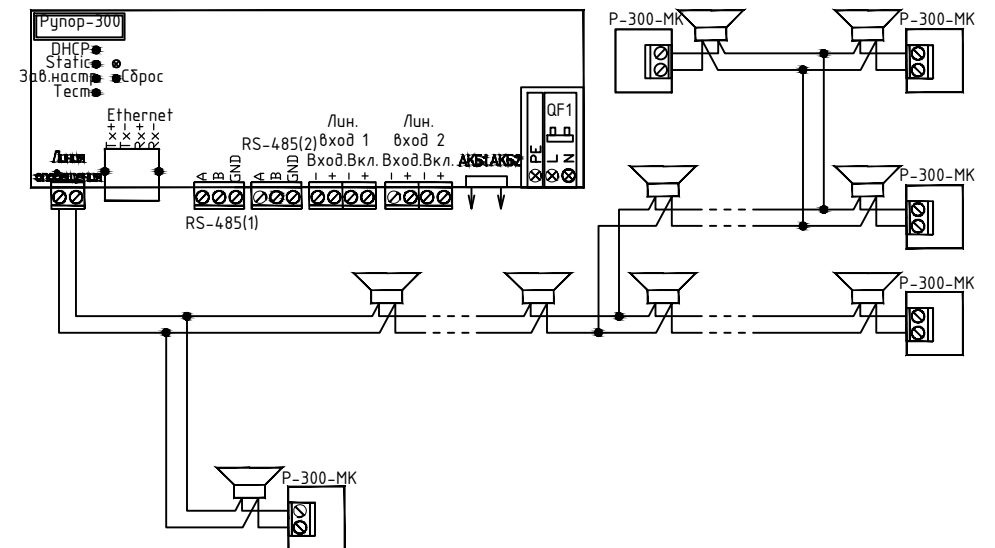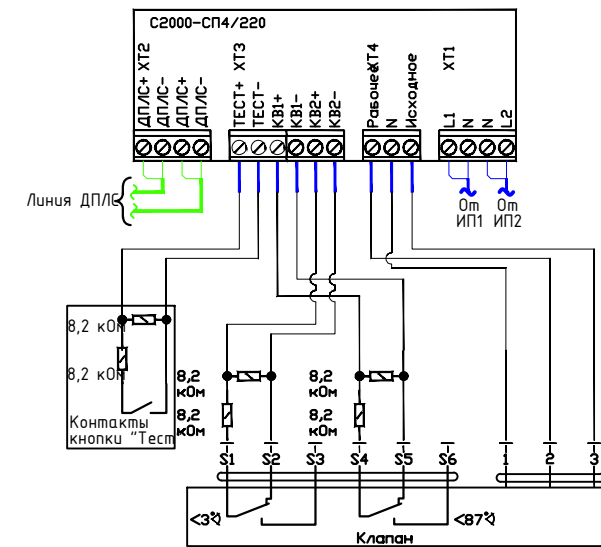

						ОПР-01/24/2024-КДЗ-АПСиСОУЭ			
						«Современный коммерческий оптово-продовольственный рынок (ОПР) по адресу: Донецкая область, г. Макеевка, Горняцкий район» Док-павильон Рыба-мясо №23			
Изм.	Количество	Лист	№ док.	Подпись	Дата	Автоматическая установка пожарной сигнализации. Система оповещения и управления эвакуацией.	Стадия	Лист	Листов
ГИП							Р	17	17
Разработал									
Н.контроль						Схема электрическая	000 "Технология"		

Пози- ция	Наименование и техническая характеристика	Тип, марка, обозначение документа, опросного листа	Код оборудо- вания, изде- лия, матери- ала	Завод-изготовитель	Единица изме- рения	Количество	Масса еди- ницы, кг	Примечание
1	2	3	4	5	6	7	8	9
2	ОКЛ СегментЛАЙН-ГФ (ТУ 27.90.33-014-37572599-2020) в составе:							
2.1	Кабель огнестойкий для систем пожарной сигнализации ТУ 3581-002-17648068-2014	КПСЭнг(A)-FRHF 1x2x0,5		ООО «СегментЭНЕРГО»	м.	1370		
2.2	Кабель огнестойкий симметричный, для интерфейса RS-485 ТУ 3563-010-82564577-2011 (ТУ 27.32.13-010-82564577-2018)	КОПСЭнг(A)-FRHF 4x2x0,5		ООО «СегментЭНЕРГО»	м.	5		
2.3	Короб монтажный 27x18 ТУ 27.33.14-001-00555459-2020	СЭ 27x18	км2718	ООО «СегментЭНЕРГО»	м.	60		
2.4	Труба гофрированная лёгкая 370 Н HF FR НГ белая с протяжкой DN5/8. Наружный диаметр — 16 мм. ТУ 27.90.12-001-00555459-2020		gт158100	ООО «СегментЭНЕРГО»	м.	250		
2.5	Комплект крепежный (дюбель, саморез, скоба СМО 16-17) уп. 100шт.		Т0999	ООО «СегментЭНЕРГО»	шт	35		
2.6	Комплект крепежный (дюбель 5x30, саморез 4,2x32, Хомут FR ПР 25) уп. 100шт.		Т0997	ООО «СегментЭНЕРГО»	шт	1		
2.7	Герметик огнезащитный терморасширяющийся	ОГНЕЗА-ГТ		ООО ПКО «ХимСтройИн- жиниринг»	шт	2		
2.8	Кабель силовой не распространяющий горение при групповой прокладке ка- тегории А, огнестойкий 180 минут, безгалогенный ТУ 16.К71-339-2004	ПВПГнг(A)-FRHF 3*1,5		ООО «СегментЭНЕРГО»	м.	200		

Задание на электроснабжение

1 Предусмотреть электроснабжение следующих электроприемников:

Электроприемник	Un, В	Обозначение	Кол-во	Категория электроснабжения	Pномреб. (ед.), кВт	Примеч.
Прибор приемно-контрольный и управления пожарный «Сириус»	1 ~ 50 Гц, 220В	РУ	1	I	0,05	См. планы
Блок речевого оповещения «Рупор-300»	1 ~ 50 Гц, 220В	АУ	1	I	0,54	См. планы

2 Предусмотреть заземление всех металлических нетоковедущих частей электрооборудования.

3 Качество электроэнергии должно соответствовать ГОСТ 32144-2013.

4 Питание электроприемников СПЗ, относящихся к первой категории по надежности электроснабжения, должно осуществляться от панели ПЭСПЗ, в соответствии с требованиями СПэлектроснабжения, должно осуществляться от панели ПЭСПЗ, в соответствии с требованиями СП При отсутствии панели ПЭСПЗ на объекте защиты допускается выполнять питание электрооборудования СПЗ от самостоятельного НКУ с АВР, при этом самостоятельное НКУ с АВР должно подключаться после аппарата управления и до аппарата защиты ВРУ, ГРЩ или НКУ здания

5 Кабельные линии питания должны быть выполнены огнестойким кабелем (в составе огнестойкой кабельной линии) с пределом огнестойкости ПО1 по ГОСТ 31565-2012.

6 Размещение оборудования уточнить при монтаже.

						ОПР-01/24/2024-КДЗ-АПСuCOYЭ			
Изм.	Кол. уч	Лист	N док.	Подпись	Дата	Задание на электроснабжение.	Стадия	Лист	Листов
ГИП							Р	20	1
Исполнитель							ООО "Технология"		
Н,контр.									