
# План 1 этажа на отм. ±0,000. М 1:100

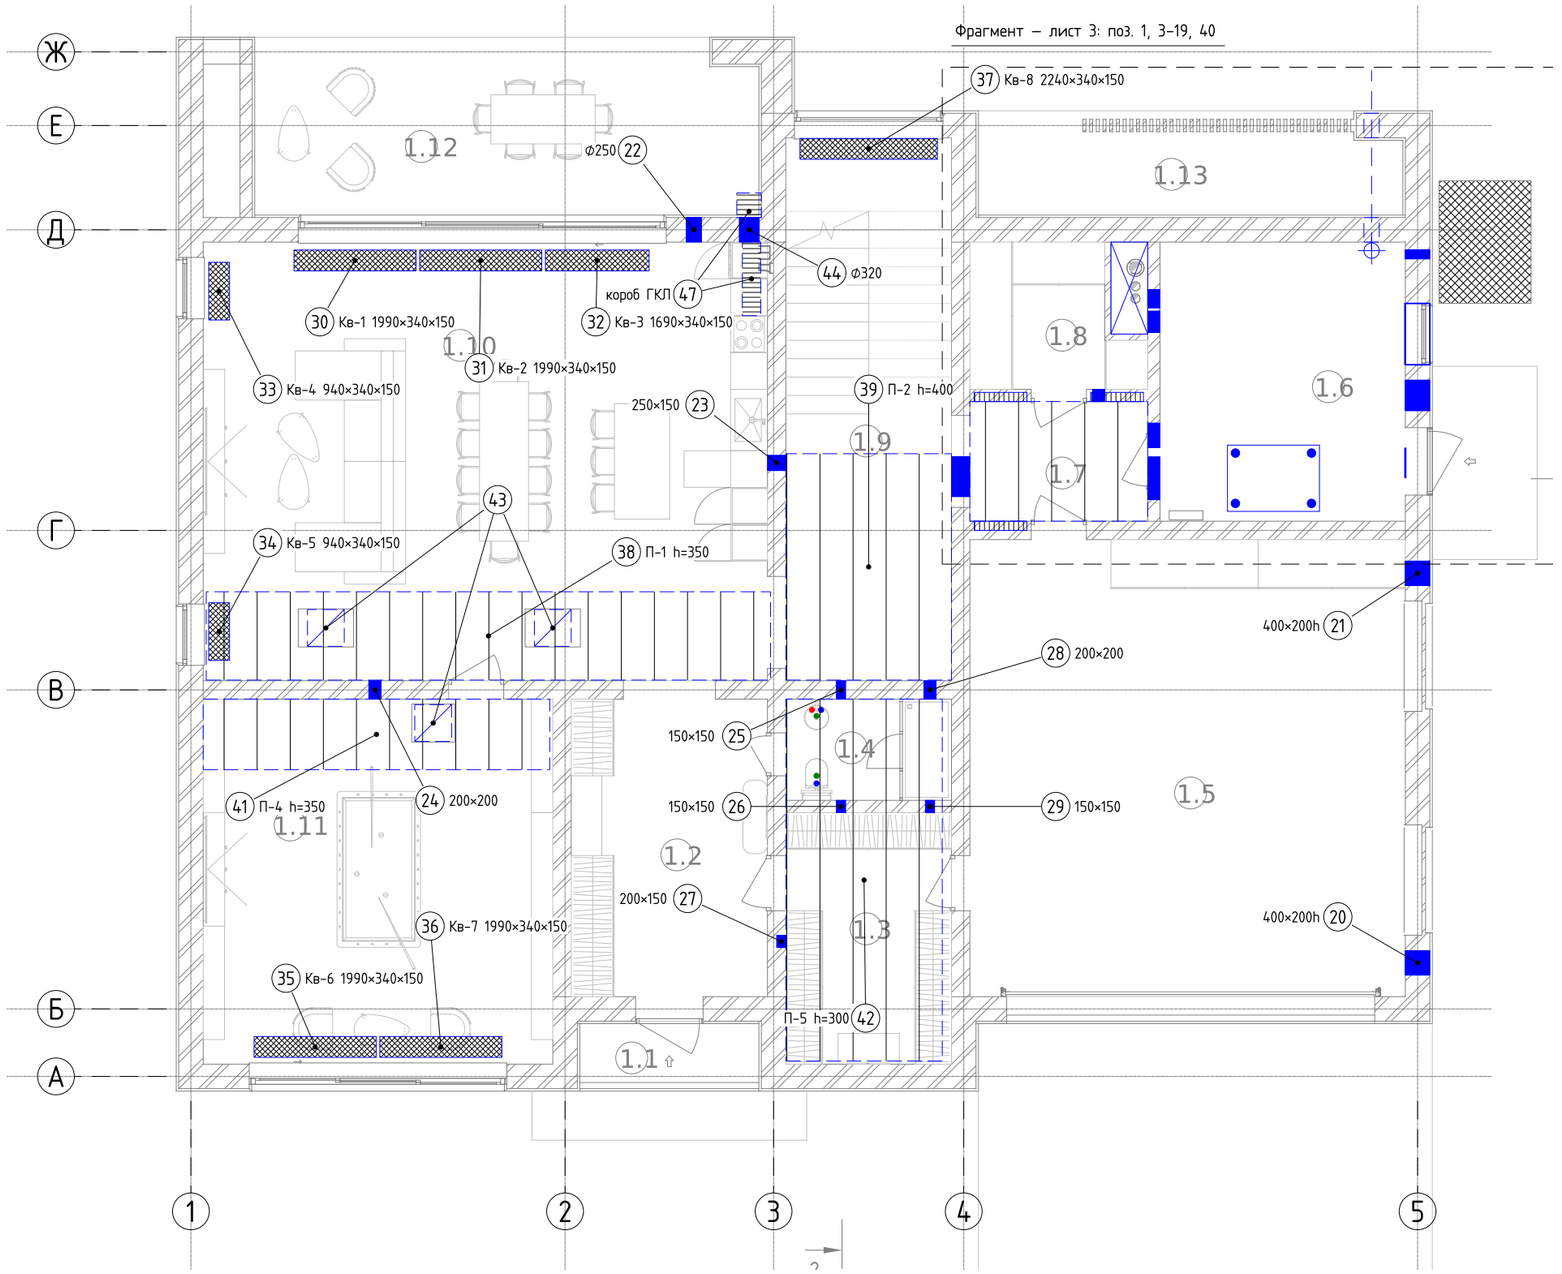


## Условные обозначения

- отверстие в стене, перегородке, стенке шахты
- круглый проход в стене (гильза)
- отверстие в перекрытии
- проход через покрытие (оголовок шахты)
- гильза в плите пола
- проход через фундамент (ниже пола)
- ниша под коллекторный шкаф
- приямок внутрипольного конвектора
- шахта (по АР)
- зона подшивки потолка
- люк 600×600 в подшивке
- зазор под дверью, решетка в двери
- площадка под наружный блок
- подвес оборудования к плите перекрытия: контур, точки подвеса
- (N) позиция ведомости; рядом – размер, мм («h» – высота)

## Примечания

1. Номер у отметки – позиция ведомости (листы 5–7): размеры, привязки, отметки, назначение.
2. Топочная 1.6, тамбур 1.7, ввод Ecoflex и площадка НБ-1 – фрагмент в М 1:50 на листе 3.
3. Отверстия в перекрытии над 1 этажом (Ш-1, стояки Т1, Т2) – на листе 2.

Согласовано

Взам.инв.№

Подпись и дата


Инв.№ подл.

| Изм. | Кол.уч | Лист | № док | Подп. | Дата | И05.09.26-ОВ.ТЗ-1 | | | |
|---|---|---|---|---|---|---|---|---|---|
| | | | | | | Двухэтажный индивидуальный жилой дом с баней. Московская область, кадастровый номер участка 50:08:0050209:1600 | | | |
| Разраб. | | | | | | Отопление, вентиляция и кондиционирование | Стадия | Лист | Листов |
| Пров. | | | | | | | Р | 1 | 7 |
| Н.контр. | | | | | | Задание на устройство отверстий, шахт, ниш и приямков. План 1 этажа | | | |
| ГИП | | | | | | | | | |

Копировал

Формат А3

# План 2 этажа на отм. +4,050. М 1:100

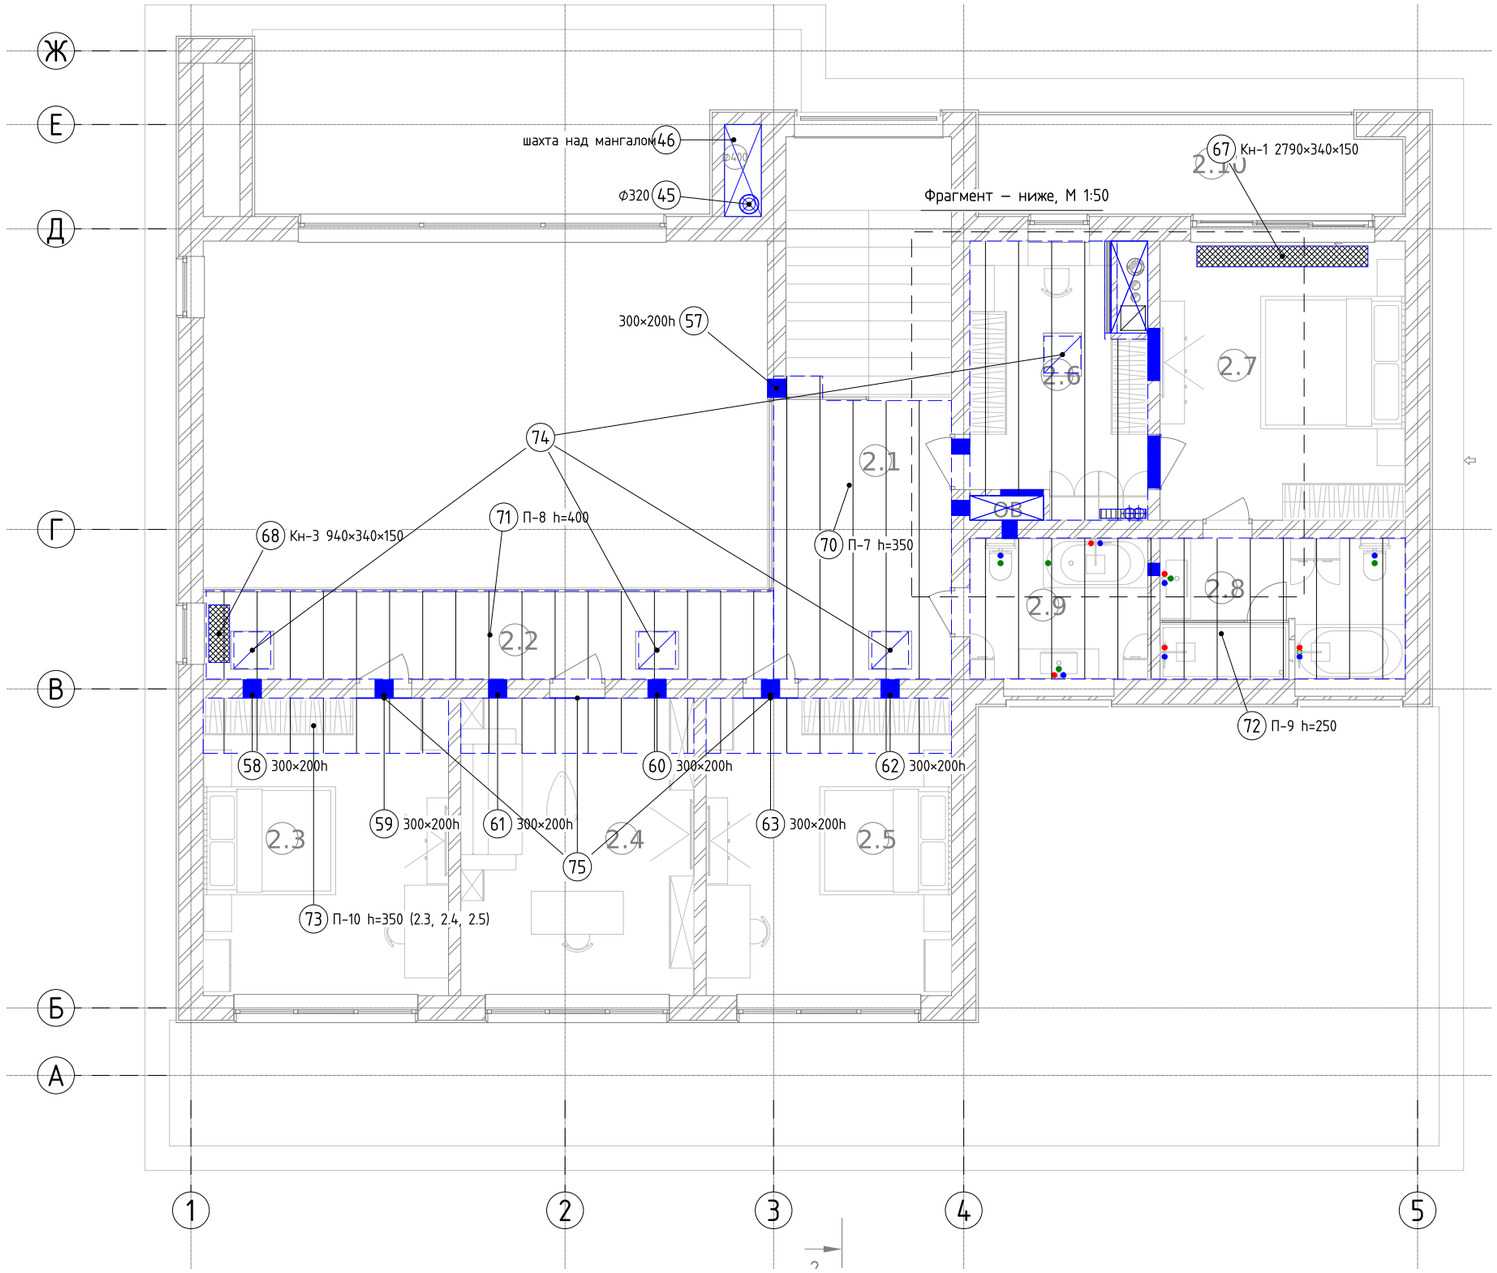


## Условные обозначения

- гильза в перекрытии
- перенос стенки шахты: новое положение (штрих – по АР)
- отверстие в стене, перегородке, стенке шахты
- отверстие в перекрытии
- ниша под коллекторный шкаф
- приямок внутрипольного конвектора
- шахта (по АР)
- зона подшивки потолка
- люк 600×600 в подшивке
- зазор под дверью, решетка в двери
- (N) позиция ведомости; рядом – размер, мм («h» – высота)

## Примечания

1. Номер у отметки – позиция ведомости (листы 5–7).
2. Отверстия в перекрытии над 1 этажом (Ш-1, стояки Т1, Т2, контур Ш-2) показаны на этом листе.
3. Спальни 2.3–2.5: подшивка над шкафами П-10, отверстия ЩП/ЩВ – под воздуховоды 250×150 (узел 6, лист 15).
4. Ш-2 на 2 этаже – 600×1500 в свету, как на 1 этаже: западную стенку перенести (поз. 51).

## Фрагмент у шахты Ш-1. М 1:50




| Изм. | Кол.уч | Лист | № док | Подп. | Дата | И05.09.26-ОВ.ТЗ-1 | | |
|---|---|---|---|---|---|---|---|---|
| | | | | | | Двухэтажный индивидуальный жилой дом с баней. Московская область, кадастровый номер участка 50:08:0050209:1600 | | |
| Разраб. | | | | | | Отопление, вентиляция и кондиционирование | Стадия | Лист | Листов |
| Пров. | | | | | | | Р | 2 | 7 |
| Н.контр. | | | | | | Задание на устройство отверстий, шахт, ниш и приямков. План 2 этажа | | | |
| ГИП | | | | | | | | | |

Согласовано

Взам.инв.№


Подпись и дата

Инв.№ подл.


Копировал

Формат А3

## Фрагмент плана 1 этажа: топочная 1.6, тамбур 1.7. М 1:50

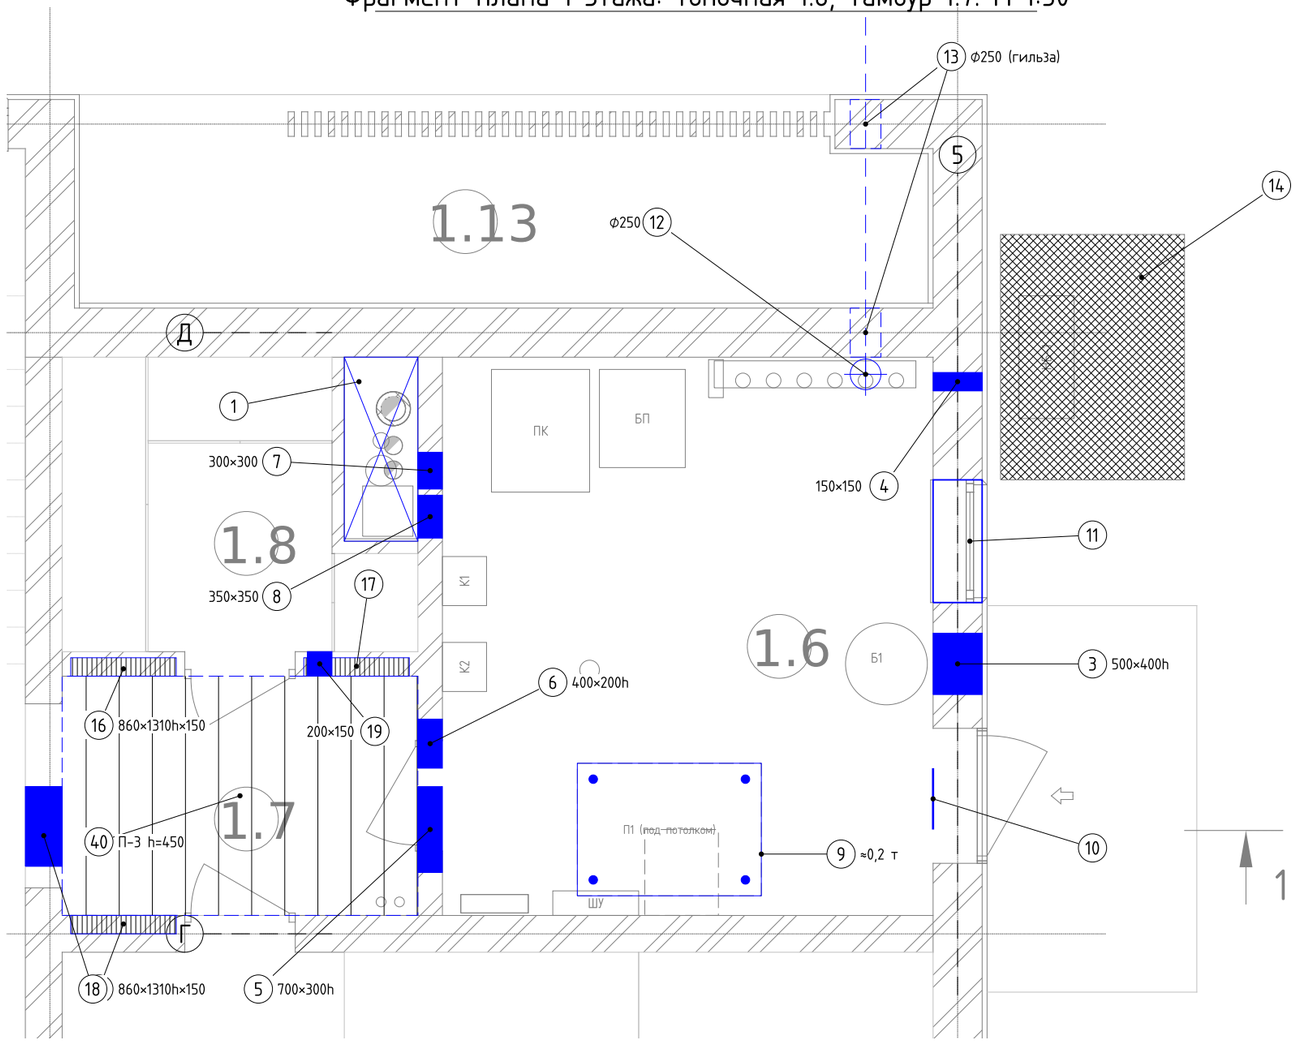


## План кровли. М 1:200

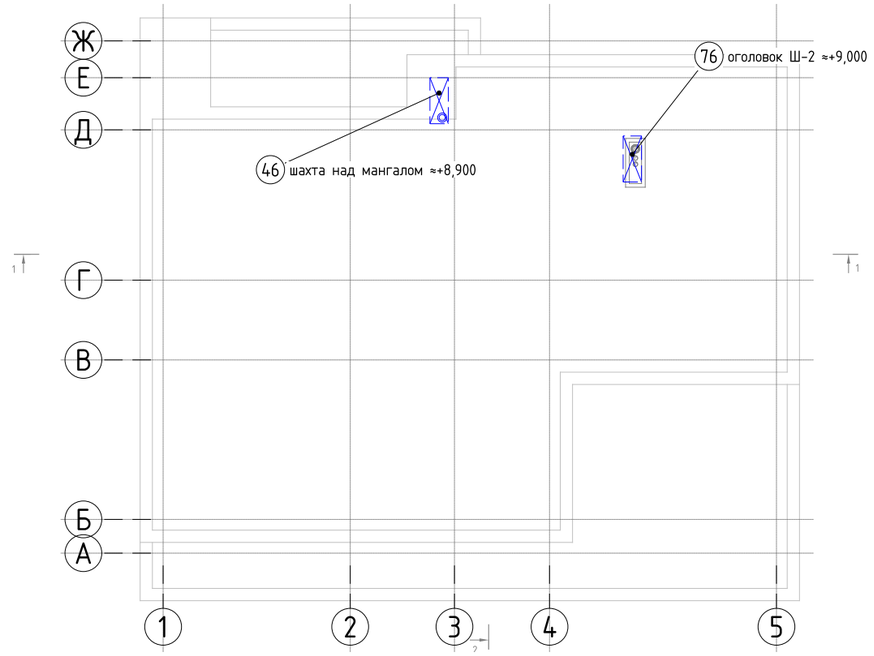


### Примечания

1. Ш-2 – в свету 600×1500 по АР; каналы (с юга на север): выброс П1 Ф250 в канале 400×400, В2 Ф250, дымоход котлов Viessmann (каскад, лист 7) Ф125, пеллетный Ф200/280 – лист 7, узел 5 л. 15.
2. Стены 1.6/1.7 и 1.6/Ш-2: над дверью и под потолком – две группы отверстий на разных отметках (трубы +3,200, воздуховоды +3,400); перемычки – по КР.
3. Трасса Ecoflex – штрихпунктиром (лист 14); подъем в 1.6 – узел 2 л. 13.
4. Условные обозначения – на листе 1.

Согласовано

Взам.инв.№

Подпись и дата


Инв.№ подл.

| Изм. | Кол.уч | Лист | № док | Подп. | Дата | И05.09.26-ОВ.ТЗ-1 | | | |
|---|---|---|---|---|---|---|---|---|---|
| | | | | | | Двухэтажный индивидуальный жилой дом с баней. Московская область, кадастровый номер участка 50:08:0050209:1600 | | | |
| Разраб. | | | | | | Отопление, вентиляция и кондиционирование | Стадия | Лист | Листов |
| Пров. | | | | | | | Р | 3 | 7 |
| Н.контр. | | | | | | Задание на устройство отверстий, шахт, ниш и приямков. Топочная 1.6. Кровля | | | |
| ГИП | | | | | | | | | |

Копировал

Формат А3

# Баня. План на отм. ±0,000. М 1:50

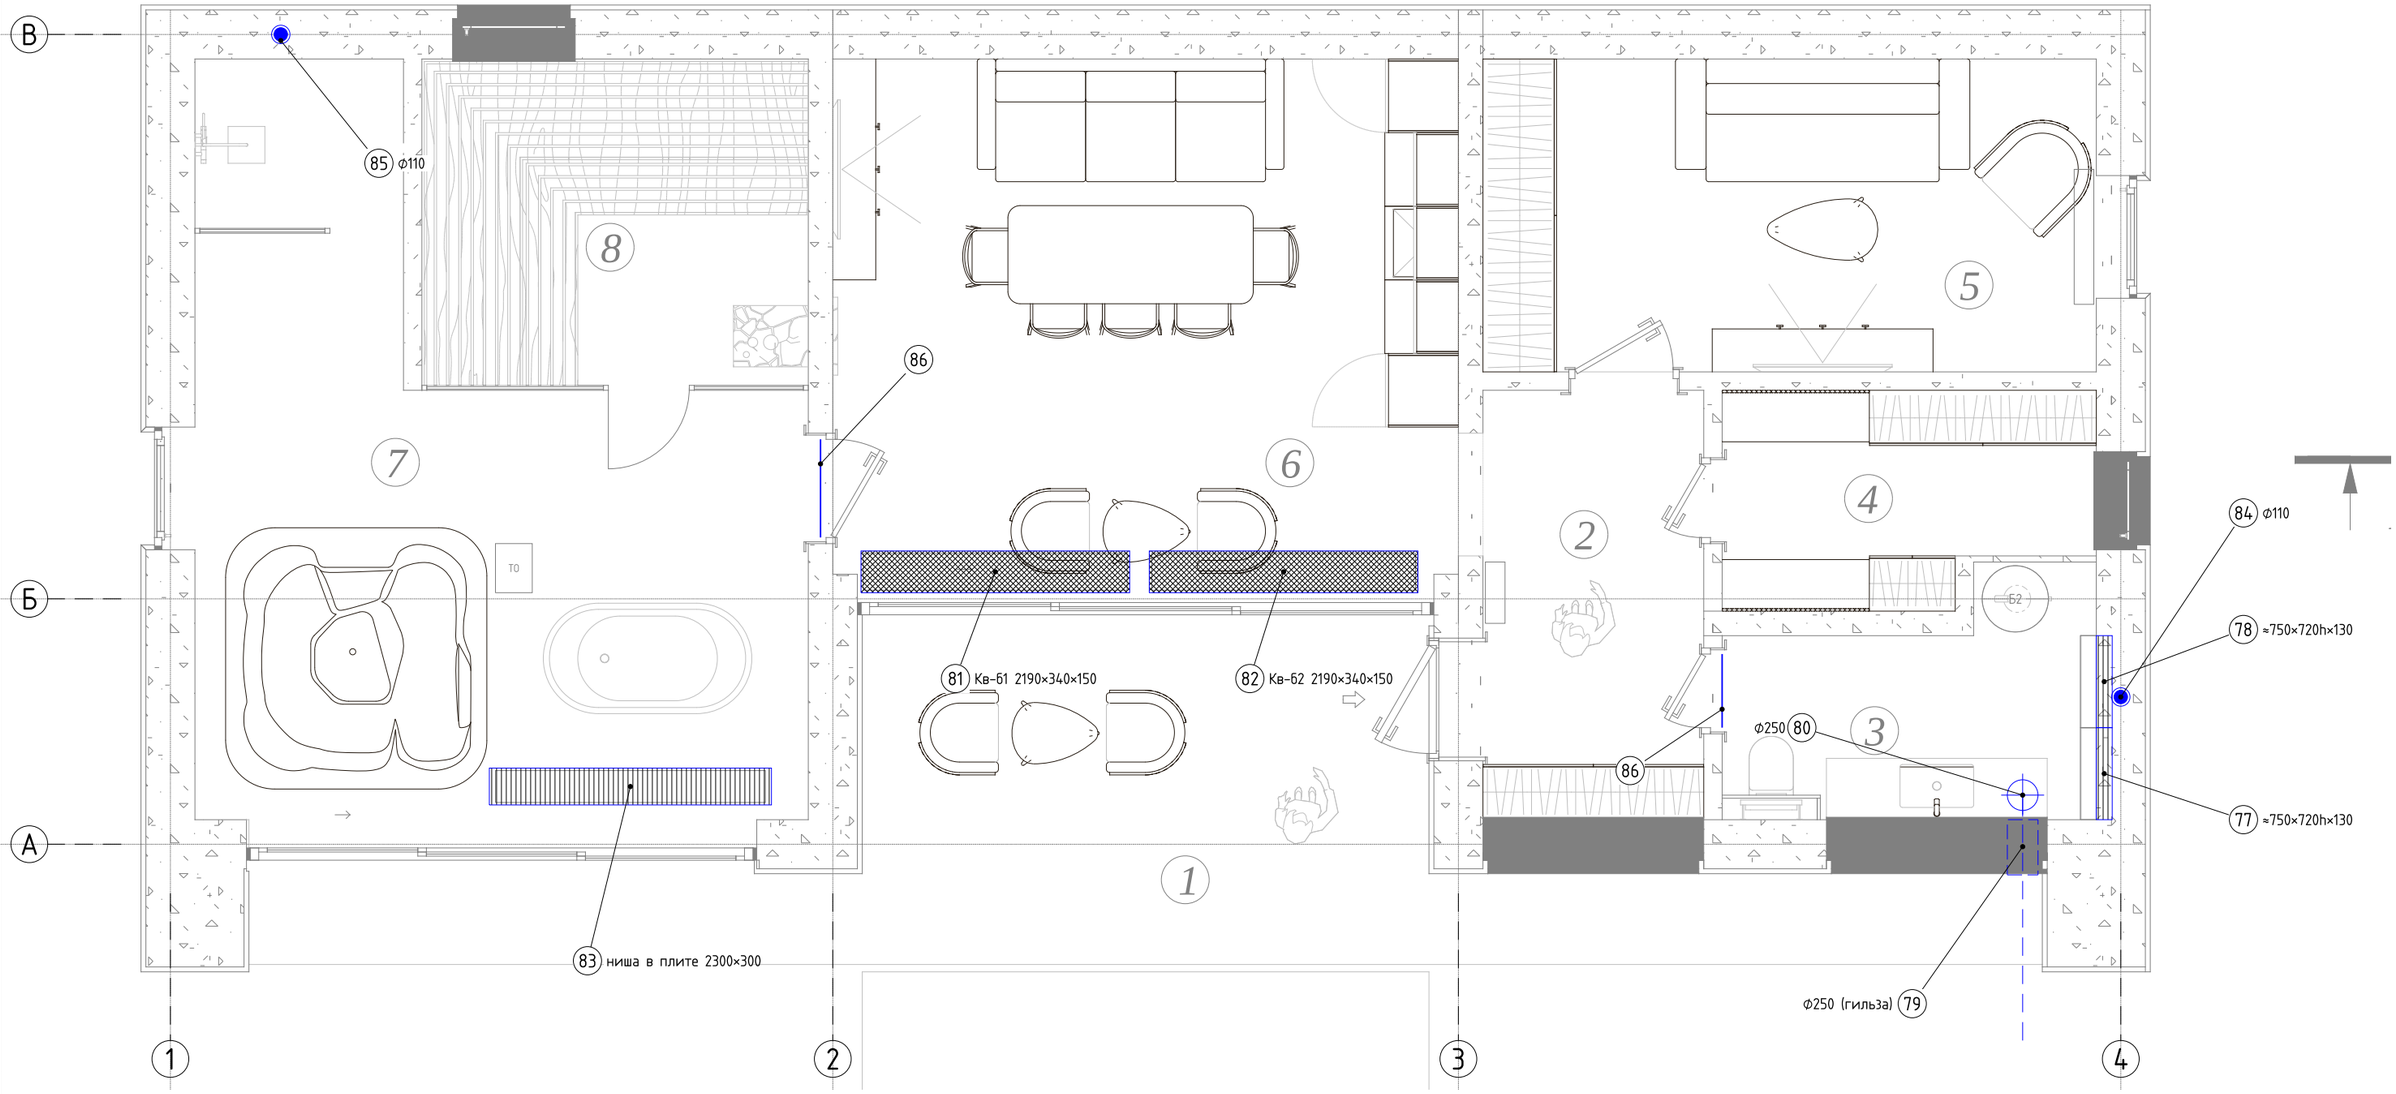


## Примечания

1. Ниши КШ-Б1, КШ-Б2 – в восточной (наружной) стене с/у Б3 под шкафы ШРВ-3, без прорезки утеплителя; подводки – снизу, из стяжки. Проход ВВ-Б1 – выше ниш (ось +2,200).
2. Кв-Б3 у джакузи – в нише плиты пола, низ на 155 ниже чистого пола; глубина в плите – по экспликации полов.
3. Ввод Ecoflex – при x≈15,10, западнее пилона АР (x 15,30–16,10): гильзы в фундаменте и в плите пола, узел 1 л. 13; место подъема уточнить по листу 12.
4. Условные обозначения – на листе 1.

| Изм. | Кол.уч | Лист | № док | Подп. | Дата | И05.09.26-ОВ.ТЗ-1 | | | |
|---|---|---|---|---|---|---|---|---|---|
| | | | | | | Двухэтажный индивидуальный жилой дом с баней. Московская область, кадастровый номер участка 50:08:0050209:1600 | | | |
| Разраб. | | | | | | Отопление, вентиляция и кондиционирование | Стадия | Лист | Листов |
| Пров. | | | | | | | Р | 4 | 7 |
| Н.контр. | | | | | | Задание на устройство отверстий, шахт, ниш и приямков. Баня | | | |
| ГИП | | | | | | | | | |

Согласовано

Взам.инв.№

Подпись и дата

Инв.№ подл.

Копировал

Формат А3

# Ведомость отверстий, шахт, ниш и приямков

| Поз. | Вид | Размер, мм | Привязка | Отметка, м | Назначение |
|---|---|---|---|---|---|
| **Шахты** | | | | | |
| 1 | шахта | 600×1500 (в свету) | За западной стеной 1.6: x 15,00–15,60 (2400 от оси 4), у 12,10–13,60 (200 от оси Д) | от ±0,000 до оголовка ≈+9,000 | Ш-2 (по АР), каналы с юга на север: выброс П1 Ф250 в канале 400×400 (АР); В2 – вытяжка топочной Ф250; дымоход котлов Viessmann (каскад, лист 7) Ф125; дымоход пеллетного котла Ф200/280. Каналы раздельные, стенки негорючие, зазоры до дымоходов – по паспортам; оголовок – поз. «Кровля» |
| 2 | шахта | 1200×400 (в свету) | гардеробная 2.6: x 12,70–13,90 (100 от оси 4), у 9,05–9,45 (150 от оси Г) | +3,850…+7,550 (2 этаж) | Ш-1 (по АР09): стояки П Ф200, В Ф200, П Ф100 (2.7) и фреонопроводы К-4…К-7 из подшивки П-3 1 этажа в подшивки 2 этажа; проходы – поз. перекрытия и стенок Ш-1 |
| **Топочная 1.6, тамбур 1.7, ввод Ecoflex, НБ-1 (фрагмент – лист 3)** | | | | | |
| 3 | стена | 500×400(h) | наружная стена по оси 5; край у=10,85 (1950 от оси Г) | низ +2,600 | Н1 – воздухозабор П1: решетка с сеткой, воздуховод Ф250 в теплоизоляции |
| 4 | стена | 150×150 | наружная стена по оси 5; ось отв. у=13,40 (400 от оси Д) | центр +3,100 | фреонопроводы НБ-1 (жидкость + газ) в изоляции и межблочный кабель; гильза с уклоном наружу |
| 5 | стена | 700×300(h) | стена 1.6/1.7 над дверью; у 9,40–10,10 (край у=9,40 (500 от оси Г)) | центр +3,400 (верх +3,550) | П Ф250 от П1 в 1.7 и В Ф250 из 1.7 к П1 (подшивка П-3) |
| 6 | стена | 400×200(h) | стена 1.6/1.7 над дверью; у 10,25–10,65 (край у=10,25 (1350 от оси Г)) | центр +3,200 | три пары труб в изоляции от РК: к КШ-1 25×3,5, к КШ-2 32×4,4, к стоякам КШ-4 25×3,5 – одним пучком; в 1.7 – под потолком к шкафам и к стоякам (листы 3, 7) |
| 7 | стена | 300×300 | стена 1.6/Ш-2 (запад); ось отв. у=12,68 (1125 от оси Д) | центр +3,350 | В2 – вытяжная решетка топочной 188 м³/ч в канал Ф250 Ш-2 (под потолком) |
| 8 | стена | 350×350 | стена 1.6/Ш-2 (запад); ось отв. у=12,30 (1500 от оси Д) | центр +3,400 | выброс П1 Ф250 в теплоизоляции – в канал 400×400 Ш-2 |
| 9 | подвес к плите перекрытия | 1500×1080×610(h), ≈0,2 т | топочная 1.6, под плитой перекрытия: x 16,90–18,40 (3100 от оси 5), у 9,21–10,29 (310 от оси Г) | низ +2,450, верх +3,060 | подвес П1 Turkov Zenit 750 Heco W (корпус 1500×1080×610, ≈145 кг) с воздуховодами, шумоглушителями и смесительным узлом – расчетно ≈0,2 т: 4 точки подвеса (шпильки/анкеры в плиту) или рама к плите – по паспорту Turkov. КР: проверить плиту на нагрузку и тип анкеров (или закладные) |
| 10 | дверь | решетка ≈500×250, ж. с. не менее 0,08 м² | наружная дверь 1.6 (ось 5) | низ решетки не выше +0,300 | ПН – приток в топочную 282 м³/ч (вытяжка и воздух на горение); решетка нерегулируемая |
| 11 | окно (проверка) | остекление не менее 1,9 м² | окно 1.6 по оси 5: у 11,60–12,60 | – | легкосбрасываемая конструкция топочной: не менее 0,03 м² остекления на 1 м³ (V≈63 м³) – проверить по АР и проекту ГСВ; при недостатке – увеличить окно |
| 12 | плита пола | Ф250 | топочная: x 19,25 (750 от оси 5); у 13,46 (340 от оси Д) | – | подъем Ecoflex Quattro (Т1, Т2 бани и две трубы ВК) – гильза, узел 2 л. 13 |
| 13 | фундамент | Ф250 (гильза) | x 19,25: под стеной 1.6/1.13 (ось Д) и через фундамент наружной стены 1.13 (у 15,30–15,70) | верх трубы – не менее 0,8 м от планировочной отметки (КР) | Ecoflex Quattro к бане (лист 14); гильза с уплотнением – комплект ввода производителя |
| 14 | площадка | ≈1500×2000 | снаружи у оси 5: x 20,35–21,85, у 12,60–14,60 | верх – по генплану | площадка НБ-1 (Daikin мини-VRV 22,4 кВт) под опорную раму 0,3–0,5 м; гравийная подушка для талой воды (КР) |
| 15 | ниша | 860×1310(h)×150 | стена 1.7/гараж (300), простенок западнее двери в гараж: x 12,77–13,63 (170 от оси 4) | низ ±0,000, верх +1,310 | КШ-1 ≈850×1300×150 – ТП 6 петель (48,5 °С). Стена 300: ниша на глубину шкафа со стороны 1.7, остается 150 мм; перемычка над нишей – КР |
| 16 | ниша | 860×1310(h)×150 | стена 1.7/1.8 (200), простенок у оси 4 западнее двери в 1.8: x 12,77–13,63 (170 от оси 4) | низ ±0,000, верх +1,310 | КШ-2 ≈850×1300×150, двухъярусный (Кв-1–Кв-8; ТП 5 петель и смесительный узел 36 °С – на КШ-2 и КШ-5). Стена 200: ниша на всю глубину шкафа, со стороны 1.8 остается 50 мм – утолщение ГКЛ или усиление – решение АР |
| 17 | ниша | 860×1310(h)×150 | стена 1.7/1.8 (200), простенок восточнее двери в 1.8: x 14,67–15,53 (2070 от оси 4) | низ ±0,000, верх +1,310 | КШ-5 ≈850×1300×150 – ТП 5 петель (1.10-1, 1.11, 1.8) от смесительного узла КШ-2, транзит в полу 1.7. Стена 200 – как КШ2 (со стороны 1.8 перед нишей – шкаф по АР) |
| 18 | стена | 650×300(h) | стена по оси 4 над проходом 1.7/1.9; у 9,45–10,10 (край у=9,45 (550 от оси Г)) | центр +3,400 | П Ф250 в 1.9, 1.10 и В Ф160 от кухни, 1.3, 1.4 (подшивки П-2, П-3); не требуется, если проход открыт до перекрытия |
| 19 | стена | 200×150 | стена 1.7/1.8; ось отв. x=14,80 (2200 от оси 4) | центр +3,400 | вытяжная решетка 1.8 (В Ф100, 30 м³/ч) |
| **План 1 этажа (лист 1)** | | | | | |
| 20 | стена | 400×200(h) | наружная стена по оси 5; ось отв. у=1,85 (750 от оси Б) | низ +0,200 | гараж 1.5 – естественный приток у ворот: решетка с сеткой |
| 21 | стена | 400×200(h) | наружная стена по оси 5; ось отв. у=8,20 (700 от оси Г) | верх +3,450 | гараж 1.5 – естественная вытяжка под перекрытием: решетка с сеткой |
| 22 | стена | Ф250 | наружная стена по оси Д; ось отв. x=8,20 (1300 от оси 3) | центр – по интерьеру (≈+2,600) | КК – клапан компенсации Ф200 с электроприводом, сблокирован с зонтом В3 |
| 23 | стена | 250×150 | стена по оси 3 (1.10/1.9); ось отв. у=10,00 (1100 от оси Г) | центр +3,400 | вытяжная решетка кухни 1.10 (В Ф125, 90 м³/ч) |
| 24 | стена | 200×200 | стена по оси В (1.10/1.11); ось отв. x=3,00 (3000 от оси 1) | центр +3,400 | П Ф125 в 1.11 (подшивки П-1, П-4) |
| 25 | стена | 150×150 | стена по оси В; ось отв. x=10,60 (1100 от оси 3) | центр +3,400 | П Ф100 в прихожую 1.2 (подшивка П-5) |
| 26 | стена | 150×150 | стена 1.4/1.3; ось отв. x=10,60 (1100 от оси 3) | центр +3,400 | П Ф100 в 1.2 |
| 27 | стена | 200×150 | стена 1.3/1.2 (у оси 3); ось отв. у=2,20 (1100 от оси Б) | центр +3,400 | приточная решетка 1.2 (П Ф100, 30 м³/ч) |
| 28 | стена | 200×200 | стена по оси В; ось отв. x=12,05 (550 от оси 4) | центр +3,400 | В Ф125 от 1.3, 1.4 к П1 |
| 29 | стена | 150×150 | стена 1.4/1.3; ось отв. x=12,05 (550 от оси 4) | центр +3,400 | В Ф100 от 1.3 |
| 30 | приямок | 1990×340×150 | зап. торец 1680 от оси 1; сев. край 330 от оси Д | верх ±0,000 | Кв-1 – внутрипольный конвектор КЗТО «Бриз В» L=1950, 1.10; в конструкции пола |
| 31 | приямок | 1990×340×150 | зап. торец 3730 от оси 1; сев. край 330 от оси Д | верх ±0,000 | Кв-2 – внутрипольный конвектор КЗТО «Бриз В» L=1950, 1.10; в конструкции пола |

Согласовано

Взам.инв.№

Подпись и дата

Инв.№ подл.

| Изм. | Кол.уч | Лист | № док | Подп. | Дата | И05.09.26-ОВ.ТЗ-1 | | | |
|---|---|---|---|---|---|---|---|---|---|
| | | | | | | Двухэтажный индивидуальный жилой дом с баней. Московская область, кадастровый номер участка 50:08:0050209:1600 | | | |
| Разраб. | | | | | | Отопление, вентиляция и кондиционирование | Стадия | Лист | Листов |
| Пров. | | | | | | | Р | 5 | 7 |
| Н.контр. | | | | | | Задание на устройство отверстий, шахт, ниш и приямков. Ведомость | | | |
| ГИП | | | | | | | | | |

Копировал

Формат А3

# Ведомость отверстий, шахт, ниш и приямков (продолжение)

| Поз. | Вид | Размер, мм | Привязка | Отметка, м | Назначение |
|---|---|---|---|---|---|
| 32 | приямок | 1690×340×150 | зап. торец 5780 от оси 1; сев. край 330 от оси Д | верх ±0,000 | Кв-3 — внутрипольный конвектор КЗТО «Бриз В» L=1650, 1.10; в конструкции пола |
| 33 | приямок | 940×340×150 | юж. торец 3430 от оси Г; зап. край 290 от оси 1 | верх ±0,000 | Кв-4 — внутрипольный конвектор КЗТО «Бриз В» L=900, 1.10; в конструкции пола |
| 34 | приямок | 940×340×150 | юж. торец 480 от оси В; зап. край 290 от оси 1 | верх ±0,000 | Кв-5 — внутрипольный конвектор КЗТО «Бриз В» L=900, 1.10; в конструкции пола |
| 35 | приямок | 1990×340×150 | зап. торец 1030 от оси 1; юж. край 310 от оси А | верх ±0,000 | Кв-6 — внутрипольный конвектор КЗТО «Бриз В» L=1950, 1.11; в конструкции пола |
| 36 | приямок | 1990×340×150 | зап. торец 3080 от оси 1; юж. край 310 от оси А | верх ±0,000 | Кв-7 — внутрипольный конвектор КЗТО «Бриз В» L=1950, 1.11; в конструкции пола |
| 37 | приямок | 2240×340×150 | зап. торец 430 от оси 3; сев. край 210 от оси Е | верх ±0,000 | Кв-8 (вместо Кн-2 по ЭП, решение Заказчика 19.10.2026) — внутрипольный конвектор КЗТО «Бриз В» L=2200, 1.9; в конструкции пола |
| 38 | подшивка | глубина 350 | зона по плану | низ +3,300 | П-1: К-1, К-2, магистраль П ⌀250…⌀125, фреон, дренаж; диффузоры в торце подшивки |
| 39 | подшивка | глубина 400 | зона по плану | низ +3,250 | П-2: П ⌀250, В ⌀160/⌀125; пересечение — В ⌀125 под П плоским 150×100 (лист 11), фреон, дренаж |
| 40 | подшивка | глубина 450 | зона по плану | низ +3,200 | П-3: магистрали П и В ⌀250 от П1 с пересечениями, стояки в Ш-1, фреон |
| 41 | подшивка | глубина 350 | зона по плану | низ +3,300 | П-4: К-3, П ⌀125/⌀100, фреон, дренаж; диффузор К-3 в торце |
| 42 | подшивка | глубина 300 | зона по плану | низ +3,350 | П-5: П ⌀100 в прихожую 1.2, В ⌀125/⌀100 от 1.3, 1.4 |
| 43 | люки | 600×600, 3 шт. | под блоками К-1, К-2 (1.10), К-3 (1.11) | в подшивке | люки обслуживания блоков К (снизу) — решетки-люки рециркуляции, через них блок забирает воздух (лист 9); к регуляторам расхода на ответвлениях — по месту монтажа |
| Выброс кухонного зонта В3 — в шахту над мангалом террасы 1.12 (листы 1, 2, 3) | | | | | |
| 44 | стена | ⌀320 | стена по оси Д (у 13,60–14,00); ось отв. x=9,10 (400 от оси 3) | ось +3,400 (верх +3,560, ниже низа плиты +3,650) | В3 — воздуховод ⌀200 (после перехода ⌀150/200) в теплоизоляции НГ 50 мм, габарит ⌀300, из кухни в подшивку террасы 1.12; гильза, заделка зазора негорючим материалом |
| 45 | перекрытие | ⌀320 | перекрытие террасы 1.12 в пределах шахты над мангалом: центр x=9,10, y=14,20 (400 от оси Д) | перекрытие террасы | проход стояка В3 ⌀200 в изоляции (габарит ⌀300) из подшивки террасы в шахту над мангалом; гидро- и теплоизоляционная заделка |
| 46 | шахта | место под ⌀300 (стояк ⌀200 в изоляции) | шахта над мангалом (АР09): в свету x 8,70–9,30, y 14,00–15,50; стояк В3 — (9,10; 14,20) у южной стены; дымоход мангала ⌀400 — (8,875; 14,97) | низ — перекрытие террасы; верх шахты +8,900 (подтверждено Заказчицей 21.10.2026); низ зонта В3 — не ниже ≈+9,400 | стояк В3 — в свету от дымохода мангала не менее 130 мм; в крышке/оголовке шахты — проход ⌀320 с фартуком; выброс В3 — с зонтом, низ не ниже 0,5 м над верхом шахты; с дымоходом мангала не соединять. Верх шахты и высоту дымохода мангала подтвердить АР |
| 47 | короб, подшивка | под ⌀150; в подшивке — под ⌀300 | кухня 1.10: от зонта (9,14; 12,12) к стене по оси Д; терраса 1.12: у стены по оси Д, x≈9,10 | короб — до +3,400 (низ плиты +3,650) | короб ГКЛ над верхними шкафами кухни и над колонной духового шкафа у стены по оси Д под воздуховод ⌀150 (вверх до +3,400), ревизионный люк у стены; подшивка террасы над мангалом у стены — под ⌀200 в изоляции |
| План 2 этажа, перекрытие на отм. +3,650 (лист 2) | | | | | |
| 48 | перекрытие | 1200×400 | в контуре Ш-1: x 12,70–13,90 (100 от оси 4), y 9,05–9,45 (150 от оси Г) | перекрытие +3,650…+3,850 | стояки П ⌀200, В ⌀200, П ⌀100 и фреонопроводы из подшивки П-3 в Ш-1; после монтажа — заделка негорючим |
| 49 | перекрытие | ⌀60, 2 шт. (гильзы ⌀40) | угол 1.7: x 15,30 и 15,45 (300 и 150 от грани стены 1.6), y 9,16 (110 от грани стены по оси Г) | перекрытие +3,650…+3,850 | стояки Т1, Т2 25×3,5 к КШ-4; гильзы с выступом 30 мм над полом — узел 4 л. 15 |
| 50 | перекрытие | 600×1500 | в контуре Ш-2 (поз. Ш-2) | перекрытие +3,650…+3,850 | каналы Ш-2 без разрывов — если шахта не выделена в плите по АР |
| 51 | шахта | 600×1500 в свету (в АР09 — 500) | Западная стенка Ш-2 на 2 этаже: перенести с x 15,00–15,10 на x 14,90–15,00 (как на 1 этаже), y 12,10–13,60 | +4,050 до оголовка | Ш-2 — 600×1500 в свету на всю высоту: каналы выброса П1, В2 и дымоходы (поз. Ш-2) идут без смещений; стенка — негорючая (по АР09 сейчас стоит на x 15,00–15,10) |
| 52 | стена | 250×250 | стена Ш-1 по оси 4 (300); ось отв. y=9,25 (350 от оси Г) | центр +7,300 | П ⌀160 из Ш-1 в холл 2.1 (подшивка П-7) |
| 53 | стена | 700×300(h) | северная стенка Ш-1; x 13,20–13,90 (600 от оси 4) | центр +7,300 | В ⌀200 от 2.6, 2.1; П ⌀100 в 2.7; фреонопроводы К-4…К-7 (подшивка П-6) |
| 54 | стена | 250×250 | стена по оси Г (300); ось отв. x=13,35 (750 от оси 4) | центр +7,300 | В ⌀160 от 2.8, 2.9 в Ш-1 (подшивка П-9) |
| 55 | стена | 200×200 | стена 2.9/2.8; ось отв. y=8,25 (650 от оси Г) | центр +7,300 | В ⌀125 от 2.8 (подшивка П-9) |
| 56 | стена | 250×250 | стена по оси 4 над проемом 2.1/2.6; ось отв. y=10,25 (1350 от оси Г) | центр +7,300 | В ⌀160 от 2.1 к Ш-1; не требуется, если проем открыт до перекрытия |
| 57 | стена | 300×200(h) | стена по оси 3 (2.1 / второй свет 1.10); ось отв. y=11,20 (2300 от оси Г) | низ +6,400 | вытяжная решетка верха второго света 1.10 (В ⌀160, 120 м³/ч) |
| 58 | стена | 300×200(h) | стена по оси В (спальня 2.3); ось отв. x=1,00 (1000 от оси 1) | низ +7,230 | воздуховод 250×150 подачи К-4 (со свежим воздухом П1) к ЩП в подшивке над шкафами П-10 (спальня 2.3, узел 6 л. 15); заделка — минвата и акустический герметик |
| 59 | стена | 300×200(h) | стена по оси В (спальня 2.3); ось отв. x=3,15 (2950 от оси 2), над дверью | низ +7,230 | воздуховод 250×150 возврата К-4 от ЩВ в подшивке над шкафами П-10 (спальня 2.3, узел 6 л. 15); заделка — минвата и акустический герметик |
| 60 | стена | 300×200(h) | стена по оси В (спальня 2.4); ось отв. x=7,60 (1500 от оси 2) | низ +7,230 | воздуховод 250×150 подачи К-5 (со свежим воздухом П1) к ЩП в подшивке над шкафами П-10 (спальня 2.4, узел 6 л. 15); заделка — минвата и акустический герметик |
| 61 | стена | 300×200(h) | стена по оси В (спальня 2.4); ось отв. x=5,00 (1100 от оси 2) | низ +7,230 | воздуховод 250×150 возврата К-5 от ЩВ в подшивке над шкафами П-10 (спальня 2.4, узел 6 л. 15); заделка — минвата и акустический герметик |
| 62 | стена | 300×200(h) | стена по оси В (спальня 2.5); ось отв. x=11,40 (1200 от оси 4) | низ +7,230 | воздуховод 250×150 подачи К-6 (со свежим воздухом П1) к ЩП в подшивке над шкафами П-10 (спальня 2.5, узел 6 л. 15); заделка — минвата и акустический герметик |
| 63 | стена | 300×200(h) | стена по оси В (спальня 2.5); ось отв. x=9,45 (50 от оси 3), над дверью | низ +7,230 | воздуховод 250×150 возврата К-6 от ЩВ в подшивке над шкафами П-10 (спальня 2.5, узел 6 л. 15); заделка — минвата и акустический герметик |

Согласовано

Взам.инв.№

Подпись и дата

Инв.№ подл.

| Изм. | Кол.уч | Лист | № док | Подп. | Дата | И05.09.26-ОВ.ТЗ-1 | | | |
|---|---|---|---|---|---|---|---|---|---|
| | | | | | | Двухэтажный индивидуальный жилой дом с баней. Московская область, кадастровый номер участка 50:08:0050209:1600 | | | |
| Разраб. | | | | | | Отопление, вентиляция и кондиционирование | Стадия | Лист | Листов |
| Пров. | | | | | | | Р | 6 | 7 |
| Н.контр. | | | | | | Задание на устройство отверстий, шахт, ниш и приямков. Ведомость | | | |
| ГИП | | | | | | | | | |

Копировал

Формат А3

# Ведомость отверстий, шахт, ниш и приямков (продолжение)

| Поз. | Вид | Размер, мм | Привязка | Отметка, м | Назначение |
|---|---|---|---|---|---|
| 64 | стена | 850×200(h) | стена 2.6/2.7; у 11,32–12,18 (2425 от оси Г) | верх +7,500 | ЩП 800×150 – подача К-7 и свежий воздух П1 (спальня 2.7, узел 6 л. 15) |
| 65 | стена | 850×200(h) | стена 2.6/2.7; у 9,57–10,43 (675 от оси Г), над дверью | верх +7,500 | ЩВ 800×150 – возврат К-7 (спальня 2.7, узел 6 л. 15) |
| 66 | ниша | 750×1250(h)×150 | встроенный шкаф у стены по оси Г, 2.6: x 14,82–15,57 (2220 от оси 4) | низ +4,050, верх +5,300 | КШ-4 двухъярусный: Р-1–Р-3, Р-5, Кн-1, Кн-3, резерв В6; ТП 2.8, 2.9; стояки снизу (поз. гильз). Полотенцесушители 2.8, 2.9 – от циркуляции ГВС, подводы Т3/Т4 – раздел ВК |
| 67 | приямок | 2790×340×150 | зап. торец 3800 от оси 4; сев. край 280 от оси Д | верх +4,050 | Кн-1 – внутрипольный конвектор КЗТО «Бриз» L=2750, 2.7; в конструкции пола |
| 68 | приямок | 940×340×150 | юж. торец 430 от оси В; зап. край 290 от оси 1 | верх +4,050 | Кн-3 – внутрипольный конвектор КЗТО «Бриз В» L=900, 2.2; в конструкции пола |
| 69 | подшивка | глубина 400 | зона по плану | низ +7,150 | П-6: К-7, стояки из Ш-1, П Ф160, В Ф200/Ф160, фреон, дренаж |
| 70 | подшивка | глубина 350 | зона по плану | низ +7,200 | П-7: К-6, П Ф160, В Ф160, фреон, дренаж |
| 71 | подшивка | глубина 400 | зона по плану | низ +7,150 | П-8: К-4, К-5, П Ф160…Ф100, возврат К, фреон, дренаж |
| 72 | подшивка | глубина 250 | зона по плану | низ по АР | П-9: В Ф160/Ф125 санузлов (низ подшивки – по АР, не ниже глубины 250) |
| 73 | подшивка | глубина 350 | спальни 2.3–2.5: полоса 0,9 м вдоль стены по оси В, на всю ширину комнаты | низ +7,200 | П-10: над шкафами спален 2.3–2.5, полоса 0,9 м от стены: КСД и решетки ЩП/ЩВ, воздуховоды К 250×150; решетки ЩП, ЩВ – в нижней плоскости подшивки, ось щели 0,75 м от стены; по 2 люка к КСД (или съемные решетки) – по дизайн-проекту |
| 74 | люки | 600×600, 4 шт. | под блоками К-4, К-5, К-6 (2.2), К-7 (2.6) | в подшивке | люки обслуживания блоков К; к регуляторам расхода – по месту монтажа |
| 75 | дверь | зазор 15–20 мм | двери спален 2.3, 2.4, 2.5 (стена по оси В) и 2.7 (из 2.6) | под полотном | перетекание воздуха из спален к вытяжке (в спальнях вытяжки нет, лист 10) |
| Кровля (лист 3) | | | | | |
| 76 | покрытие | 600×1500 + стенки шахты | в контуре Ш-2 (поз. Ш-2) | оголовок ≈+9,000 (кровля ≈+8,40) | оголовок Ш-2: каналы раздельные; высота дымоходов над кровлей – по паспортам и СП 7.13130 (с учетом конька); выброс П1 и В2 – с зонтами |
| Баня (лист 4) | | | | | |
| 77 | ниша | ≈750×720(h)×130 | восточная стена с/у Б3 (ось 4): у 0,20–0,95 (200 от оси А) | низ ±0,000, верх +0,720 | КШ-Б1 – прямой коллектор: ШРВ-3; утеплитель наружной стены не прорезать (иначе – короб ГКЛ с выступом) |
| 78 | ниша | ≈750×720(h)×130 | восточная стена с/у Б3 (ось 4): у 0,95–1,70 (950 от оси А) | низ ±0,000, верх +0,720 | КШ-Б2 – коллектор ТП со смесительным узлом (при нехватке высоты – шкаф увеличенной высоты, лист 12): ШРВ-3; утеплитель наружной стены не прорезать (иначе – короб ГКЛ с выступом) |
| 79 | фундамент | Ф250 (гильза) | южная стена с/у Б3 под окном, x=15,10 (800 от оси 4), западнее пилона АР (x 15,30–16,10) | верх трубы – не менее 0,8 м от планировочной отметки (КР) | ввод Ecoflex Quattro в баню (лист 14); гильза с уплотнением – комплект производителя |
| 80 | плита пола | Ф250 | с/у Б3: x=15,10 (800 от оси 4); y=0,40 (400 от оси А) – уточнить по листу 12 | – | подъем Ecoflex к КШ-Б1 – гильза, узел 1 л. 13 |
| 81 | приямок | 2190×340×150 | зап. торец 230 от оси 2; юж. край 50 от оси Б | верх ±0,000 бани | Кв-Б1 – внутрипольный конвектор КЗТО L=2150, Б6; в конструкции пола |
| 82 | приямок | 2190×340×150 | зап. торец 2580 от оси 2; юж. край 50 от оси Б | верх ±0,000 бани | Кв-Б2 – внутрипольный конвектор КЗТО L=2150, Б6; в конструкции пола |
| 83 | ниша в плите пола | 2300×300 | помывочная Б7, у джакузи: x 2,60–4,90; y 0,32–0,62 (оси бани) | низ на 155 ниже чистого пола (корпус 140 + выверка 15); глубина в плите – по экспликации полов | Кв-Б3 – КЗТО «Бриз В TURBO Нерж» 260×140, L=2200; ниша в плите пола (решение Заказчика); подвод Т1, Т2 16×2,0 к торцу – в конструкции пола |
| 84 | стена | Ф110 (гильза под Ф100) | восточная стена по оси 4; y=1,20 (1200 от оси А) | ось +2,200 (не выше низа потолка минус 100; потолки +2,370…+2,750 – сверить с АР) | ВВ-Б1 – вытяжной вентилятор, с/у Б3 (решение Заказчика), воздуховод Ф100; снаружи – решетка с гравитационными жалюзи |
| 85 | стена | Ф110 (гильза под Ф100) | северная стена по оси В; x=0,90 (900 от оси 1) | ось +2,200 (не выше низа потолка минус 100; потолки +2,370…+2,750 – сверить с АР) | ВВ-Б2 – вытяжной вентилятор, помывочная Б7 (решение Заказчика), воздуховод Ф100; снаружи – решетка с гравитационными жалюзи |
| 86 | дверь | подрезка 20 мм (или решетка в полотне) | двери с/у Б3 (из прихожей Б2) и помывочной Б7 (из комнаты отдыха Б6) | под полотном | перетекание воздуха к вытяжным вентиляторам ВВ-Б1, ВВ-Б2 |

## Примечания

1. Задание разделам АР и КР на отверстия, шахты, ниши, приямки и подшивки для систем отопления, вентиляции и кондиционирования по И05.09.26-ОВ (листы 3–15). Размеры – в мм, «h» – высота отверстия; отметки – в м от чистого пола 1 этажа ±0,000 (баня – от своего ±0,000); привязки – к осям, x и y – в м от пересечения осей 1/А, как на листах ОВ. Подложки – АР03, АР09, АР14, план бани (Revit, 19.10.2026).
2. Отверстия в несущих стенах, перекрытиях и фундаментах – по решению КР (перемычки, обрамления, усиление). Размеры даны с запасом на изоляцию и заделку.
3. Проходы через стены и перекрытия – в гильзах и обрамлениях; зазоры заделываются негорючими материалами с пределом огнестойкости не ниже, чем у пересекаемой конструкции (узел 4 л. 15). Стенки Ш-2 и проходы в них – негорючие.
4. Отверстия до Ф50 (фреонопроводы и дренаж в перегородках, подводки) выполняются по месту при монтаже и в задании не показаны, кроме проходов в стенках Ш-1 и наружных стенах.
5. Подшивки (поз. 38–42, 69–72): глубины и низ – по таблицам листов 9, 10, низ – не ниже верха окон; люки 600×600 – под каждым блоком К и у регуляторов расхода на ответвлениях (по месту монтажа).
6. Приямки конвекторов: длина и ширина – по корпусу выбранной серии КЗТО плюс 20 мм на сторону (принята ширина корпуса 300), глубина – не более 150 мм от чистого пола; плита не затрагивается (узел 2 л. 15). Размеры уточняются после подбора серии.
7. Ниши шкафов (поз. 15, 16, 17, 66, 77, 78) – по ориентировочным размерам шкафов, уточнить по каталогу производителя коллекторов. КШ-1, КШ-2, КШ-5 – одного размера, утоплены в простенки тамбура 1.7 (решение Заказчицы 20.10.2026). КШ-3 (1.6) – накладной, ниши не требует.
8. Ecoflex (поз. 12, 13, 79, 80): гильзы, уплотнения и концевые манжеты – комплект производителя под наружный диаметр кожуха Ecoflex Quattro (175 или 200 мм – по каталогу); глубина до верха трубы не менее 0,8 м; отметки фундаментов – по КР (узлы 1, 2 л. 13).
9. Шахта Ш-2 (поз. 1, 50, 51, 76) – 600×1500 в свету на всю высоту; зазоры от дымоходов до конструкций – по паспортам; ревизии и сбор конденсата – в топочной (лист 7). Ввод газа, сигнализатор загазованности – по проекту ГСВ (Т3-4).
10. Двери спален 2.3, 2.4, 2.5, 2.7 – с зазором 15–20 мм под полотном (поз. 75) или с переточными решетками; наружная дверь топочной – с решеткой ПН (поз. 10).
11. Баня: вытяжные вентиляторы помывочной Б7 и с/у Б3 – решение Заказчика (поз. 84, 85); двери Б3, Б7 – с подрезкой 20 мм (поз. 86); Кв-Б3 – в нише плиты пола (поз. 83).

Согласовано

Взам.инв.№

Подпись и дата

Инв.№ подл.

| Изм. | Кол.уч | Лист | № док | Подп. | Дата | И05.09.26-ОВ.Т3-1 | | | |
|---|---|---|---|---|---|---|---|---|---|
| | | | | | | Двухэтажный индивидуальный жилой дом с баней. Московская область, кадастровый номер участка 50:08:0050209:1600 | | | |
| Разраб. | | | | | | Отопление, вентиляция и кондиционирование | Стадия | Лист | Листов |
| Пров. | | | | | | | Р | 7 | 7 |
| Н.контр. | | | | | | Задание на устройство отверстий, шахт, ниш и приямков. Ведомость (окончание). Примечания | | | |
| ГИП | | | | | | | | | |

Копировал

Формат А3