
План 1 этажа. Задание АР и КР. М 1:100

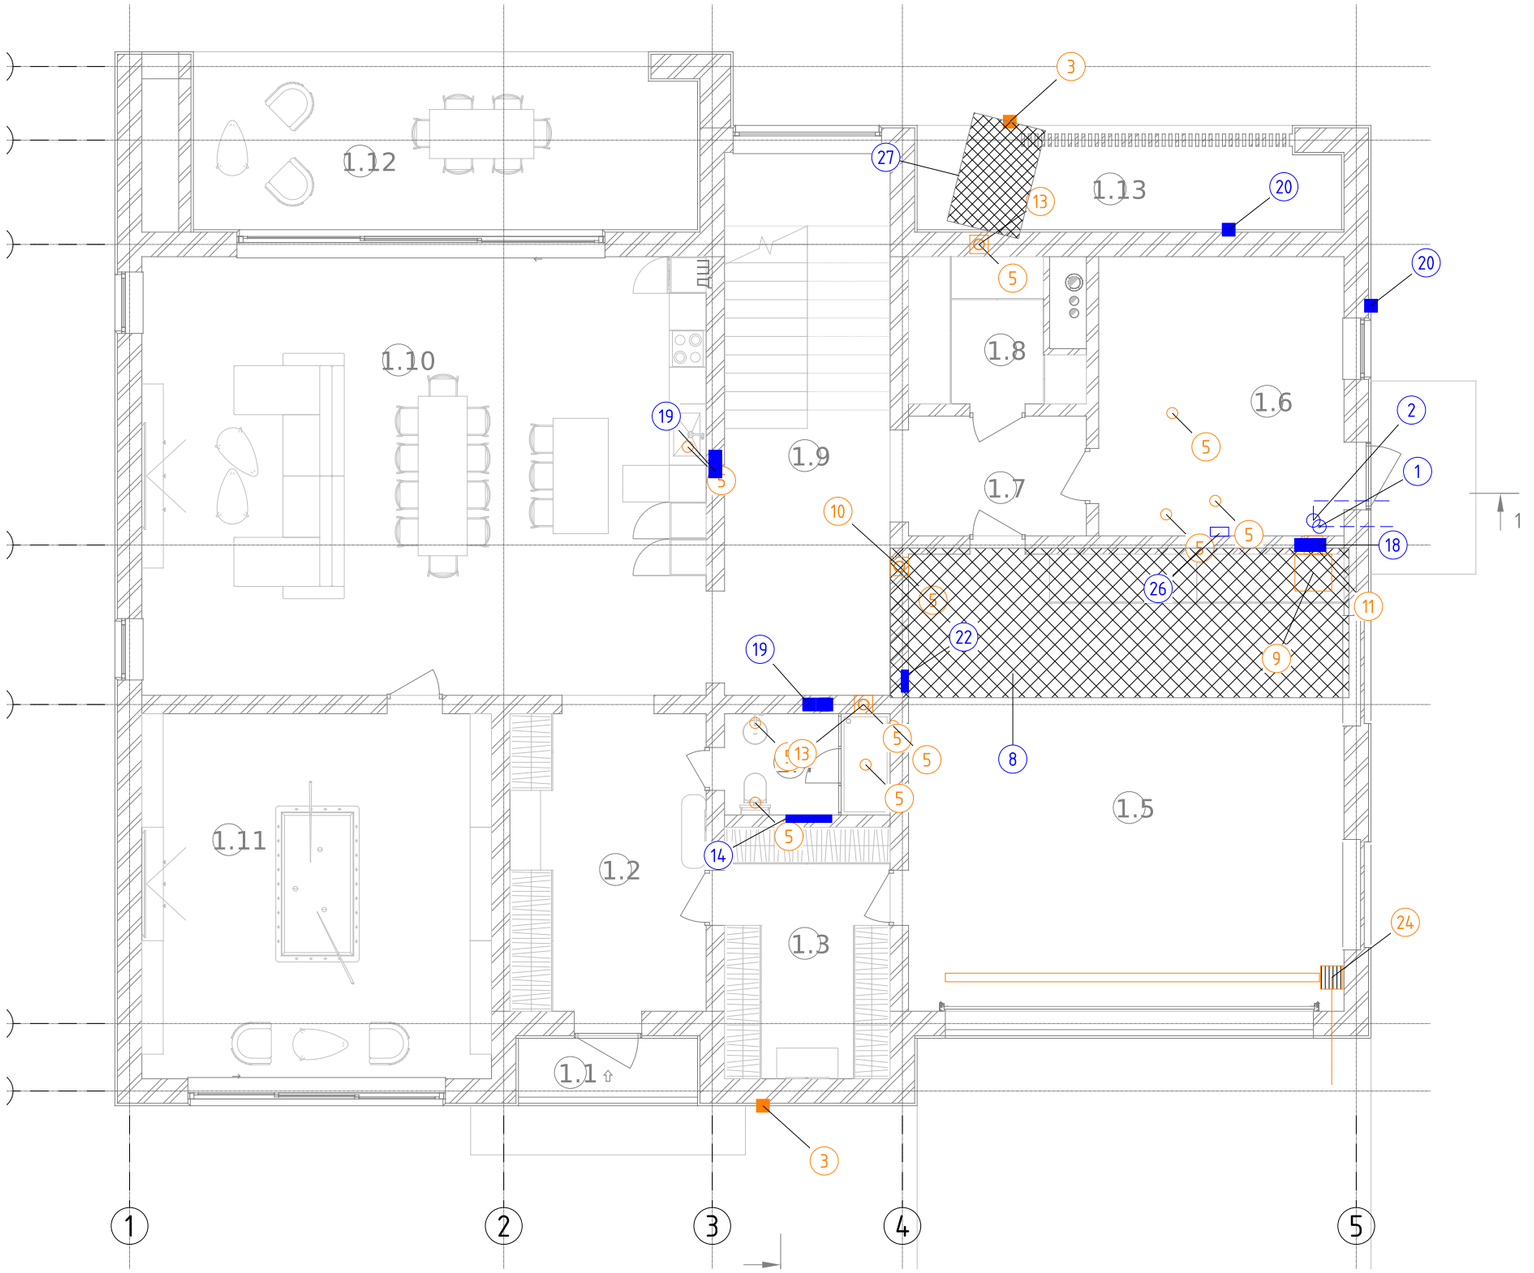

Условные обозначения

- гильза, ниша, проход водопровода
- проход канализации К1 (футляр, люк)
- гильза в плите (координаты — лист 4)
- О-блок газобетонный с отверстием Ф160
- короб гаража, утепление под террасой

Позиции на плане (подробно — листы 3, 4)

1 — футляр Ф75 ввода сквозь плиту (без приямка)
2 — футляр Ф75 подводки автополива КХ-8
3 — футляры Ф160 сборного К1-1 под краем плиты (юг и север)
5 — гильзы в фундаментной плите (кружки)
8 — короб гаража, низ не выше +2,800
9 — люк 600×600 в коробе у ревизии
10 — Ст.К1-1 в О-блоках, люк 300×400 со стороны гаража
11 — Ст.К1-1в в О-блоках в стене по оси Г
13 — прочистки: О-блок в основании стены, люк 300×400
14 — ниша ШВК-1 с нажимным люком
18 — гильзы в стене гараж/1.6
19 — гильзы в основаниях стен (лист 4)
20 — гильзы Ф50 незамерзающих кранов
22 — штроба в стене гаража
24 — гараж: лоток ЛГ-1, понижение плиты под ПУ-1, футляр К2-1
26 — места контроллеров защиты от протечек
27 — утепление над К1-1 под террасой 1.13

Примечания

1. Номер у точки — позиция таблицы (листы 3, 4); координаты — в метрах от осей 1/А (дом, баня — свои оси), отметки — от ±0,000 своего здания.
2. Подложка — АР (Revit 19.10.2026). Точки и размеры — по 3D-модели систем ВК; при изменении АР или КР задание уточняется.
3. Решения Заказчицы 26–27.10.2026: коллекторы — в санузлах и помывочной в нишах за нажимными люками, стояки К1 — в стенах в О-блоках с отверстием Ф160 (в бане перегородки — 250 мм), ревизии и прочистки — за люками в стенах, люков в полу нет; ввод воды — без приямка, в футляре сквозь плиту.

Согласовано

Взам.инв.№

Подпись и дата


Инв.№ подл.

Изм.	Кол.уч	Лист	№ док	Подп.	Дата	И05.09.26-ВК.ТЗ-1			
						Двухэтажный индивидуальный жилой дом с баней. Московская область, кадастровый номер участка 50:08:0050209:1600			
Разраб.						Водопровод и канализация	Стадия	Лист	Листов
Пров.							Р	1	4
Н.контр.						Задание АР и КР. План 1 этажа			
ГИП									


Копировал

Формат А3

Гильзы в перекрытии над гаражом, ниша ШВК-2 (вид на план 2 этажа). М 1:50

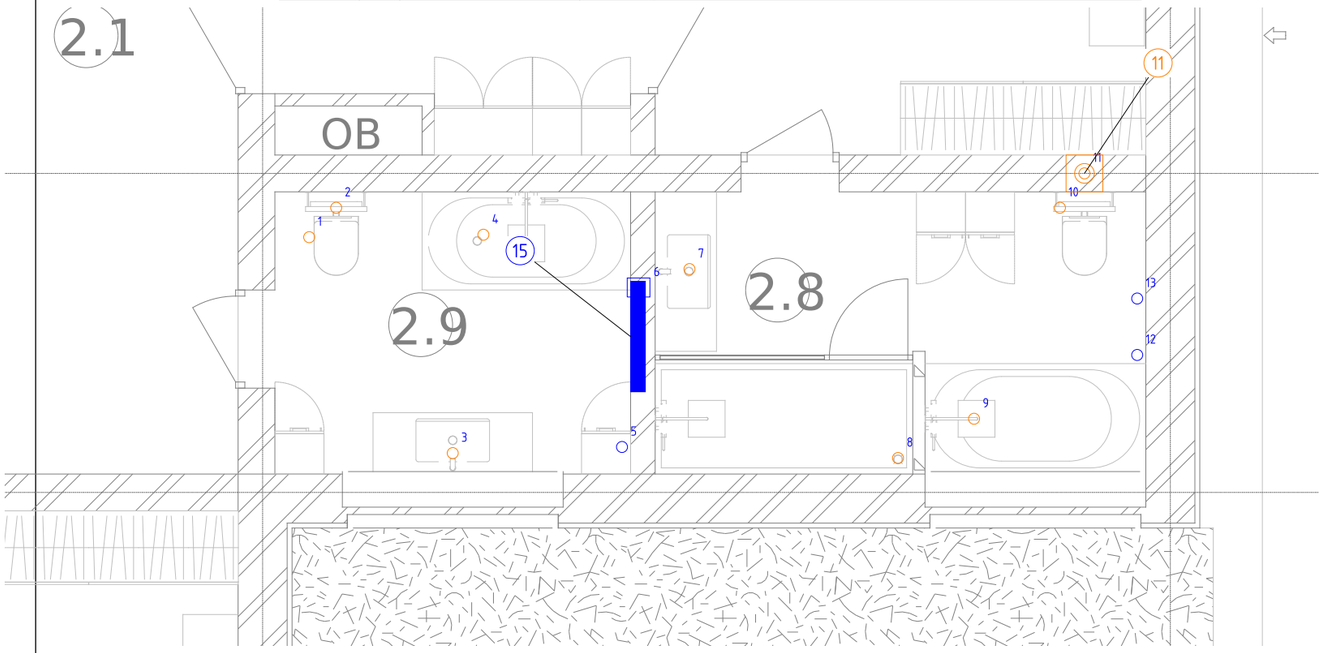

Баня. План. Задание АР и КР. М 1:100

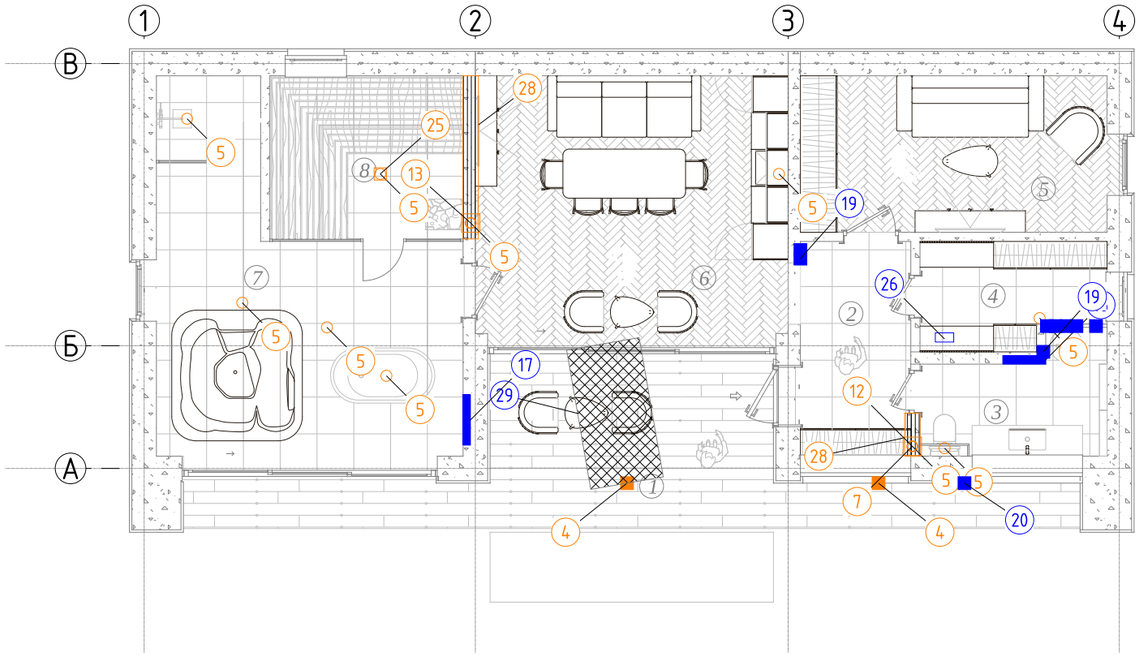

Условные обозначения

- гильза, ниша, проход водопровода
- проход канализации К1 (футляр, люк)
- гильза в плите (координаты — лист 4)
- О-блок газобетонный с отверстием Ф160
- короб гаража, утепление под террасой

Позиции на плане (подробно — листы 3, 4)

4 — футляры Ф160 выпусков К1-б и К1-бв (баня)
5 — гильзы в фундаментной плите (кружки)
6 — гильзы в перекрытии над гаражом (лист 2)
7 — гильзы Ф160 в покрытии, проход кровли
11 — Ст.К1-1в в О-блоках в стене по оси Г
12 — Ст.К1-б в О-блоках, перегородка Б2/Б3 250 мм
13 — прочистки: О-блок в основании стены, люк 300×400
15 — ниша ШВК-2 с нажимным люком
16 — ниша ШВК-Б2 с нажимным люком
17 — ниша ШВК-Б1 в восточной стене Б7
19 — гильзы в основаниях стен (лист 4)
20 — гильзы Ф50 незамерзающих кранов
25 — трап Т-Б2 в парной
26 — места контроллеров защиты от протечек
28 — перегородки Б2/Б3 и Б6/Б8 — 250 мм под О-блоки
29 — утепление над К1-б под террасой Б1

Примечания

1. Номер у точки — позиция таблицы (листы 3, 4); координаты — в метрах от осей 1/А (дом, баня — свои оси), отметки — от ±0,000 своего здания.
2. Подложка — АР (Revit 19.10.2026). Точки и размеры — по 3D-модели систем ВК; при изменении АР или КР задание уточняется.
3. Номер у гильзы перекрытия — строка таблицы «Гильзы в перекрытии» (лист 4).

Изм.	Кол.уч	Лист	№ док	Подп.	Дата	И05.09.26-ВК.ТЗ-1			
						Двухэтажный индивидуальный жилой дом с баней. Московская область, кадастровый номер участка 50:08:0050209:1600			
Разраб.						Водопровод и канализация	Стадия	Лист	Листов
Пров.							Р	2	4
Н.контр.						Задание АР и КР. Перекрытие над гаражом. Баня			
ГИП									

Согласовано

Взам.инв.№

Подпись и дата

Инв.№ подл.

Копировал

Формат А3

Задания АР и КР от раздела ВК

Поз.	Задание	Помещение, место	Привязка, отметки	Раздел	Лист ВК
1	Ввод водопровода без приямка (решение Заказчицы 27.10.2026): футляр ПЭ Ф75 под ввод В1 ПЭ 32 — от наружной грани фундамента под краем плиты (ось −0,850) и вверх сквозь плиту в топочную 1.6 плавным отводом R ≥ 0,3 м; закладывается до бетонирования, трубу можно заменить без вскрытия плиты; торцы футляра — эластичная водо- и газонепроницаемая заделка (п. 8.8 СП 30.13330.2020), заделка — ВК	топочная 1.6, у восточной стены	подъем: х 19,40, у 9,20; под плитой — по у 9,20 до наружной грани, ось −0,850	КР	лист 7, лист 14 узел 1
2	То же — футляр ПЭ Ф75 под подводку автополива КХ-8 РЕ-Ха 25 рядом с вводом: опуск сквозь плиту и под краем плиты наружу	то же	опуск: х 19,30, у 9,30; под плитой — по у 9,62, ось −0,950	КР	лист 7, лист 14 узел 1
3	Футляры ПП Ф160 SN8 L = 1,0 м под краем фундаментной плиты для сборного К1-1 Ф110 (трасса Заказчицы — одной прямой): выпуск на юг в ДК5-018 и ввод линии бани с севера под краем плиты террасы 1.13 — укладываются до бетонирования; если по краю плиты ребро — проем 550×550 (зазор 0,2 м)	дом: юг (у южной стены 1.3), север (терраса 1.13)	юг: х 10,33, у −0,24, лоток −1,350; север: х 14,35, у 15,80, лоток −1,102	КР	лист 6, лист 14 узел 2
4	То же для двух выпусков бани Ф110 на колодец КК-1 во дворе: К1-6 (сборный от Д-61, под террасой 61) и К1-6в (от стояка Ст.К1-6)	баня, юг	К1-6: х 7,87, у −0,24, лоток −0,861; К1-6в: х 11,97, у −0,24, лоток −0,920 (оси бани)	КР	лист 9, лист 14 узел 2
5	Гильзы в фундаментной плите для подъемов К1 к приборам, стояков и выводов прочисток (сеть под плитой — решение Заказчика) — до бетонирования: дом 11 шт., баня 10 шт.	дом, баня	координаты — лист 4	КР	листы 6, 9, 14
6	Гильзы в перекрытии над гаражом (+3,650…+3,850) для подъемов В1, Т3, Т4 и опусков К1 — 12 шт. и 1 проем; близкие трубы — одним проемом под пучок (зазор между гильзами был бы меньше 10 мм)	гараж / с/у 2.8, 2.9	координаты — лист 4	КР	листы 5, 14 узел 4
7	Гильзы Ф160 в плитах покрытия для вытяжных частей стояков: Ст.К1-1в (дом), Ст.К1-6 (баня); проходные элементы кровли — по системе кровли; выход — не ближе 4 м от открываемых окон (п. 18.18)	кровля дома, кровля бани	дом: х 19,30, у 8,90; баня: х 12,53, у 0,36; верх +0,35 над кровлей	АР, КР	листы 12, 14 узел 6
8	Короб (подшивной потолок) под сетями ВК в гараже: низ не выше +2,800 (низ труб в изоляции — +2,829: В1, Т3 к ШВК-1 — ниже магистралей ШВК-2), ширина по трубам; материал — негорючий (гараж); коллекторов и соединений РЕ-Ха над подшивкой нет	гараж	х 12,40…19,88, у 6,41…8,85 (по листу 5)	АР	лист 5
9	Люк 600×600 мм в коробе гаража у ревизии в начале сборного К1 (у стены по оси Г)	гараж	центр х 19,30, у 8,45; ревизия +3,41	АР	лист 5
10	Стояк Ст.К1-1 Ф110 — в стене гараж/1.9 (ось 4) из газобетонных D-блоков с отверстием Ф160 (решение Заказчицы) от плиты до перекрытия; сбоку под потолком гаража — проем Ф160 под вход сборного; люк 300×400 мм в стене со стороны гаража у ревизии +1,000; низ стояка — в грунт под плитой (гильза — поз. 5)	гараж / 1.9	ось отверстия х 12,55, у 8,55	АР	листы 3, 5, 6, 14 узел 5
11	Вытяжная часть Ст.К1-1в Ф110 — в стене по оси Г из газобетонных D-блоков с отверстием Ф160 от потолка гаража (+3,400) сквозь 2 этаж до покрытия, за инсталляцией УН-3 (с/у 2.8); в нижнем блоке — проем Ф160 на юг под отвод к сборному	гараж / с/у 2.8	ось отверстия х 19,30, у 8,90	АР	листы 4, 5, 12
12	Стояк Ст.К1-6 Ф110 (баня) — в перегородке 62/63, расширенной до 250 мм (поз. 28), из газобетонных D-блоков с отверстием Ф160 от плиты до покрытия (решение Заказчицы 27.10.2026); люк 300×400 мм со стороны 62 у ревизии +0,500; низ стояка — двухплоскостная крестовина и два отвода 45° под плитой (гильза Ф160 в плите — поз. 5), проход кровли — поз. 7	баня, перегородка 62/63	ось стояка х 12,53, у 0,36 (оси бани)	АР, КР	листы 8, 9
13	Прочистки сборных К1 в грунте: тройник 45° и короткий прямой вывод вверх (Заказчица 27.10.2026) — заглушка на +0,200 в основании стены в D-блоке с отверстием Ф160 (стена не тоньше 250 мм), люк в стене 300×400 мм (нажимной, под плитку или окраску), низ люка +0,050; люков в полу нет	дом: стена 1.4/1.9 (ось В) — люк из 1.9, стена 1.8/1.13 (ось Д) — люк из 1.8; баня: стена 66/68 — люк из 66	1.8: х 13,85, у 13,80; 1.9: х 11,97, у 6,30; 66: х 5,33, у 4,00	АР	листы 6, 9, 14 узел 5
14	Ниша под шкаф ШВК-1 (В1, Т3) ≈750×600×120 мм (ш×в×г), низ +0,250, со стороны 1.4 между унитазом и душем (эскиз Заказчицы 26.10.2026); нажимной люк под плитку; из низа ниши — канал в стене до пола под трубы в гофре; над нишей — штроба подводок к душу Д-1 (+1,000…+1,080); стена 200 мм, если она несущая — перемычка над нишей по КР	с/у 1.4, стена 1.4/1.3 (гардеробная)	х 10,70…11,45, грань у 4,50	АР	листы 3, 13, 14 узел 10
15	Ниша под шкаф ШВК-2 (В1, Т3) ≈900×650×120 мм, низ +0,250 от пола 2 этажа, со стороны 2.9; нажимной люк под плитку; канал из низа ниши до пола	с/у 2.9, перегородка 2.9/2.8	грань х 15,60, у 7,12…8,02	АР	листы 4, 13, 14 узел 10
16	Ниша под шкаф ШВК-Б2 (В1, Т3) ≈700×600×120 мм, низ +0,300, со стороны 63; нажимной люк под плитку; за нишей — проход Т3 от бойлера Б2 (гильза); канал из низа ниши до пола	баня, с/у 63, перегородка 63/64	х 14,00…14,70, грань у 1,70	АР	листы 8, 13, 14 узел 10
17	Ниша под шкаф ШВК-Б1 (В1, Т3) ≈820×650×120 мм в восточной стене помывочной у южного угла, низ +0,250, со стороны 67 (решение Заказчицы 27.10.2026); нажимной люк под плитку; канал из низа ниши до пола; стена наружная — ниша без ослабления утепления (по КР)	баня, помывочная 67, восточная стена	грань х 5,20, у 0,38…1,20	АР	листы 8, 13, 14 узел 10
18	Гильзы в стене гараж / топочная 1.6 под потолком для магистралей В1, Т3, Т4 — 1 шт. и 1 проем (Ф75 — 5)	гараж / 1.6	х 19,10, х 19,20, х 19,25, х 19,32, х 19,40; отм. +2,850…+2,950…+2,970…+3,100	АР	лист 5
19	Гильзы в основаниях стен и перегородок для труб В1, Т3, Т4 в пироге пола и в выгородке Б2: дом 1 этаж — 4 шт. и 1 проем, 2 этаж — нет, баня — 8 шт.; выходы труб из ниш коллекторов и штроб — каналами в гофре (поз. 14–16, 22)	дом, баня	координаты — лист 4	АР	листы 3, 4, 8, 14 узел 8
20	Гильзы ПП Ф50 в наружных стенах с уклоном 1–2° наружу под незамерзающие поливочные краны ПК-1…ПК-3 (шток 350 мм через стену); слива на зиму не нужно	1.6, терраса 1.13, баня 63	ПК-1: х 20,24, у 12,80, +0,490; ПК-2: х 17,92, у 14,04, +0,340; ПК-3: х 13,38, у −0,24, +0,440 (ПК-3 — оси бани)	АР	листы 3, 8, 14 узел 9
21	Пирог пола 1 этажа и бани: ЭППС не менее 100 мм — трубы В1, Т3, Т4 в пазах в два ряда (оси −0,230 и −0,175); 2 этаж — оси +3,870 и +3,925; стяжка над трубами — по АР; трубы в полу без соединений	дом, баня	лист 14 узел 3	АР	листы 3, 4, 8, 14
22	Штробы: в стене гаража у оси В со стороны гаража ≈120×360 мм от пола до потолка гаража под В1 25, Т3 25, Т4 20 в изоляции; в стенах с/у 1.4 — подводки к душу Д-1 (в стене 1.4/1.3 над нишей ШВК-1 и в стене гаража) и к умывальнику УМ-1 (подъемы из пола в стене по оси В, Т3 — по ней же на +0,900), смесители скрытого монтажа +1,100; в бане — Т4 в перегородке 63/64 под нишей ШВК-Б2 (+0,250) и петля кольца Т3 к смесителю душа Д-61 в стене у душа (+1,100, кран — за люком); дренажи конденсата кондиционеров (ОВ) — в штробах стен (решение Заказчицы)	дом, баня	гараж: х 12,64, у 6,50…6,86; остальное — по листам 3, 8	АР	листы 3, 5, 8
23	Уклон пола и гидроизоляция у трапов Т-1, Т-61, Т-62 и душей Д-3, Д-61; высота трапов — в пироге пола; инсталляции унитазов и подвесных приборов — по АР	с/у, 1.6, 67, 68	по листам 3–6, 8, 9	АР	листы 3–6, 8, 9

Согласовано

Взам.инв.№

Подпись и дата

Инв.№ подл.

Изм.	Кол.уч	Лист	№ док	Подп.	Дата	И05.09.26-ВК.ТЗ-1			
						Двухэтажный индивидуальный жилой дом с баней. Московская область, кадастровый номер участка 50:08:0050209:1600			
Разраб.						Водопровод и канализация	Стадия	Лист	Листов
Пров.							Р	3	4
Н.контр.						Задание АР и КР. Таблица заданий			
ГИП									

Копировал

Формат А3

Задания АР и КР от раЗдела ВК (окончание)

Поз.	Задание	Помещение, место	ПриВяЗка, отметки	РаЗдел	Лист ВК
24	Гараж: углубление в стяжке под лоток ЛГ-1 DN100 вдоль ворот (≈200×150 мм) и уклон пола к лотку; местное понижение фундаментной плиты под пескоуловитель ПУ-1 (≈450×450 мм, на ≈200 мм) с гильЗой Ф160 под вертикальный выпуск; футляр ПП Ф160 SN8 L = 1,0 м под южным краем плиты для выпуска К2-1 (до бетонирования)	гараж, у ворот	ЛГ-1: х 13,30…19,40, у 1,85; ПУ-1: х 19,60, у 1,85; К2-1: х 19,60, лоток −0,800…−0,835	АР, КР	лист 6, лист 14 узел 2
25	Трап Т-Б2 Ду50 в парной: уклон пола к трапу, гидроиЗоляция; гильЗа в плите — в поЗ. 5	баня, Б8	х 3,85, у 4,80	АР	лист 9
26	Защита от протечек: места контроллеров КЗП-1 и КЗП-2; каналы для кабелей датчиков ДП-1…ДП-19 в стенах и полу	1.6 (над стиральной машиной), Б4 (у перегородки Б3/Б4)	КЗП-1: х 17,77, у 9,09, низ +1,620; КЗП-2: х 13,05, у 2,11, низ +1,200	АР	ТЗ-2
27	Терраса 1.13 (неотапливаемая): сборный К1-1 под ней выше глубины промерЗания — над трубой утеплитель ЭППС 50 мм шириной 1,2 м на песчаной подготовке (ВК); учесть в основании террасы	терраса 1.13	по оси К1-1 от у 14,04 до 15,80	КР	лист 6
28	Перегородки бани расширить до 250 мм под гаЗобетонные О-блоки с отверстием Ф160 (решение ЗаказчиЦы 27.10.2026): Б2/Б3 — у стояка Ст.К1-б (в сторону Б2), Б6/Б8 — у прочистки сборного К1-б (в сторону Б6)	баня, Б2/Б3, Б6/Б8	Б2/Б3: х 12,40…12,65, у 0,20…0,90; Б6/Б8: х 5,20…5,45, ось О-блока у 4,00	АР, КР	листы 8, 9
29	Терраса бани Б1 (неотапливаемая): выпуск К1-б под ней выше глубины промерЗания — над трубой утеплитель ЭППС 50 мм шириной 1,2 м на песчаной подготовке (ВК); учесть в основании террасы	баня, терраса Б1	по оси К1-б от х 7,48, у 2,03 до края плиты х 7,87, у −0,24	КР	лист 9

ГильЗы в перекрытии +3,650 (листы 1, 2)

№	ГильЗа	х, м	у, м	Труба
1	Ф75	12,98	8,38	К1 Ф50
2	Ф160	13,20	8,62	К1 Ф110
3	Ф75	14,15	6,62	К1 Ф50
4	Ф75	14,40	8,40	К1 Ф50
5	Ф75	15,53	6,67	Т4 20
6	проем 190×160	15,66	7,97	В1 32, Т3 25
7	Ф75	16,08	8,12	К1 Ф50

№	ГильЗа	х, м	у, м	Труба
8	Ф75	17,78	6,58	К1 Ф50
9	Ф75	18,40	6,90	К1 Ф50
10	Ф160	19,10	8,62	К1 Ф110
11	Ф160	19,30	8,90	К1в Ф110
12	Ф75	19,73	7,42	Т4 20
13	Ф75	19,73	7,88	Т4 20

ГильЗы в фундаментных плитах

Плита	ГильЗа	х, м	у, м	Труба
дом	Ф160	9,10	10,50	К1 Ф110
дом	Ф160	10,20	4,70	К1 Ф110
дом	Ф75	10,20	6,00	К1 Ф50
дом	Ф75	12,00	5,32	К1 Ф50
дом	Ф160	11,97	6,30	К1 прочистка
дом	Ф75	12,45	5,95	К1 Ф50
дом	Ф160	12,55	8,55	К1 Ф110
дом	Ф160	13,85	13,80	К1 прочистка
дом	Ф75	16,90	9,40	К1 Ф50
дом	Ф75	17,00	11,05	К1 Ф50
дом	Ф75	17,70	9,62	К1 Ф50

Плита	ГильЗа	х, м	у, м	Труба
баня	Ф160	0,70	5,70	К1 Ф110
баня	Ф75	1,60	2,70	К1 Ф50
баня	Ф160	2,98	2,30	К1 Ф110
баня	Ф75	3,85	4,80	К1 Ф50
баня	Ф75	3,95	1,51	К1 Ф50
баня	Ф160	5,33	4,00	К1 прочистка
баня	Ф75	10,35	4,80	К1 Ф50
баня	Ф160	12,53	0,36	К1в Ф110
баня	Ф160	13,05	0,33	К1 Ф110
баня	Ф75	14,60	2,45	К1 Ф50

ГильЗы и проемы в основаниях стен и перегородок, в выгородке Б2 — 13 (поЗ. 19)

Где	ГильЗа	х, м	у, м	Отм. оси	Трубы
дом 1 эт.	Ф50	9,55	10,10	−0,230	В1 20
дом 1 эт.	Ф75	9,55	10,22	−0,175	Т3 20
дом 1 эт.	Ф75	9,55	10,34	−0,175	Т4 20
дом 1 эт.	Ф75	11,08	6,30	−0,175	Т4 20
дом 1 эт.	проем 180×170	11,33	6,30	−0,230…−0,175	В1 25, Т3 25

Где	ГильЗа	х, м	у, м	Отм. оси	Трубы
баня	Ф75	10,70	3,42	−0,175	Т4 20
баня	Ф50	10,70	3,56	−0,230	В1 16
баня	Ф75	14,66	1,90	+0,500	Т3 20
баня	Ф75	14,72	2,32	+0,250	Т4 20
баня	Ф50	14,86	2,32	+0,300	В1 20

Где	ГильЗа	х, м	у, м	Отм. оси	Трубы
баня	Ф75	15,04	2,32	+1,100	Т3 20
баня	Ф75	15,20	2,32	+0,650	Т4 20
баня	Ф50	15,52	2,32	+0,800	В1 16

Примечания

1. ГильЗы — по п. 11.5 СП 30.13330.2020 и уЗлу 8 листа 14: внутренний диаметр — с заЗором вокруг трубы в изоляции, Заделка — эластичным негорючим материалом. Соединения труб в гильЗах не допускаются. Проем под пучок — с Заделкой тем же материалом вокруг каждой трубы.
2. Выходы труб иЗ ниш коллекторов и штроб — в гофре по каналу в стене (поЗ. 14–16, 22), отдельных гильЗ не требуют.

Согласовано

Взам.инв.№

Подпись и дата

Инв.№ подл.

Изм.	Кол.уч	Лист	№ док	Подп.	Дата	И05.09.26-ВК.ТЗ-1			
						Двухэтажный индивидуальный жилой дом с баней. Московская область, кадастровый номер участка 50:08:0050209:1600			
Разраб.						Водопровод и канализация	Стадия	Лист	Листов
Пров.							Р	4	4
Н.контр.						Задание АР и КР. Таблица заданий (окончание). ГильЗы			
ГИП									

Копировал

Формат А3