
# План 1 этажа. Задание АР и КР. М 1:100

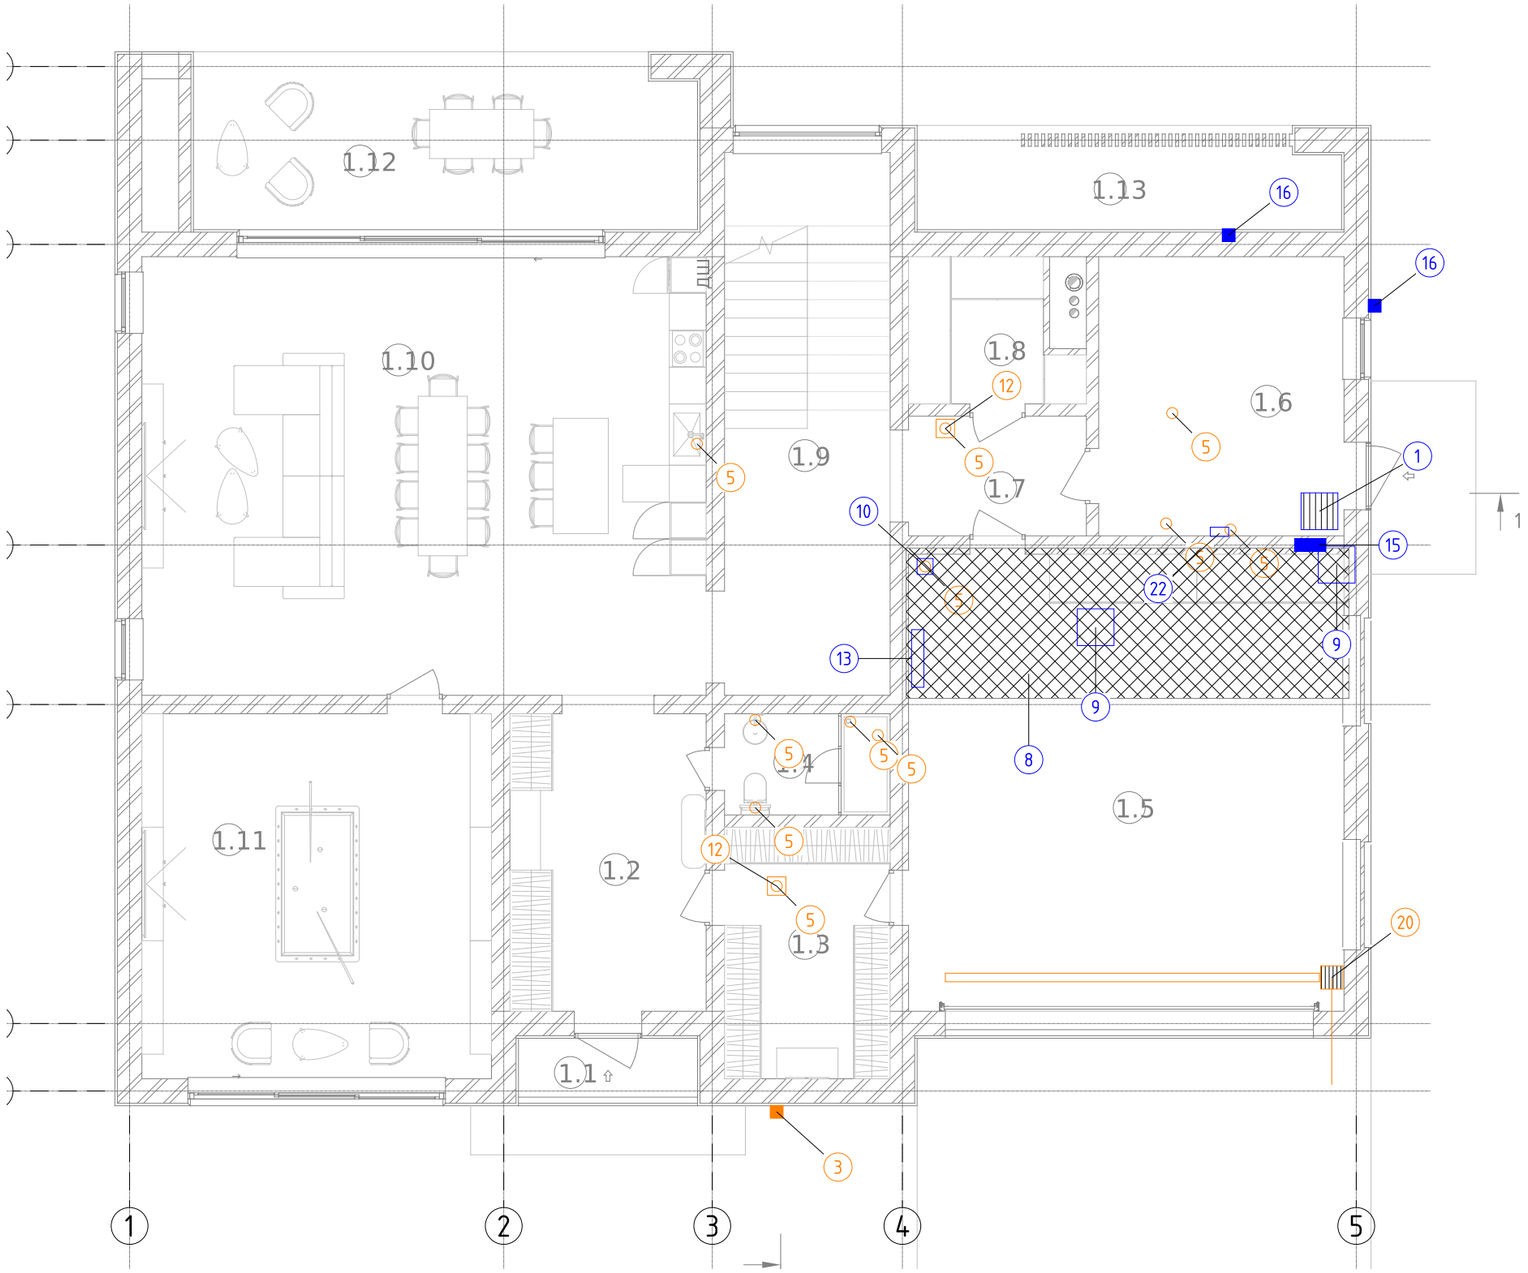


## Условные обозначения

- проход, место оборудования, люк (водопровод)
- проход канализации К1 (футляр, гильза, люк)
- гильза в плите (номер — таблица листа 3)
- короб (подшивной потолок) гаража

## Позиции на плане (подробно — лист 3)

1 — приямок ввода 600×600, дно −1,100; 2 — проем 450×450 под ввод
3 — футляр Ø160 выпуска К1-1 под краем плиты
5 — гильзы в фундаментной плите (кружки)
8 — короб гаража, низ не выше +2,900
9 — люки 600×600 в коробе
10 — короб стояка Ст.К1-1, люк 300×400
12 — люки в полу 300×300 над прочистками
13 — место ШВК-1
15 — гильзы в стене гараж/1.6
16 — гильзы поливочных кранов
20 — гараж: лоток ЛГ-1, понижение плиты под ПУ-1, футляр К2-1
22 — места контроллеров защиты от протечек

## Примечания

1. Номер у точки — позиция таблицы (лист 3); координаты — в метрах от осей 1/А (дом, баня — свои оси), отметки — от ±0,000 своего здания.
2. Подложка — АР (Revit 19.10.2026). Точки и размеры — по 3D-модели систем ВК; при изменении АР или КР задание уточняется.

Согласовано

Взам.инв.№

Подпись и дата


Инв.№ подл.

| Изм. | Кол.уч | Лист | № док | Подп. | Дата | И05.09.26-ВК.ТЗ-1 | | |
|---|---|---|---|---|---|---|---|---|
| | | | | | | Двухэтажный индивидуальный жилой дом с баней. Московская область, кадастровый номер участка 50:08:0050209:1600 | | |
| Разраб. | | | | | | Водопровод и канализация | Стадия | Лист | Листов |
| Пров. | | | | | | | Р | 1 | 3 |
| Н.контр. | | | | | | Задание АР и КР. План 1 этажа | | | |
| ГИП | | | | | | | | | |


Копировал

Формат А3

## Гильзы в перекрытии над гаражом (вид на план 2 этажа). М 1:50

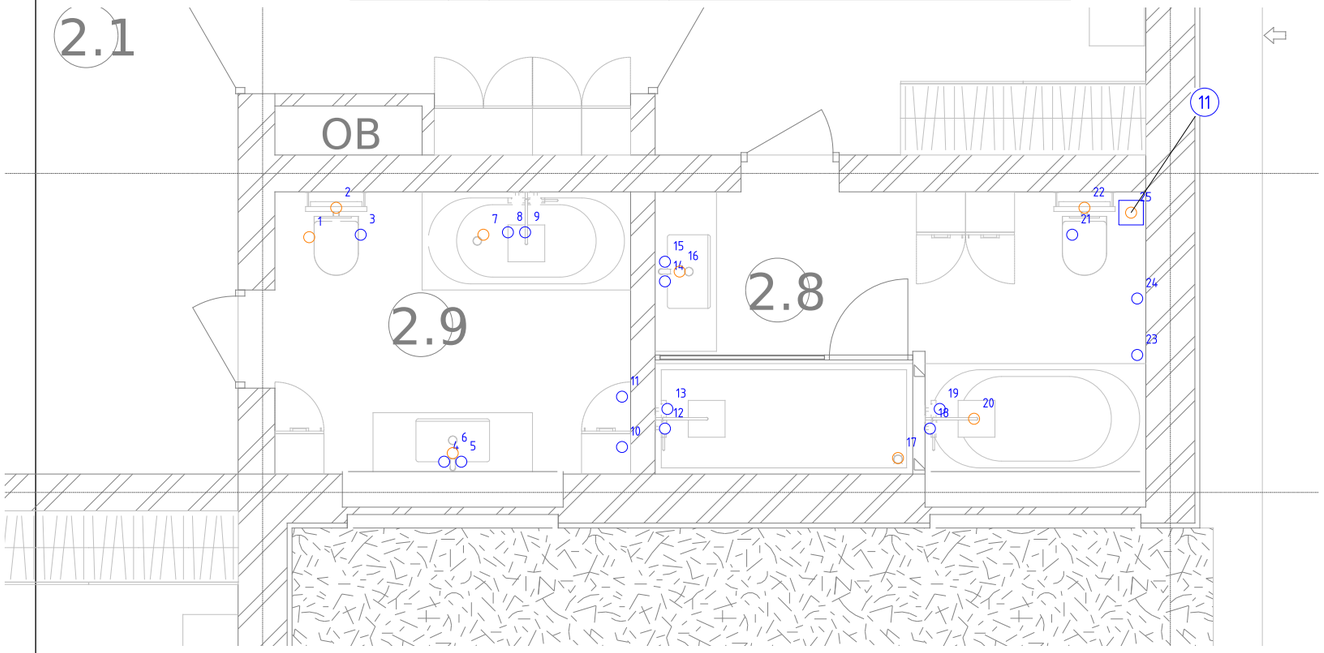


## Баня. План. Задание АР и КР. М 1:100

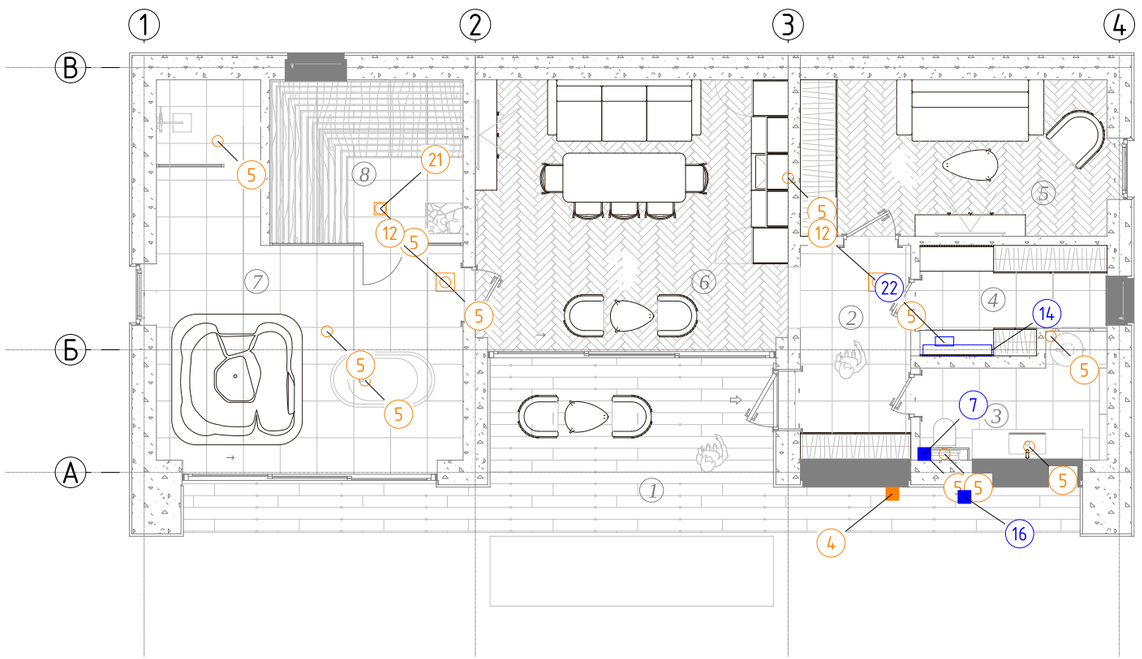


## Условные обозначения

- проход, место оборудования, люк (водопровод)
- проход канализации К1 (футляр, гильза, люк)
- гильза в плите (номер — таблица листа 3)
- короб (подшивной потолок) гаража

## Позиции на плане (подробно — лист 3)

4 — футляр Ф160 выпуска К1-6 (баня)
5 — гильзы в фундаментной плите (кружки)
6 — гильзы в перекрытии над гаражом (лист 2)
7 — гильзы Ф160 в покрытии, проход кровли
11 — короб вытяжной части Ст.К1-1в (2.8), гильза Ф160 в покрытии (7)
12 — люки в полу 300×300 над прочистками
14 — место ШВК-Б
16 — гильзы поливочных кранов
17 — гильзы в стене Б2/Б6 (лист 8)
21 — трап Т-Б2 в парной
22 — места контроллеров Защиты от протечек

## Примечания

1. Номер у точки — позиция таблицы (лист 3); координаты — в метрах от осей 1/А (дом, баня — свои оси), отметки — от ±0,000 своего здания.
2. Подложка — АР (Revit 19.10.2026). Точки и размеры — по 3D-модели систем ВК; при изменении АР или КР задание уточняется.
3. Номер у гильзы перекрытия — строка таблицы «Гильзы в перекрытии» (лист 3).

Согласовано

Взам.инв.№

Подпись и дата

Инв.№ подл.

| Изм. | Кол.уч | Лист | № док | Подп. | Дата | И05.09.26-ВК.ТЗ-1 | | | |
|---|---|---|---|---|---|---|---|---|---|
| | | | | | | Двухэтажный индивидуальный жилой дом с баней. Московская область, кадастровый номер участка 50:08:0050209:1600 | | | |
| Разраб. | | | | | | Водопровод и канализация | Стадия | Лист | Листов |
| Пров. | | | | | | | Р | 2 | 3 |
| Н.контр. | | | | | | Задание АР и КР. Перекрытие над гаражом. Баня | | | |
| ГИП | | | | | | | | | |

Копировал

Формат А3

# Задания АР и КР от раЗдела ВК

| Поз. | Задание | Помещение, место | ПривяЗка, отметки | РаЗдел | Лист ВК |
|---|---|---|---|---|---|
| 1 | Приямок ввода водопровода 600×600 мм в свету, дно −1,100, водонепроницаемый, с утепленной крышкой в уровне пола; местное Заглубление фундаментной плиты от приямка до наружной грани (низ −1,250) | топочная 1.6, у восточной стены | x 19,10…19,70, y 9,15…9,75 | КР | лист 7, лист 14 узел 1 |
| 2 | Проем 450×450 мм в наружной стенке приямка (заглублении плиты) под ввод В1 ПЭ 32 — ЗаЗор 0,2 м вокруг трубы (п. 8.8 СП 30.13330.2020); в том же проеме — подводка автополива КХ-8 РЕ-Ха 25 (y 9,62, отм. −0,950); Заделка — ВК | то же | ось ввода y 9,45, отм. оси −0,850 | КР | лист 14 узел 1 |
| 3 | Футляр ПП Ф160 SN8 L = 1,0 м под краем фундаментной плиты для выпуска К1-1 Ф110 — укладывается до бетонирования; если плита продолжается под террасой 1.13 — футляр у ее края; если по краю плиты ребро — проем 550×550 (ЗаЗор 0,2 м) | дом, юг (южная стена гардеробной 1.3, восточнее крыльца) | x 10,55; лоток у границы −1,169 | КР | лист 6, лист 14 узел 2 |
| 4 | То же для выпуска К1-б Ф110 | баня, юг | x 12,20; лоток у границы −0,994 | КР | лист 9, лист 14 узел 2 |
| 5 | ГильЗы в фундаментной плите для стояков К1 (сеть под плитой — решение Заказчика) — до бетонирования: дом 11 шт., баня 11 шт. | дом, баня | координаты — таблица на листе 3 | КР | листы 6, 9, 14 |
| 6 | ГильЗы в перекрытии над гаражом (+3,650…+3,850) для подъемов В1, Т3, Т4 и опусков К1 — 25 шт. | гараж / с/у 2.8, 2.9 | координаты — таблица на листе 3 | КР | листы 5, 14 узел 4 |
| 7 | ГильЗы Ф160 в плитах покрытия для вытяжных частей стояков: Ст.К1-1в (дом), Ст.К1-б (баня); проходные элементы кровли — по системе кровли; выход — не ближе 4 м от открываемых окон (п. 18.18) | кровля дома, кровля бани | дом: x 19,68, y 8,58; баня: x 12,72, y 0,30; верх +0,35 над кровлей | АР, КР | листы 12, 14 узел 6 |
| 8 | Короб (подшивной потолок) под сетями ВК в гараже: низ не выше +2,900, ширина по трубам; материал — негорючий (гараж) | гараж | x 12,66…19,88, y 6,40…8,85 (по листу 5) | АР | лист 5 |
| 9 | Люки 600×600 мм в коробе гаража: у коллекторов ШВК-2 и у прочистки в начале сборного К1 | гараж | ШВК-2: x 15,75, y 7,56; прочистка: x 19,68, y 8,58 | АР | лист 5 |
| 10 | Короб стояка Ст.К1-1 Ф110 (≈250×250 мм) от пола до потолка гаража с люком 300×400 мм у ревиЗии на +1,000; звукоиЗоляция стояка | гараж, северо-Западный угол | x 12,97, y 8,55 | АР | листы 5, 6 |
| 11 | Короб вытяжной части Ст.К1-1в Ф110 (≈200×200 мм) сквоЗь 2 этаж до кровли | с/у 2.8 | x 19,68, y 8,58 | АР | листы 5, 12 |
| 12 | Люки напольные 300×300 мм (герметичные, под плитку) над стояками прочисток К1 в грунте | 1.7, 1.3; б7, б2 | дом: x 13,30, y 10,80 и x 10,55, y 3,34; баня: x 4,91, y 3,10 и x 11,96, y 3,10 | АР | лист 14 узел 5 |
| 13 | Место под шкаф ШВК-1 накладной ≈950×700×200 мм, низ +0,400; выходы труб из шкафа — вниЗ в пол | гараж, Западная стена | x 12,75, y 6,58…7,52 | АР | листы 4, 13 |
| 14 | Место под шкаф ШВК-Б накладной ≈1100×650×180 мм, низ +0,300; перегородка — под нагрузку ≈40 кг | баня, б4, на перегородке б3/б4 | x 12,70…13,82, y 2,08 | АР | листы 8, 13 |
| 15 | ГильЗы в стене гараж / топочная 1.6 под потолком для магистралей В1, Т3, Т4 — 3 шт. | гараж / 1.6 | x 19,10, x 19,25, x 19,40; отм. +3,050…+3,250 | АР | лист 5 |
| 16 | ГильЗы Ф75 в наружных стенах для поливочных кранов ПК-1, ПК-2, ПК-3 | 1.6, терраса 1.13, баня б3 | ПК-1: x 20,30, y 12,80, +0,47; ПК-2: x 17,92, y 13,95, +0,32; ПК-3: x 13,38, y −0,40, +0,42 | АР | листы 3, 8 |
| 17 | ГильЗы в стене б2/б6 и дверных проемах для пучка труб В1, Т3 к б6, б7 (лист 8): Ф50 — 4, Ф75 — 4 | баня | по листу 8 | АР | лист 8 |
| 18 | Пирог пола 1 этажа и бани: ЭППС не менее 100 мм — трубы В1, Т3, Т4 в паЗах в два ряда (оси −0,230 и −0,175); стяжка над трубами — по АР; трубы в полу беЗ соединений | дом, баня | лист 14 узел 3 | АР | листы 3, 8, 14 |
| 19 | Штробы и инсталляции для подъемов к приборам; уклон пола и гидроиЗоляция у трапов Т-1, Т-б1, Д-3, Д-б1; высота трапов — в пироге пола | с/у, 1.6, б7 | по листам 3–5, 8, 9 | АР | листы 3–6, 8, 9 |
| 20 | Гараж: углубление в стяжке под лоток ЛГ-1 DN100 вдоль ворот (≈200×150 мм) и уклон пола к лотку; местное понижение фундаментной плиты под пескоуловитель ПУ-1 (≈450×450 мм, на ≈200 мм) с гильЗой Ф160 под вертикальный выпуск; футляр ПП Ф160 SN8 L = 1,0 м под южным краем плиты для выпуска К2-1 (до бетонирования) | гараж, у ворот | ЛГ-1: x 13,30…19,40, y 1,85; ПУ-1: x 19,60, y 1,85; К2-1: x 19,60, лоток −0,800…−0,835 | АР, КР | лист 4, лист 14 узел 2 |
| 21 | Трап Т-б2 Ду50 в парной: уклон пола к трапу, гидроиЗоляция; гильЗа в плите — в поЗ. 5 | баня, б8 | x 3,85, y 4,30 | АР | лист 9 |
| 22 | Защита от протечек: места контроллеров КЗП-1 (1.6, над стиральной машиной, низ +1,620) и КЗП-2 (б4, над ШВК-Б, низ +1,200); каналы для кабелей датчиков ДП в стенах и полу | дом, баня | листы 3–5, 8 | АР | Т3-2 |

## ГильЗы в перекрытии +3,650 (лист 2)

| № | ГильЗа | x, м | y, м | Труба |
|---|---|---|---|---|
| 1 | Ф75 | 12,98 | 8,38 | К1 Ф50 |
| 2 | Ф160 | 13,20 | 8,62 | К1 Ф110 |
| 3 | Ф50 | 13,40 | 8,40 | В1 РЕ-Ха 16×2,2 |
| 4 | Ф50 | 14,08 | 6,55 | В1 РЕ-Ха 16×2,2 |
| 5 | Ф75 | 14,22 | 6,55 | Т3 РЕ-Ха 16×2,2 |
| 6 | Ф75 | 14,15 | 6,62 | К1 Ф50 |
| 7 | Ф75 | 14,40 | 8,40 | К1 Ф50 |
| 8 | Ф50 | 14,60 | 8,42 | В1 РЕ-Ха 20×2,8 |
| 9 | Ф75 | 14,74 | 8,42 | Т3 РЕ-Ха 20×2,8 |
| 10 | Ф75 | 15,53 | 6,67 | Т4 РЕ-Ха 20×2,8 |
| 11 | Ф75 | 15,53 | 7,08 | Т4 РЕ-Ха 20×2,8 |
| 12 | Ф50 | 15,88 | 6,82 | В1 РЕ-Ха 16×2,2 |
| 13 | Ф75 | 15,90 | 6,98 | Т3 РЕ-Ха 16×2,2 |
| 14 | Ф50 | 15,88 | 8,02 | В1 РЕ-Ха 16×2,2 |
| 15 | Ф75 | 15,88 | 8,18 | Т3 РЕ-Ха 16×2,2 |
| 16 | Ф75 | 16,00 | 8,10 | К1 Ф50 |
| 17 | Ф75 | 17,78 | 6,58 | К1 Ф50 |
| 18 | Ф50 | 18,04 | 6,82 | В1 РЕ-Ха 20×2,8 |
| 19 | Ф75 | 18,12 | 6,98 | Т3 РЕ-Ха 20×2,8 |
| 20 | Ф75 | 18,40 | 6,90 | К1 Ф50 |
| 21 | Ф50 | 19,20 | 8,40 | В1 РЕ-Ха 16×2,2 |
| 22 | Ф160 | 19,30 | 8,62 | К1 Ф110 |
| 23 | Ф75 | 19,73 | 7,42 | Т4 РЕ-Ха 20×2,8 |
| 24 | Ф75 | 19,73 | 7,88 | Т4 РЕ-Ха 20×2,8 |
| 25 | Ф160 | 19,68 | 8,58 | К1в Ф110 |

## ГильЗы в фундаментных плитах

| Плита | ГильЗа | x, м | y, м | Труба |
|---|---|---|---|---|
| дом | Ф75 | 9,25 | 10,55 | К1 Ф50 |
| дом | Ф160 | 10,20 | 4,62 | К1 Ф110 |
| дом | Ф75 | 10,20 | 6,05 | К1 Ф50 |
| дом | Ф75 | 11,75 | 6,02 | К1 Ф50 |
| дом | Ф75 | 12,20 | 5,80 | К1 Ф50 |
| дом | Ф160 | 12,97 | 8,55 | К1 Ф110 |
| дом | Ф75 | 16,90 | 9,25 | К1 Ф50 |
| дом | Ф75 | 17,00 | 11,05 | К1 Ф50 |
| дом | Ф75 | 17,95 | 9,15 | К1 Ф50 |
| дом | Ф160 | 13,30 | 10,80 | К1 прочистка |
| дом | Ф160 | 10,55 | 3,34 | К1 прочистка |
| баня | Ф160 | 1,20 | 5,40 | К1 Ф110 |
| баня | Ф160 | 2,98 | 2,30 | К1 Ф110 |
| баня | Ф75 | 3,60 | 1,50 | К1 Ф50 |
| баня | Ф75 | 3,85 | 4,30 | К1 Ф50 |
| баня | Ф75 | 10,50 | 4,80 | К1 Ф50 |
| баня | Ф160 | 12,72 | 0,30 | К1в Ф110 |
| баня | Ф160 | 13,05 | 0,30 | К1 Ф110 |
| баня | Ф75 | 14,43 | 0,42 | К1 Ф50 |
| баня | Ф75 | 14,78 | 2,22 | К1 Ф50 |
| баня | Ф160 | 4,91 | 3,10 | К1 прочистка |
| баня | Ф160 | 11,96 | 3,10 | К1 прочистка |

Согласовано

Взам.инв.№

Подпись и дата

Инв.№ подл.

| Изм. | Кол.уч | Лист | № док | Подп. | Дата |
|---|---|---|---|---|---|
| Разраб. | | | | | |
| Пров. | | | | | |
| | | | | | |
| Н.контр. | | | | | |
| ГИП | | | | | |

**И05.09.26-ВК.Т3-1**

Двухэтажный индивидуальный жилой дом с баней. Московская область, кадастровый номер участка 50:08:0050209:1600

Водопровод и канализация

| Стадия | Лист | Листов |
|---|---|---|
| Р | 3 | 3 |

Задание АР и КР. Таблица заданий. ГильЗы

Копировал

Формат А3