
План 1 этажа на отм. 0,000

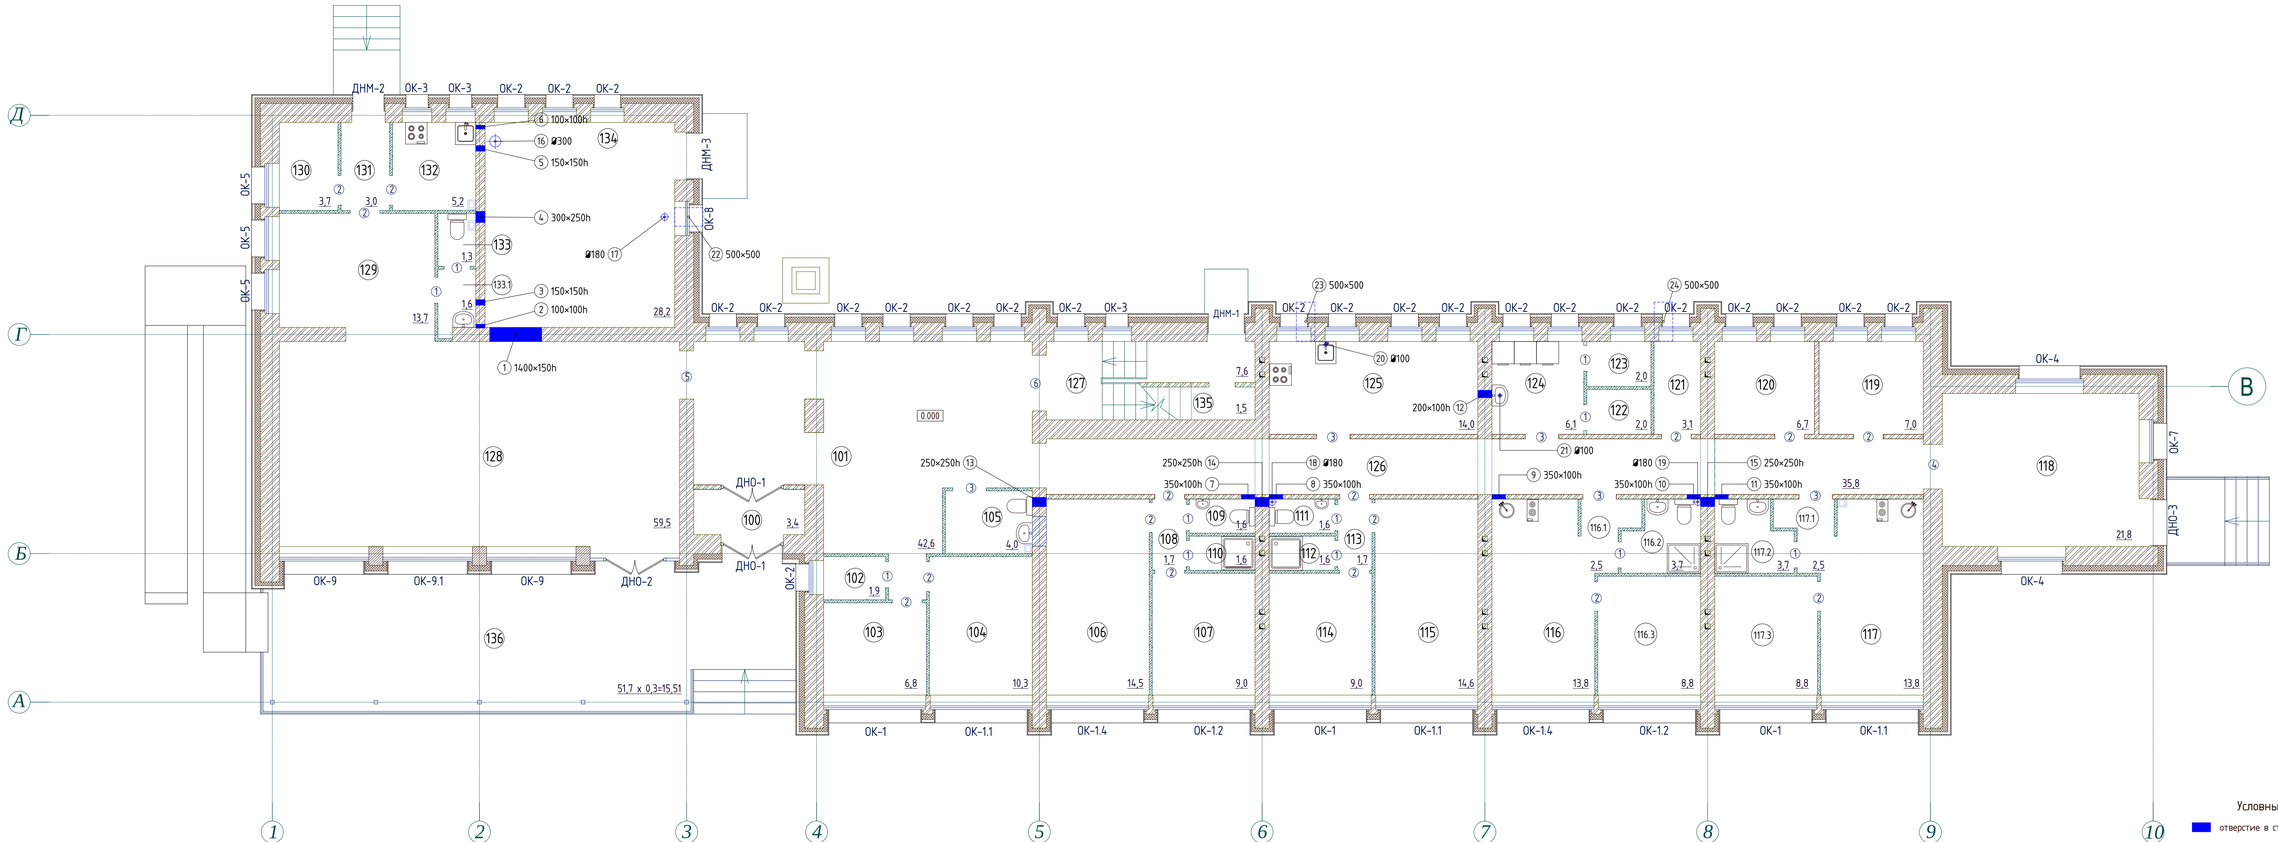


Ведомость отверстий

Поз.	Размер, мм	Конструкция	Низ, м	Назначение
1	1400×150h	Стена между пом. 134 и 128 (ось Г)	−0,150	В1, Т3, Т4 от коллекторов к стоякам – 15 труб d 20–32 в изоляции
2	100×100h	Стена по оси 2, пом. 133.1	−0,150	подводки В1, Т3 d 20
3	150×150h	Стена по оси 2, пом. 133.1	−0,250	К1 d 50 (умывальник)
4	300×250h	Стена по оси 2, пом. 133	−0,350	К1 d 110 к выпуску К1-1, В1 d 20
5	150×150h	Стена по оси 2, пом. 132	−0,250	К1 d 50 (мойка)
6	100×100h	Стена по оси 2, пом. 132	−0,150	подводки В1, Т3 d 20 (мойка)
7	350×100h	Перегородка кирпичная (сущ.) в осях 5–6	−0,150	стояки В1-2, Т3-2, Т4-2 – 3 трубы
8	350×100h	Перегородка кирпичная (сущ.) в осях 6–7	−0,150	стояки В1-3, Т3-3, Т4-3 – 3 трубы
9	350×100h	Перегородка кирпичная (сущ.) в осях 7–8	−0,150	стояки В1-4, Т3-4, Т4-4 – 3 трубы
10	350×100h	Перегородка кирпичная (сущ.) в осях 7–8	−0,150	стояки В1-5, Т3-5, Т4-5 – 3 трубы
11	350×100h	Перегородка кирпичная (сущ.) в осях 8–9	−0,150	стояки В1-6, Т3-6, Т4-6 – 3 трубы
12	200×100h	Стена по оси 7	−0,150	В1, Т3 к пом. 124
13	250×250h	Стена по оси 5	−0,350	К1 d 110 от Ст К1-1 к выпуску К1-2
14	250×250h	Стена по оси 6	−0,450	К1 d 110 от Ст К1-1 к выпуску К1-2
15	250×250h	Стена по оси 8	−0,400	К1 d 110 от приборов пом. 117.1, 117.2 к Ст К1-3
16	Ø300	Плита пола, пом. 134	–	ввод В1 d 63 в гильзе Ду 250 (узел 1 ВК; гильза – по разделу НВ)
17	Ø180	Плита пола, пом. 134	–	К1 d 110 к выпуску К1-1 (узел 2 ВК)
18	Ø180	Плита пола в осях 6–7	–	стояк К1-2 к выпуску К1-2 (узел 2 ВК)
19	Ø180	Плита пола в осях 7–8	–	стояк К1-3 к выпуску К1-3 (узел 2 ВК)
20	Ø100	Плита пола, пом. 125	–	К1 d 50 (мойка) к выпуску К1-2
21	Ø100	Плита пола, пом. 124	–	К1 d 50 к выпуску К1-3
22	500×500	Фундамент наружной стены по оси 3	−2,260	выпуск К1-1 d 110, лоток у наружной грани стены −2,060
23	500×500	Фундамент наружной стены по оси Г	−2,400	выпуск К1-2 d 110, лоток у наружной грани стены −2,200
24	500×500	Фундамент наружной стены по оси Г	−2,360	выпуск К1-3 d 110, лоток у наружной грани стены −2,160
25	550×200	Перекрытие 1 этажа в осях 4–5	–	стояки В1-1, Т3-1, Т4-1 (гильзы d 63) и К1-1 (гильза d 125, противопожарная муфта)
26	350×150	Перекрытие 1 этажа в осях 5–6	–	стояки В1-2, Т3-2, Т4-2 (гильзы d 63)
27	550×200	Перекрытие 1 этажа в осях 6–7	–	стояки В1-3, Т3-3, Т4-3 (гильзы d 63) и К1-2 (гильза d 125, противопожарная муфта)
28	350×150	Перекрытие 1 этажа в осях 7–8	–	стояки В1-4, Т3-4, Т4-4 (гильзы d 63)
29	550×200	Перекрытие 1 этажа в осях 7–8	–	стояки В1-5, Т3-5, Т4-5 (гильзы d 63) и К1-3 (гильза d 125, противопожарная муфта)
30	350×150	Перекрытие 1 этажа в осях 8–9	–	стояки В1-6, Т3-6, Т4-6 (гильзы d 63)
31	300×250h	Стена по оси 5, 2 этаж	+3,650	К1 d 110, В1 и Т3 d 20
32	250×250h	Стена по оси 6, 2 этаж	+3,650	К1 d 110
33	150×100h	Стена по оси 7, 2 этаж	+3,700	подводки В1, Т3 d 20
34	250×250h	Стена по оси 8, 2 этаж	+3,650	К1 d 110
35	Ø200	Покрытие над 2 этажом и кровля	–	вентстояк К1-1 d 110, выход на кровлю (поз. 83 ВК.СО)
36	Ø200	Покрытие над 2 этажом и кровля	–	вентстояк К1-2 d 110, выход на кровлю (поз. 83 ВК.СО)
37	Ø200	Покрытие над 2 этажом и кровля	–	вентстояк К1-3 d 110, выход на кровлю (поз. 83 ВК.СО)

Примечания

1. Задание разделам АР и КР на устройство отверстий для трубопроводов внутренних систем В1, Т3, Т4 и К1 по разделу 140-1/2026-ВК (листы 2, 4, 6). Размеры – в мм, отметки – в м от чистого пола 1 этажа (0,000); «h» – высота отверстия в стене.
2. Отверстия в существующих несущих стенах, перекрытиях и фундаментах – по решению раздела КР (при необходимости – с перемычками и усилением). Групповое отверстие поз. 1 по согласованию с КР допускается выполнить двумя отверстиями.
3. Проходы – по узлам 1–3 листа 6 ВК: трубопроводы в гильзах. Зазоры Заделываются негорючим материалом, стояки К1 в перекрытии – с противопожарными муфтами. Отверстия в плите пола – алмазным бурением.
4. Выпуски К1 через фундамент – с зазором вокруг трубы около 0,2 м и заделкой эластичным водогазонепроницаемым материалом; если подошва фундамента выше выпуска, отверстие не требуется. Проход ввода В1 через фундамент – по разделу 140-1/2026-НВ.
5. Отметки отверстий для К1 уточняются по месту с учётом уклона трубопроводов (лист 5 ВК).
6. Отверстия в новых перегородках выполняются при их возведении по месту и в задании не показаны; штрабы для подводок к приборам в несущих стенах – по согласованию с КР.
7. Выход вентстояков К1 через кровлю (поз. 35–37) – проходными элементами под тип кровли (поз. 83 ВК.СО).

План 2 этажа на отм. +3,650

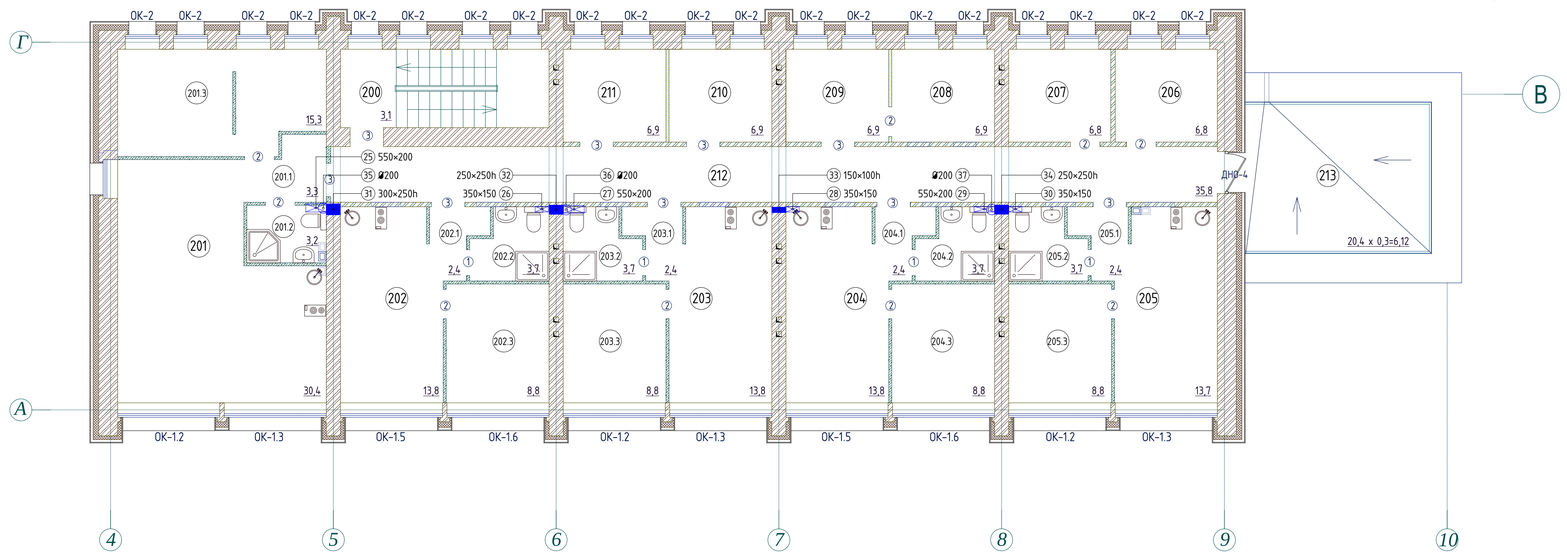

Условные обозначения

- отверстие в стене, перегородке
- отверстие в перекрытии
- отверстие в плите пола
- отверстие в фундаменте (ниже пола)
- отверстие в покрытии (на кровлю)
- (N) позиция по ведомости и размер

Изм.	Колуч	Лист	№ док.	Подп.	Дата	140-1/2026-ВК.ТЗ-1			
Разработал	Захаров				10.26	Двухэтажное здание главного корпуса базы отдыха по адресу: Россия, 188767, Северо-западный ФО, Ленинградская область, Приозерский район, с/п Плодовое, поселок Кутузовское, территория Базы отдыха, д. 6/н, литера А			
						Внутренние водопровод и канализация	Стадия	Лист	Листов
Проверил	Ковшов				10.26		РД	1	1
						Техническое задание на устройство отверстий. План 1 этажа. План 2 этажа	ООО"Петровская Архитектура"		
ГИП	Ковшов				10.26				

Согласовано

Взам.инв.№

Подпись и дата

Инв.№ подл.

Копировал

Формат А1