
План 1 этажа на отм. 0,000

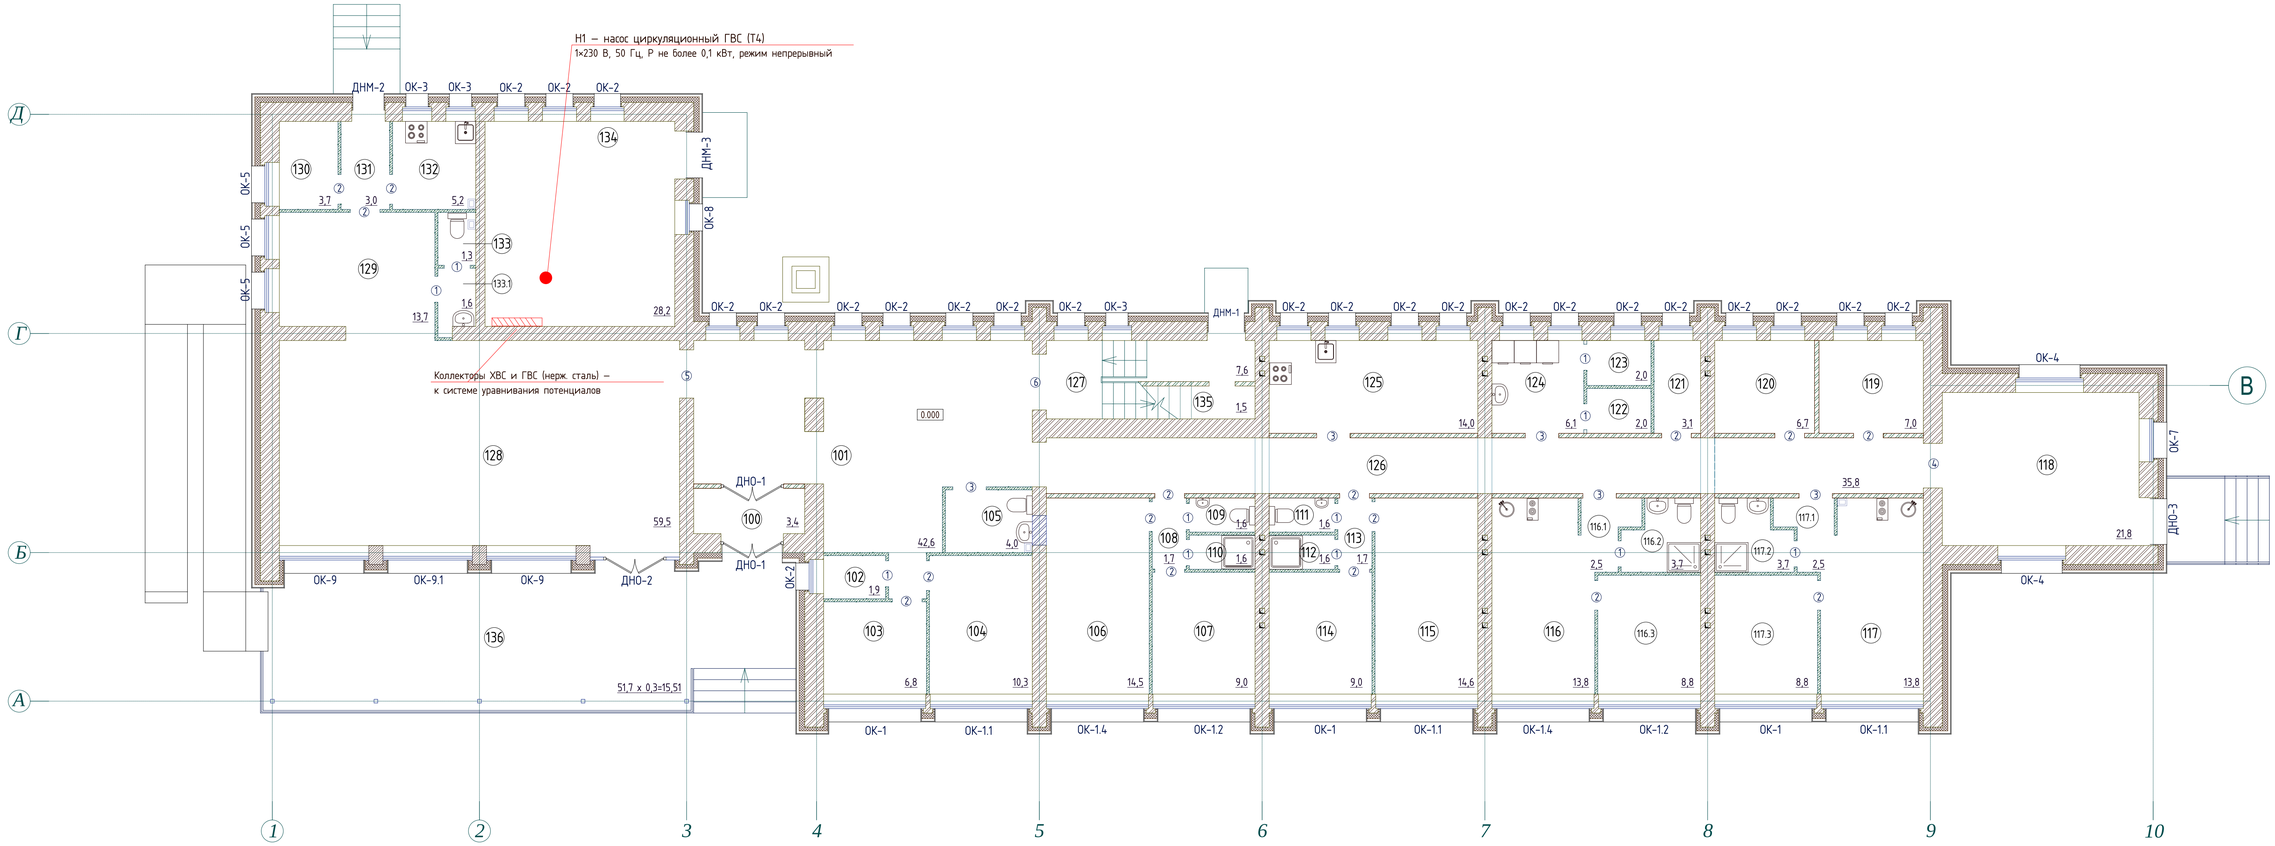

Перечень электропотребителей раздела ВК

Поз.	Наименование	Помещение	Кол.	Напряжение, В	Р уст., кВт	Режим работы	Примечание
Н1	Насос циркуляционный ГВС (система Т4): Q = 1,5 м³/ч, Н не менее 1,8 м, t до 95 °С	134 (котельная)	1	1×230, 50 Гц	не более 0,1	непрерывный, круглосуточно	мощность – по паспорту выбранного насоса (поз. 46 ВК.СО)

Примечания

1. Задание разделу ЭОМ на электроснабжение оборудования внутренних систем водопровода и канализации по разделу 140-1/2026-ВК. Других электропотребителей в разделе ВК нет: водонагреватель (ИТП) – по разделу ОВ, ввод В1 и водомерный узел – по разделу НВ.
2. Насос Н1 подключить отдельной группой; место подключения – розетка с заземляющим контактом или клеммная коробка со степенью защиты не ниже IP44 на стене у насоса, на высоте около 1,0 м от пола (уточнить по месту при монтаже). Защитные аппараты – по решению ЭОМ.
3. Металлические части систем ВК в пом. 134 – коллекторы ХВС и ГВС из нержавеющей стали и стальная оцинкованная труба Ду 32 от водомерного узла к коллектору – присоединить к системе уравнивания потенциалов. Трубопроводы В1, Т3, Т4 и К1 внутри здания – полимерные.
4. Электрообогрев трубопроводов не требуется: ввод В1 проложен на отм. −2,480 (раздел НВ), трубопроводы внутри здания – в отапливаемых помещениях.

Условные обозначения

- электропотребитель ВК (насос)
- металлическое оборудование – к системе уравнивания потенциалов

Изм.	Кол.уч	Лист	№ док	Подп.	Дата	140-1/2026-ВК.ТЗ-2	
Разработал		Захаров			10.26	Двухэтажное здание главного корпуса базы отдыха по адресу: Россия, 188767, Северо-Западный ФО, Ленинградская область, Приозерский район, с/п Плодовое, поселок Кутузовское, территория базы отдыха, д. б/н, литера А	
Проверил		Ковшов			10.26	Внутренние водопровод и канализация	Стадия: РД; Лист: 1; Листов: 1
ГИП		Ковшов			10.26	Техническое Задание на подвод электропитания. План 1 этажа	ООО "Петровская Архитектура"

Согласовано | Взам.инв.№ | Подпись и дата | Инв.№ подл.

Копировал | Формат А1