


Общий вид с юго-запада — с сетями ОВ (П1, воздуховоды) для увязки

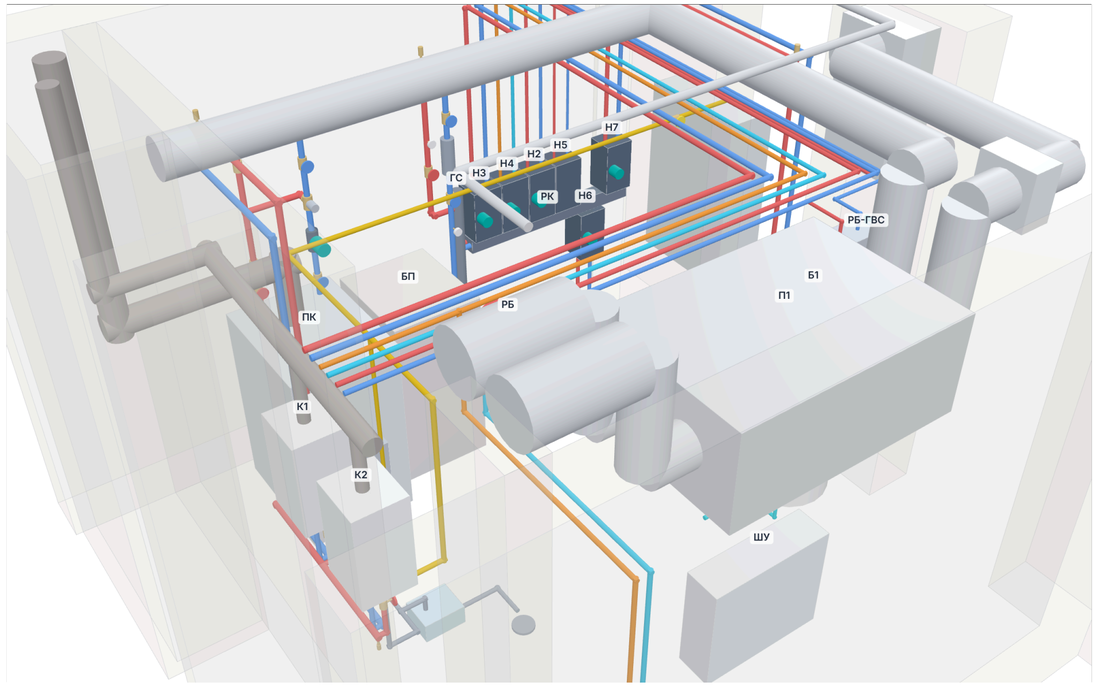


Тот же вид без сетей ОВ

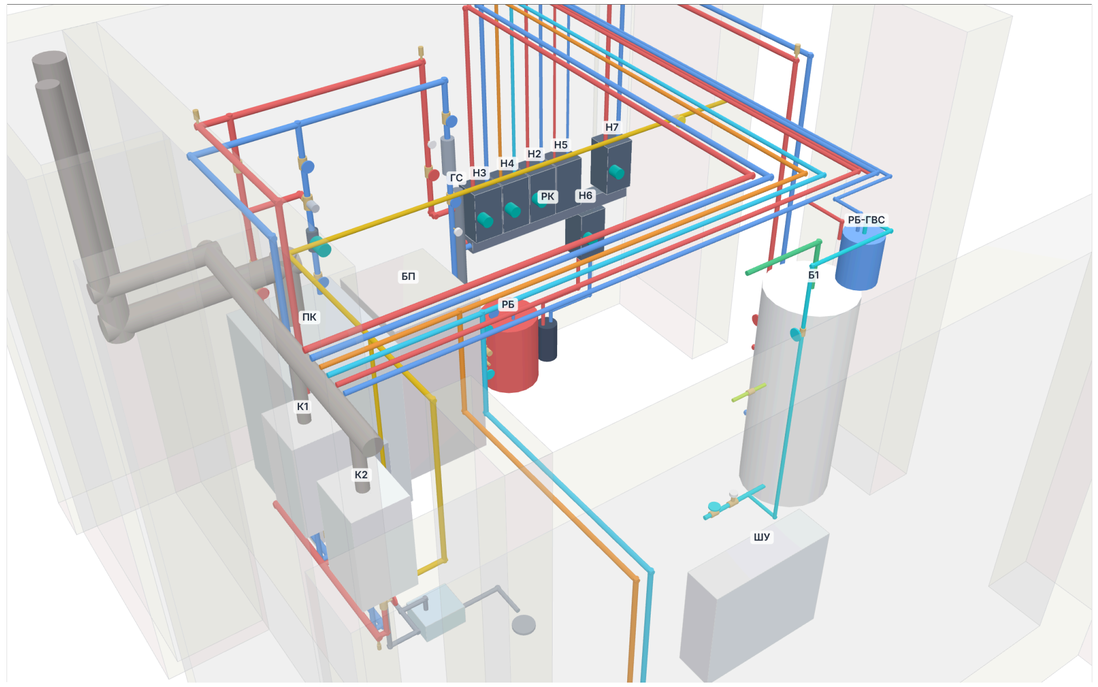

Котлы К1, К2 и пеллетный котел ПК: подключения, газ, дымоходы

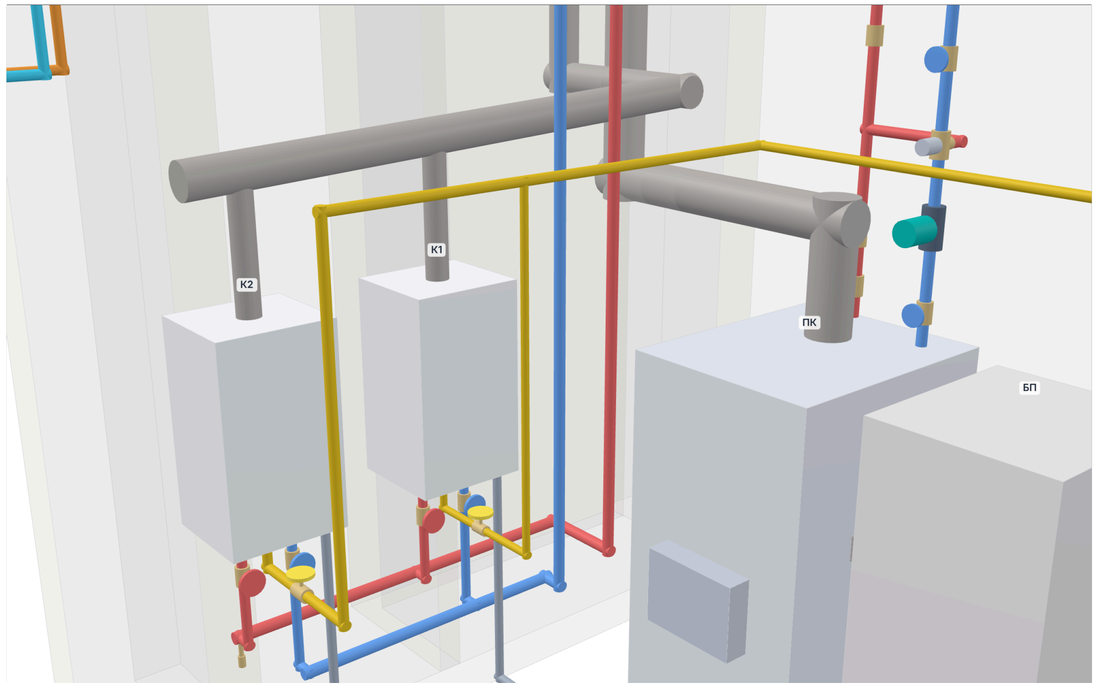

Гидрострелка ГС, коллектор РК и насосные группы Н2…Н7

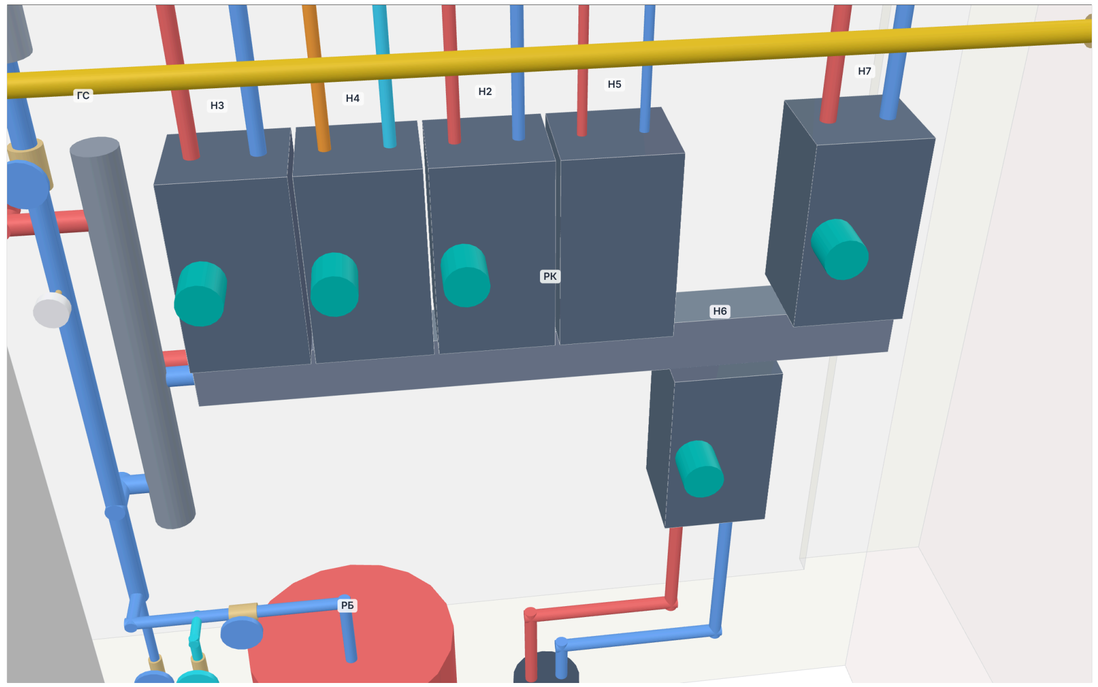

Снимки 3D-модели котельной (И05.09.26-ТМ 3D). Модель открывается в браузере (файл «просмотр в браузере»: вращение, виды, включение систем), в AutoCAD (DWG 3D) и в BIM-программах (IFC4). Марки — как на листах 2–5 и в ТМ.СО.

Изм.	Кол.уч	Лист	№ док	Подп.	Дата	И05.09.26-ТМ		
						Двухэтажный индивидуальный жилой дом с баней. Московская область, кадастровый номер участка 50:08:0050209:1600		
Разраб.						Тепломеханические решения котельной	Стадия	Лист	Листов
Пров.							Р	6	6
Н.контр.						Котельная. 3D-виды модели			
ГИП									

Согласовано

Взам.инв.№

Подпись и дата

Инв.№ подл.

Копировал

Формат А2