
План 1 этажа. Вентиляция и кондиционирование. Зоны подшивки потолков. М 1:100

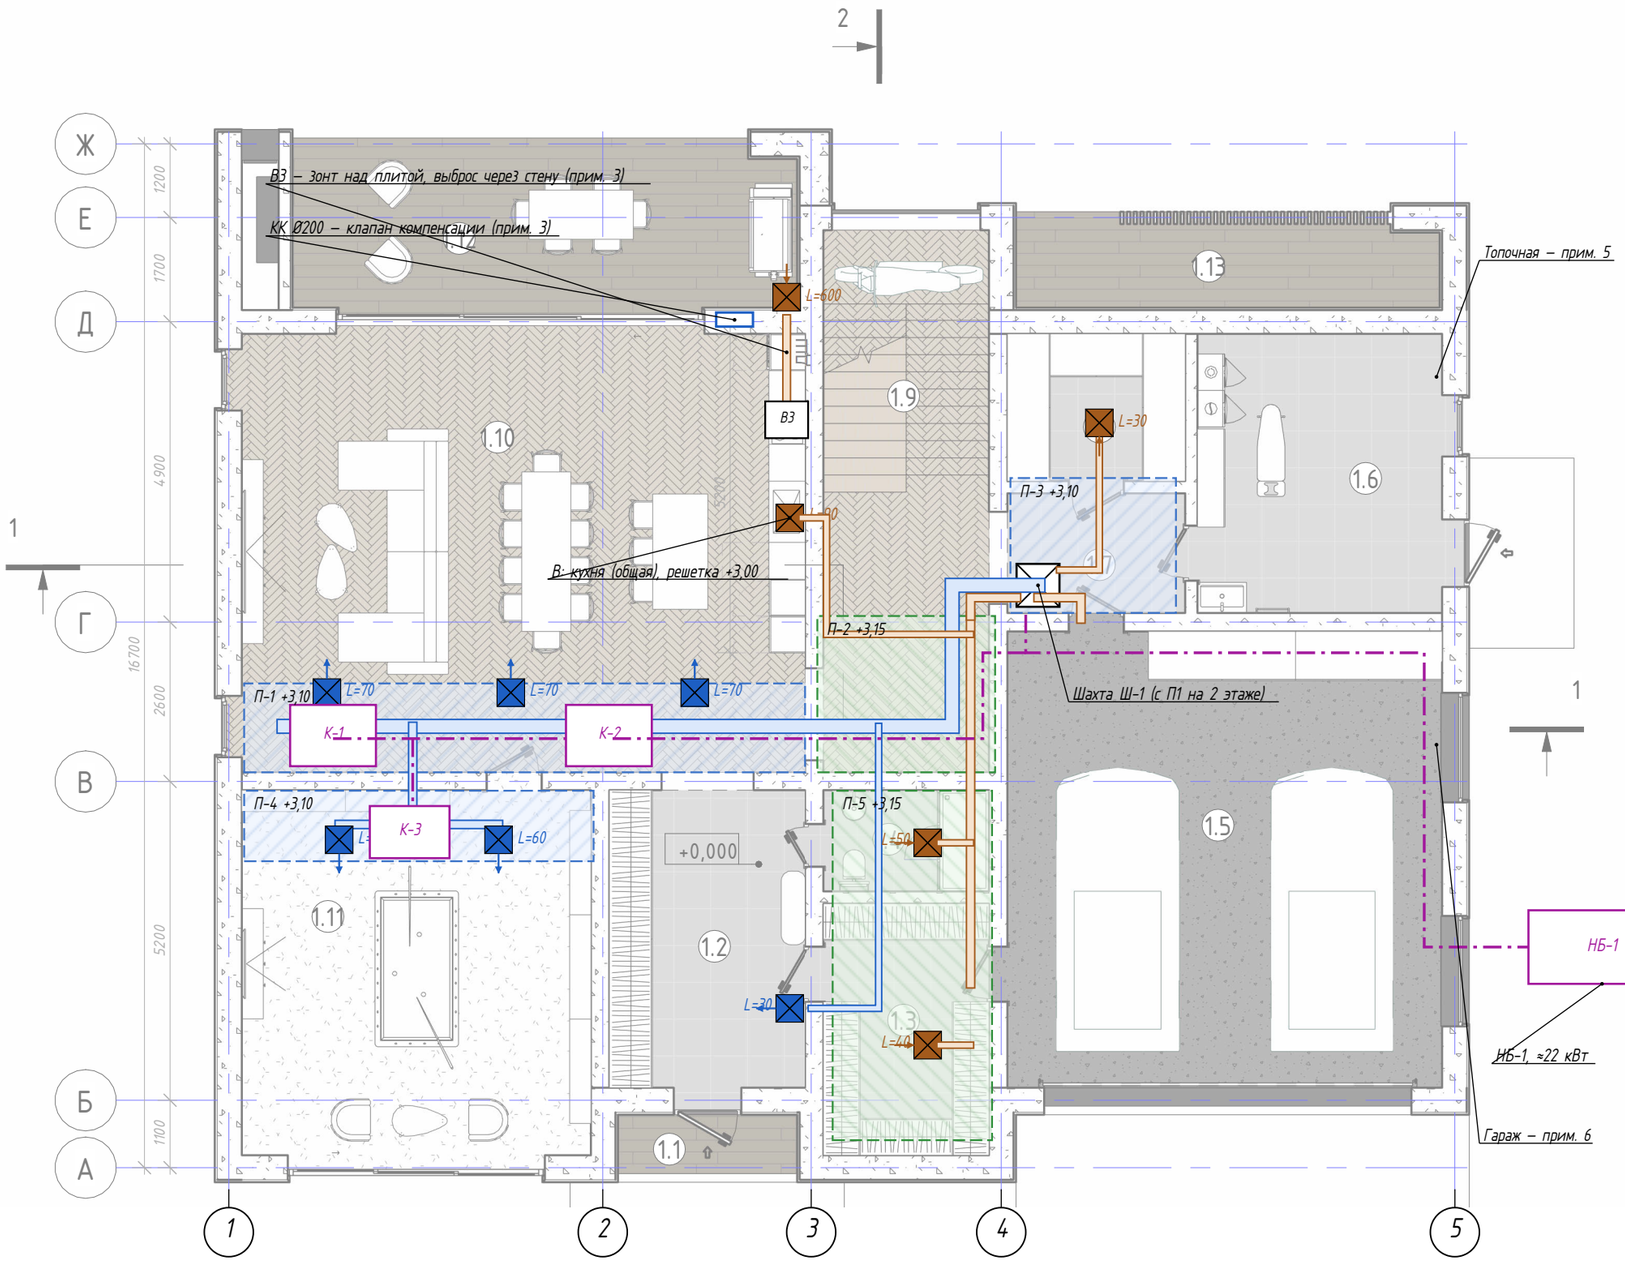

Условные обозначения

- Приточный воздуховод от П1 (Ø – на листе)
- Вытяжной воздуховод к П1
- Приточная решетка/диффузор, L – м³/ч
- Вытяжная решетка, L – м³/ч
- K — Внутренний канальный блок кондиционирования
- Фреонопроводы и дренаж
- Шахта воздуховодов и фреонопроводов
- Подшивка: зона с блоками/магистралями
- Подшивка: зона только воздуховодов

Зона	Что проходит	Глубина от низа плиты, мм	Низ подшивки
П-1	К-1, К-2 (гостиная), магистраль П Ø250, щелевые диффузоры на север	350	+3,10
П-2	магистраль П Ø250, В Ø160, фреон	300	+3,15
П-3	шахта Ш-1, магистрали П и В	350	+3,10
П-4	К-3 (бильярдная), П Ø160	350	+3,10
П-5	В от с/у и тамбура, П Ø125 в прихожую	300	+3,15

Примечания

1. Глубина подшивки – от низа плиты; отметки – при низе плиты +3,45 (уточнить по КР). Низ подшивки не ниже верха окон (+3,00).
2. Гостиная (второй свет): подача – из подшивки под галереей 2.2 щелевыми диффузорами в сторону остекления; вытяжка – из верхней зоны второго света (лист 4).
3. Кухня (ответ Заказчика): зонт ВЗ только над плитой, над островом вытяжки нет; 500–600 м³/ч, Ø150 в коробе над шкафами к стене по оси Д, выброс с обратным клапаном (место – с архитектором). Компенсация – КК Ø200 с электроприводом, сблокирован с зонтом; П1 – в режим усиленного притока.
4. Воздуховоды – оцинкованная сталь, с шумоглушителями; дренаж блоков – в канализацию через сифон (ВК).
5. Топочная 1.6: вытяжка 3 обмена в час (≈190 м³/ч) – отдельный канал в шахте Ш-2 выше кровли; приток – решетка в наружной стене с учетом воздуха на горение пеллетного котла; газовые котлы – с закрытой камерой, воздух – трубами через наружную стену.
6. Гараж 1.5: естественная вентиляция – приточная решетка внизу, вытяжная вверху противоположной стены.


Изм.	Кол.уч	Лист	№ док.	Подп.	Дата	ЭП-ОВ			
						Двухэтажный индивидуальный жилой дом с баней. Московская область, кадастровый номер участка 50:08:0050209:1600			
Разраб.						Отопление, вентиляция и кондиционирование. Принципиальные решения	Стадия	Лист	Листов
Пров.							ЭП	3	7
Н.контр.						План 1 этажа дома. Вентиляция и кондиционирование. Зоны подшивки			
Утв.									

Взам. инв. № | Подп. и дата | Инв. № подл.

Копировал

Формат А3

План 2 этажа. Вентиляция и кондиционирование. Зоны подшивки потолков. М 1:100

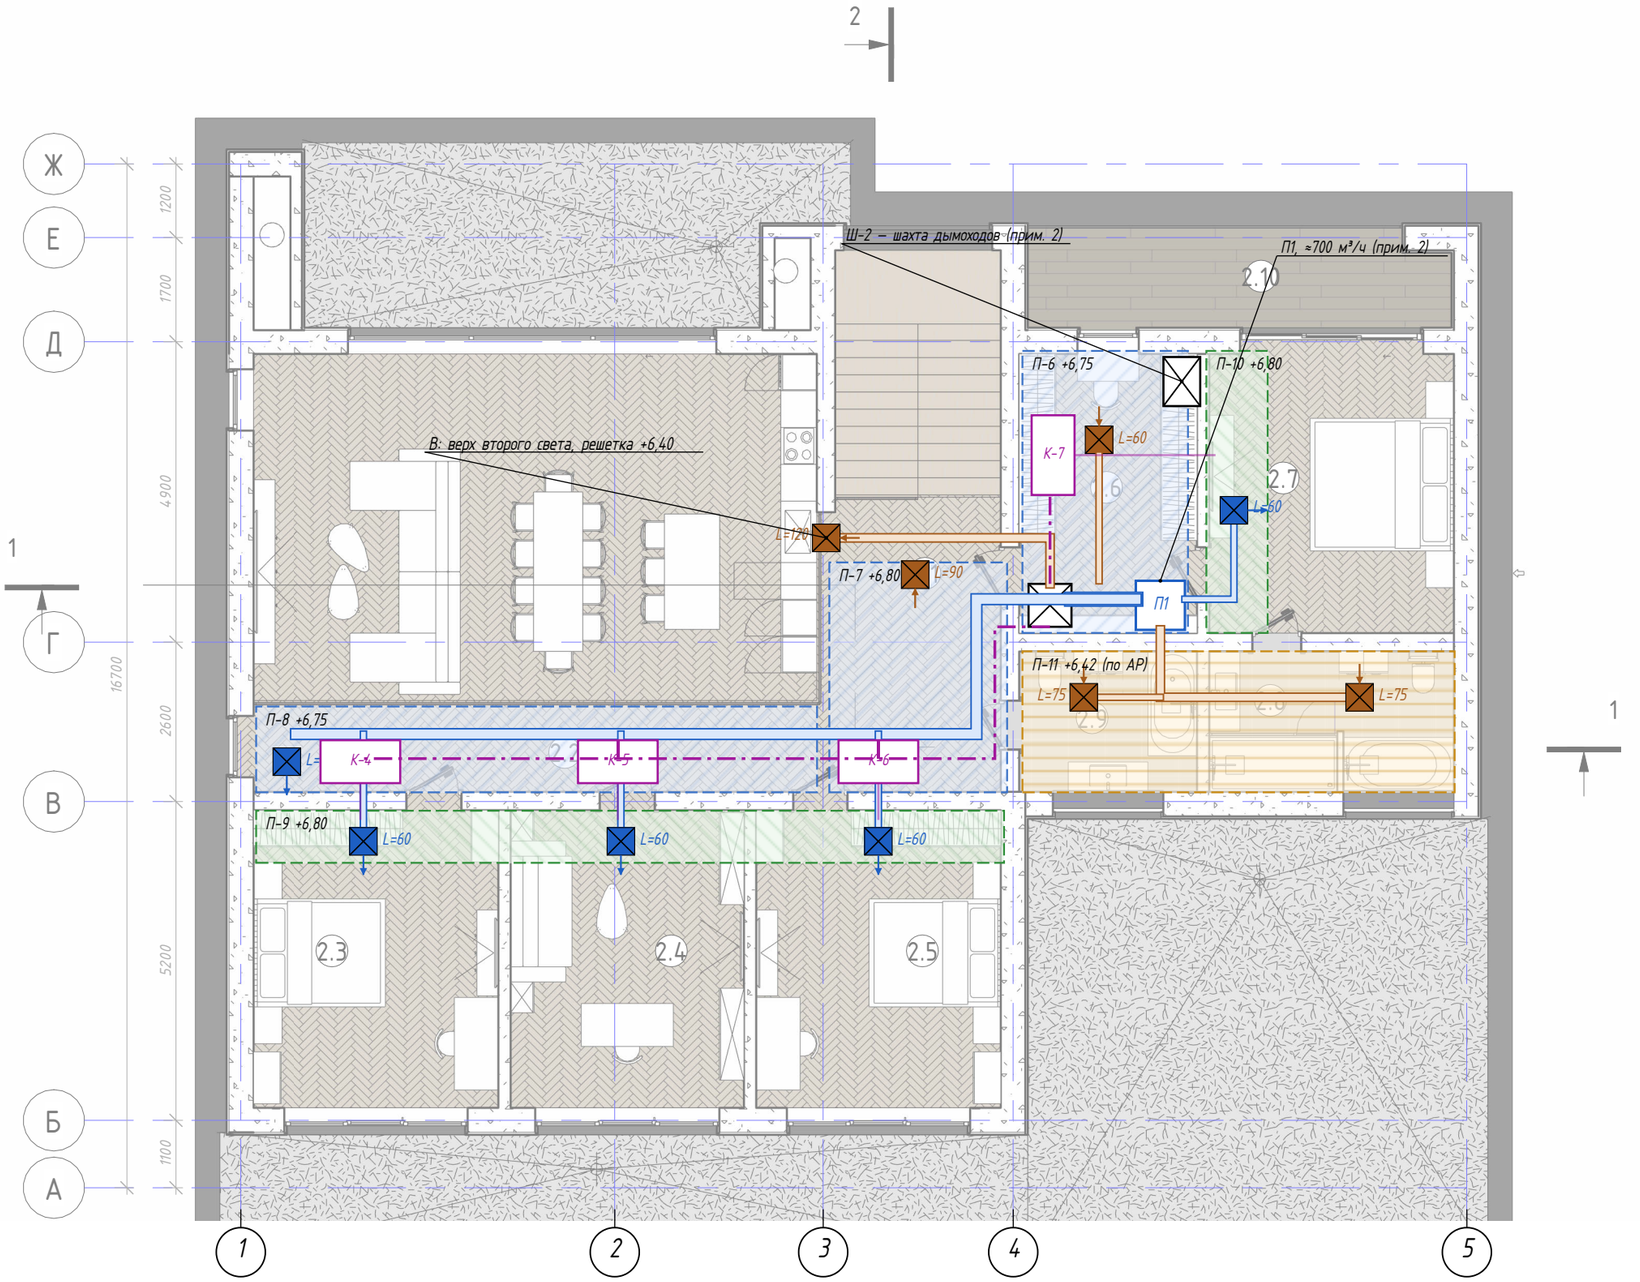

Условные обозначения

- П1 — Приточно-вытяжная установка П1 с рекуперацией
- Приточный воздуховод
- Вытяжной воздуховод
- Приточная решетка, L — м³/ч
- Вытяжная решетка, L — м³/ч
- K — Канальный блок кондиционирования
- Фреонопроводы и дренаж
- Подшивка: зона с блоками/магистралями
- Подшивка: зона диффузоров
- Подшивка санузлов — по АР

Зона	Что проходит	Глубина от низа плиты, мм	Низ подшивки
П-6	П1, шахта Ш-1, К-7, магистрали	400	+6,75
П-7	магистрали П Ø200, В Ø160, фреон	350	+6,80
П-8	К-4, К-5, магистраль П Ø200	400	+6,75
П-9	диффузоры и возврат кондиционеров спален	350	+6,80
П-10	диффузоры К-7 и приток спальни 2.7	350	+6,80
П-11	вытяжка с/у Ø125	–	+6,42 (по АР)

Примечания

1. Отметки — при низе плиты покрытия +7,15 (3,5 м от пола по опросному листу); уточнить по КР. Верх окон 2 этажа +6,65 — подшивка у окон не заходит.
2. П1 — в гардеробной 2.6 (выгородка ≈1,5×1,5 м с дверью для обслуживания) рядом с шахтой дымоходов Ш-2; воздухозабор — через фасад, выброс — через кровлю, оба — с разносом от оголовков дымоходов.
3. Канальные блоки спален — в подшивке галереи/холла; в спальни — подача и возврат через стену, обслуживание — из коридора.

Взам. инв. №

Подп. и дата

Инв. № подл.

Изм.	Кол.уч	Лист	№ док.	Подп.	Дата
Разраб.					
Пров.					
Н.контр.					
Утв.					

ЭП-ОВ

Двухэтажный индивидуальный жилой дом с баней. Московская область, кадастровый номер участка 50:08:0050209:1600

Отопление, вентиляция и кондиционирование. Принципиальные решения

Стадия	Лист	Листов
ЭП	4	7

План 2 этажа дома. Вентиляция и кондиционирование. Зоны подшивки

Копировал

Формат А3