
План 1 этажа на отм. ±0,000. М 1:100

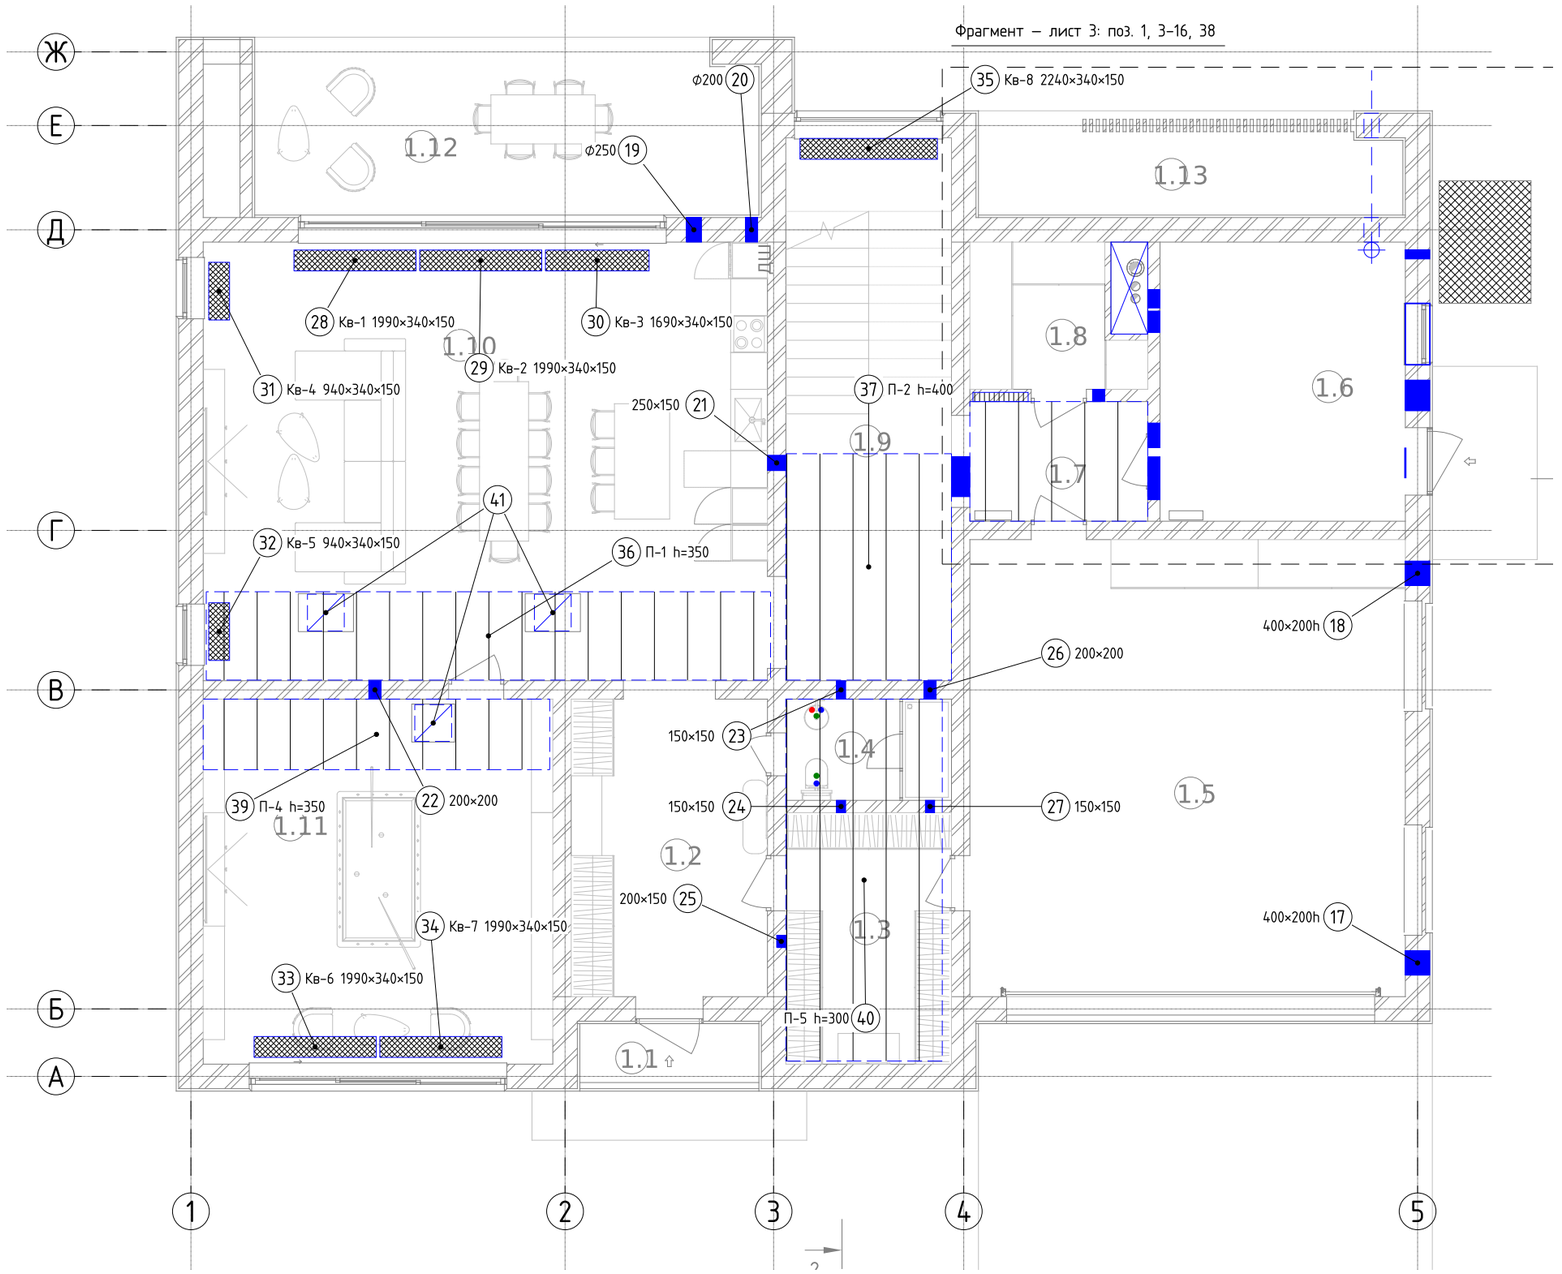

Условные обозначения

- отверстие в стене, перегородке, стенке шахты
- отверстие в перекрытии
- проход через покрытие (оголовок шахты)
- гильза в плите пола
- проход через фундамент (ниже пола)
- ниша под коллекторный шкаф
- приямок внутрипольного конвектора
- шахта (по АР)
- зона подшивки потолка
- люк 600×600 в подшивке
- зазор под дверью, решетка в двери
- площадка под наружный блок
- (N) позиция ведомости; рядом – размер, мм («h» – высота)

Примечания

1. Номер у отметки – позиция ведомости (листы 5–7): размеры, привязки, отметки, назначение.
2. Топочная 1.6, тамбур 1.7, ввод Ecoflex и площадка НБ-1 – фрагмент в М 1:50 на листе 3.
3. Отверстия в перекрытии над 1 этажом (Ш-1, стояки Т1, Т2) – на листе 2.

Согласовано

Взам.инв.№

Подпись и дата


Инв.№ подл.

Изм.	Кол.уч	Лист	№ док	Подп.	Дата	И05.09.26-ОВ.ТЗ-1			
						Двухэтажный индивидуальный жилой дом с баней. Московская область, кадастровый номер участка 50:08:0050209:1600			
Разраб.						Отопление, вентиляция и кондиционирование	Стадия	Лист	Листов
Пров.							Р	1	7
Н.контр.						Задание на устройство отверстий, шахт, ниш и приямков. План 1 этажа			
ГИП									

Копировал

Формат А3

План 2 этажа на отм. +4,050. М 1:100

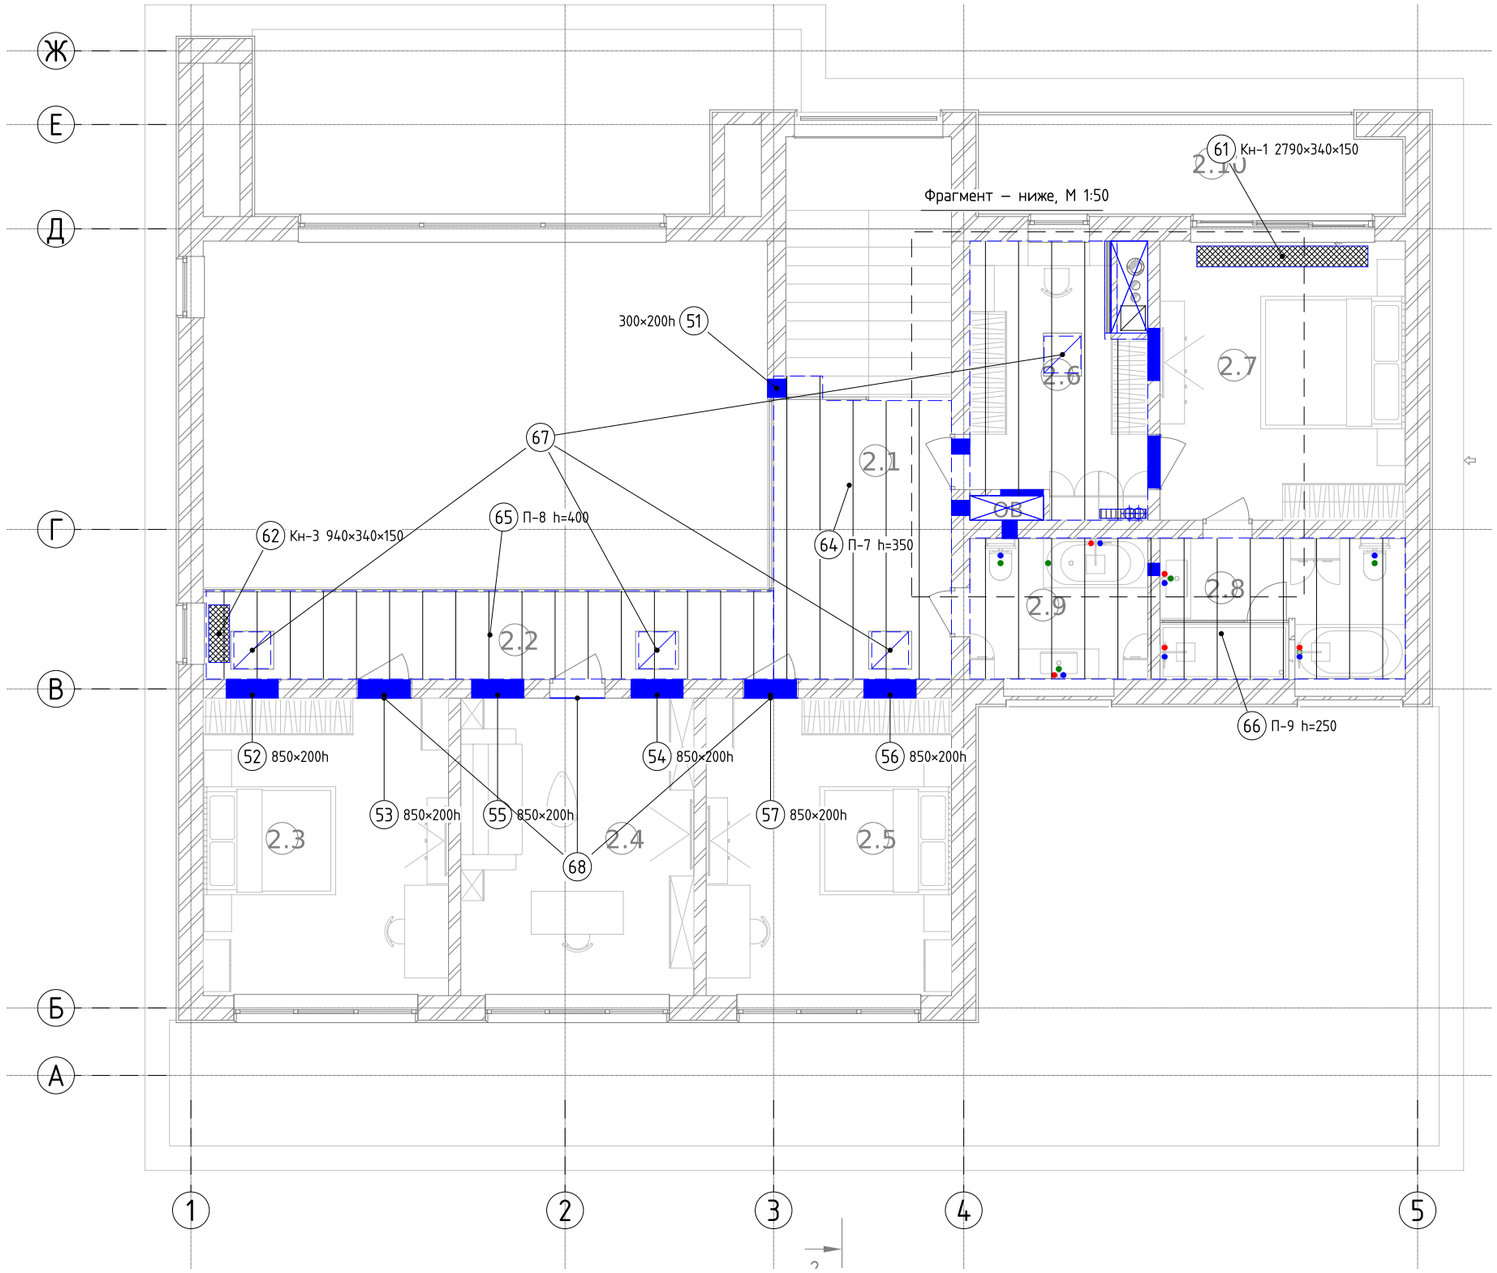

Условные обозначения

- гильза в перекрытии
- перенос стенки шахты: новое положение (штрих – по АР)
- отверстие в стене, перегородке, стенке шахты
- отверстие в перекрытии
- ниша под коллекторный шкаф
- приямок внутрипольного конвектора
- шахта (по АР)
- Зона подшивки потолка
- люк 600×600 в подшивке
- Зазор под дверью, решетка в двери
- (N) позиция ведомости; рядом – размер, мм («h» – высота)

Примечания

1. Номер у отметки – позиция ведомости (листы 5–7).
2. Отверстия в перекрытии над 1 этажом (Ш-1, стояки Т1, Т2, контур Ш-2) показаны на этом листе.
3. ЩП, ЩВ – узел 6 на листе 15; в спальнях подшивки нет.
4. Ш-2 на 2 этаже – 600×1500 в свету, как на 1 этаже: западную стенку перенести (поз. 45).

Фрагмент у шахты Ш-1. М 1:50

Изм.	Кол.уч	Лист	№ док	Подп.	Дата	И05.09.26-ОВ.ТЗ-1		
						Двухэтажный индивидуальный жилой дом с баней. Московская область, кадастровый номер участка 50:08:0050209:1600		
Разраб.						Отопление, вентиляция и кондиционирование	Стадия	Лист	Листов
Пров.							Р	2	7
Н.контр.						Задание на устройство отверстий, шахт, ниш и приямков. План 2 этажа			
ГИП									

Согласовано

Взам.инв.№


Подпись и дата

Инв.№ подл.


Копировал

Формат А3

Фрагмент плана 1 этажа: топочная 1.6, тамбур 1.7. М 1:50

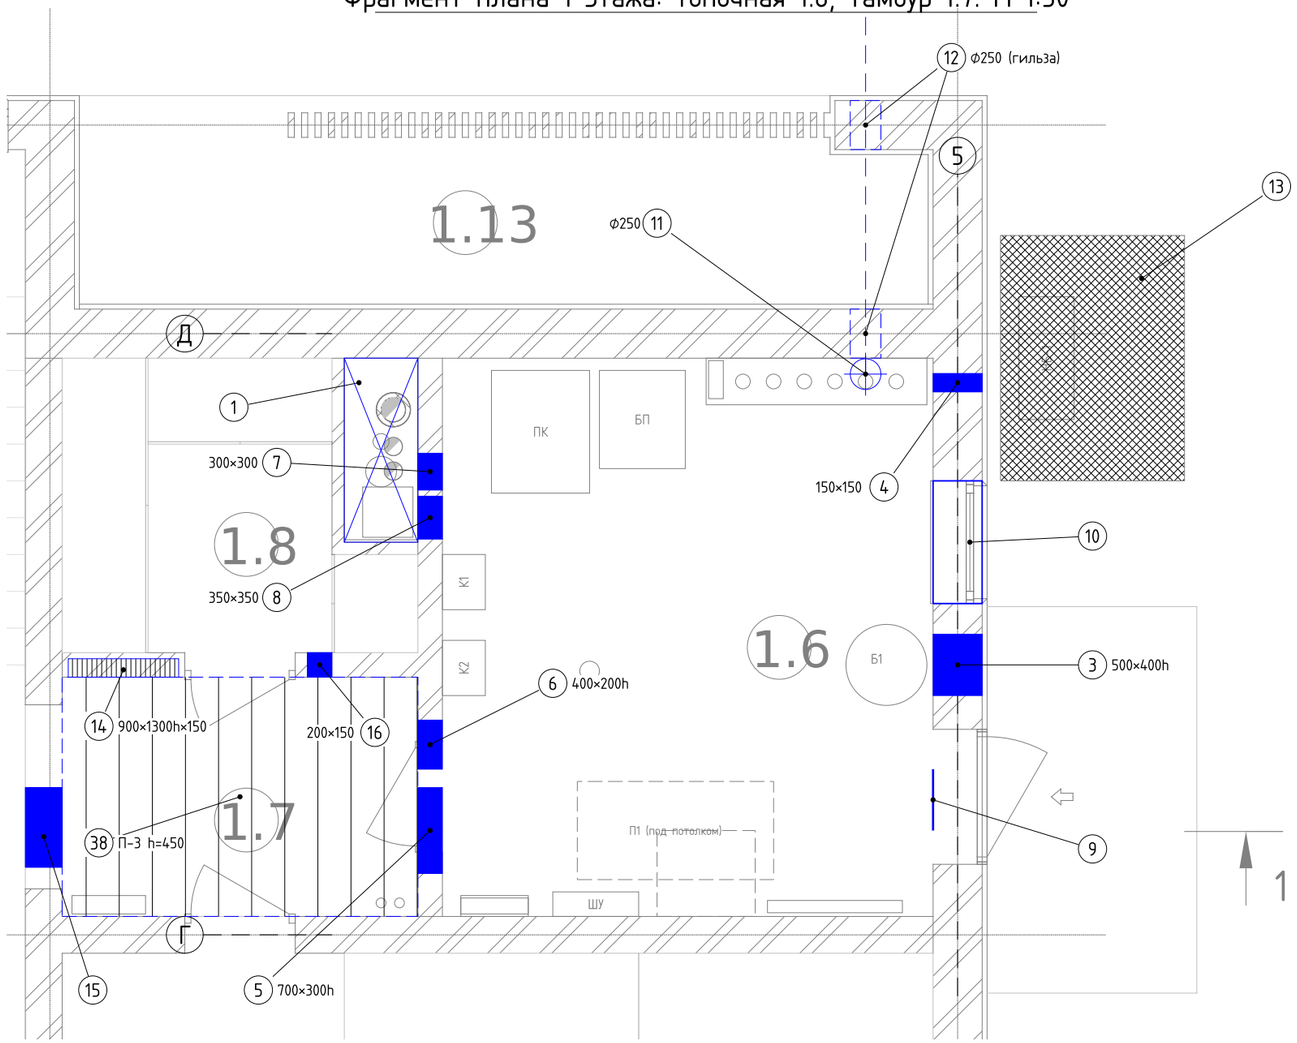

План кровли. М 1:200

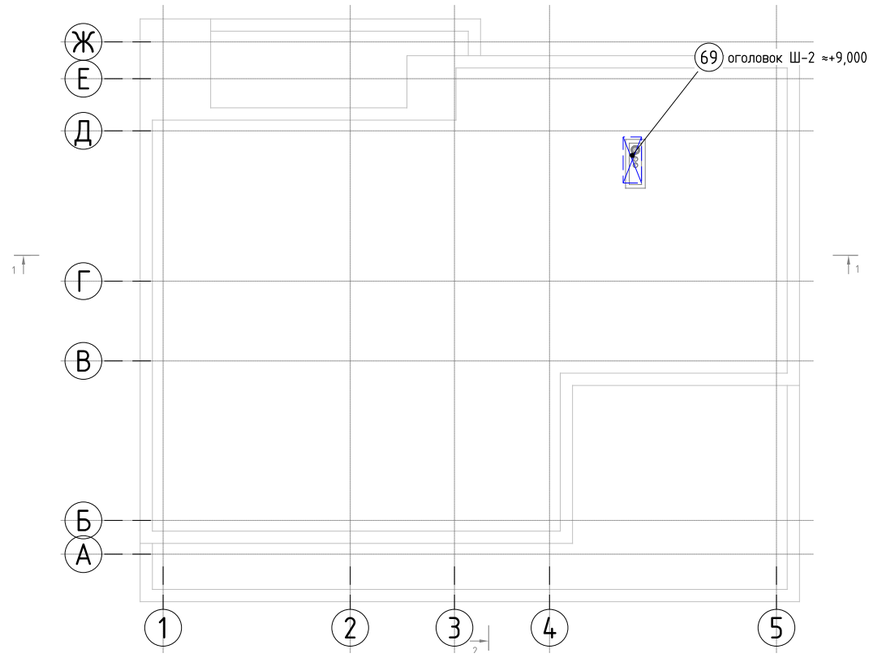

Примечания

1. Ш-2 – в свету 600×1500 по АР; каналы (с юга на север): выброс П1 Ф250 в канале 400×400, В2 Ф250, дымоход котлов Viessmann (каскад, лист 7) Ф125, пеллетный Ф200/280 – лист 7, узел 5 л. 15.
2. Стены 1.6/1.7 и 1.6/Ш-2: над дверью и под потолком – две группы отверстий на разных отметках (трубы +3,200, воздуховоды +3,400); перемычки – по КР.
3. Трасса Ecoflex – штрихпунктиром (лист 14); подъем в 1.6 – узел 2 л. 13.
4. Условные обозначения – на листе 1.

Согласовано

Взам.инв.№

Подпись и дата


Инв.№ подл.

Изм.	Кол.уч	Лист	№ док	Подп.	Дата	И05.09.26-ОВ.ТЗ-1			
						Двухэтажный индивидуальный жилой дом с баней. Московская область, кадастровый номер участка 50:08:0050209:1600			
Разраб.						Отопление, вентиляция и кондиционирование	Стадия	Лист	Листов
Пров.							Р	3	7
Н.контр.						Задание на устройство отверстий, шахт, ниш и приямков. Топочная 1.6. Кровля			
ГИП									

Копировал

Формат А3

Баня. План на отм. ±0,000. М 1:50

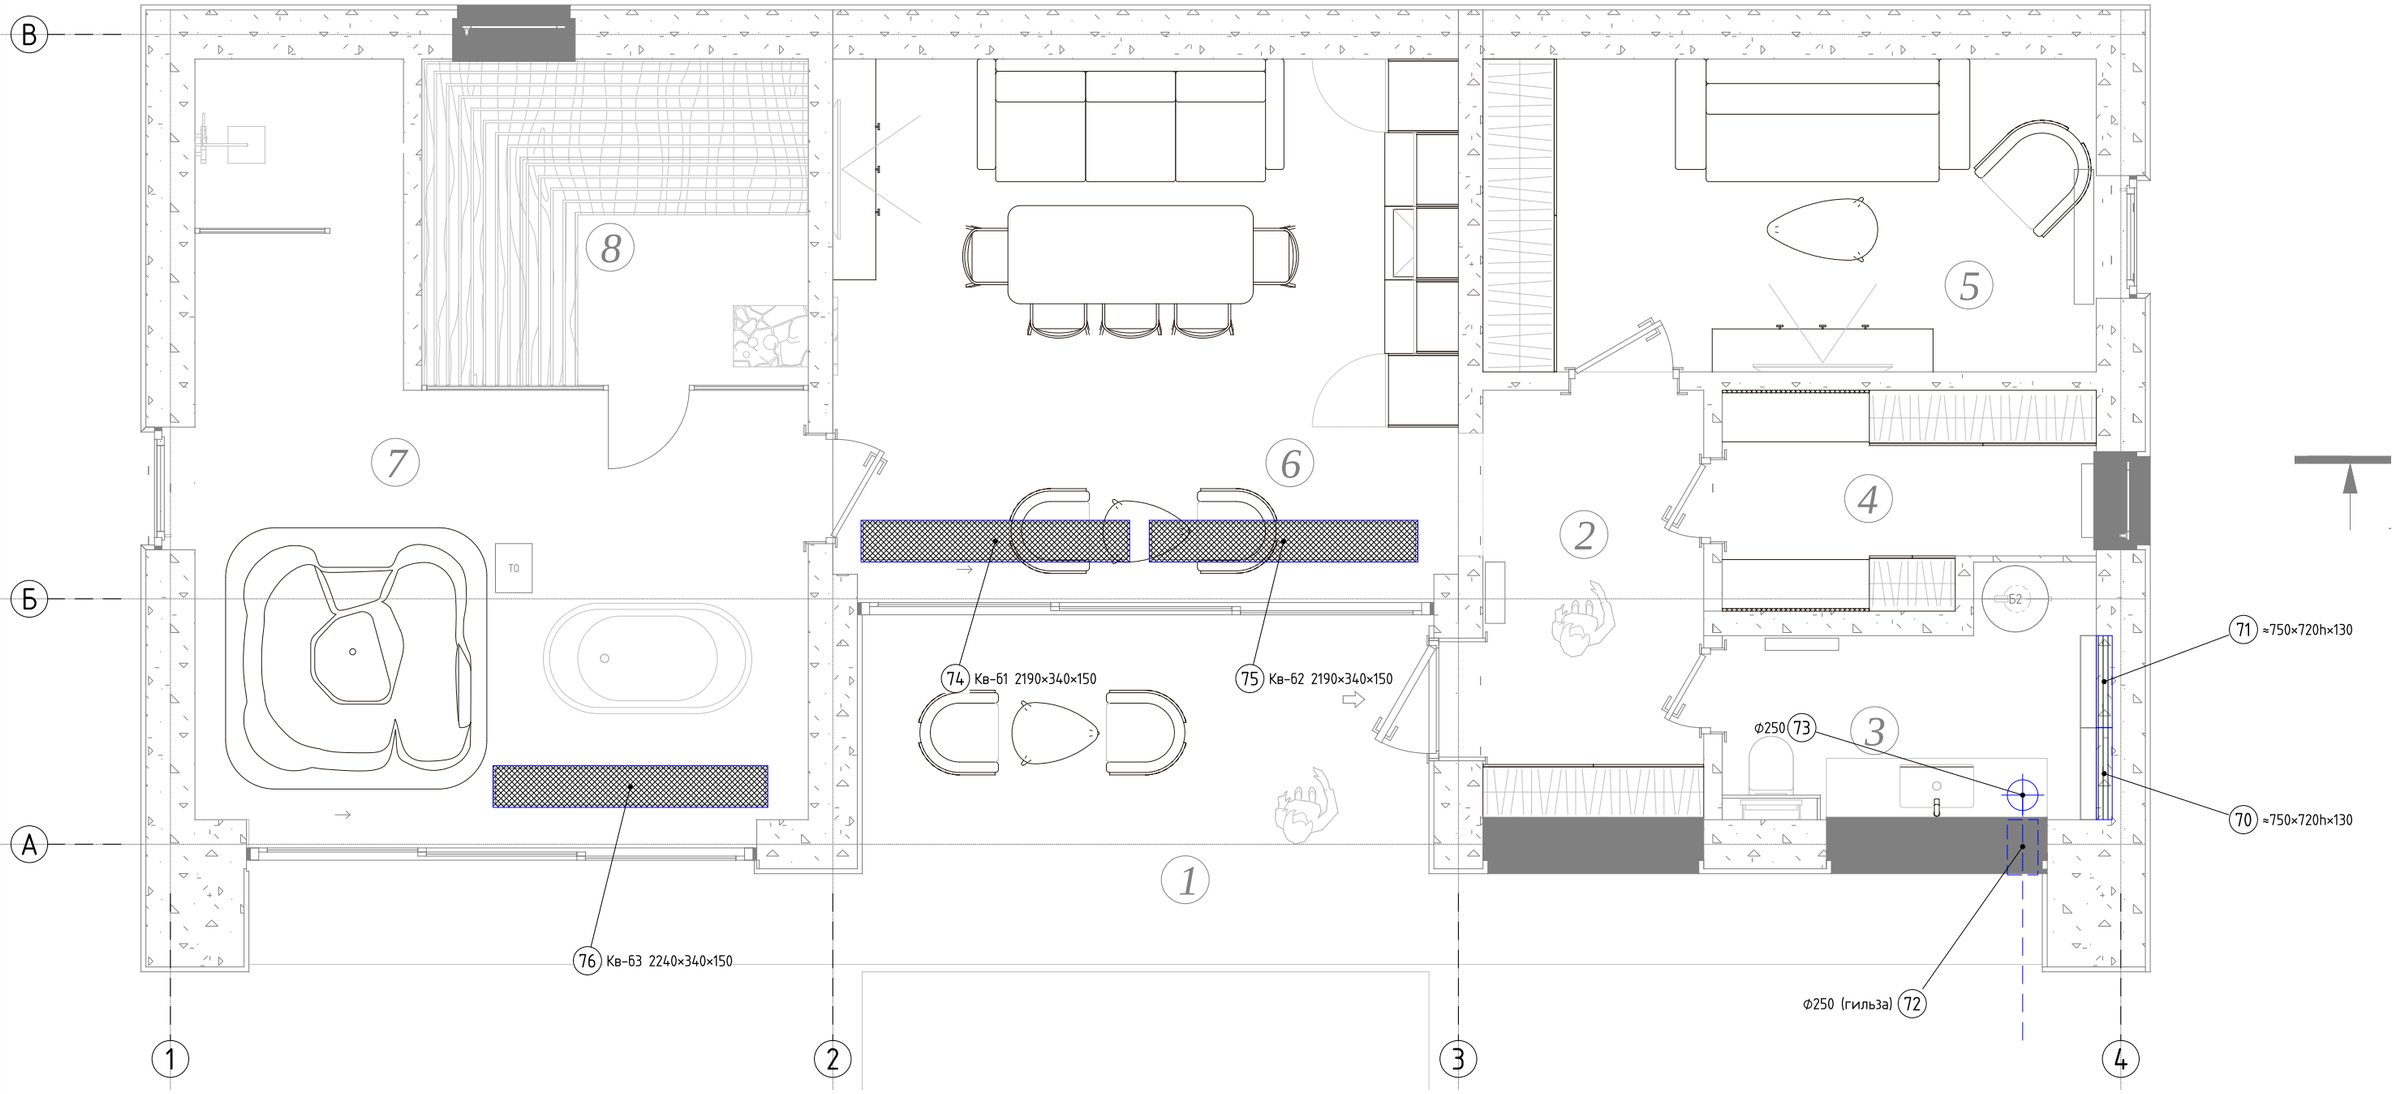

Примечания

1. Ниши КШ-Б1, КШ-Б2 – в восточной (наружной) стене с/у 63 под шкафы ШРВ-3, без прорезки утеплителя; подводки – снизу, из стяжки.
2. Ввод Ecoflex – при x≈15,10, западнее пилона АР (x 15,30–16,10): гильзы в фундаменте и в плите пола, узел 1 л. 13; место подъема уточнить по листу 12.
3. Условные обозначения – на листе 1.

Согласовано

Взам.инв.№

Подпись и дата

Инв.№ подл.

Изм.	Кол.уч	Лист	№ док	Подп.	Дата	И05.09.26-ОВ.ТЗ-1			
						Двухэтажный индивидуальный жилой дом с баней. Московская область, кадастровый номер участка 50:08:0050209:1600			
Разраб.						Отопление, вентиляция и кондиционирование	Стадия	Лист	Листов
Пров.							Р	4	7
Н.контр.						Задание на устройство отверстий, шахт, ниш и приямков. Баня			
ГИП									

Копировал

Формат А3

Ведомость отверстий, шахт, ниш и приямков

Поз.	Вид	Размер, мм	Привязка	Отметка, м	Назначение
Шахты					
1	шахта	600×1500 (в свету)	За Западной стеной 1.6: x 15,00–15,60 (2400 от оси 4), у 12,10–13,60 (200 от оси Д)	от ±0,000 до оголовка ≈+9,000	Ш-2 (по АР), каналы с юга на север: выброс П1 Ф250 в канале 400×400 (АР); В2 – вытяжка топочной Ф250; дымоход котлов Viessmann (каскад, лист 7) Ф125; дымоход пеллетного котла Ф200/280. Каналы раздельные, стенки негорючие, зазоры до дымоходов – по паспортам; оголовок – поз. «Кровля»
2	шахта	1200×400 (в свету)	гардеробная 2.6: x 12,70–13,90 (100 от оси 4), у 9,05–9,45 (150 от оси Г)	+3,850…+7,550 (2 этаж)	Ш-1 (по АР09): стояки П Ф200, В Ф200, П Ф100 (2.7) и фреонопроводы К-4…К-7 из подшивки П-3 1 этажа в подшивки 2 этажа; проходы – поз. перекрытия и стенок Ш-1
Топочная 1.6, тамбур 1.7, ввод Ecoflex, НБ-1 (фрагмент – лист 3)					
3	стена	500×400(h)	наружная стена по оси 5; край у=10,85 (1950 от оси Г)	низ +2,600	Н1 – воздухозабор П1: решетка с сеткой, воздуховод Ф250 в теплоизоляции
4	стена	150×150	наружная стена по оси 5; ось отв. у=13,40 (400 от оси Д)	центр +3,100	фреонопроводы НБ-1 (жидкость + газ) в изоляции и межблочный кабель; гильза с уклоном наружу
5	стена	700×300(h)	стена 1.6/1.7 над дверью; у 9,40–10,10 (край у=9,40 (500 от оси Г))	центр +3,400 (верх +3,550)	П Ф250 от П1 в 1.7 и В Ф250 из 1.7 к П1 (подшивка П-3)
6	стена	400×200(h)	стена 1.6/1.7 над дверью; у 10,25–10,65 (край у=10,25 (1350 от оси Г))	центр +3,200	три пары труб в изоляции от РК: к КШ-1 20×2,8, к КШ-2 32×4,4, к стоякам КШ-4 25×3,5 – одним пучком; в 1.7 – под потолком к шкафам и к стоякам (листы 3, 7)
7	стена	300×300	стена 1.6/Ш-2 (запад); ось отв. у=12,68 (1125 от оси Д)	центр +3,350	В2 – вытяжная решетка топочной 188 м³/ч в канал Ф250 Ш-2 (под потолком)
8	стена	350×350	стена 1.6/Ш-2 (запад); ось отв. у=12,30 (1500 от оси Д)	центр +3,400	выброс П1 Ф250 в теплоизоляции – в канал 400×400 Ш-2
9	дверь	решетка ≈500×250, ж. с. не менее 0,08 м²	наружная дверь 1.6 (ось 5)	низ решетки не выше +0,300	ПН – приток в топочную 282 м³/ч (вытяжка и воздух на горение); решетка нерегулируемая
10	окно (проверка)	остекление не менее 1,9 м²	окно 1.6 по оси 5: у 11,60–12,60	–	легкосбрасываемая конструкция топочной: не менее 0,03 м² остекления на 1 м³ (V≈63 м³) – проверить по АР и проекту ГСВ; при недостатке – увеличить окно
11	плита пола	Ф250	топочная: x 19,25 (750 от оси 5); у 13,47 (330 от оси Д)	–	подъем Ecoflex Quattro (Т1, Т2 бани и две трубы ВК) – гильза, узел 2 л. 13
12	фундамент	Ф250 (гильза)	x 19,25: под стеной 1.6/1.13 (ось Д) и через фундамент наружной стены 1.13 (у 15,30–15,70)	верх трубы – не менее 0,8 м от планировочной отметки (КР)	Ecoflex Quattro к бане (лист 14); гильза с уплотнением – комплект ввода производителя
13	площадка	≈1500×2000	снаружи у оси 5: x 20,35–21,85, у 12,60–14,60	верх – по генплану	площадка НБ-1 (Daikin мини-VRV 22,4 кВт) под опорную раму 0,3–0,5 м; гравийная подушка для талой воды (КР)
14	ниша	900×1300(h)×150	стена 1.7/1.8 (200), простенок у оси 4: x 12,75–13,65 (150 от оси 4)	низ ±0,000, верх +1,300	КШ-2 двухъярусный (Кв-1–Кв-8; смесительный узел ТП 36 °С). Стена 200: ниша со стороны 1.7, выступ шкафа или утолщение ГКЛ со стороны 1.8 – решение АР
15	стена	650×300(h)	стена по оси 4 над проходом 1.7/1.9; у 9,45–10,10 (край у=9,45 (550 от оси Г))	центр +3,400	П Ф250 в 1.9, 1.10 и В Ф160 от кухни, 1.3, 1.4 (подшивки П-2, П-3); не требуется, если проход открыт до перекрытия
16	стена	200×150	стена 1.7/1.8; ось отв. x=14,80 (2200 от оси 4)	центр +3,400	вытяжная решетка 1.8 (В Ф100, 30 м³/ч)
План 1 этажа (лист 1)					
17	стена	400×200(h)	наружная стена по оси 5; ось отв. у=1,85 (750 от оси Б)	низ +0,200	гараж 1.5 – естественный приток у ворот: решетка с сеткой
18	стена	400×200(h)	наружная стена по оси 5; ось отв. у=8,20 (700 от оси Г)	верх +3,450	гараж 1.5 – естественная вытяжка под перекрытием: решетка с сеткой
19	стена	Ф250	наружная стена по оси Д; ось отв. x=8,20 (1300 от оси 3)	центр – по интерьеру (≈+2,600)	КК – клапан компенсации Ф200 с электроприводом, сблокирован с зонтом В3
20	стена	Ф200	стена по оси Д, x≈9,14 (360 от оси 3) – место уточняется по АР	выше кровли террасы 1.12 – по АР	В3 – выброс кухонного зонта Ф150 (500–600 м³/ч) на фасад; обратный клапан и наружная решетка
21	стена	250×150	стена по оси 3 (1.10/1.9); ось отв. у=10,00 (1100 от оси Г)	центр +3,400	вытяжная решетка кухни 1.10 (В Ф125, 90 м³/ч)
22	стена	200×200	стена по оси В (1.10/1.11); ось отв. x=3,00 (3000 от оси 1)	центр +3,400	П Ф125 в 1.11 (подшивки П-1, П-4)
23	стена	150×150	стена по оси В; ось отв. x=10,60 (1100 от оси 3)	центр +3,400	П Ф100 в прихожую 1.2 (подшивка П-5)
24	стена	150×150	стена 1.4/1.3; ось отв. x=10,60 (1100 от оси 3)	центр +3,400	П Ф100 в 1.2
25	стена	200×150	стена 1.3/1.2 (у оси 3); ось отв. у=2,20 (1100 от оси Б)	центр +3,400	приточная решетка 1.2 (П Ф100, 30 м³/ч)
26	стена	200×200	стена по оси В; ось отв. x=12,05 (550 от оси 4)	центр +3,400	В Ф125 от 1.3, 1.4 к П1
27	стена	150×150	стена 1.4/1.3; ось отв. x=12,05 (550 от оси 4)	центр +3,400	В Ф100 от 1.3
28	приямок	1990×340×150	Зап. торец 1680 от оси 1; сев. край 330 от оси Д	верх ±0,000	Кв-1 – внутрипольный конвектор КЗТО L=1950, 1.10; в конструкции пола
29	приямок	1990×340×150	Зап. торец 3730 от оси 1; сев. край 330 от оси Д	верх ±0,000	Кв-2 – внутрипольный конвектор КЗТО L=1950, 1.10; в конструкции пола
30	приямок	1690×340×150	Зап. торец 5780 от оси 1; сев. край 330 от оси Д	верх ±0,000	Кв-3 – внутрипольный конвектор КЗТО L=1650, 1.10; в конструкции пола
31	приямок	940×340×150	юж. торец 3430 от оси Г; Зап. край 290 от оси 1	верх ±0,000	Кв-4 – внутрипольный конвектор КЗТО L=900, 1.10; в конструкции пола
32	приямок	940×340×150	юж. торец 480 от оси В; Зап. край 290 от оси 1	верх ±0,000	Кв-5 – внутрипольный конвектор КЗТО L=900, 1.10; в конструкции пола
33	приямок	1990×340×150	Зап. торец 1030 от оси 1; юж. край 310 от оси А	верх ±0,000	Кв-6 – внутрипольный конвектор КЗТО L=1950, 1.11; в конструкции пола

Согласовано

Взам.инв.№

Подпись и дата

Инв.№ подл.

Изм.	Кол.уч	Лист	№ док	Подп.	Дата
Разраб.					
Пров.					
Н.контр.					
ГИП					

И05.09.26-ОВ.ТЗ-1

Двухэтажный индивидуальный жилой дом с баней. Московская область, кадастровый номер участка 50:08:0050209:1600

Отопление, вентиляция и кондиционирование	Стадия	Лист	Листов
	Р	5	7

Задание на устройство отверстий, шахт, ниш и приямков. Ведомость

Копировал

Формат А3

Ведомость отверстий, шахт, ниш и приямков (продолжение)

Поз.	Вид	Размер, мм	Привязка	Отметка, м	Назначение
34	приямок	1990×340×150	Зап. торец 3080 от оси 1; юж. край 310 от оси А	верх ±0,000	Кв-7 — внутрипольный конвектор КЗТО L=1950, 1.11; в конструкции пола
35	приямок	2240×340×150	Зап. торец 430 от оси 3; сев. край 210 от оси Е	верх ±0,000	Кв-8 (вместо Кн-2 по ЭП, решение Заказчика 19.10.2026) — внутрипольный конвектор КЗТО L=2200, 1.9; в конструкции пола
36	подшивка	глубина 350	Зона по плану	низ +3,300	П-1: К-1, К-2, магистраль П Ф250…Ф125, фреон, дренаж; диффузоры в торце подшивки
37	подшивка	глубина 400	Зона по плану	низ +3,250	П-2: П Ф250, В Ф160/Ф125 с пересечением, фреон, дренаж
38	подшивка	глубина 450	Зона по плану	низ +3,200	П-3: магистрали П и В Ф250 от П1 с пересечениями, стояки в Ш-1, фреон
39	подшивка	глубина 350	Зона по плану	низ +3,300	П-4: К-3, П Ф125/Ф100, фреон, дренаж; диффузор К-3 в торце
40	подшивка	глубина 300	Зона по плану	низ +3,350	П-5: П Ф100 в прихожую 1.2, В Ф125/Ф100 от 1.3, 1.4
41	люки	600×600, 3 шт.	под блоками К-1, К-2 (1.10), К-3 (1.11)	в подшивке	люки обслуживания блоков К (снизу); к регуляторам расхода на ответвлениях — по месту монтажа
План 2 этажа, перекрытие на отм. +3,650 (лист 2)					
42	перекрытие	1200×400	в контуре Ш-1: x 12,70–13,90 (100 от оси 4), y 9,05–9,45 (150 от оси Г)	перекрытие +3,650…+3,850	стояки П Ф200, В Ф200, П Ф100 и фреонопроводы из подшивки П-3 в Ш-1; после монтажа — заделка негорючим
43	перекрытие	Ф60, 2 шт. (гильзы Ф40)	угол 1.7: x 15,30 и 15,45 (300 и 150 от грани стены 1.6), y 9,16 (110 от грани стены по оси Г)	перекрытие +3,650…+3,850	стояки Т1, Т2 25×3,5 к КШ-4; гильзы с выступом 30 мм над полом — узел 4 л. 15
44	перекрытие	600×1500	в контуре Ш-2 (поз. Ш-2)	перекрытие +3,650…+3,850	каналы Ш-2 без разрывов — если шахта не выделена в плите по АР
45	шахта	600×1500 в свету (в АР09 — 500)	Западная стенка Ш-2 на 2 этаже: перенести с x 15,00–15,10 на x 14,90–15,00 (как на 1 этаже), y 12,10–13,60	+4,050 до оголовка	Ш-2 — 600×1500 в свету на всю высоту: каналы выброса П1, В2 и дымоходы (поз. Ш-2) идут без смещений; стенка — негорючая (по АР09 сейчас стоит на x 15,00–15,10)
46	стена	250×250	стена Ш-1 по оси 4 (300); ось отв. y=9,25 (350 от оси Г)	центр +7,300	П Ф160 из Ш-1 в холл 2.1 (подшивка П-7)
47	стена	700×300(h)	северная стенка Ш-1; x 13,20–13,90 (600 от оси 4)	центр +7,300	В Ф200 от 2.6, 2.1; П Ф100 в 2.7; фреонопроводы К-4…К-7 (подшивка П-6)
48	стена	250×250	стена по оси Г (300); ось отв. x=13,35 (750 от оси 4)	центр +7,300	В Ф160 от 2.8, 2.9 в Ш-1 (подшивка П-9)
49	стена	200×200	стена 2.9/2.8; ось отв. y=8,25 (650 от оси Г)	центр +7,300	В Ф125 от 2.8 (подшивка П-9)
50	стена	250×250	стена по оси 4 над проемом 2.1/2.6; ось отв. y=10,25 (1350 от оси Г)	центр +7,300	В Ф160 от 2.1 к Ш-1; не требуется, если проем открыт до перекрытия
51	стена	300×200(h)	стена по оси 3 (2.1 / второй свет 1.10); ось отв. y=11,20 (2300 от оси Г)	низ +6,400	вытяжная решетка верха второго света 1.10 (В Ф160, 120 м³/ч)
52	стена	850×200(h)	стена по оси В (спальня 2.3); x 0,57–1,43 (575 от оси 1)	верх +7,500	ЩП 800×150 — подача К-4 и свежий воздух П1 (спальня 2.3, узел 6 л. 15)
53	стена	850×200(h)	стена по оси В (спальня 2.3); x 2,73–3,57 (2725 от оси 1), над дверью	верх +7,500	ЩВ 800×150 — возврат К-4 (спальня 2.3, узел 6 л. 15)
54	стена	850×200(h)	стена по оси В (спальня 2.4); x 7,17–8,03 (1075 от оси 2)	верх +7,500	ЩП 800×150 — подача К-5 и свежий воздух П1 (спальня 2.4, узел 6 л. 15)
55	стена	850×200(h)	стена по оси В (спальня 2.4); x 4,58–5,42 (1525 от оси 2)	верх +7,500	ЩВ 800×150 — возврат К-5 (спальня 2.4, узел 6 л. 15)
56	стена	850×200(h)	стена по оси В (спальня 2.5); x 10,97–11,83 (1475 от оси 3)	верх +7,500	ЩП 800×150 — подача К-6 и свежий воздух П1 (спальня 2.5, узел 6 л. 15)
57	стена	850×200(h)	стена по оси В (спальня 2.5); x 9,02–9,88 (475 от оси 3), над дверью	верх +7,500	ЩВ 800×150 — возврат К-6 (спальня 2.5, узел 6 л. 15)
58	стена	850×200(h)	стена 2.6/2.7; y 11,32–12,18 (2425 от оси Г)	верх +7,500	ЩП 800×150 — подача К-7 и свежий воздух П1 (спальня 2.7, узел 6 л. 15)
59	стена	850×200(h)	стена 2.6/2.7; y 9,57–10,43 (675 от оси Г), над дверью	верх +7,500	ЩВ 800×150 — возврат К-7 (спальня 2.7, узел 6 л. 15)
60	ниша	750×1250(h)×150	встроенный шкаф у стены по оси Г, 2.6: x 14,82–15,57 (2220 от оси 4)	низ +4,050, верх +5,300	КШ-4 двухъярусный: Р-1–Р-3, Р-5, Кн-1, Кн-3, Пс-1, Пс-2, резерв В6; ТП 2.8, 2.9; стояки снизу (поз. гильз)
61	приямок	2790×340×150	Зап. торец 3800 от оси 4; сев. край 280 от оси Д	верх +4,050	Кн-1 — внутрипольный конвектор КЗТО L=2750, 2.7; в конструкции пола
62	приямок	940×340×150	юж. торец 430 от оси В; зап. край 290 от оси 1	верх +4,050	Кн-3 — внутрипольный конвектор КЗТО L=900, 2.2; в конструкции пола
63	подшивка	глубина 400	Зона по плану	низ +7,150	П-6: К-7, стояки из Ш-1, П Ф160, В Ф200/Ф160, фреон, дренаж
64	подшивка	глубина 350	Зона по плану	низ +7,200	П-7: К-6, П Ф160, В Ф160, фреон, дренаж
65	подшивка	глубина 400	Зона по плану	низ +7,150	П-8: К-4, К-5, П Ф160…Ф100, возврат К, фреон, дренаж
66	подшивка	глубина 250	Зона по плану	низ по АР	П-9: В Ф160/Ф125 санузлов (низ подшивки — по АР, не ниже глубины 250)
67	люки	600×600, 4 шт.	под блоками К-4, К-5, К-6 (2.2), К-7 (2.6)	в подшивке	люки обслуживания блоков К; к регуляторам расхода — по месту монтажа
68	дверь	зазор 15–20 мм	двери спален 2.3, 2.4, 2.5 (стена по оси В) и 2.7 (из 2.6)	под полотном	перетекание воздуха из спален к вытяжке (в спальнях вытяжки нет, лист 10)
Кровля (лист 3)					

Согласовано

Взам.инв.№

Подпись и дата

Инв.№ подл.

Изм.	Кол.уч	Лист	№ док	Подп.	Дата	И05.09.26-ОВ.ТЗ-1		
						Двухэтажный индивидуальный жилой дом с баней. Московская область, кадастровый номер участка 50:08:0050209:1600		
Разраб.						Отопление, вентиляция и кондиционирование	Стадия	Лист	Листов
Пров.							Р	6	7
Н.контр.						Задание на устройство отверстий, шахт, ниш и приямков. Ведомость			
ГИП									

Копировал

Формат А3

Ведомость отверстий, шахт, ниш и приямков (продолжение)

Поз.	Вид	Размер, мм	Привязка	Отметка, м	Назначение
69	покрытие	600×1500 + стенки шахты	в контуре Ш-2 (поз. Ш-2)	оголовок ≈+9,000 (кровля ≈+8,40)	оголовок Ш-2: каналы раздельные; высота дымоходов над кровлей — по паспортам и СП 7.13130 (с учетом конька); выброс П1 и В2 — с зонтами
Баня (лист 4)					
70	ниша	≈750×720(h)×130	восточная стена с/у Б3 (ось 4): у 0,20–0,95 (200 от оси А)	низ ±0,000, верх +0,720	КШ-Б1 — прямой коллектор: ШРВ-3; утеплитель наружной стены не прорезать (иначе — короб ГКЛ с выступом)
71	ниша	≈750×720(h)×130	восточная стена с/у Б3 (ось 4): у 0,95–1,70 (950 от оси А)	низ ±0,000, верх +0,720	КШ-Б2 — коллектор ТП со смесительным узлом (при нехватке высоты — шкаф увеличенной высоты, лист 12): ШРВ-3; утеплитель наружной стены не прорезать (иначе — короб ГКЛ с выступом)
72	фундамент	Ф250 (гильза)	южная стена с/у Б3 под окном, x=15,10 (800 от оси 4), западнее пилона АР (x 15,30–16,10)	верх трубы — не менее 0,8 м от планировочной отметки (КР)	ввод Ecoflex Quattro в баню (лист 14); гильза с уплотнением — комплект производителя
73	плита пола	Ф250	с/у Б3: x=15,10 (800 от оси 4); y=0,40 (400 от оси А) — уточнить по листу 12	—	подъем Ecoflex к КШ-Б1 — гильза, узел 1 л. 13
74	приямок	2190×340×150	Зап. торец 230 от оси 2; юж. край 300 от оси Б	верх ±0,000 бани	Кв-Б1 — внутрипольный конвектор КЗТО L=2150, Б6; в конструкции пола
75	приямок	2190×340×150	Зап. торец 2580 от оси 2; юж. край 300 от оси Б	верх ±0,000 бани	Кв-Б2 — внутрипольный конвектор КЗТО L=2150, Б6; в конструкции пола
76	приямок	2240×340×150	Зап. торец 2630 от оси 1; юж. край 300 от оси А	верх ±0,000 бани	Кв-Б3 — внутрипольный конвектор КЗТО L=2200, Б7; в конструкции пола

Примечания

1. Задание разделам АР и КР на отверстия, шахты, ниши, приямки и подшивки для систем отопления, вентиляции и кондиционирования по И05.09.26-ОВ (листы 3–15). Размеры — в мм, «h» — высота отверстия; отметки — в м от чистого пола 1 этажа ±0,000 (баня — от своего ±0,000); привязки — к осям, x и y — в м от пересечения осей 1/А, как на листах ОВ. Подложки — АР03, АР09, АР14, план бани (Revit, 19.10.2026).
2. Отверстия в несущих стенах, перекрытиях и фундаментах — по решению КР (перемычки, обрамления, усиление). Размеры даны с запасом на изоляцию и заделку.
3. Проходы через стены и перекрытия — в гильзах и обрамлениях; зазоры заделываются негорючими материалами с пределом огнестойкости не ниже, чем у пересекаемой конструкции (узел 4 л. 15). Стенки Ш-2 и проходы в них — негорючие.
4. Отверстия до Ф50 (фреонопроводы и дренаж в перегородках, подводки) выполняются по месту при монтаже и в задании не показаны, кроме проходов в стенках Ш-1 и наружных стенах.
5. Подшивки (поз. 36–40, 63–66): глубины и низ — по таблицам листов 9, 10, низ — не ниже верха окон; люки 600×600 — под каждым блоком К и у регуляторов расхода на ответвлениях (по месту монтажа).
6. Приямки конвекторов: длина и ширина — по корпусу выбранной серии КЗТО плюс 20 мм на сторону (принята ширина корпуса 300), глубина — не более 150 мм от чистого пола; плита не затрагивается (узел 2 л. 15). Размеры уточняются после подбора серии.
7. Ниши шкафов (поз. 14, 60, 70, 71) — по ориентировочным размерам шкафов, уточнить по каталогу производителя коллекторов. КШ-1 (1.7) и КШ-3 (1.6) — накладные, ниш не требуют.
8. Ecoflex (поз. 11, 12, 72, 73): гильзы, уплотнения и концевые манжеты — комплект производителя под наружный диаметр кожуха Ecoflex Quattro (175 или 200 мм — по каталогу); глубина до верха трубы не менее 0,8 м; отметки фундаментов — по КР (узлы 1, 2 л. 13).
9. Шахта Ш-2 (поз. 1, 44, 45, 69) — 600×1500 в свету на всю высоту; зазоры от дымоходов до конструкций — по паспортам; ревизии и сбор конденсата — в топочной (лист 7). Ввод газа, сигнализатор загазованности — по проекту ГСВ (ТЗ-4).
10. Двери спален 2.3, 2.4, 2.5, 2.7 — с зазором 15–20 мм под полотном (поз. 68) или с переточными решетками; наружная дверь топочной — с решеткой ПН (поз. 9).
11. Баня: при установке рекомендуемых вытяжных вентиляторов (лист 12) — отверстия Ф125 (помывочная 67) и Ф100 (с/у Б3) в наружной стене под потолком, место — по АР.

Согласовано

Взам.инв.№

Подпись и дата

Инв.№ подл.

Изм.	Кол.уч	Лист	№ док	Подп.	Дата	И05.09.26-ОВ.ТЗ-1			
						Двухэтажный индивидуальный жилой дом с баней. Московская область, кадастровый номер участка 50:08:0050209:1600			
Разраб.						Отопление, вентиляция и кондиционирование	Стадия	Лист	Листов
Пров.							Р	7	7
Н.контр.						Задание на устройство отверстий, шахт, ниш и приямков. Ведомость (окончание). Примечания			
ГИП									

Копировал

Формат А3