
План 1 этажа. Вентиляция и кондиционирование. Зоны подшивки потолков. М 1:100

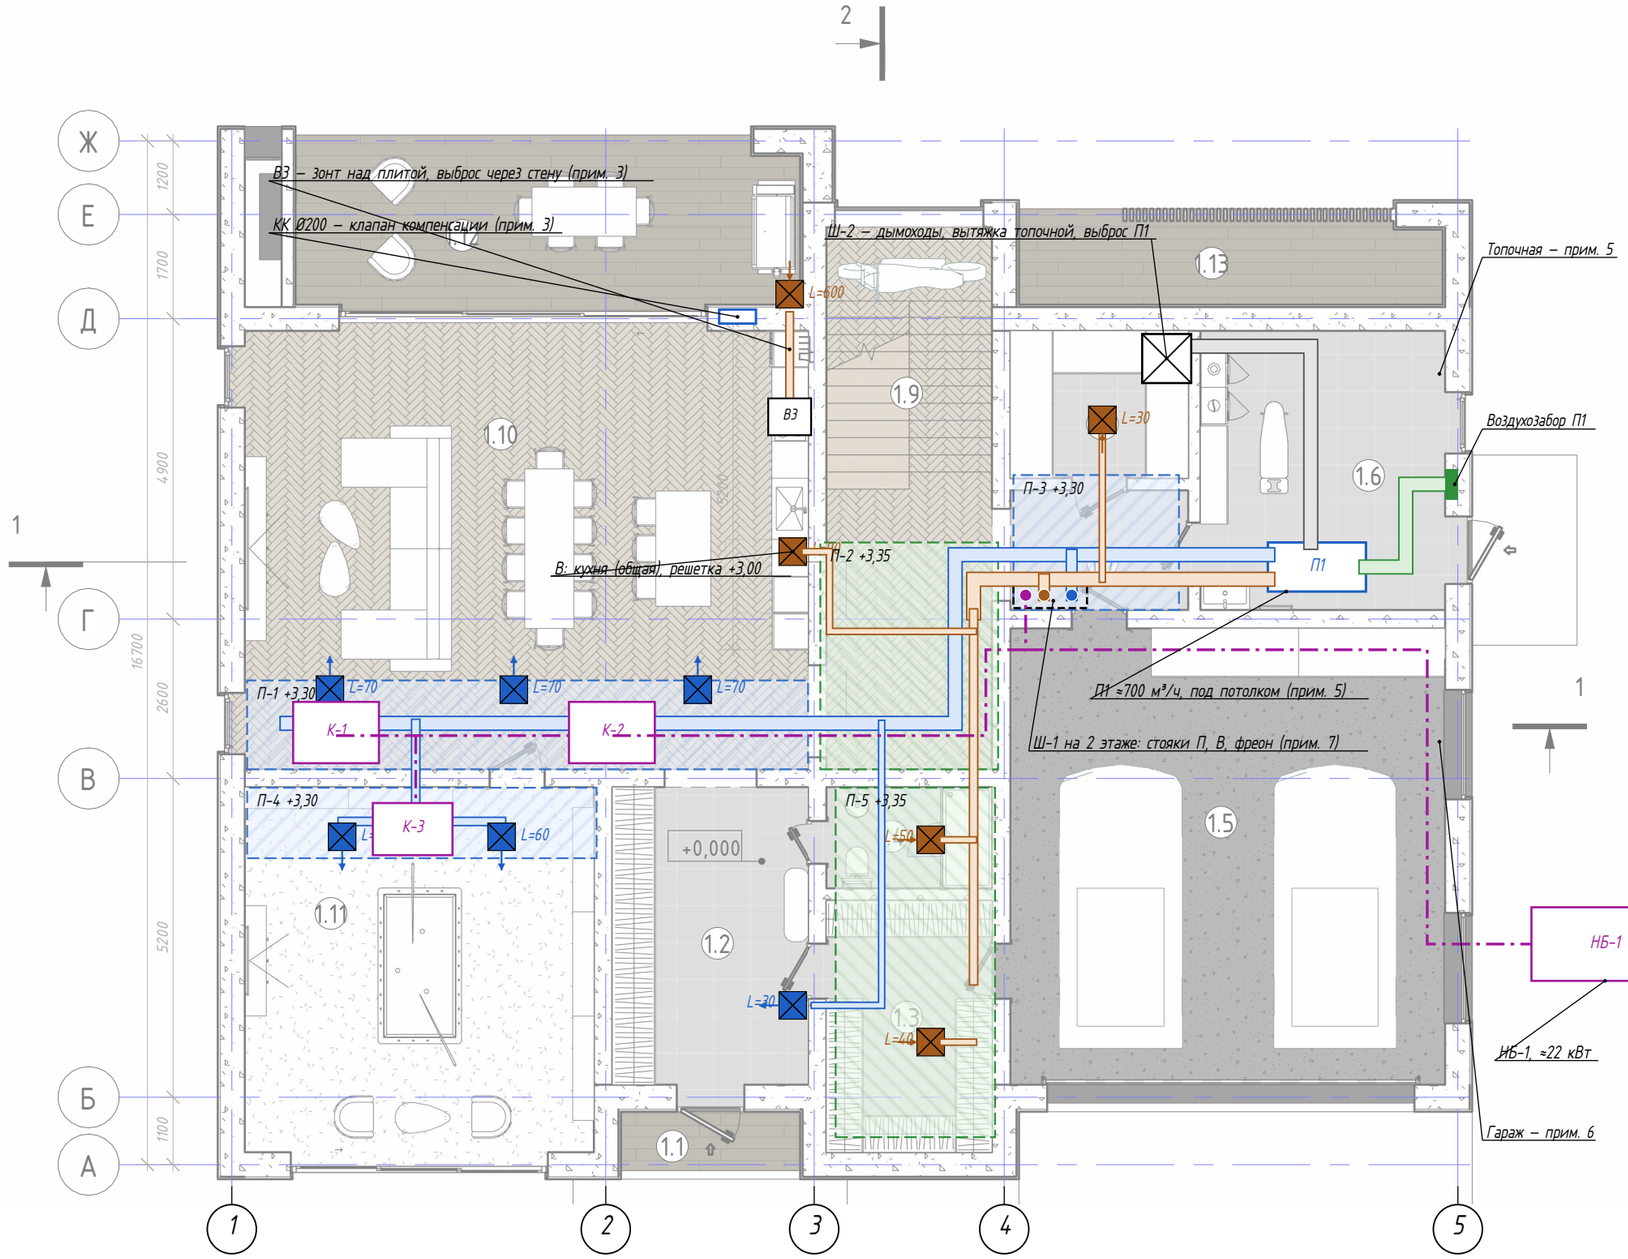

Условные обозначения

- П1 — Приточно-вытяжная установка П1 с рекуперацией
- Приточный воздуховод от П1 (Ø – на листе)
- Вытяжной воздуховод к П1
- Наружный воздух к П1
- Выброс от П1 в шахту Ш-2
- Стояки П и В на 2 этаж (шахта Ш-1)
- Приточная решетка/диффузор, L – м³/ч
- Вытяжная решетка, L – м³/ч
- K — Внутренний канальный блок кондиционирования
- Фреонопроводы и дренаж
- Шахта (Ш-1 – на 2 этаже, пунктиром)
- Подшивка: зона с блоками/магистралями
- Подшивка: зона только воздуховодов

Зона	Что проходит	Глубина от низа плиты, мм	Низ подшивки
П-1	K-1, K-2 (гостиная), магистраль П Ø250, щелевые диффузоры на север	350	+3,30
П-2	магистраль П Ø250, В Ø160, фреон	300	+3,35
П-3	магистрали П, В от П1, стояки в Ш-1	350	+3,30
П-4	K-3 (бильярдная), П Ø160	350	+3,30
П-5	В от с/у и тамбура, П Ø125 в прихожую	300	+3,35

Примечания

1. Глубина подшивки – от низа плиты; отметки – при низе плиты ≈+3,65 (разрезы АР15, АР16; уточнить по КР). Низ подшивки не ниже верха окон (≈+3,00).
2. Гостиная (второй свет): подача – из подшивки под галереей 2.2 щелевыми диффузорами в сторону остекления; вытяжка – из верхней зоны второго света (лист 4).
3. Кухня (ответ Заказчика): зонт ВЗ только над плитой, над островом вытяжки нет; 500–600 м³/ч, Ø150 в коробе над шкафами к стене по оси Д, выброс с обратным клапаном (место – с архитектором). Компенсация – КК Ø200 с электроприводом, сблокирован с зонтом; П1 – в режим усиленного притока.
4. Воздуховоды – оцинкованная сталь, с шумоглушителями; дренаж блоков – в канализацию через сифон (ВК).
5. Топочная 1.6 (решение Заказчика): П1 – под потолком у южной стены, обслуживание с пола; воздухозабор – решетка в восточной стене между дверью и окном (место – с архитектором), выброс – отдельным каналом в шахте Ш-2 выше кровли. Вытяжка топочной – 3 обмена (≈190 м³/ч) отдельным каналом в Ш-2; приток – решетка в наружной стене с учетом воздуха на горение всех котлов; дымоходы – в шахте, на фасад не выводятся.
6. Гараж 1.5: естественная вентиляция – приточная решетка внизу, вытяжная вверху противоположной стены.
7. На 2 этаж воздуховоды и фреонопроводы поднимаются через шахту Ш-1 у южной стены гардеробной 2.6 (зона, указанная Заказчиком; лист 4); на 1 этаже – в подшивке П-3 тамбура 1.7.

Взам. инв. №

Подп. и дата

Инв. № подл.

Изм.	Кол.уч	Лист	№ док.	Подп.	Дата
Разраб.					
Пров.					
Н.контр.					
Утв.					

ЭП-ОВ

Двухэтажный индивидуальный жилой дом с баней. Московская область, кадастровый номер участка 50:08:0050209:1600

Отопление, вентиляция и кондиционирование. Принципиальные решения


Стадия	Лист	Листов
ЭП	3	7

План 1 этажа дома. Вентиляция и кондиционирование. Зоны подшивки

Копировал

Формат А3

План 2 этажа. Вентиляция и кондиционирование. Зоны подшивки потолков. М 1:100

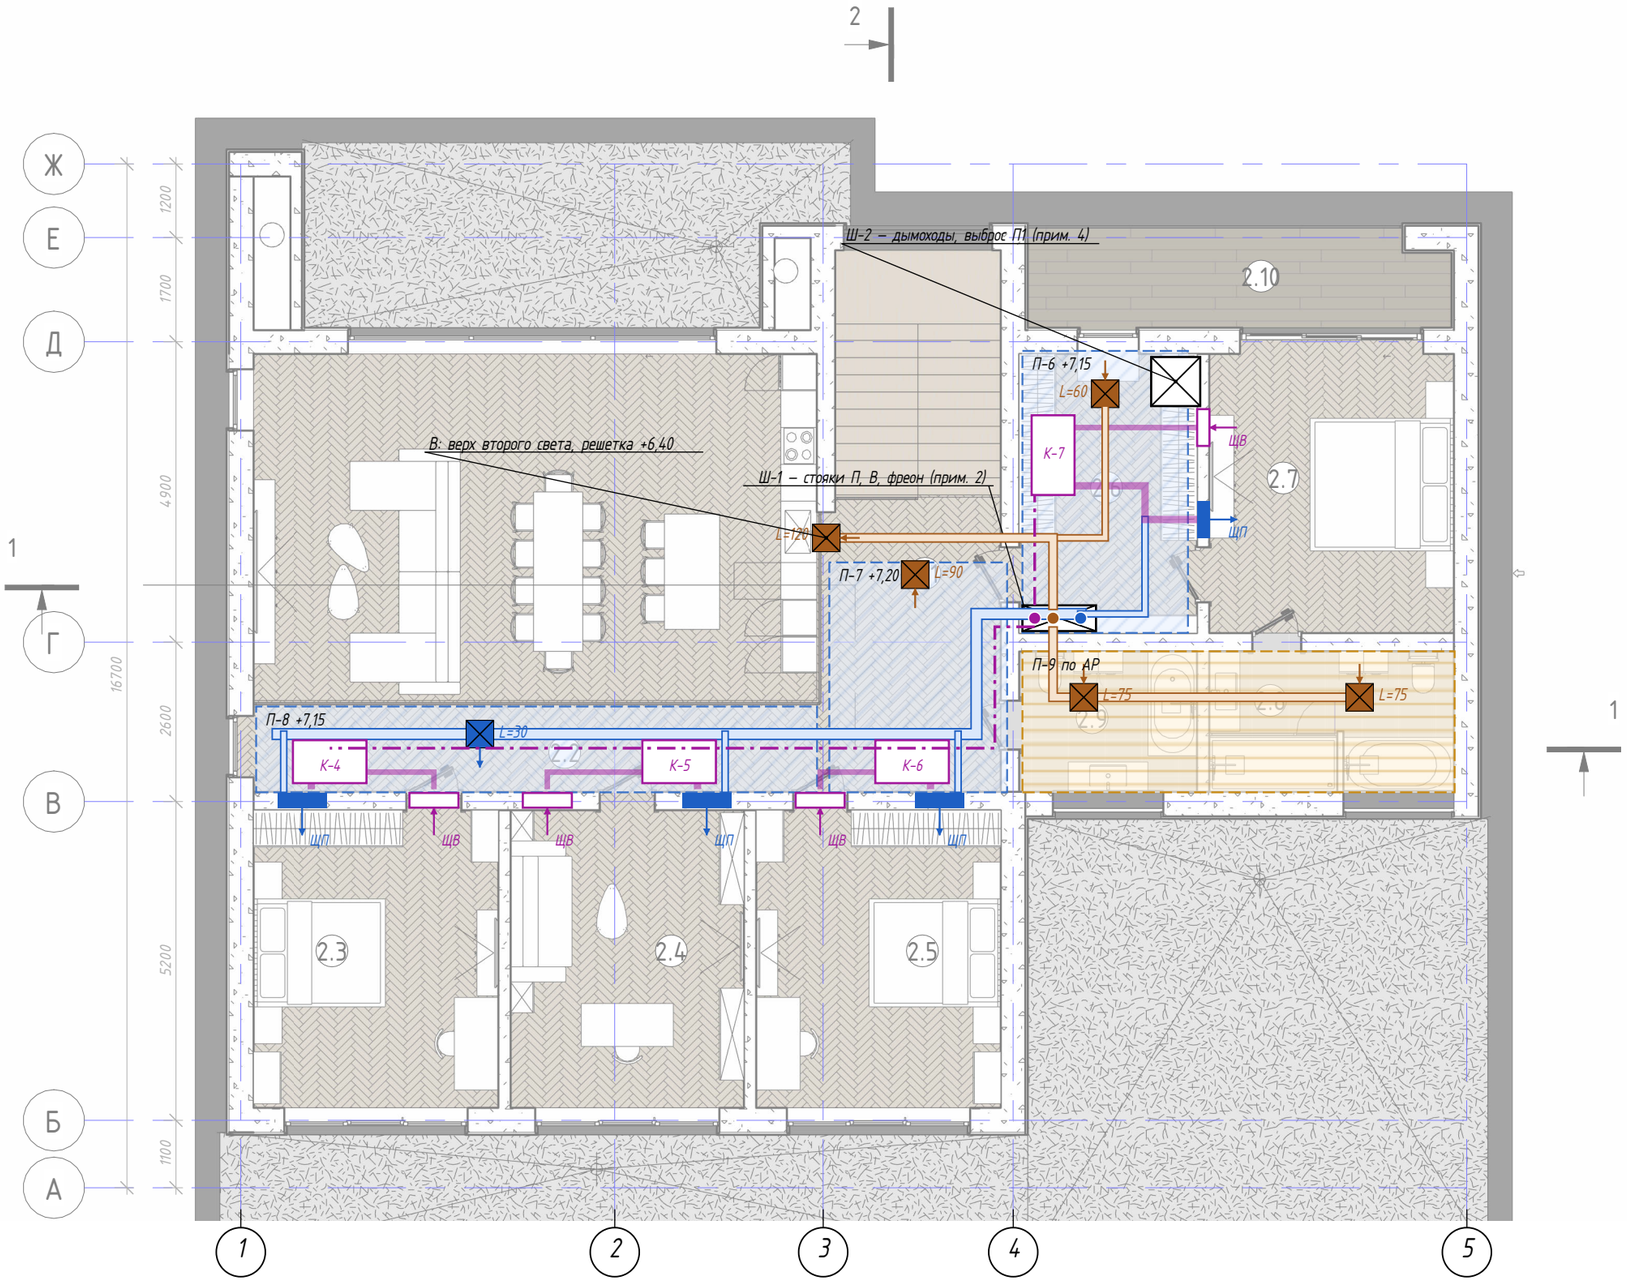

Условные обозначения

- Приточный воздуховод от П1 (П1 – лист 3)
- Вытяжной воздуховод к П1
- Стояки П и В с 1 этажа (шахта Ш-1)
- Приточная решетка, L – м³/ч
- Вытяжная решетка, L – м³/ч
- ЩП – щелевая решетка в стене: подача К + свежий воздух
- ЩВ – щелевая решетка в стене: возврат К
- К – Канальный блок кондиционирования
- Фреонопроводы и дренаж
- Шахта
- Подшивка: зона с блоками/магистралями
- Подшивка санузлов – по АР

Зона	Что проходит	Глубина от низа плиты, мм	Низ подшивки
П-6	К-7, магистрали, шахта Ш-1	400	+7,15
П-7	К-6, магистрали П Ø200, В Ø160, фреон	350	+7,20
П-8	К-4, К-5, магистраль П Ø200	400	+7,15
П-9	вытяжка с/у Ø160	–	по АР

Примечания

1. Отметки – при низе плиты покрытия ≈+7,55 (пол 2 этажа ≈+4,05, высота 3,5 м – разрезы АР15, АР16); уточнить по КР. Подшивка на окна не заходит.
2. П1 – в топочной 1.6 (лист 3). Шахта Ш-1 – у южной стены гардеробной 2.6, в зоне, указанной Заказчиком, ≈1,2×0,45 м (остаток полосы свободен): стояки П и В Ø200 и фреонопроводы. Дверь из 2.6 в спальню 2.7 открывается свободно.
3. Спальни 2.3–2.5 и 2.7 – без подшивки потолков (решение Заказчика): подача кондиционера вместе со свежим воздухом (ЩП) и возврат (ЩВ) – щелевыми решетками в верхней части стены со стороны галереи и гардеробной, скорость в решетке до 2 м/с, ЩП и ЩВ разнесены. ЩВ – рециркуляция кондиционера, не вытяжка: свежий воздух от П1 идет через ЩП круглый год (зимой – при выключенном кондиционере), из спален уходит перетеканием под дверью (зазор 15–20 мм или переточная решетка – АР) и удаляется вытяжкой санузлов, гардеробной и верхней зоны второго света. Канальные блоки – в подшивке галереи, холла и гардеробной, обслуживание – из коридора. Точные места решеток – по мебели на стадии Р.
4. Ш-2 – шахта ≈0,8×0,8 м в свету: дымоходы котлов, вытяжка топочной и выброс П1 – раздельными каналами выше кровли.

Изм.	Кол.уч	Лист	№ док.	Подп.	Дата	ЭП-ОВ			
						Двухэтажный индивидуальный жилой дом с баней. Московская область, кадастровый номер участка 50:08:0050209:1600			
Разраб.						Отопление, вентиляция и кондиционирование. Принципиальные решения	Стадия	Лист	Листов
Пров.							ЭП	4	7
Н.контр.						План 2 этажа дома. Вентиляция и кондиционирование. Зоны подшивки			
Утв.									

Взам. инв. №

Подп. и дата

Инв. № подл.

Копировал

Формат А3