
План 1 этажа. Задание АР и КР. М 1:100

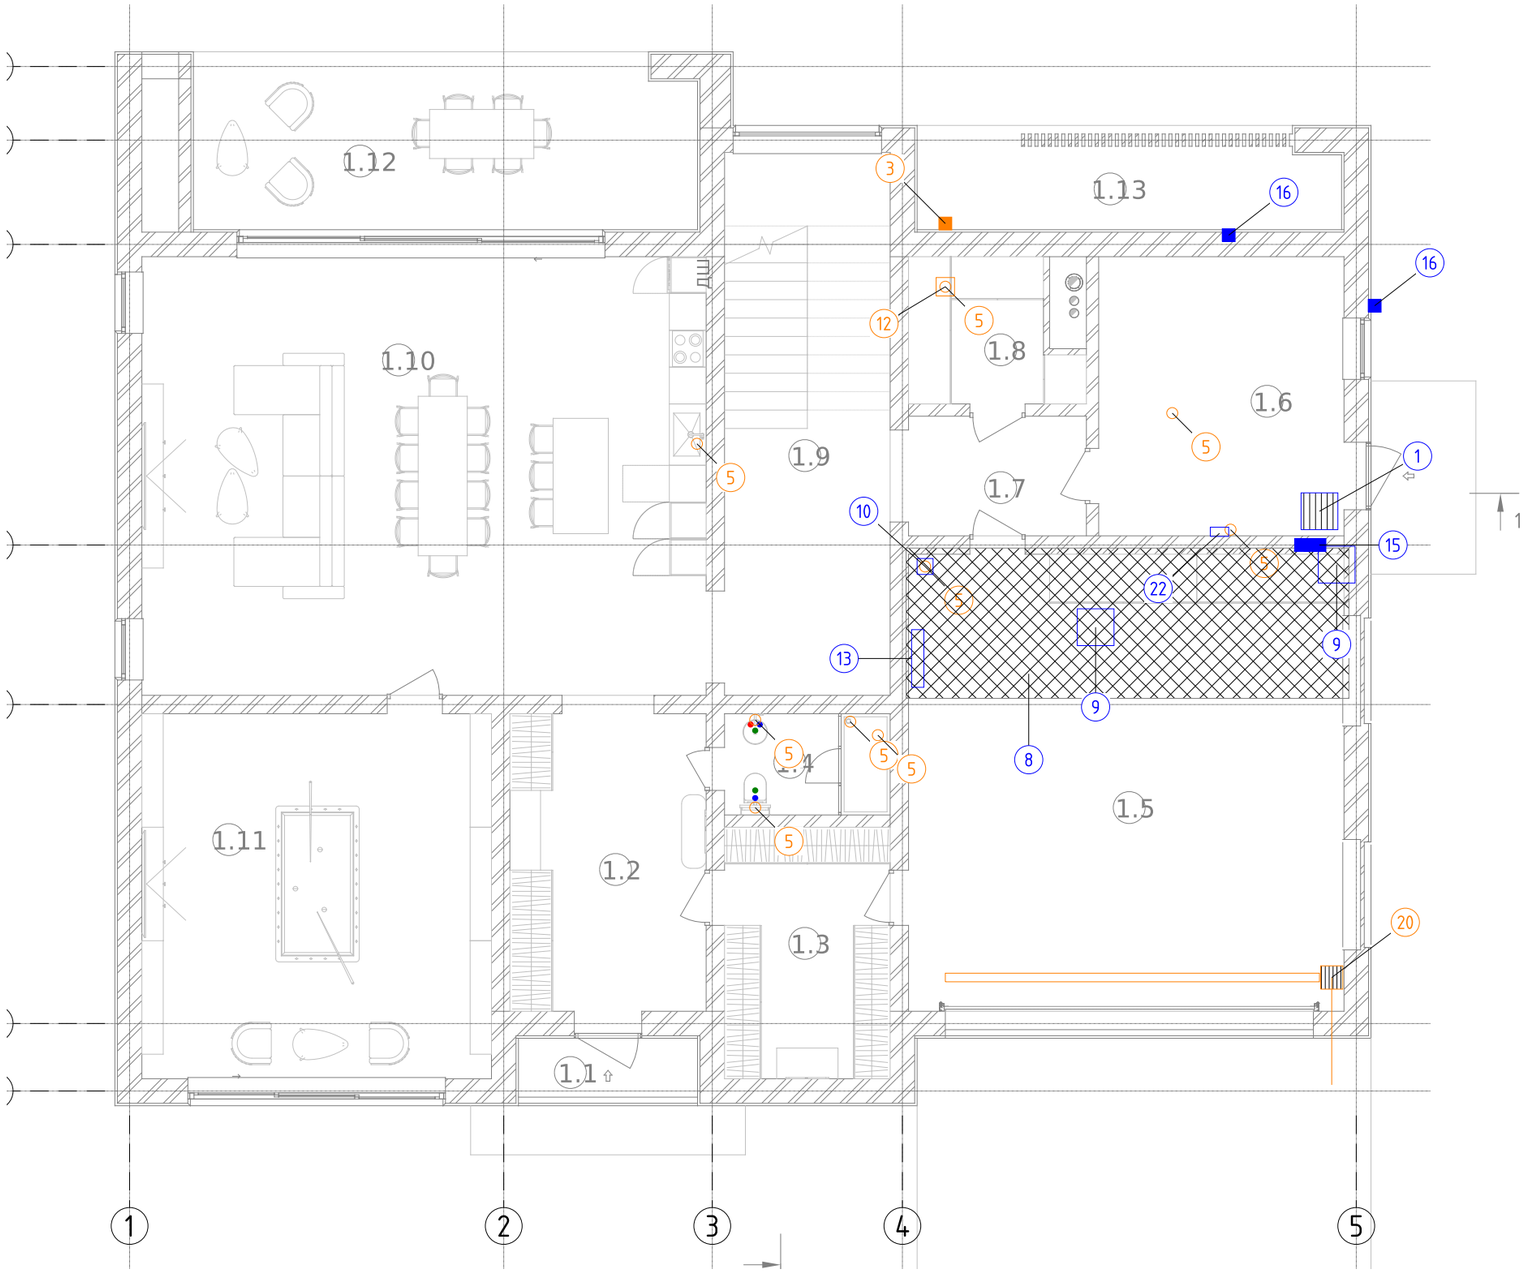

Условные обозначения

- проход, место оборудования, люк (водопровод)
- проход канализации К1 (футляр, гильза, люк)
- гильза в плите (номер — таблица листа 3)
- короб (подшивной потолок) гаража

Позиции на плане (подробно — лист 3)

1 — приямок ввода 600×600, дно −1,100; 2 — проем 450×450 под ввод
3 — футляр Ф160 выпуска К1-1 под краем плиты
5 — гильзы в фундаментной плите (кружки)
8 — короб гаража, низ не выше +2,900
9 — люки 600×600 в коробе
10 — короб стояка Ст.К1-1, люк 300×400
12 — люки в полу 300×300 над прочистками
13 — место ШВК-1
15 — гильзы в стене гараж/1.6
16 — гильзы поливочных кранов
20 — гараж: лоток ЛГ-1, понижение плиты под ПУ-1, футляр К2-1
22 — места контроллеров защиты от протечек

Примечания

1. Номер у точки — позиция таблицы (лист 3); координаты — в метрах от осей 1/А (дом, баня — свои оси), отметки — от ±0,000 своего здания.
2. Подложка — АР (Revit 19.10.2026). Точки и размеры — по 3D-модели систем ВК; при изменении АР или КР задание уточняется.

Согласовано

Взам.инв.№

Подпись и дата


Инв.№ подл.

Изм.	Кол.уч	Лист	№ док	Подп.	Дата	И05.09.26-ВК.ТЗ-1		
						Двухэтажный индивидуальный жилой дом с баней. Московская область, кадастровый номер участка 50:08:0050209:1600		
Разраб.						Водопровод и канализация	Стадия	Лист	Листов
Пров.							Р	1	3
Н.контр.						Задание АР и КР. План 1 этажа			
ГИП									


Копировал

Формат А3

Гильзы в перекрытии над гаражом (вид на план 2 этажа). М 1:50

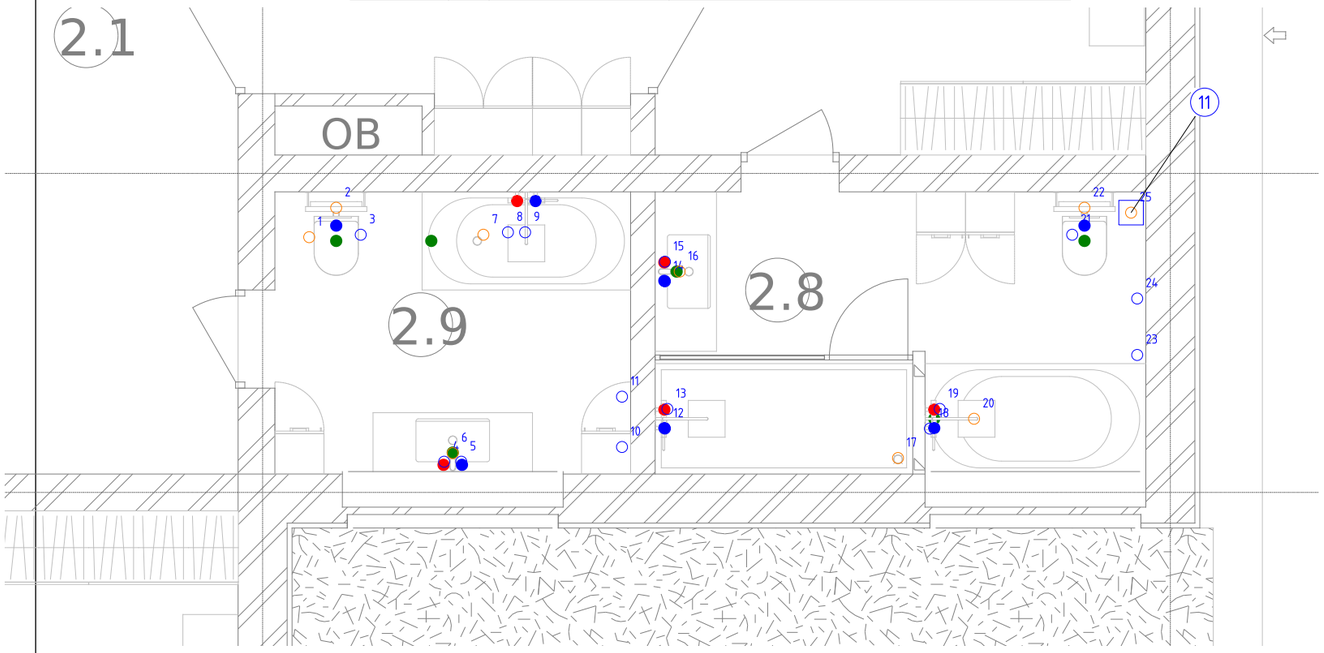

Баня. План. Задание АР и КР. М 1:100

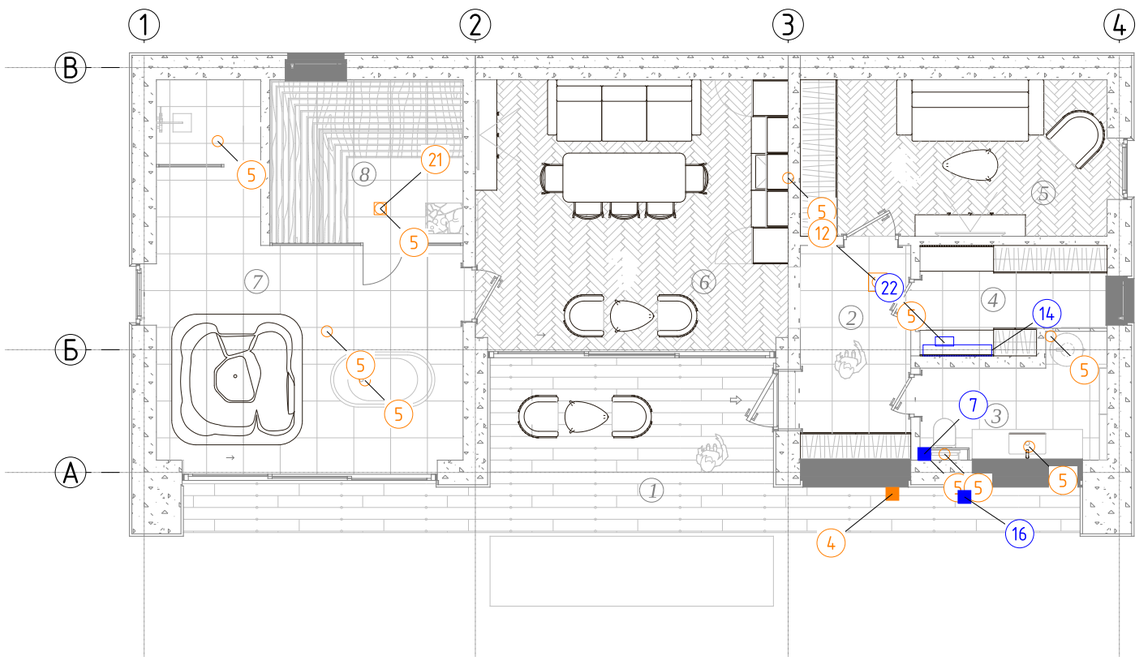

Условные обозначения

- проход, место оборудования, люк (водопровод)
- проход канализации К1 (футляр, гильза, люк)
- гильза в плите (номер — таблица листа 3)
- короб (подшивной потолок) гаража

Позиции на плане (подробно — лист 3)

4 — футляр Ф160 выпуска К1-б (баня)
5 — гильзы в фундаментной плите (кружки)
6 — гильзы в перекрытии над гаражом (лист 2)
7 — гильзы Ф160 в покрытии, проход кровли
11 — короб вытяжной части Ст.К1-1в (2.8), гильза Ф160 в покрытии (7)
12 — люки в полу 300×300 над прочистками
14 — место ШВК-Б
16 — гильзы поливочных кранов
17 — гильзы в стене б2/б6 (лист 8)
21 — трап Т-б2 в парной
22 — места контроллеров защиты от протечек

Примечания

1. Номер у точки — позиция таблицы (лист 3); координаты — в метрах от осей 1/А (дом, баня — свои оси), отметки — от ±0,000 своего здания.
2. Подложка — АР (Revit 19.10.2026). Точки и размеры — по 3D-модели систем ВК; при изменении АР или КР задание уточняется.
3. Номер у гильзы перекрытия — строка таблицы «Гильзы в перекрытии» (лист 3).

Согласовано

Взам.инв.№

Подпись и дата

Инв.№ подл.

Изм.	Кол.уч	Лист	№ док	Подп.	Дата	И05.09.26-ВК.ТЗ-1			
						Двухэтажный индивидуальный жилой дом с баней. Московская область, кадастровый номер участка 50:08:0050209:1600			
Разраб.						Водопровод и канализация	Стадия	Лист	Листов
Пров.							Р	2	3
Н.контр.						Задание АР и КР. Перекрытие над гаражом. Баня			
ГИП									

Копировал

Формат А3

Задания АР и КР от раЗдела ВК

Поз.	Задание	Помещение, место	ПривяЗка, отметки	РаЗдел	Лист ВК
1	Приямок ввода водопровода 600×600 мм в свету, дно −1,100, водонепроницаемый, с утепленной крышкой в уровне пола; местное Заглубление фундаментной плиты от приямка до наружной грани (низ −1,250)	топочная 1.6, у восточной стены	х 19,10…19,70, у 9,15…9,75	КР	лист 7, лист 14 узел 1
2	Проем 450×450 мм в наружной стенке приямка (заглублении плиты) под ввод В1 ПЭ 32 — Зазор 0,2 м вокруг трубы (п. 8.8 СП 30.13330.2020); в том же проеме — подводка автополива КХ-8 PE-Xa 25 (у 9,62, отм. −0,950); Заделка — ВК	то же	ось ввода у 9,45, отм. оси −0,850	КР	лист 14 узел 1
3	Футляр ПП Ф160 SN8 L = 1,0 м под краем фундаментной плиты для выпуска К1-1 Ф110 — укладывается до бетонирования; если плита продолжается под террасой 1.13 — футляр у ее края; если по краю плиты ребро — проем 550×550 (Зазор 0,2 м)	дом, север (у стены 1.8 / под террасой 1.13)	х 13,30; лоток у границы −1,043	КР	лист 6, лист 14 узел 2
4	То же для выпуска К1-б Ф110	баня, юг	х 12,20; лоток у границы −0,994	КР	лист 9, лист 14 узел 2
5	ГильЗы в фундаментной плите для стояков К1 (сеть под плитой — решение Заказчика) — до бетонирования: дом 9 шт., баня 10 шт.	дом, баня	координаты — таблица на листе 3	КР	листы 6, 9, 14
6	ГильЗы в перекрытии над гаражом (+3,650…+3,850) для подъемов В1, Т3, Т4 и опусков К1 — 25 шт.	гараж / с/у 2.8, 2.9	координаты — таблица на листе 3	КР	листы 5, 14 узел 4
7	ГильЗы Ф160 в плитах покрытия для вытяжных частей стояков: Ст.К1-1в (дом), Ст.К1-б (баня); проходные элементы кровли — по системе кровли; выход — не ближе 4 м от открываемых окон (п. 18.18)	кровля дома, кровля бани	дом: х 19,68, у 8,58; баня: х 12,72, у 0,30; верх +0,35 над кровлей	АР, КР	листы 12, 14 узел 6
8	Короб (подшивной потолок) под сетями ВК в гараже: низ не выше +2,900, ширина по трубам; материал — негорючий (гараж)	гараж	х 12,66…19,88, у 6,40…8,85 (по листу 5)	АР	лист 5
9	Люки 600×600 мм в коробе гаража: у коллекторов ШВК-2 и у прочистки в начале сборного К1	гараж	ШВК-2: х 15,75, у 7,56; прочистка: х 19,68, у 8,58	АР	лист 5
10	Короб стояка Ст.К1-1 Ф110 (≈250×250 мм) от пола до потолка гаража с люком 300×400 мм у ревиЗии на +1,000; звукоиЗоляция стояка	гараж, северо-Западный угол	х 12,97, у 8,55	АР	листы 5, 6
11	Короб вытяжной части Ст.К1-1в Ф110 (≈200×200 мм) сквоЗь 2 этаж до кровли	с/у 2.8	х 19,68, у 8,58	АР	листы 5, 12
12	Люки напольные 300×300 мм (герметичные, под плитку) над стояками прочисток К1 в грунте	1.8; б2	дом: х 13,30, у 13,11; баня: х 11,96, у 3,10	АР	лист 14 узел 5
13	Место под шкаф ШВК-1 накладной ≈950×700×200 мм, низ +0,400; выходы труб из шкафа — вниЗ в пол	гараж, Западная стена	х 12,75, у 6,58…7,52	АР	листы 4, 13
14	Место под шкаф ШВК-Б накладной ≈1100×650×180 мм, низ +0,300; перегородка — под нагрузку ≈40 кг	баня, б4, на перегородке б3/б4	х 12,70…13,82, у 2,08	АР	листы 8, 13
15	ГильЗы в стене гараж / топочная 1.6 под потолком для магистралей В1, Т3, Т4 — 3 шт.	гараж / 1.6	х 19,10, х 19,25, х 19,40; отм. +3,050…+3,250	АР	лист 5
16	ГильЗы Ф75 в наружных стенах для поливочных кранов ПК-1, ПК-2, ПК-3	1.6, терраса 1.13, баня б3	ПК-1: х 20,30, у 12,80, +0,47; ПК-2: х 17,92, у 13,95, +0,32; ПК-3: х 13,38, у −0,40, +0,42	АР	листы 3, 8
17	ГильЗы в стене б2/б6 и дверных проемах для пучка труб В1, Т3 к б6, б7 (лист 8): Ф50 — 4, Ф75 — 4	баня	по листу 8	АР	лист 8
18	Пирог пола 1 этажа и бани: ЭППС не менее 100 мм — трубы В1, Т3, Т4 в паЗах в два ряда (оси −0,230 и −0,175); стяжка над трубами — по АР; трубы в полу беЗ соединений	дом, баня	лист 14 узел 3	АР	листы 3, 8, 14
19	Штробы и инсталляции для подъемов к приборам; уклон пола и гидроиЗоляция у трапов Т-1, Т-б1, Д-3, Д-б1; высота трапов — в пироге пола	с/у, 1.6, б7	по листам 3–5, 8, 9	АР	
20	Гараж: углубление в стяжке под лоток ЛГ-1 DN100 вдоль ворот (≈200×150 мм) и уклон пола к лотку; местное понижение фундаментной плиты под пескоуловитель ПУ-1 (≈450×450 мм, на ≈200 мм) с гильЗой Ф160 под вертикальный выпуск; футляр ПП Ф160 SN8 L = 1,0 м под южным краем плиты для выпуска К2-1 (до бетонирования)	гараж, у ворот	ЛГ-1: х 13,30…19,40, у 1,85; ПУ-1: х 19,60, у 1,85; К2-1: х 19,60, лоток −0,800…−0,835	АР, КР	лист 4, лист 14 узел 2
21	Трап Т-б2 Ду50 в парной: уклон пола к трапу, гидроиЗоляция; гильЗа в плите — в поЗ. 5	баня, б8	х 3,85, у 4,30	АР	лист 9
22	Защита от протечек: места контроллеров КЗП-1 (1.6, над стиральной машиной, низ +1,620) и КЗП-2 (б4, над ШВК-Б, низ +1,200); каналы для кабелей датчиков ДП в стенах и полу	дом, баня	листы 3–5, 8	АР	ТЗ-2

ГильЗы в перекрытии +3,650 (лист 2)

№	ГильЗа	х, м	у, м	Труба
1	Ф75	12,98	8,38	К1 Ф50
2	Ф160	13,20	8,62	К1 Ф110
3	Ф50	13,40	8,40	В1 PE-Xa 16×2,2
4	Ф50	14,08	6,55	В1 PE-Xa 16×2,2
5	Ф75	14,22	6,55	Т3 PE-Xa 16×2,2
6	Ф75	14,15	6,62	К1 Ф50
7	Ф75	14,40	8,40	К1 Ф50
8	Ф50	14,60	8,42	В1 PE-Xa 20×2,8
9	Ф75	14,74	8,42	Т3 PE-Xa 20×2,8
10	Ф75	15,53	6,67	Т4 PE-Xa 20×2,8
11	Ф75	15,53	7,08	Т4 PE-Xa 20×2,8
12	Ф50	15,88	6,82	В1 PE-Xa 16×2,2
13	Ф75	15,90	6,98	Т3 PE-Xa 16×2,2

№	ГильЗа	х, м	у, м	Труба
14	Ф50	15,88	8,02	В1 PE-Xa 16×2,2
15	Ф75	15,88	8,18	Т3 PE-Xa 16×2,2
16	Ф75	16,00	8,10	К1 Ф50
17	Ф75	17,78	6,58	К1 Ф50
18	Ф50	18,04	6,82	В1 PE-Xa 20×2,8
19	Ф75	18,12	6,98	Т3 PE-Xa 20×2,8
20	Ф75	18,40	6,90	К1 Ф50
21	Ф50	19,20	8,40	В1 PE-Xa 16×2,2
22	Ф160	19,30	8,62	К1 Ф110
23	Ф75	19,73	7,42	Т4 PE-Xa 20×2,8
24	Ф75	19,73	7,88	Т4 PE-Xa 20×2,8
25	Ф160	19,68	8,58	К1в Ф110

ГильЗы в фундаментных плитах

Плита	ГильЗа	х, м	у, м	Труба
дом	Ф75	9,25	10,55	К1 Ф50
дом	Ф160	10,20	4,62	К1 Ф110
дом	Ф75	10,20	6,05	К1 Ф50
дом	Ф75	11,75	6,02	К1 Ф50
дом	Ф75	12,20	5,80	К1 Ф50
дом	Ф160	12,97	8,55	К1 Ф110
дом	Ф75	17,00	11,05	К1 Ф50
дом	Ф75	17,95	9,15	К1 Ф50
дом	Ф160	13,30	13,11	К1 прочистка

Плита	ГильЗа	х, м	у, м	Труба
баня	Ф160	1,20	5,40	К1 Ф110
баня	Ф160	2,98	2,30	К1 Ф110
баня	Ф75	3,60	1,50	К1 Ф50
баня	Ф75	3,85	4,30	К1 Ф50
баня	Ф75	10,50	4,80	К1 Ф50
баня	Ф160	12,72	0,30	К1в Ф110
баня	Ф160	13,05	0,30	К1 Ф110
баня	Ф75	14,43	0,42	К1 Ф50
баня	Ф75	14,78	2,22	К1 Ф50
баня	Ф160	11,96	3,10	К1 прочистка

Согласовано

Взам.инв.№

Подпись и дата

Инв.№ подл.

Изм.	Кол.уч	Лист	№ док	Подп.	Дата
Разраб.					
Пров.					
Н.контр.					
ГИП					

И05.09.26-ВК.ТЗ-1

Двухэтажный индивидуальный жилой дом с баней. Московская область, кадастровый номер участка 50:08:0050209:1600

Водопровод и канализация

Стадия	Лист	Листов
Р	3	3

Задание АР и КР. Таблица Заданий. ГильЗы

Копировал

Формат А3