




План насосной станции на отм. -2,200 (фрагмент) М 1:50

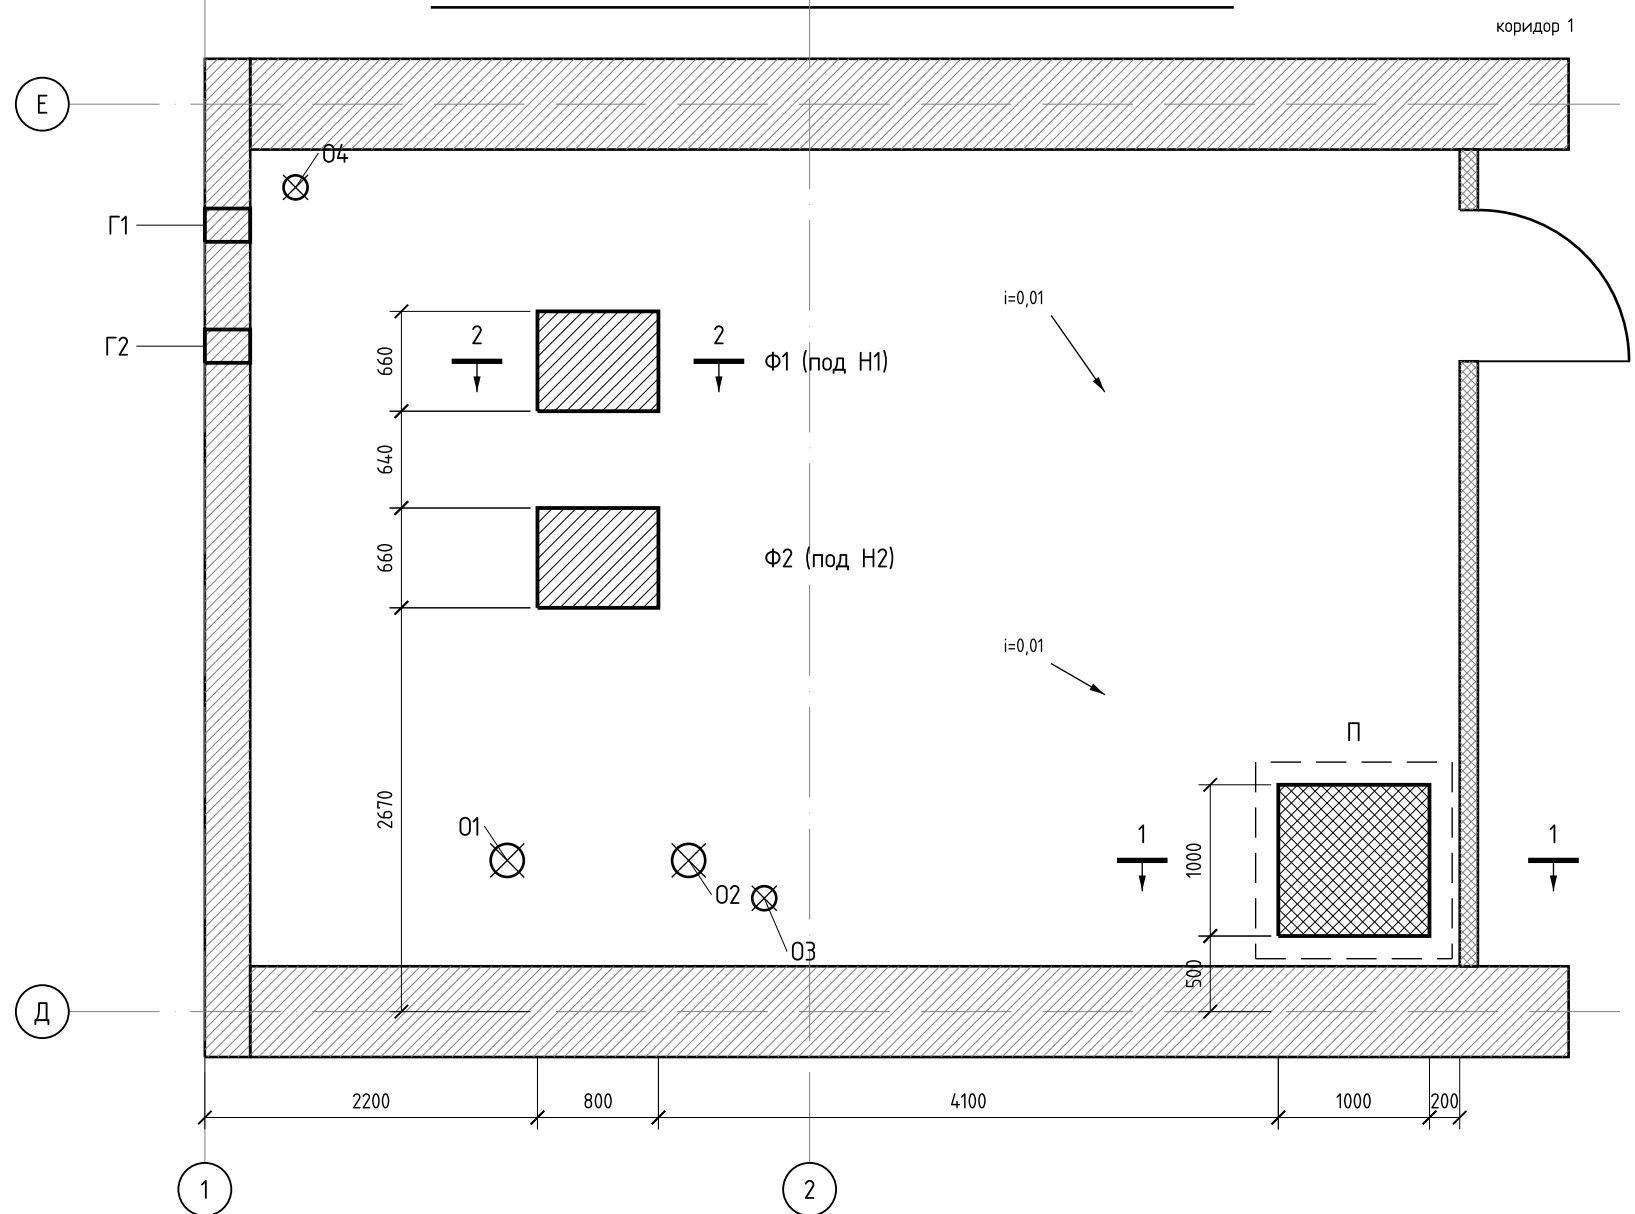

Разрез 1-1 М 1:20

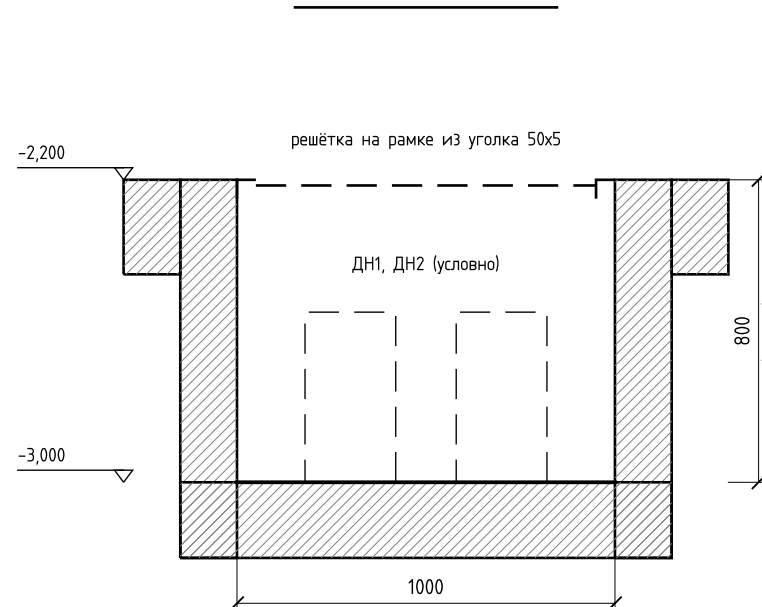

Разрез 2-2 М 1:20

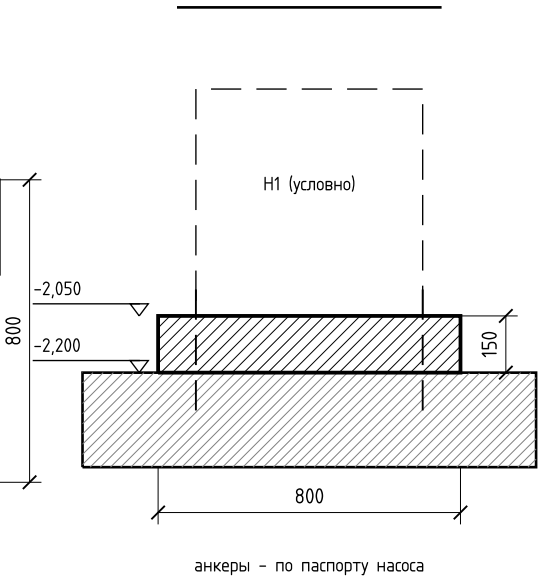

- Требования к выполнению
1. Приемок – монолитный железобетонный, водонепроницаемый; толщины, армирование и гидроизоляция определяет раздел КР. По периметру – Закладная рамка из уголка 50х5 под съёмную решётку 1000х1000 (решётка – по спецификации ПТ, поз. 28), верх рамки – в уровне чистого пола. В приемке устанавливаются два погружных насоса массой по 16 кг.
 2. Пол насосной – с уклоном 0,01 к приемку.
 3. Основания Ф1, Ф2 – бетонные, размеры уточняются по паспорту поставленного насоса. Нагрузка на основание – до 3,0 кН (насос с водой и арматурой), анкерные болты – по паспорту насоса.
 4. Гильзы Г1, Г2 закладываются в стену подвала по оси 1 при бетонировании; проход вводов – герметичный (узел 1, лист 11).
 5. Отверстия 01-04 – в перекрытии над подвалом (пом. 05 1 этажа), под стальные гильзы, закладываемые при бетонировании (узел 3, лист 11). Балки 20К2 не ослаблять.
 6. Погонная нагрузка от трубопроводов обвязки на перекрытие подвала – до 0,7 кН/м (Ду200 с водой), крепление – по узлу 4.
 7. Привязки – от осей Здания; размеры – в мм, отметки – в м.

Перечень элементов

Обозн.	Элемент	Размеры, мм	Отметка	От оси 1 / оси Д, мм
П	Приемок	1000х1000х800 (в свету)	дно -3,000	7100 / 500 (угол)
Ф1	Основание под насос Н1	800х660х150	верх -2,050	2200 / 3970 (угол)
Ф2	Основание под насос Н2	800х660х150	верх -2,050	2200 / 2670 (угол)
Г1, Г2	Гильзы вводов в стене по оси 1	труба 219х6, L=500	ось -1,900	ось 1 / 5200 и 4400
01	Отверстие: стояк Ст.В21-1 Ду150	под гильзу 219х6	перекрытие	2000 / 1000 (ось)
02	Отверстие: стояк Ст.В22-1 Ду150	под гильзу 219х6	перекрытие	3200 / 1000 (ось)
03	Отверстие: перемычка В2 Ду100	под гильзу 159х4,5	перекрытие	3700 / 750 (ось)
04	Отверстие: линия к ГМ-80 Ду100	под гильзу 159х4,5	перекрытие	600 / 5450 (ось)

Задание принял

Раздел	Должность	Фамилия	Подпись	Дата
КР				

ОПР-01/24/2024-ДП1-ПТ.ЗД1

«Современный коммерческий оптово-продовольственный рынок (ОПР) по адресу: Донецкая область, г. Макеевка, Горняцкий район»

Док-павильон №23, №23.2 Рыба-Мясо.
Пожаротушение (ВПВ, АУПТ, АУПП ВРУ)

Задание разделу КР. Приемок, основания
под насосы, гильзы и отверстия

000 «Технология»