

Топочная 1.6. План. М 1:50

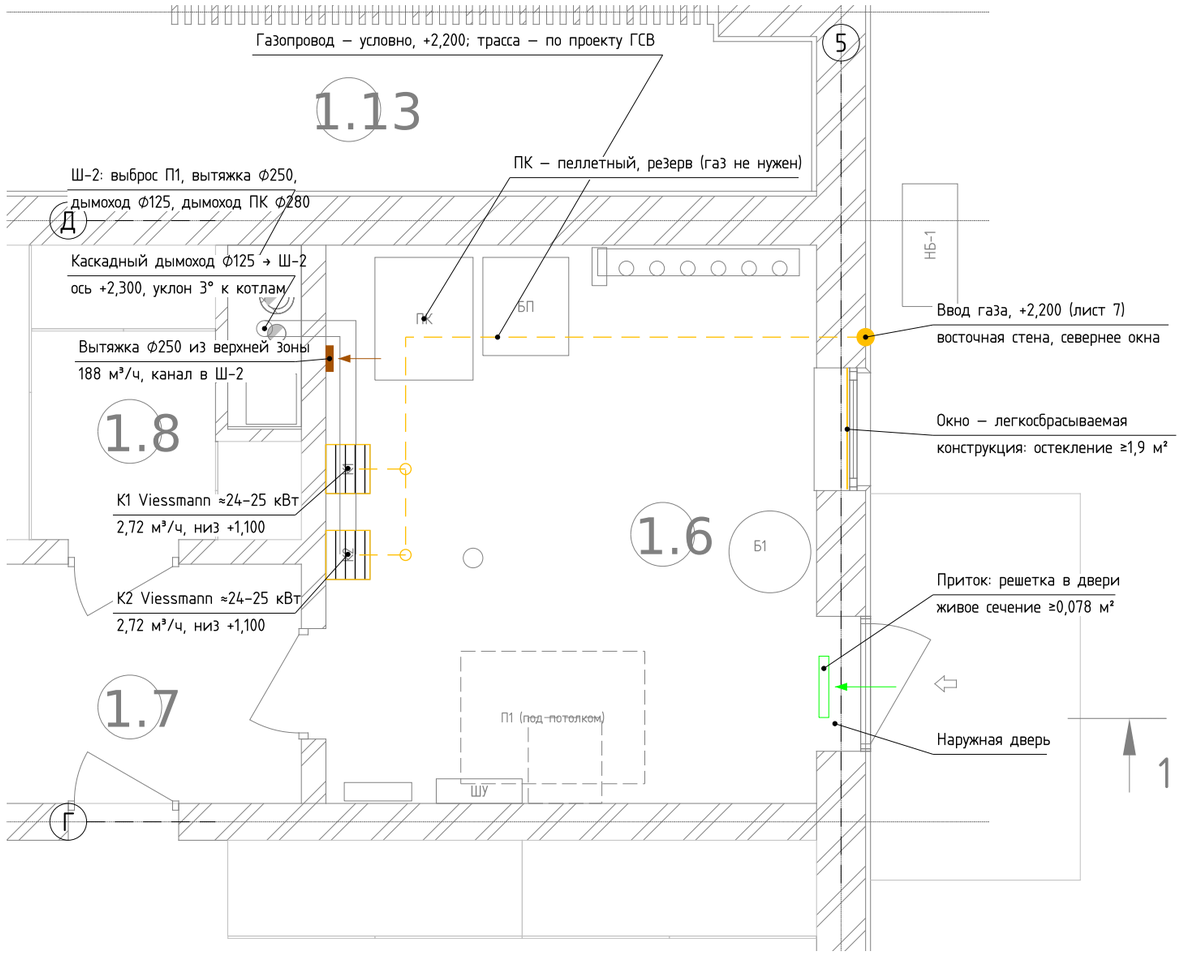

Развертка по западной стене (вид А). М 1:50

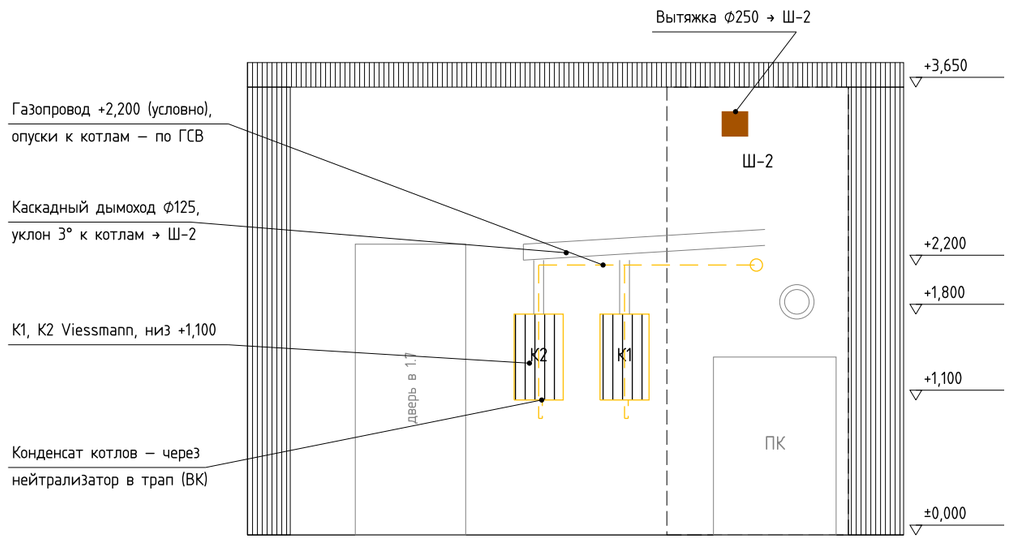

Потребители газа

Поз.	Марка	Потребитель газа	Ном. мощность, кВт	Расход газа, м³/ч	Примечание
1	K1	Котел газовый настенный конденсационный одноконтурный Viessmann (напр. Vitodens 200-W), каскадное управление	24–25	2,72	уточняется по паспорту типоразмера
2	K2	То же	24–25	2,72	то же
		Итого: каскад K1 + K2, одновременная работа	48	5,43	уточняется по паспорту

Примечания

1. Задание разделу ГСВ на газоснабжение котлов отопления и ГВС по И05.09.26-ОВ. Газ природный; расход — при низшей теплоте сгорания 33,5 МДж/м³ (9,3 кВт·ч/м³) и КПД 95 %: 5,43 м³/ч при 2×24 кВт — уточняется по паспорту выбранного типоразмера Viessmann (решение Заказчика).
2. Ввод газопровода — в восточной стене топочной севернее окна, на отметке +2,200 (лист 7 ОВ). Разводка внутри показана условно (по модели котельной И05.09.26-ТМ): открыто на +2,200 от ввода на Запад и вдоль котлов в 0,65 м от западной стены, опуски к котлам до +0,950 с подключением снизу. Трасса, отключающие устройства на вводе и перед котлами, счетчик газа и его место — по проекту ГСВ и ТУ.
3. Сигнализатор загазованности с клапаном-отсекателем на вводе — по проекту ГСВ; электропитание — ТЗ-2 (ЭОМ), поз. 18.
4. Воздух на горение — из помещения топочной (67 м³/ч при работе каскада). Приток наружного воздуха — решетка в нижней части наружной двери, живое сечение не менее 0,078 м², 282 м³/ч (вытяжка 188 м³/ч + воздух на горение).
5. Вытяжка — естественная, из верхней зоны топочной каналом Ф250 в шахте Ш-2, 188 м³/ч (3 обмена в час).
6. Отвод продуктов сгорания — общий каскадный дымоход Ф125 системы производителя котлов: коллектор на +2,300 с уклоном 3° к котлам, ввод в канал шахты Ш-2 (вместо двух Ф150 по модели АР), выход выше кровли — по АР. Подбор и расчет — по паспорту котлов Viessmann. Конденсат — через нейтрализатор в трап (ТЗ-3, ВК).
7. Топочная 1.6: объем ≈63 м³, до низа плиты перекрытия 3,65 м, выход наружу через дверь в восточной стене. Легкосбрасываемая конструкция — окно в восточной стене: площадь остекления не менее 0,03 м² на 1 м³ объема (≈1,9 м²) — проверить разделом АР.
8. В топочной также установлен пеллетный котел ПК ≈50 кВт (резерв, газом не питается) с отдельным дымоходом Ф280 в шахте Ш-2 — учесть в проекте ГСВ.
9. Отметки — от ±0,000 (чистый пол 1 этажа). Подложка — АР03 (выгрузка из Revit 19.10.2026); оборудование — по листам 7, 8 И05.09.26-ОВ.

Топочная 1.6 — исходные данные для ГСВ

Показатель	Значение
Объем топочной 1.6 / высота до низа плиты	≈63 м³ / 3,65 м
Газовые котлы: число, мощность	2 × 24 кВт (каскад, 48 кВт)
Расход газа (уточнить по паспорту)	5,43 м³/ч
Воздух на горение газа (из помещения)	67 м³/ч
Вытяжка естественная, канал Ф250 в Ш-2	188 м³/ч
Приток: решетка в наружной двери	282 м³/ч, ≥0,078 м²
Дымоход котлов	каскадный Ф125, канал в Ш-2
Ввод газа	восточная стена, +2,200
Остекление окна (ЛСК), требуется	≥1,9 м² — проверить АР
Выход наружу	дверь в восточной стене

Изм.	Кол.уч	Лист	№ док	Подп.	Дата	И05.09.26-ОВ.ТЗ-4			
						Двухэтажный индивидуальный жилой дом с баней. Московская область, кадастровый номер участка 50:08:0050209:1600			
Разраб.						Отопление, вентиляция и кондиционирование	Стадия	Лист	Листов
Пров.							Р	1	1
Н.контр.						Задание на газоснабжение (ГСВ). Топочная 1.6			
ГИП									

Согласовано

Взам.инв.№

Подпись и дата

Инв.№ подл.

Копировал

Формат А3