

И05.09.26-ОВ. Вентиляция и кондиционирование дома. 3D-модель — Общий вид с юго-запада

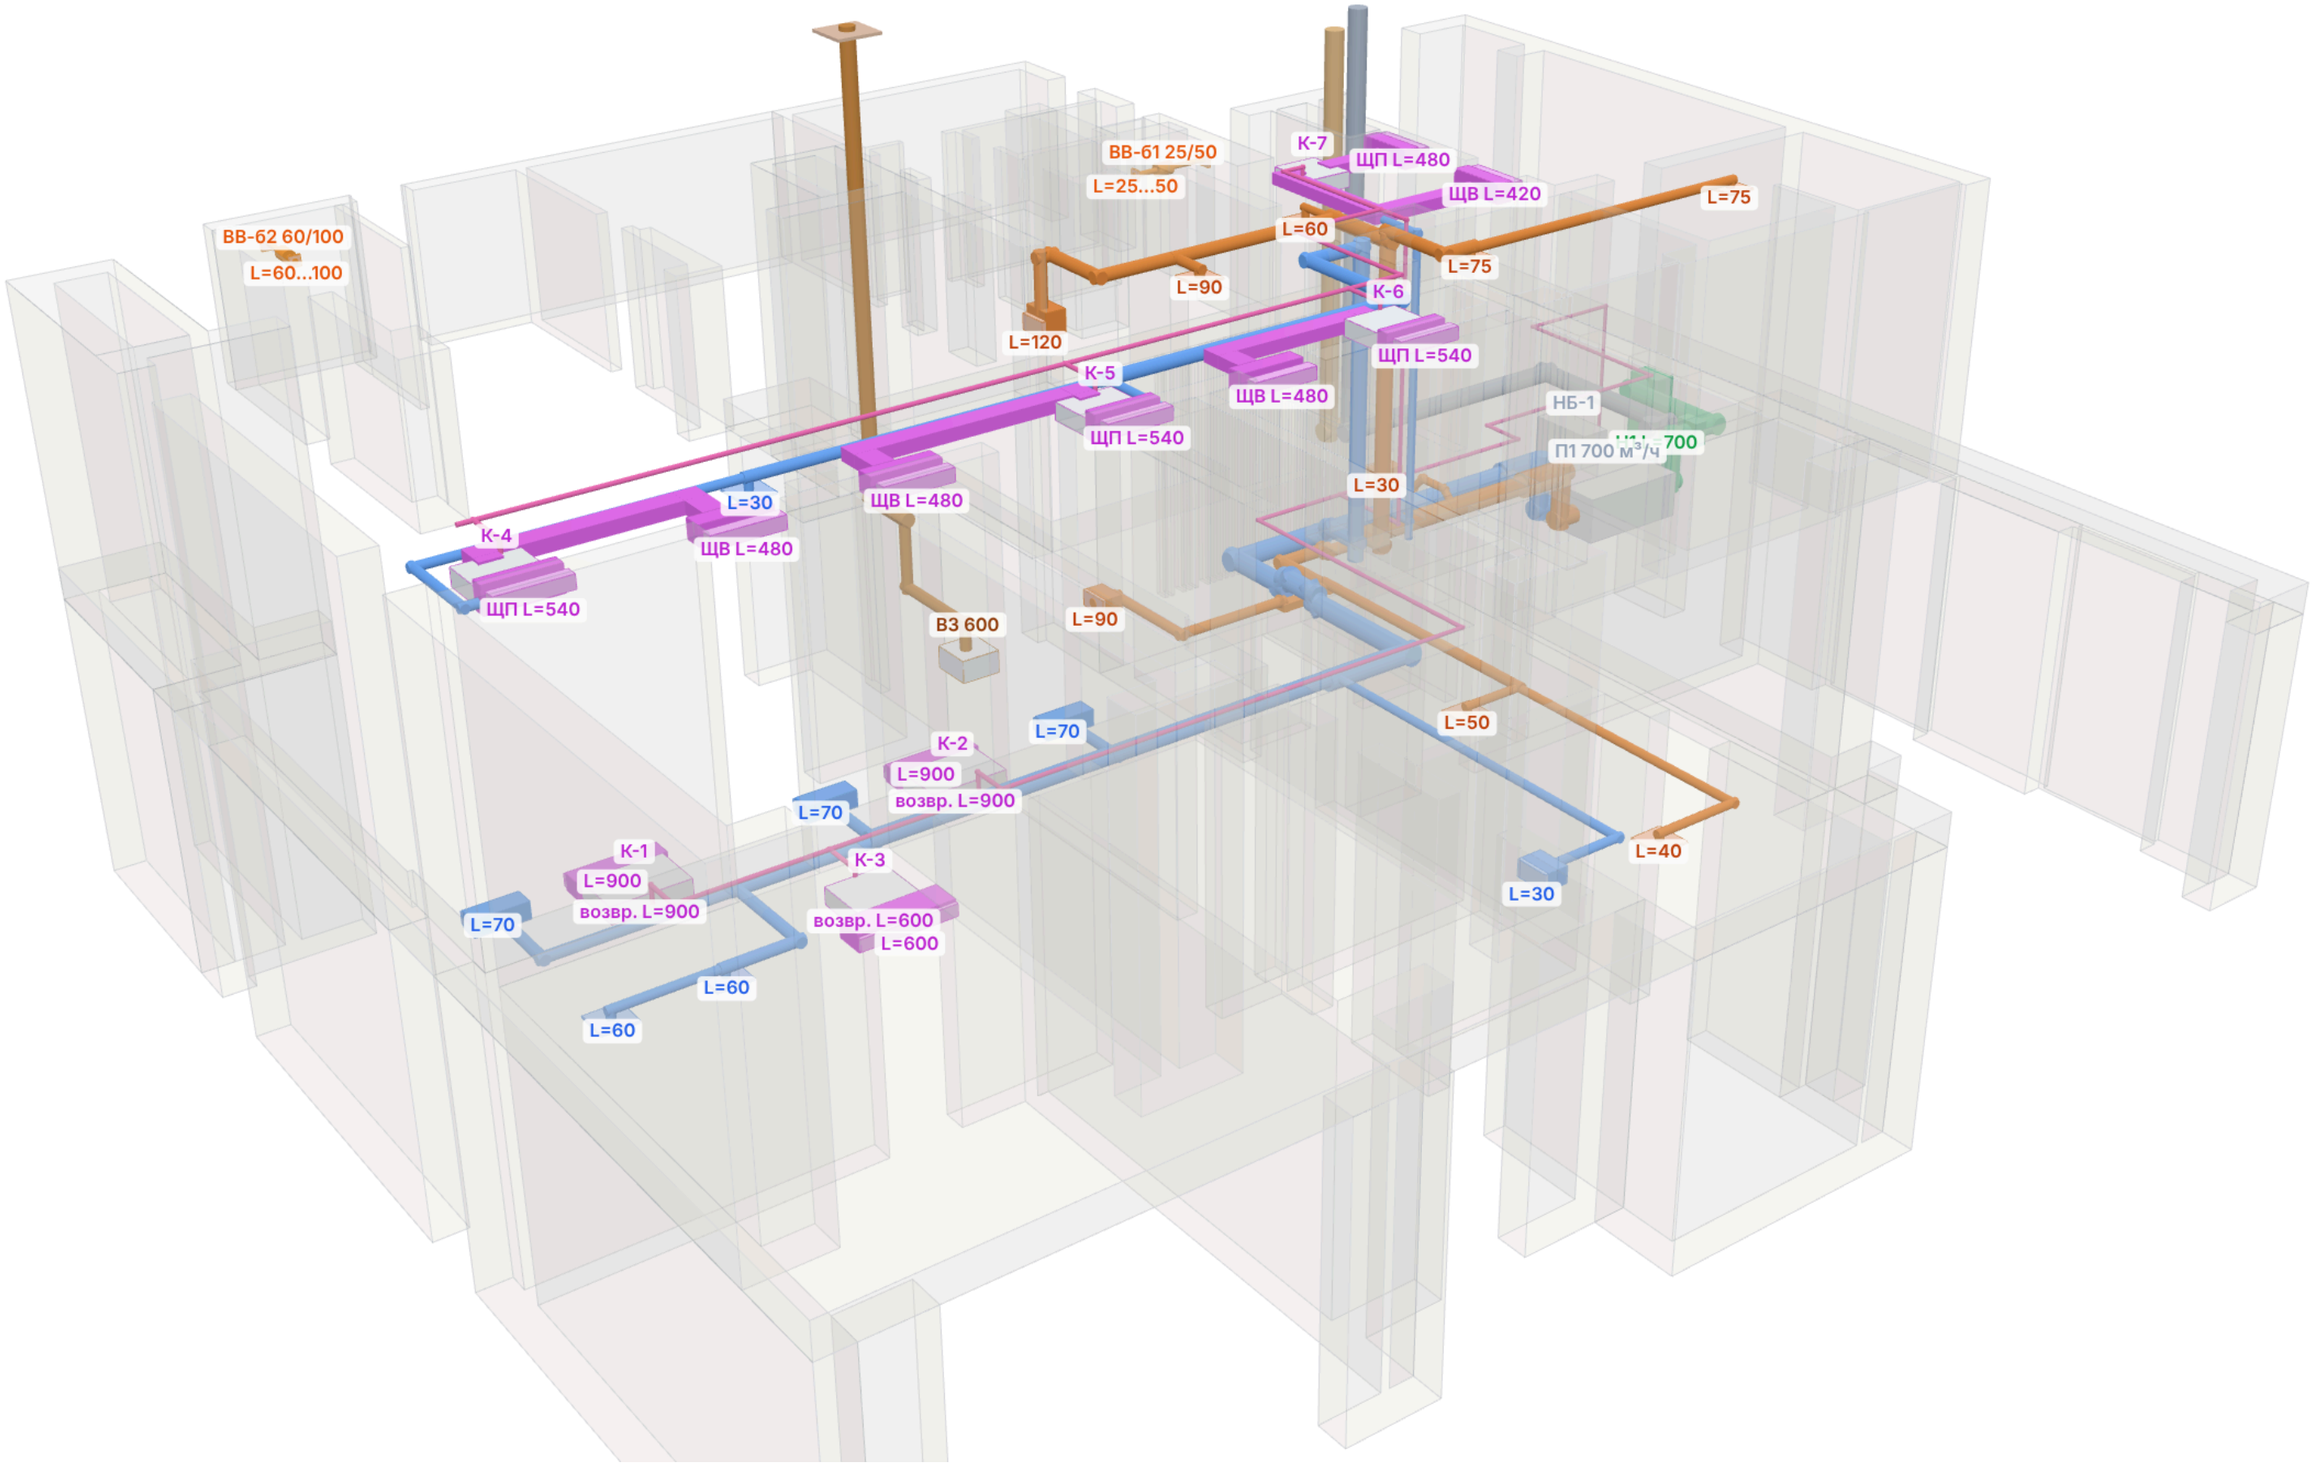

Стены — по АР03 и АР09 (полупрозрачно), подписи — расходы у решёток, м³/ч.

Модель по трассам листов 9–12; файлы И05.09.26-ОВ 3D (DWG, IFC, просмотр в браузере). Дренаж конденсата — по листам 9, 10.


И05.09.26-ОВ. Вентиляция и кондиционирование дома. 3D-модель — Общий вид без стен

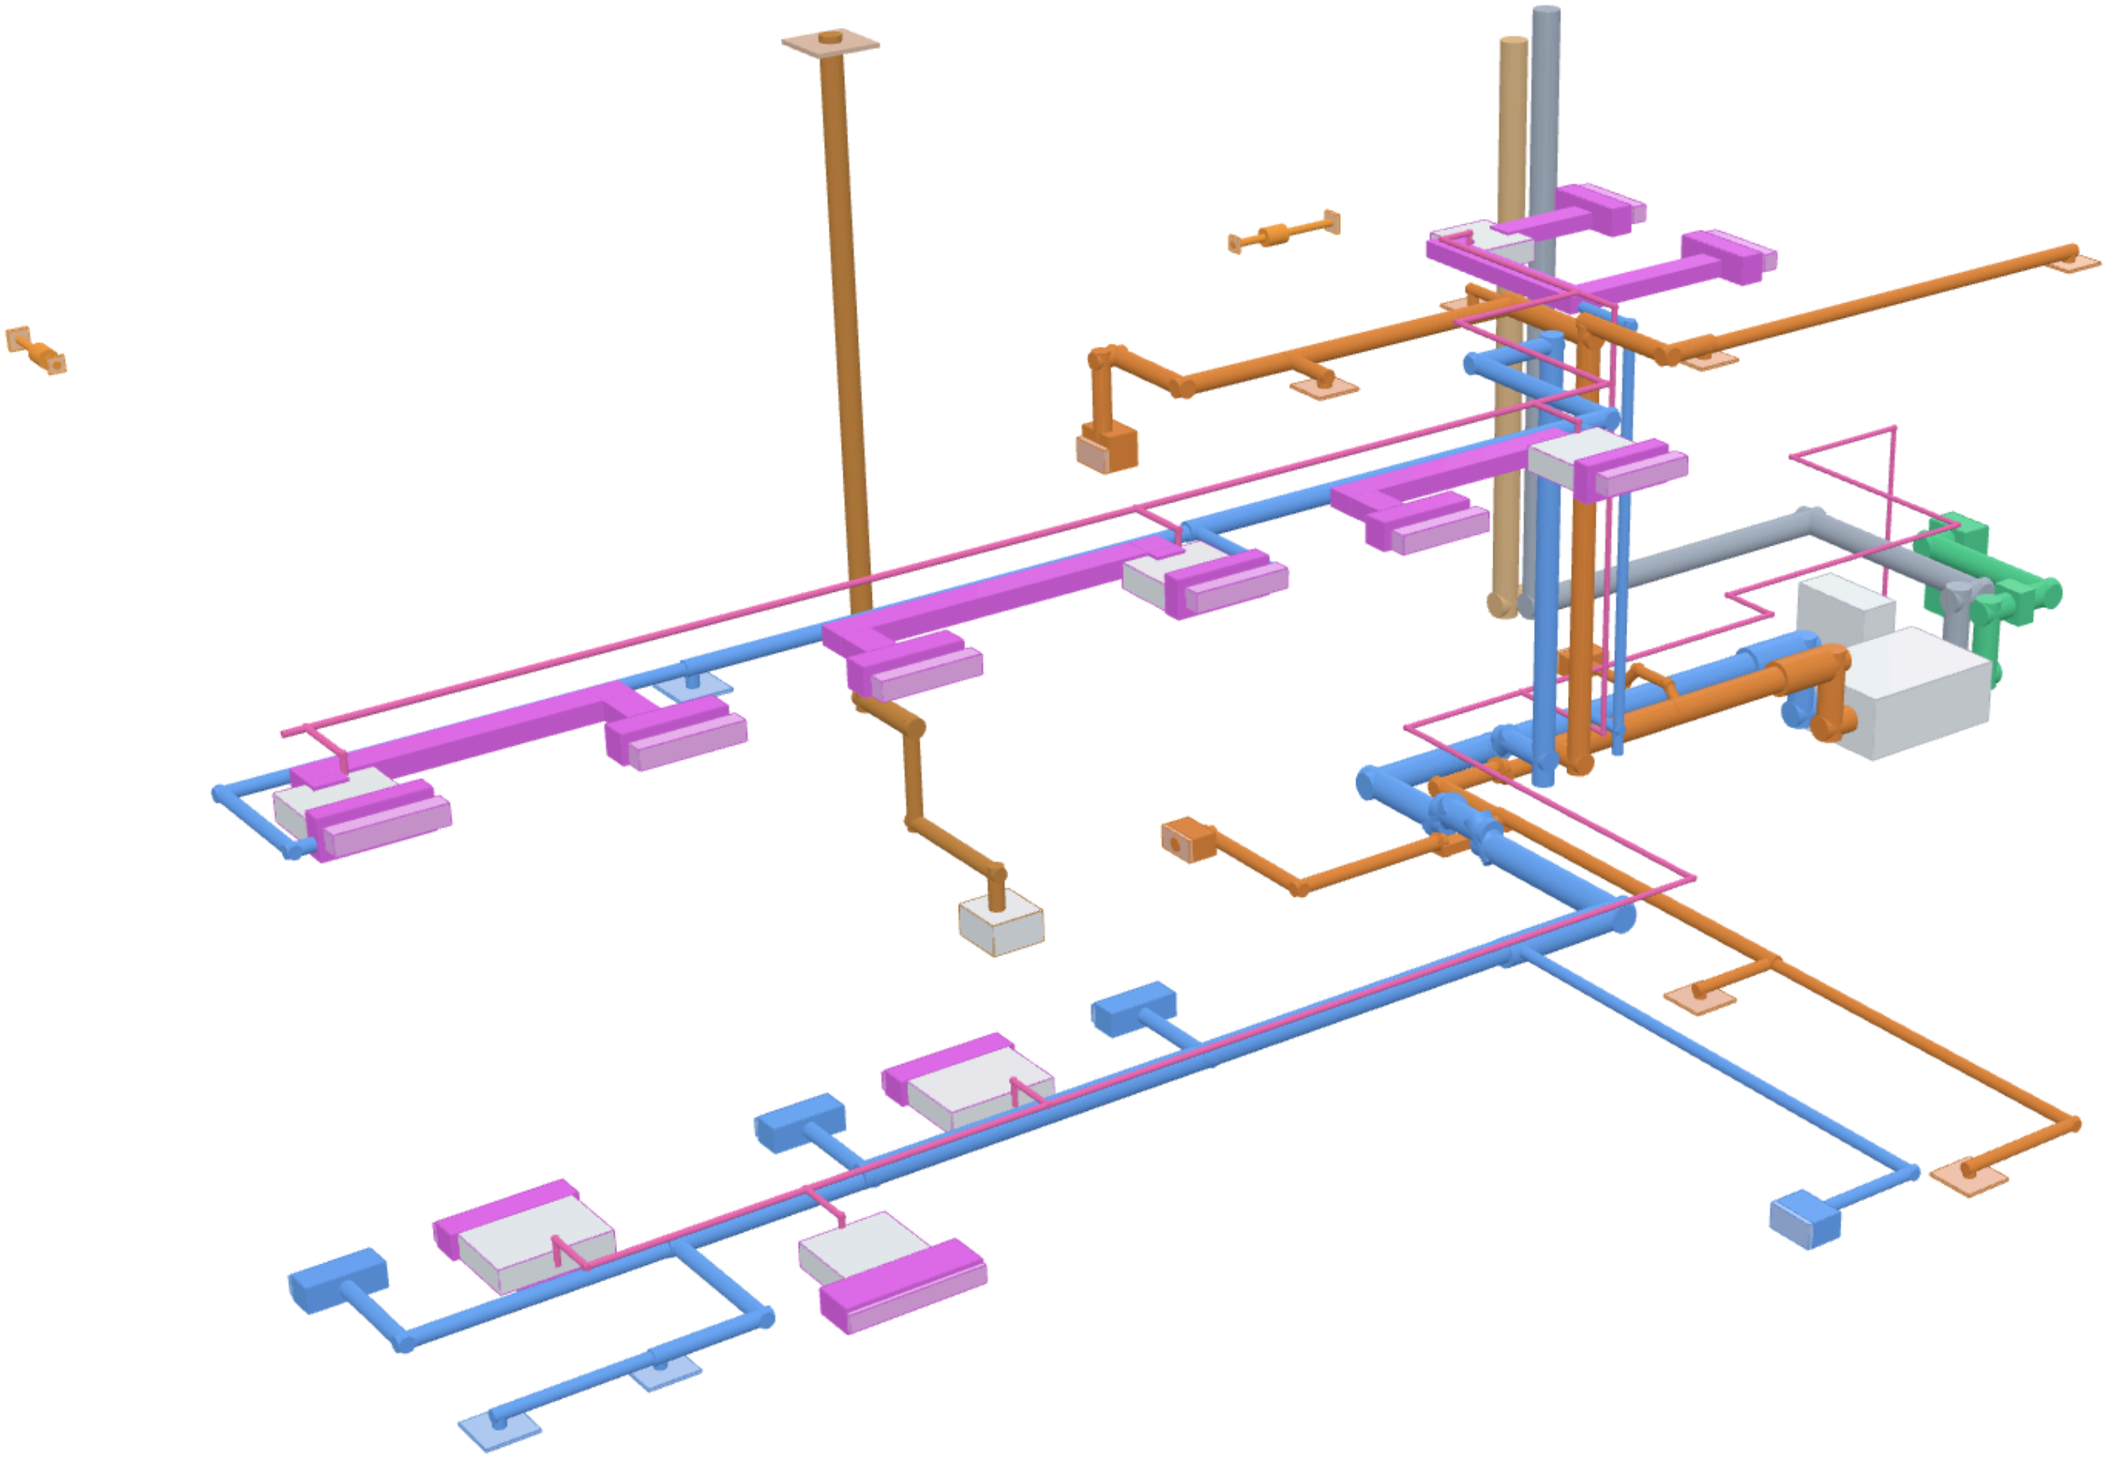

Сети П1 (приток — синий, вытяжка — оранжевый, наружный воздух — зелёный, выброс — серый), В3, В2, кондиционирование (сиреневый), фреон (розовый).

Модель по трассам листов 9–12; файлы И05.09.26-ОВ 3D (DWG, IFC, просмотр в браузере). Дренаж конденсата — по листам 9, 10.


И05.09.26-ОВ. Вентиляция и кондиционирование дома. 3D-модель — Вид с востока

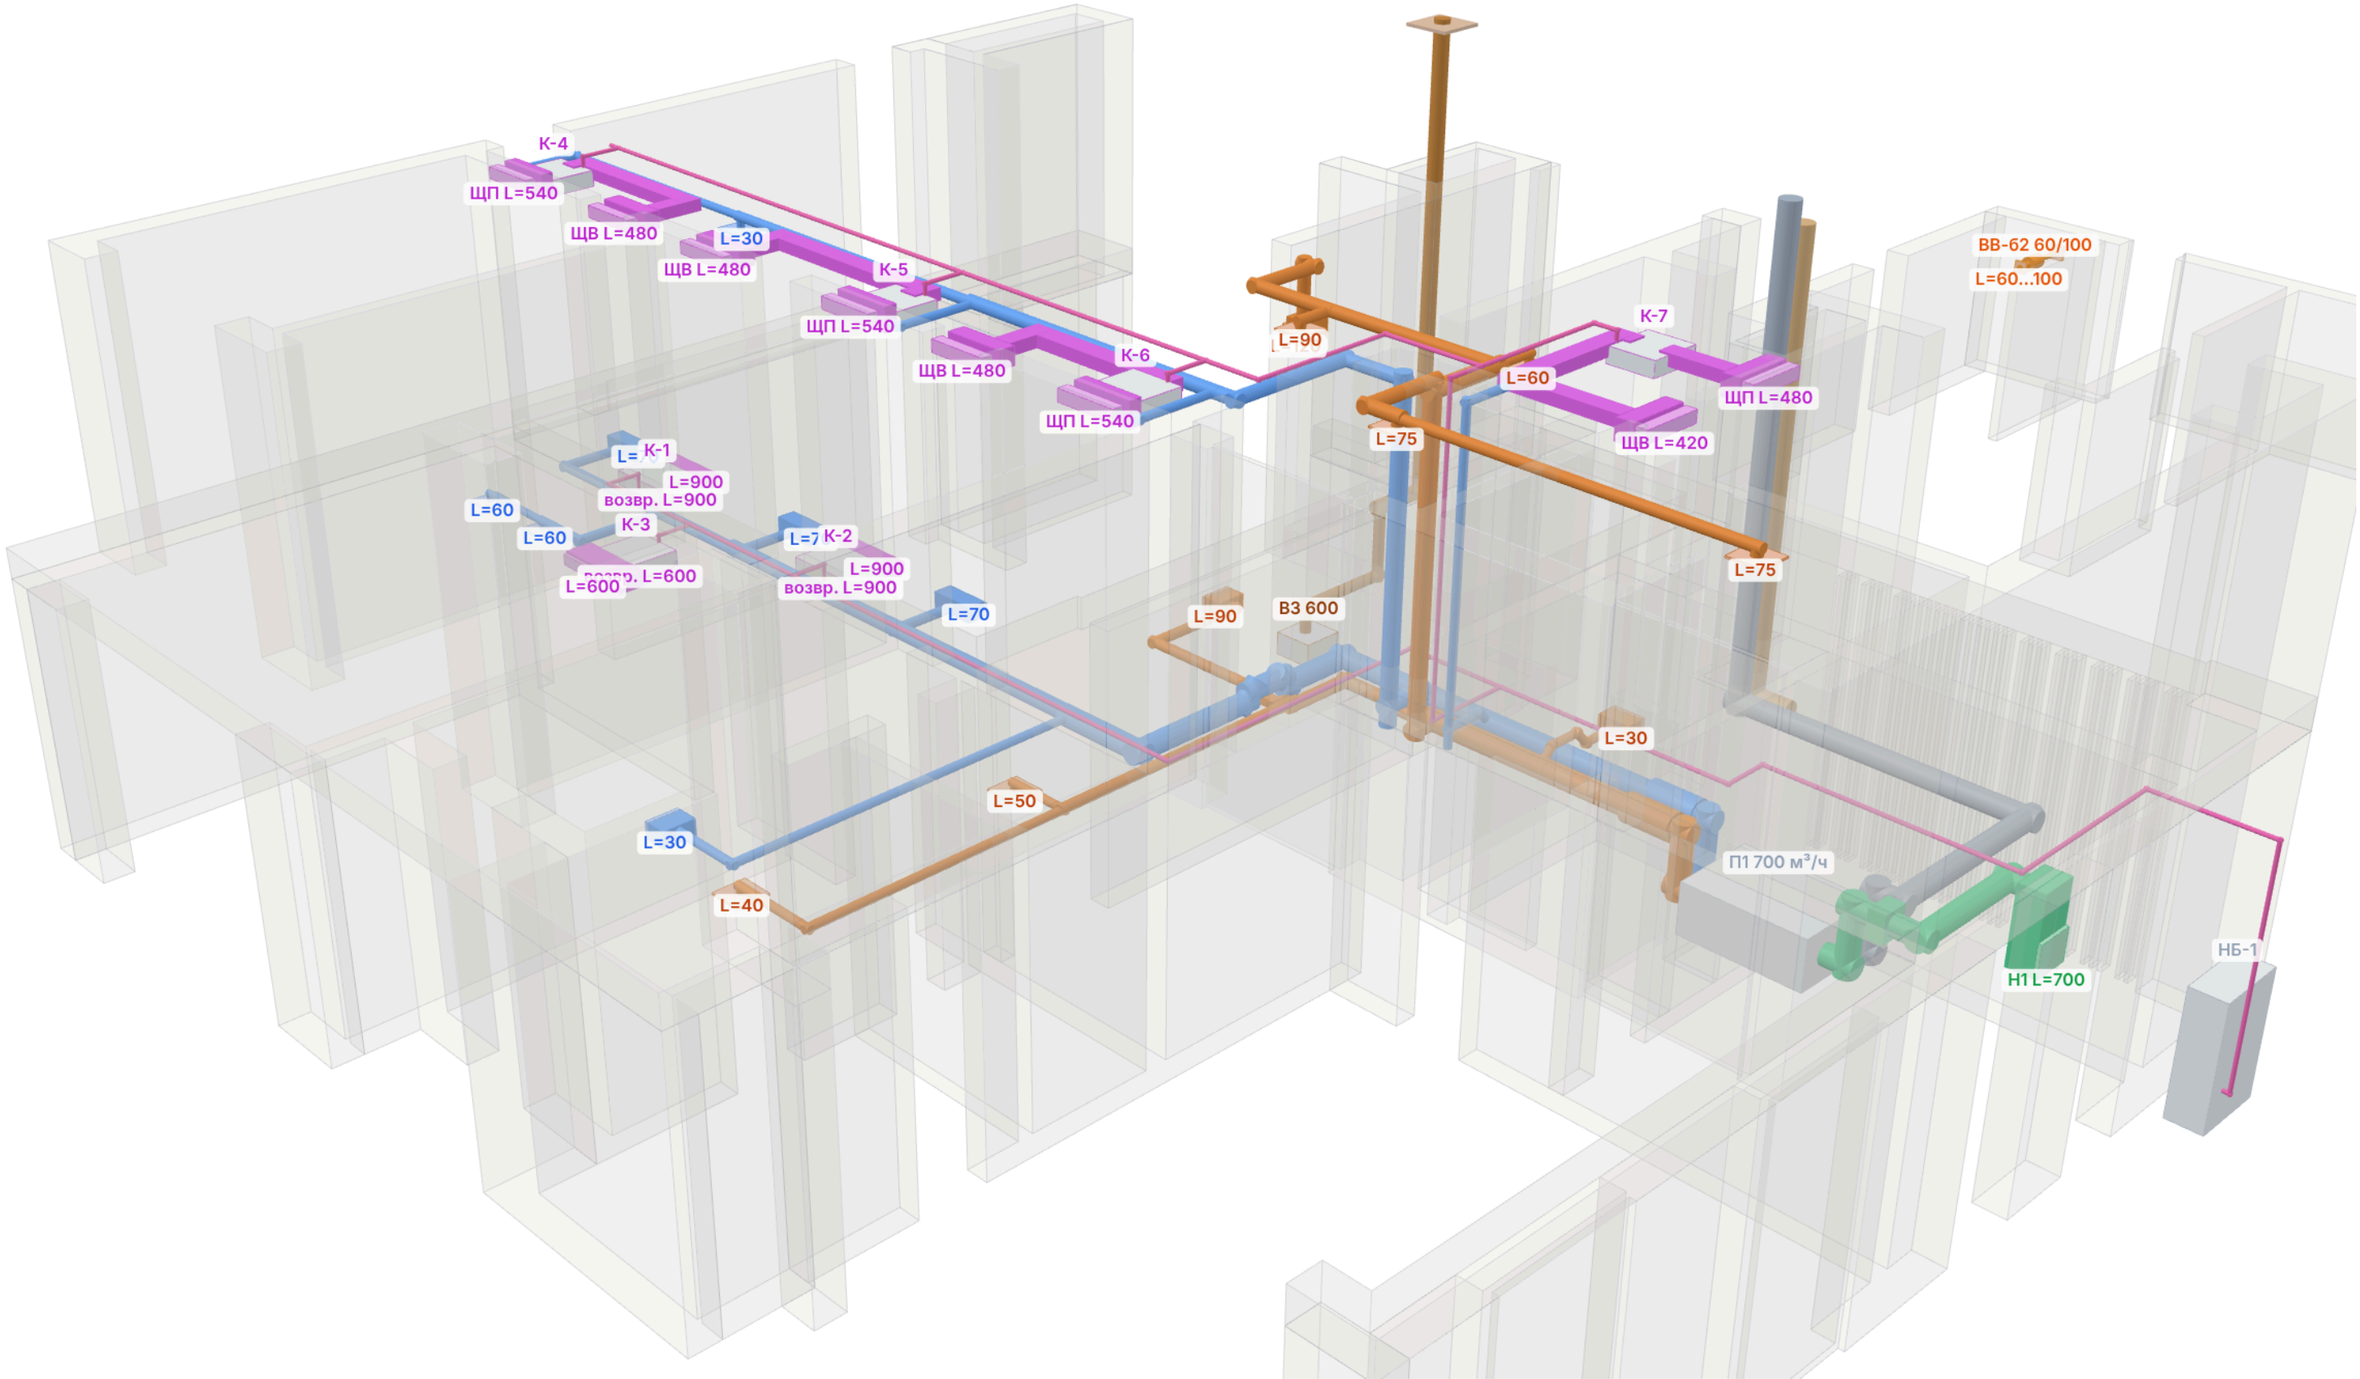

Топочная с П1, шахты Ш-1 и Ш-2, стояки на 2 этаж.

Модель по трассам листов 9–12; файлы И05.09.26-ОВ 3D (DWG, IFC, просмотр в браузере). Дренаж конденсата — по листам 9, 10.


И05.09.26-ОВ. Вентиляция и кондиционирование дома. 3D-модель — 1 этаж

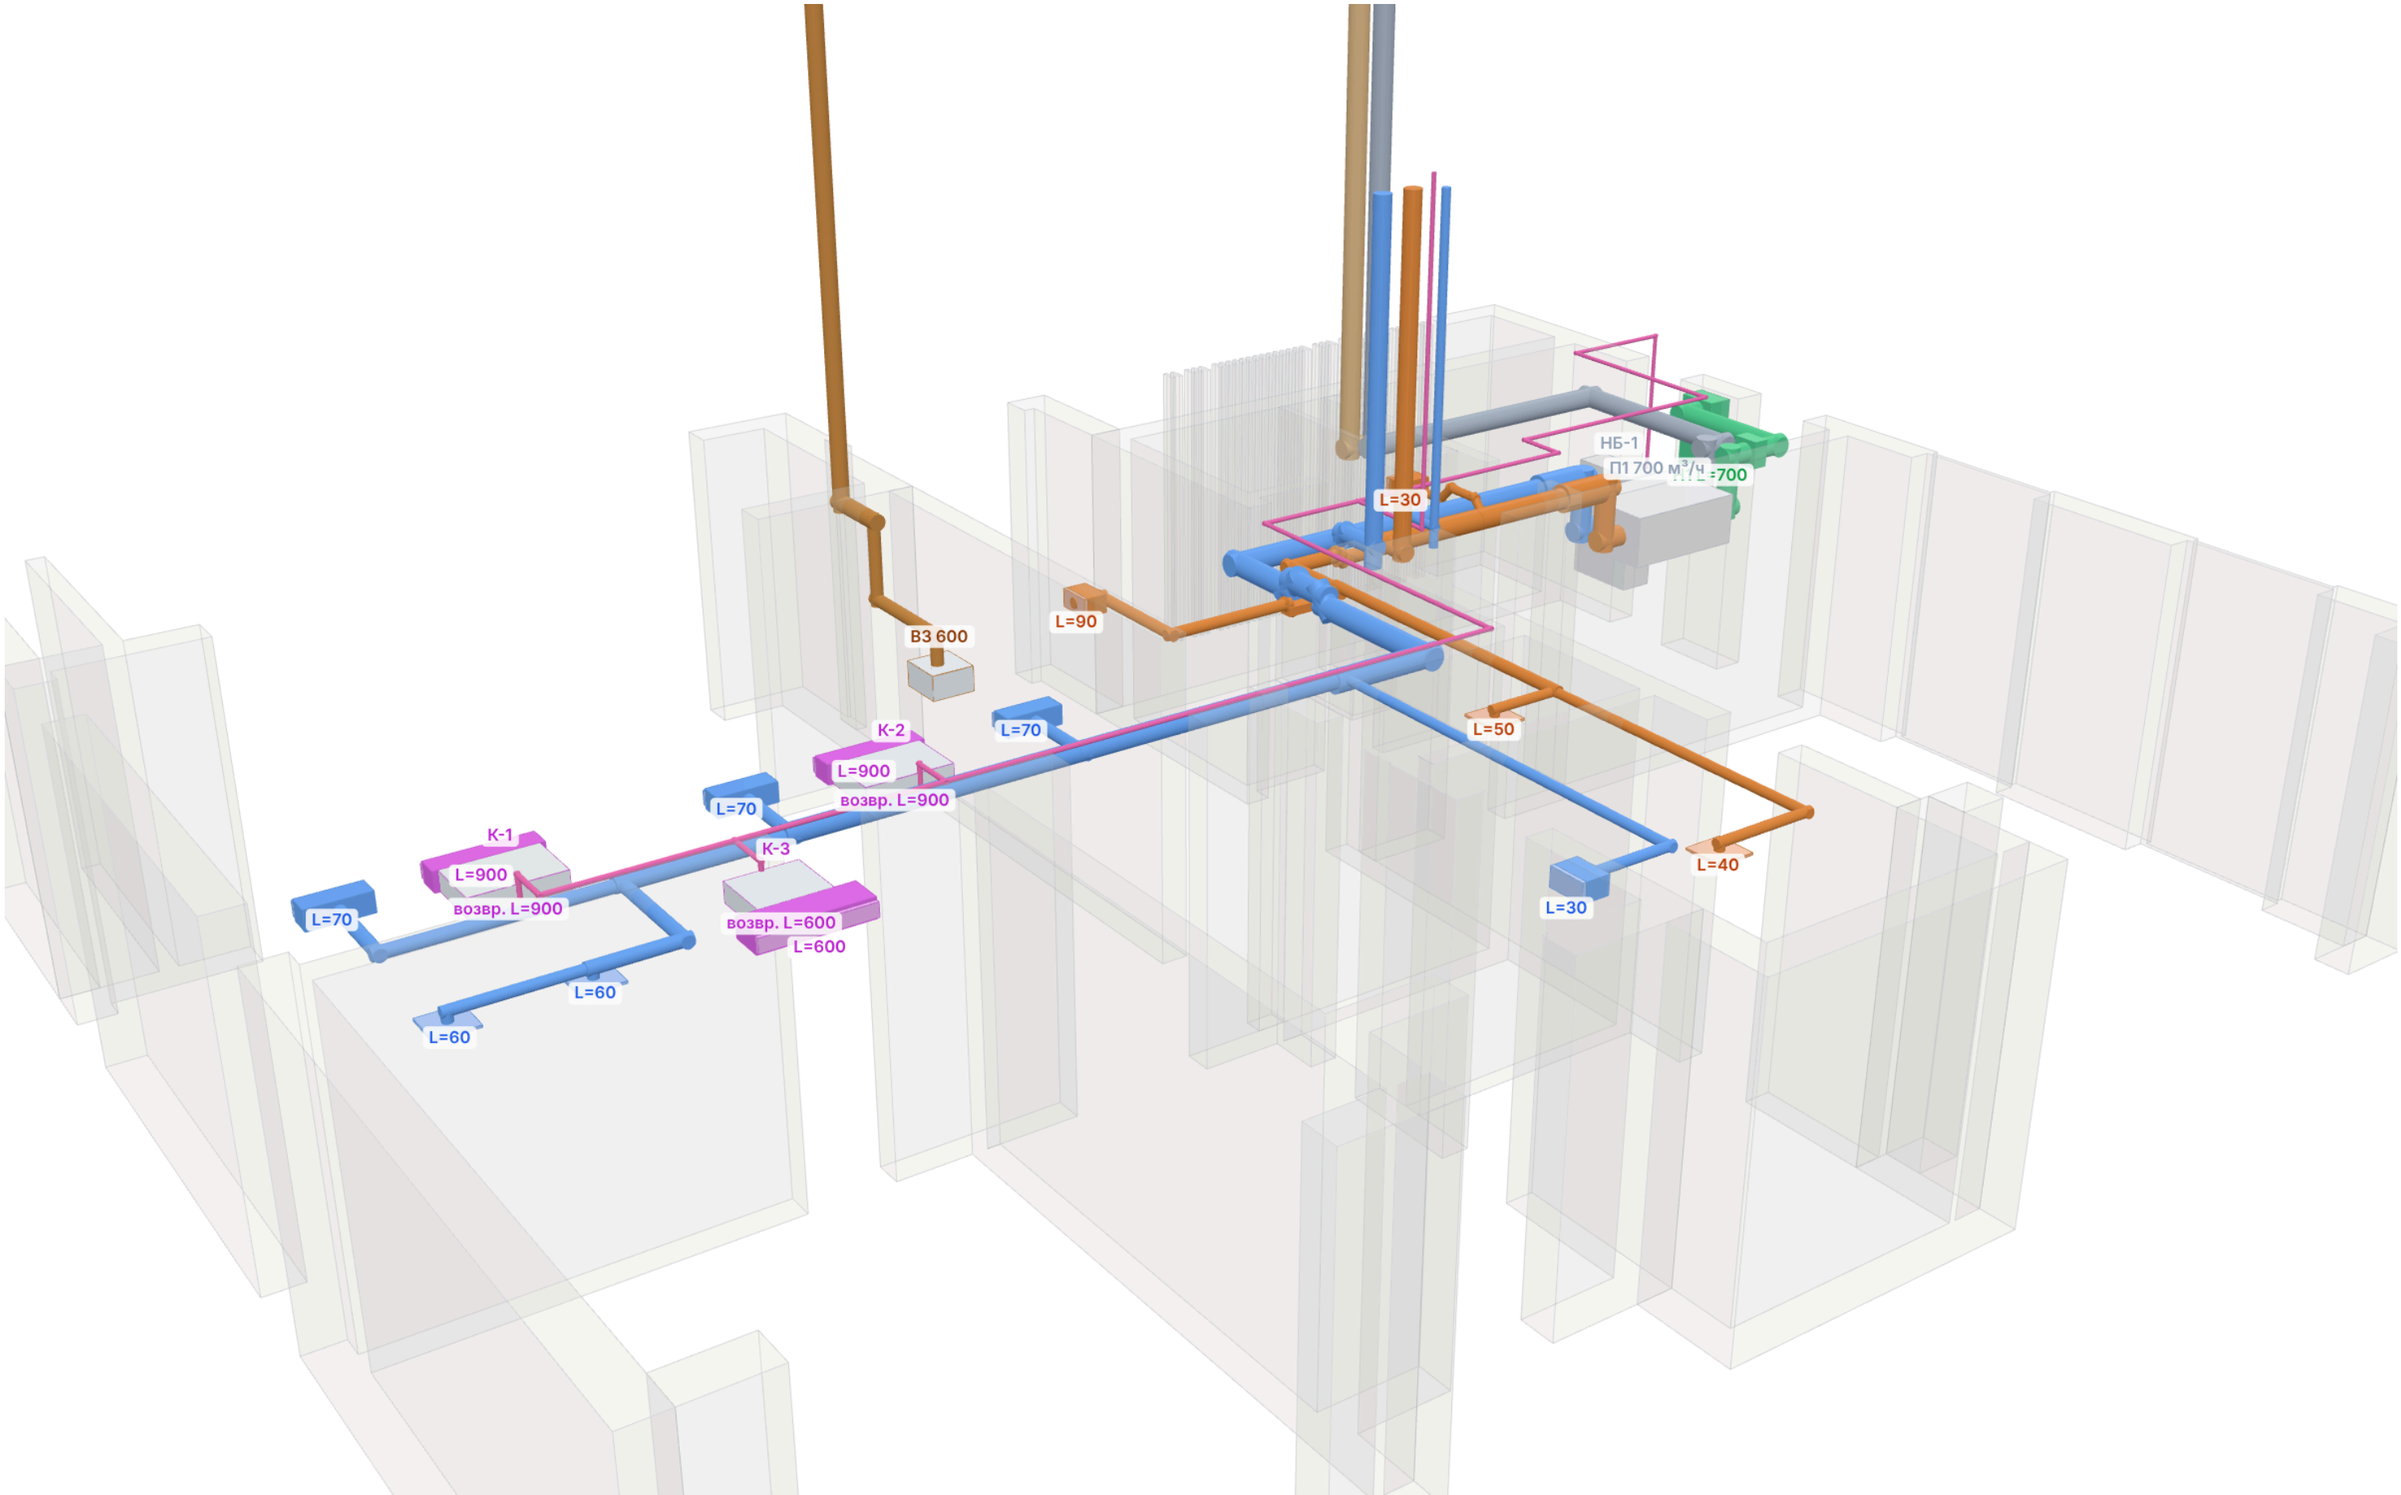

Подшивки П-1…П-5: К-1…К-3 с КСД и щелевыми диффузорами, магистрали П1, пересечения у Ш-1 разведены по высоте (лист 11).


Модель по трассам листов 9–12; файлы И05.09.26-ОВ 3D (DWG, IFC, просмотр в браузере). Дренаж конденсата — по листам 9, 10.

И05.09.26-ОВ. Вентиляция и кондиционирование дома. 3D-модель — 2 этаж

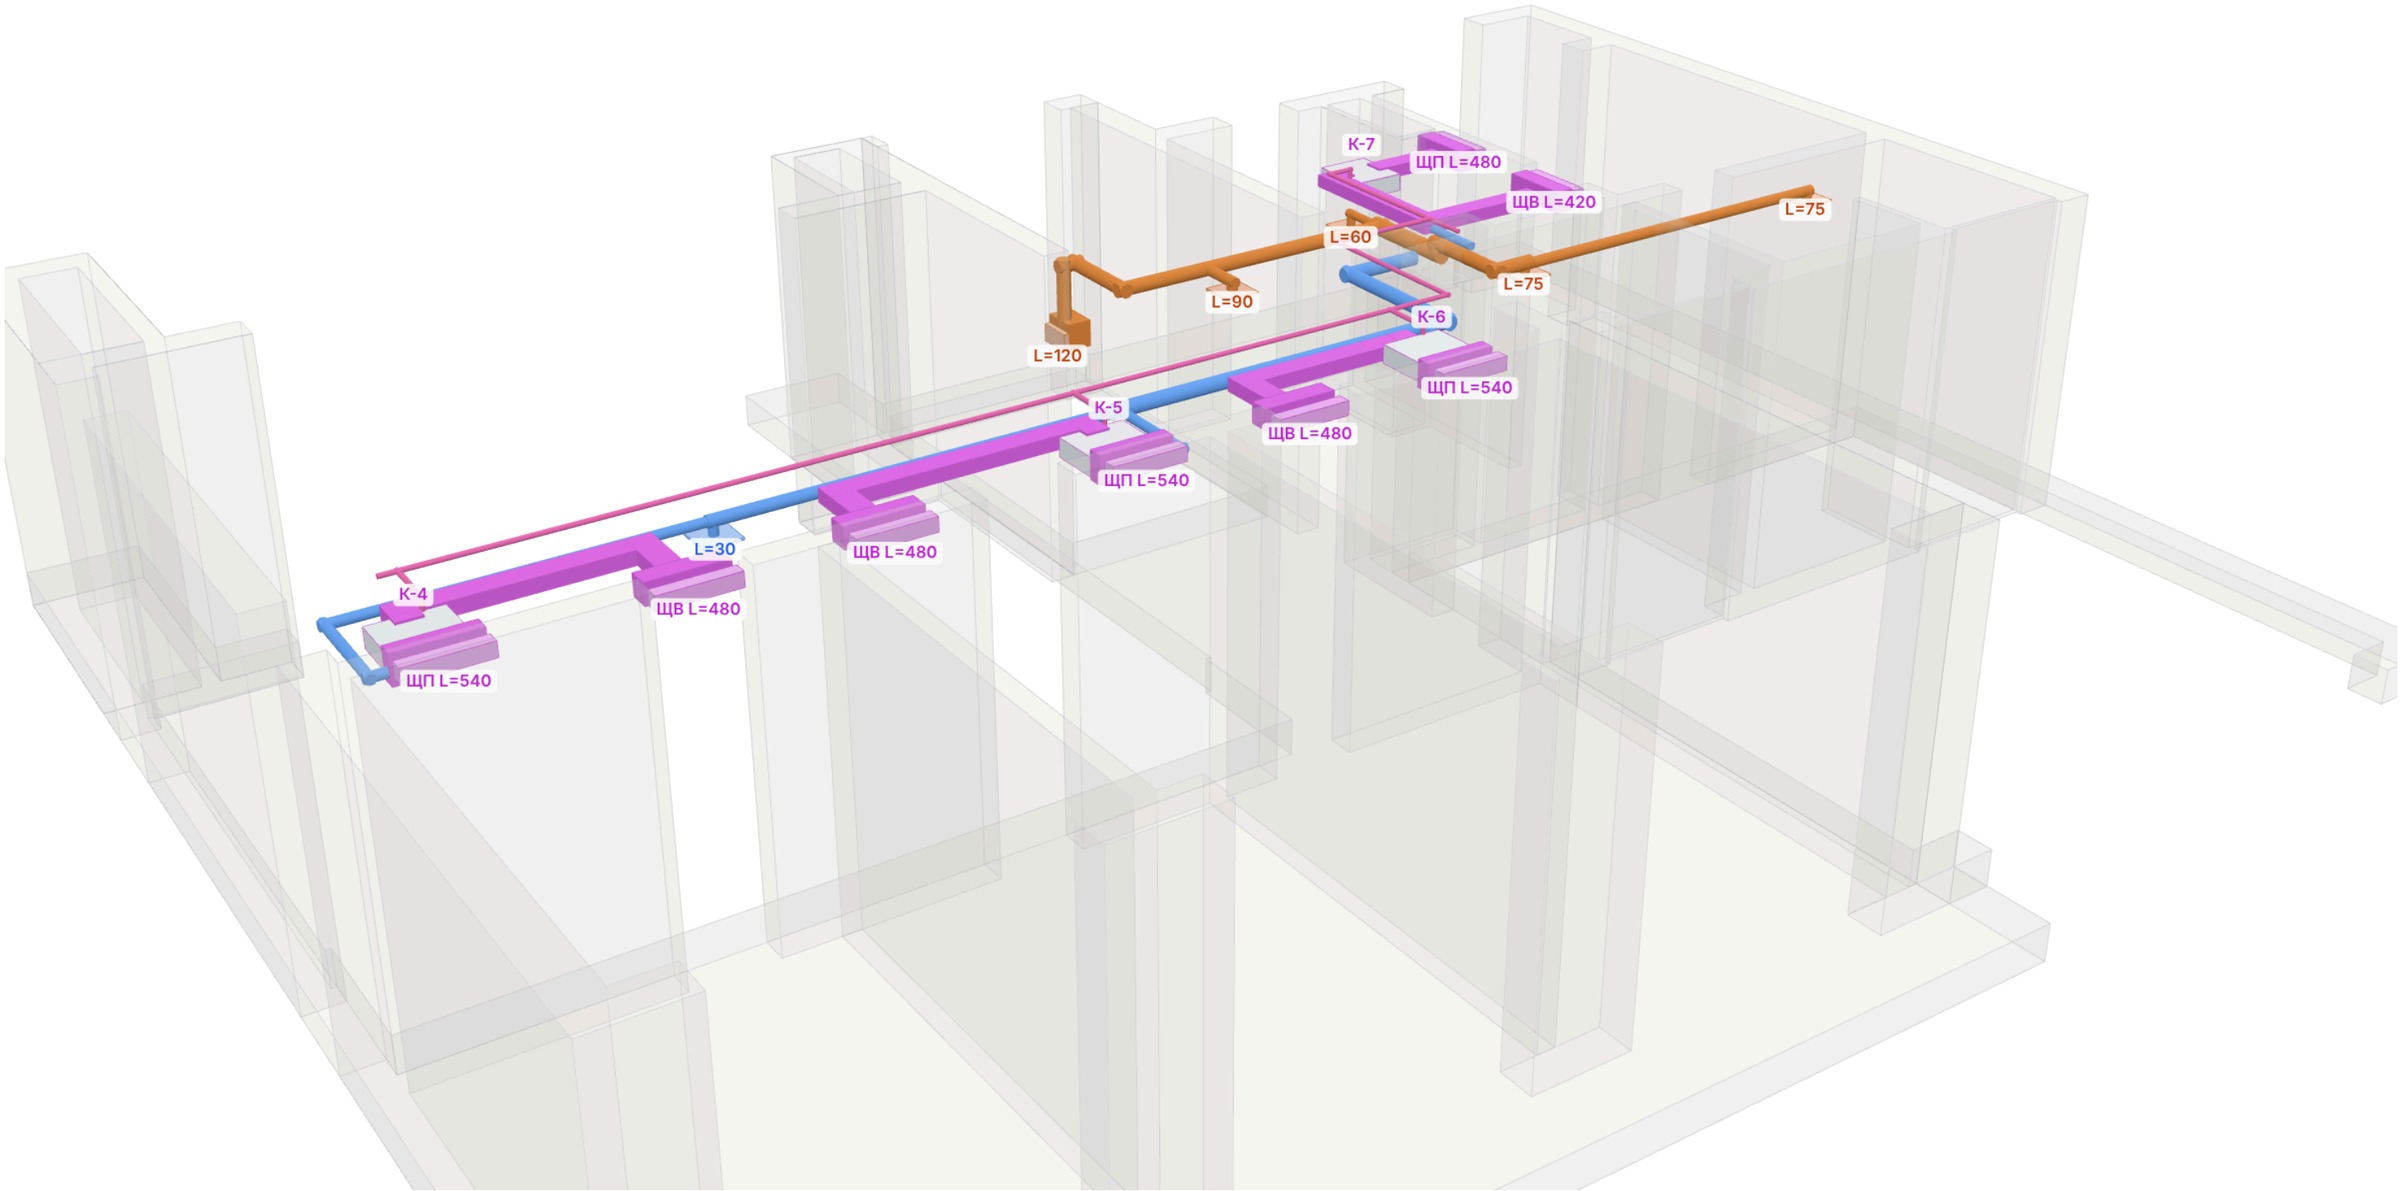

К-4…К-7: ЩП и ЩВ в стенах спален через КСД, возврат 250×150, приток и вытяжка П1.


Модель по трассам листов 9–12; файлы И05.09.26-ОВ 3D (DWG, IFC, просмотр в браузере). Дренаж конденсата — по листам 9, 10.

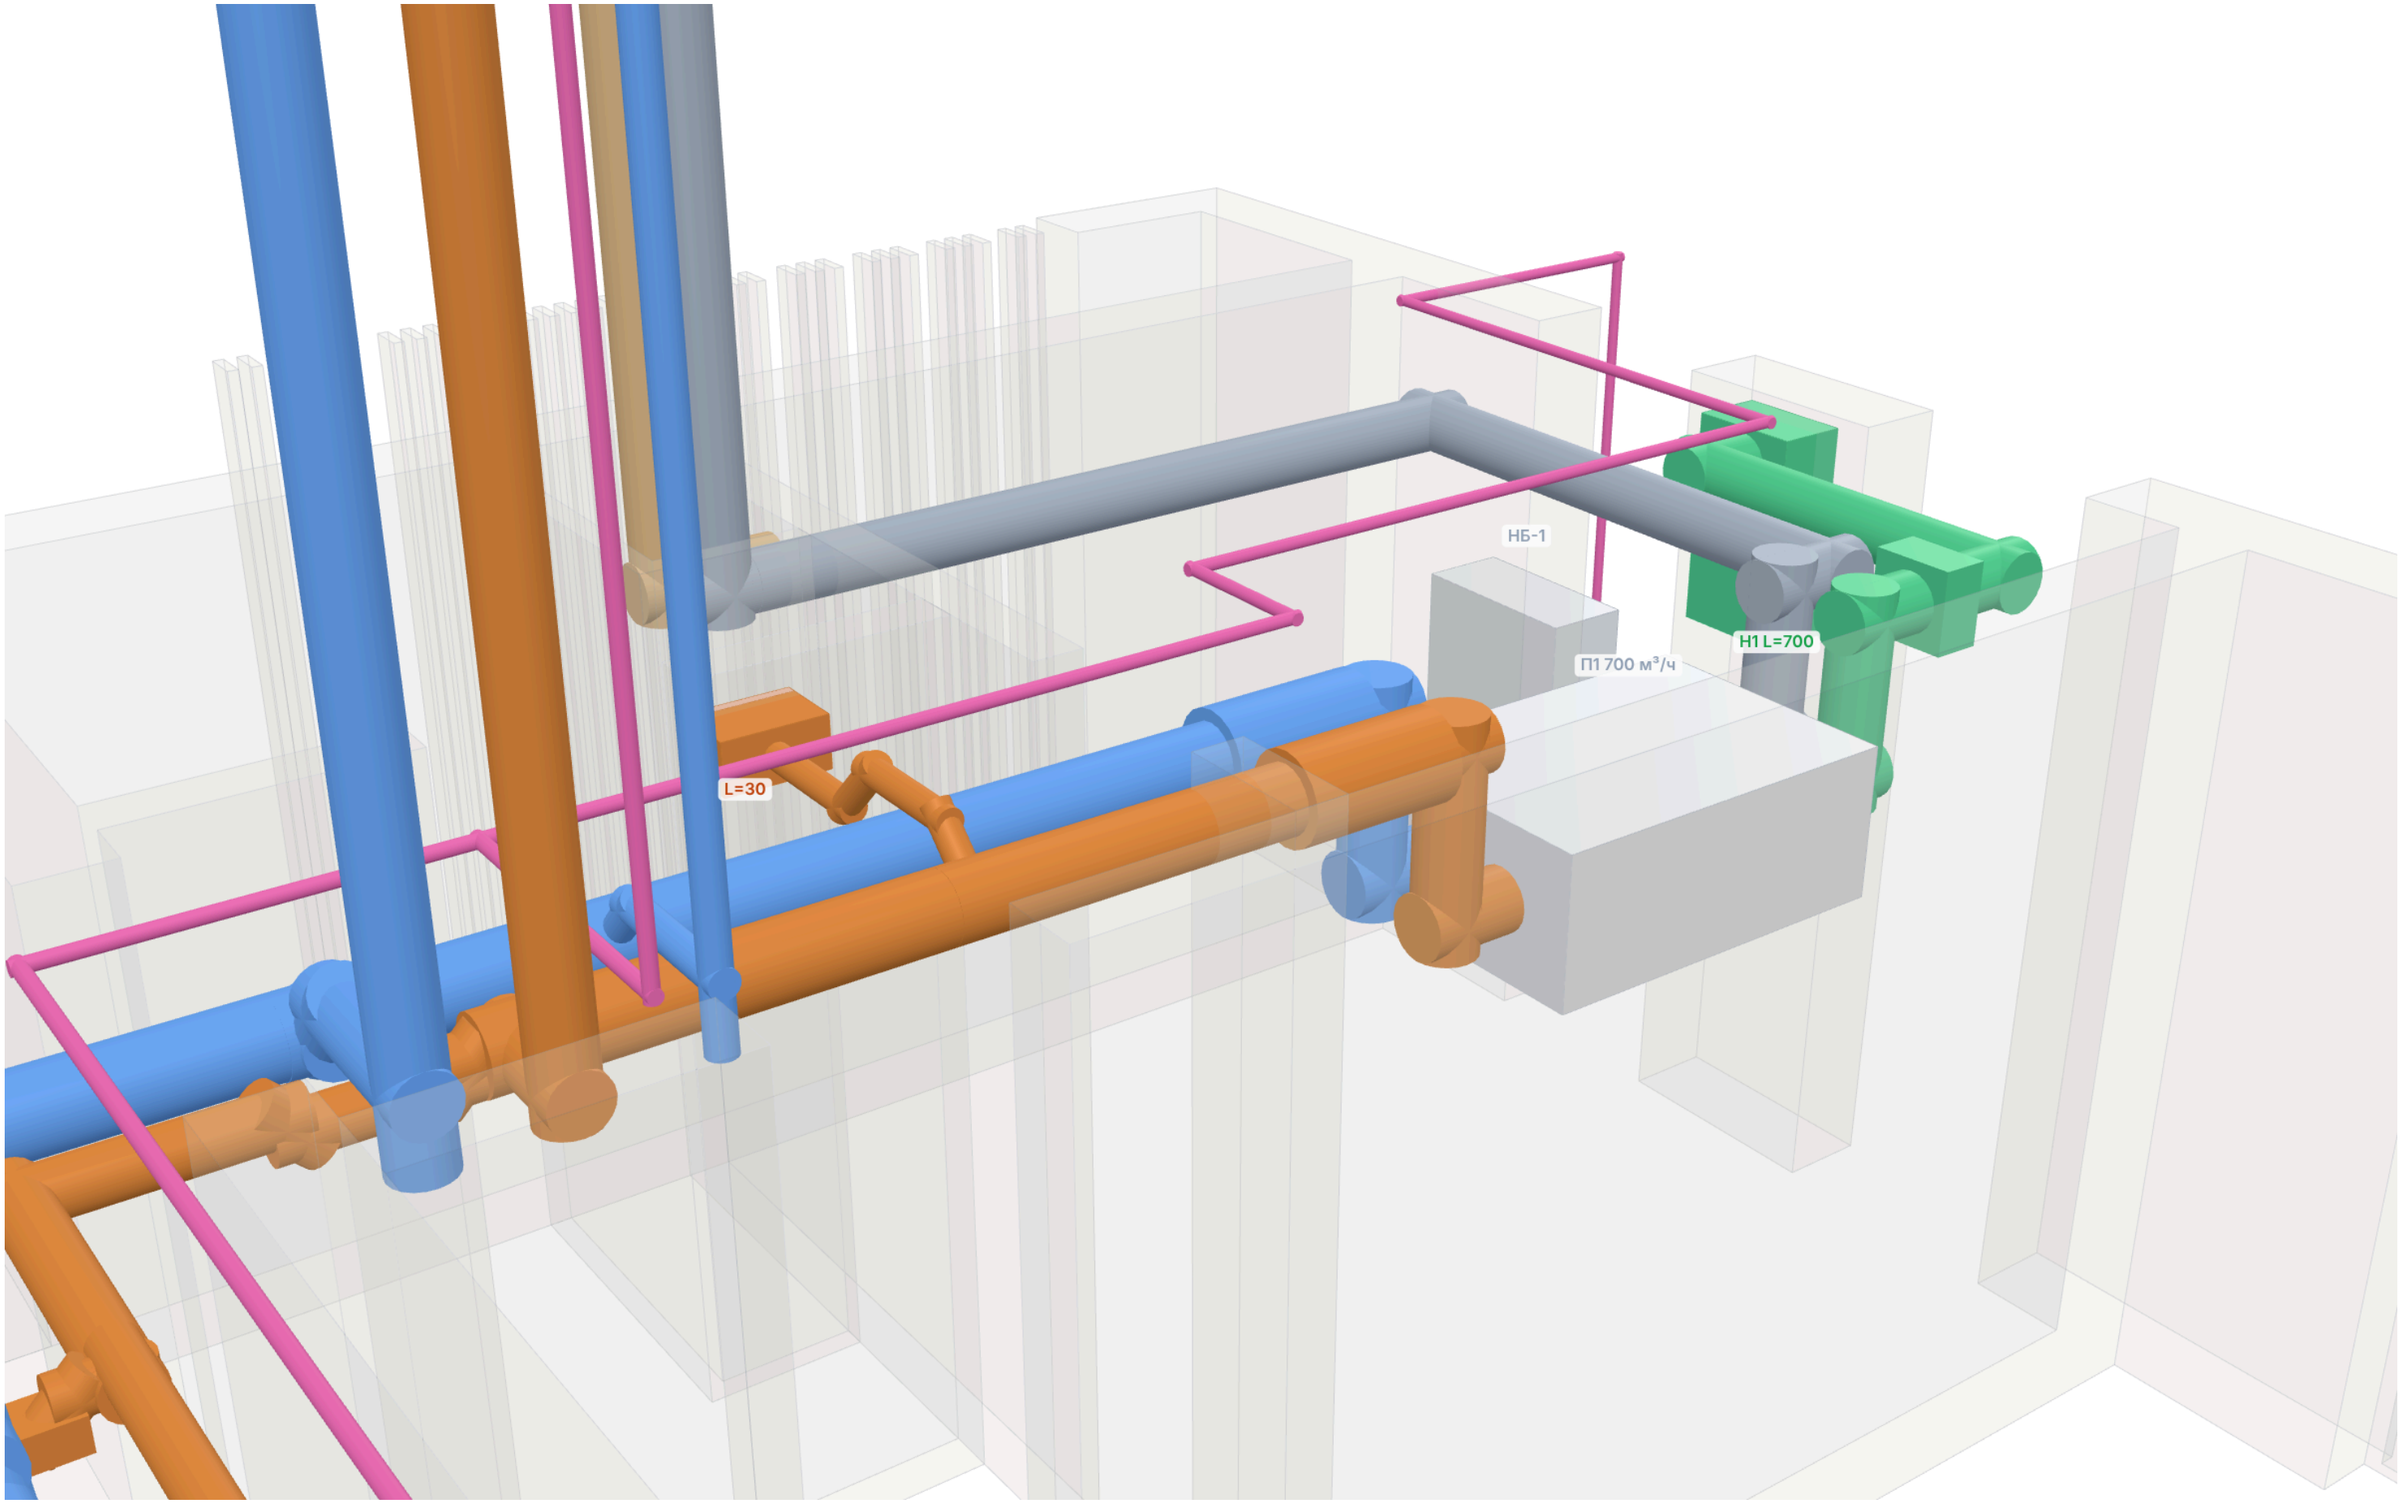

П1 Turkov Zenit 750 Heco W, шумоглушители, клапан КВ-Н, наружный воздух от Н1, выброс в Ш-2.


Модель по трассам листов 9–12; файлы И05.09.26-ОВ 3D (DWG, IFC, просмотр в браузере). Дренаж конденсата — по листам 9, 10.

И05.09.26-ОВ. Вентиляция и кондиционирование дома. 3D-модель — Вид сверху

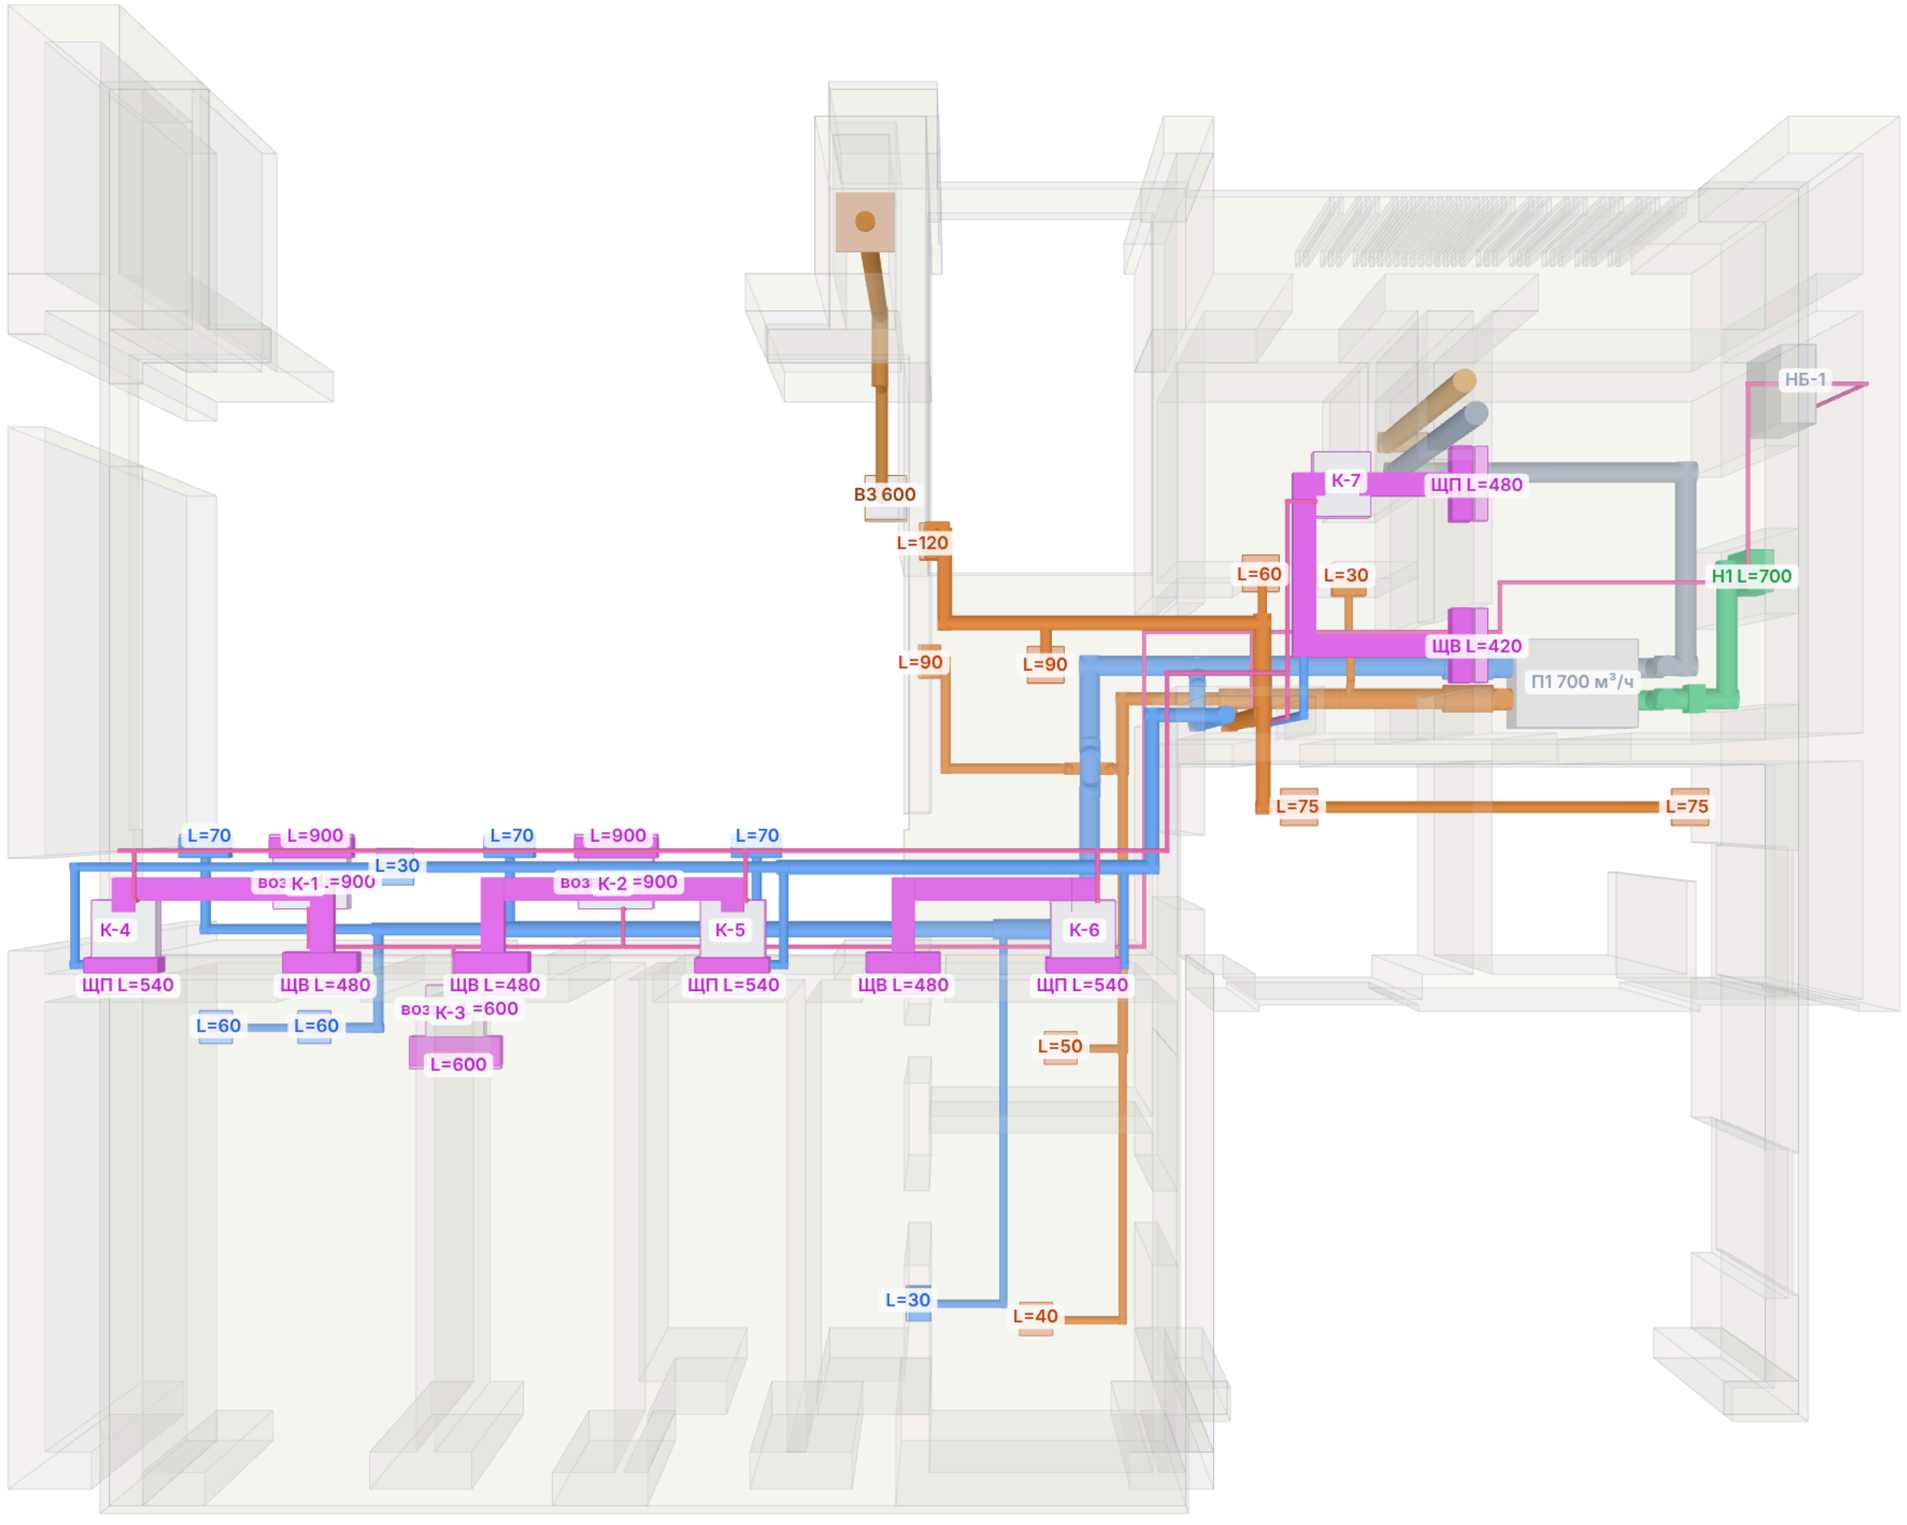


Начало координат — пересечение осей 1/А.

Модель по трассам листов 9–12; файлы И05.09.26-ОВ 3D (DWG, IFC, просмотр в браузере). Дренаж конденсата — по листам 9, 10.

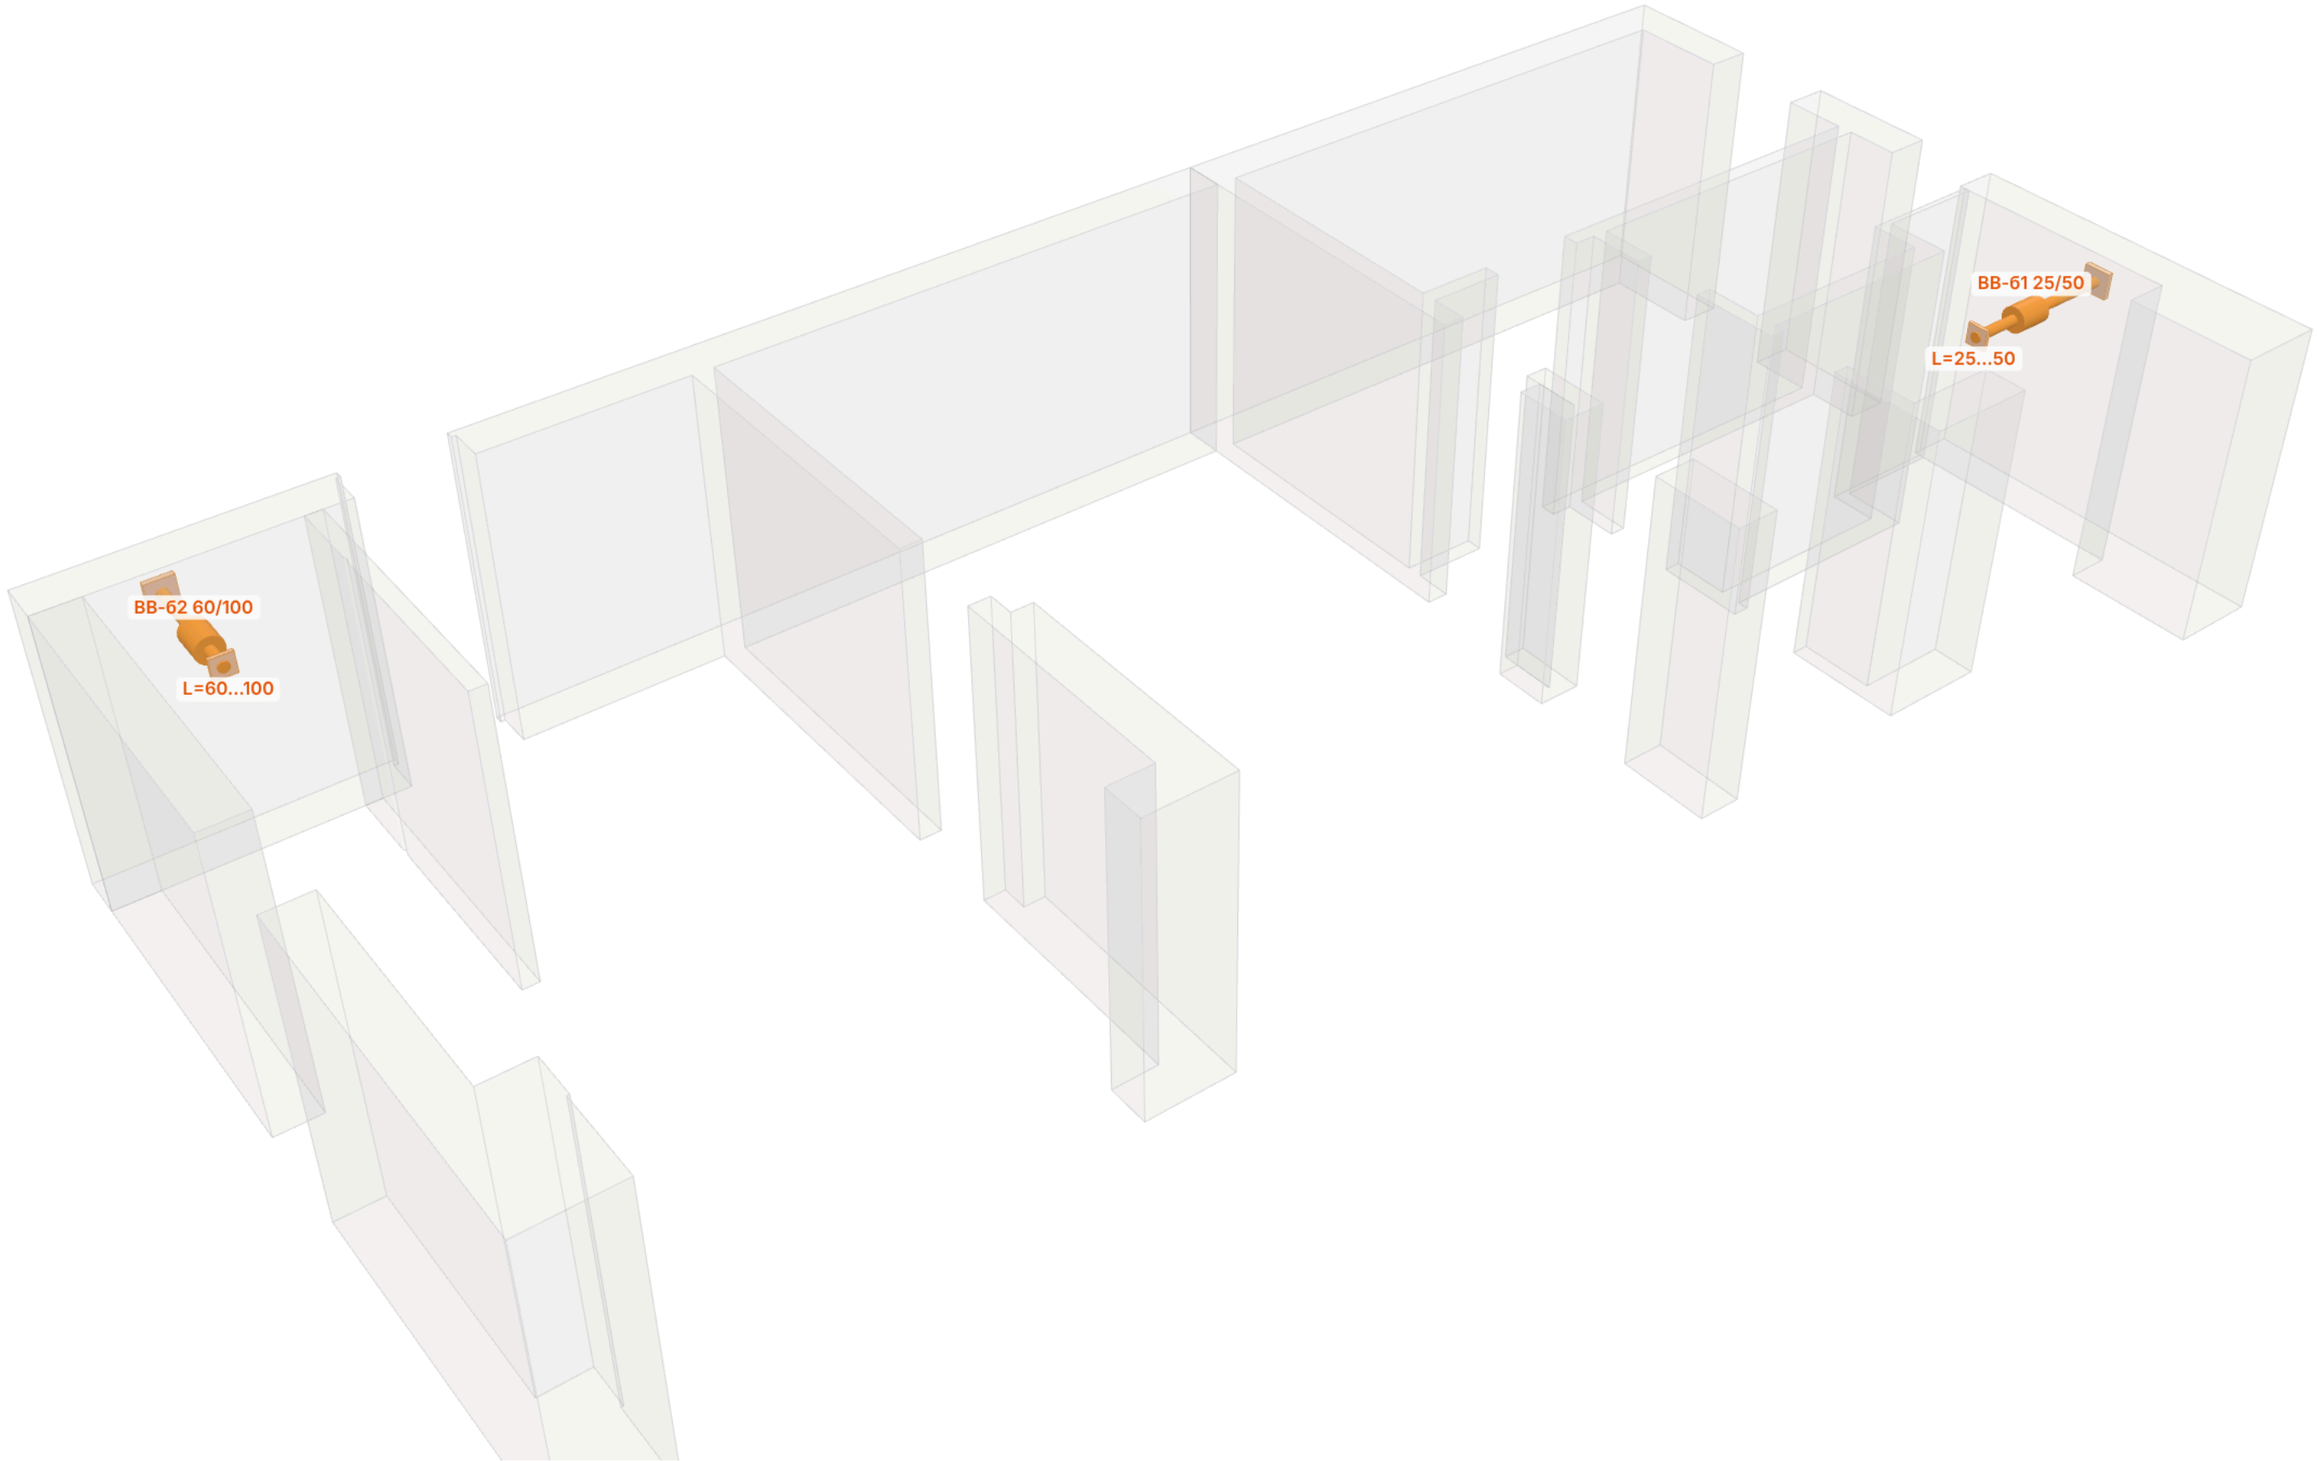

ВВ-б1 (с/у б3) и ВВ-б2 (помывочная б7): решётка под потолком, канальный вентилятор Ø100, проход в наружной стене, ось +2,200 (лист 12). Стены — по АР4.

Модель по трассам листов 9–12; файлы И05.09.26-ОВ 3D (DWG, IFC, просмотр в браузере). Дренаж конденсата — по листам 9, 10.

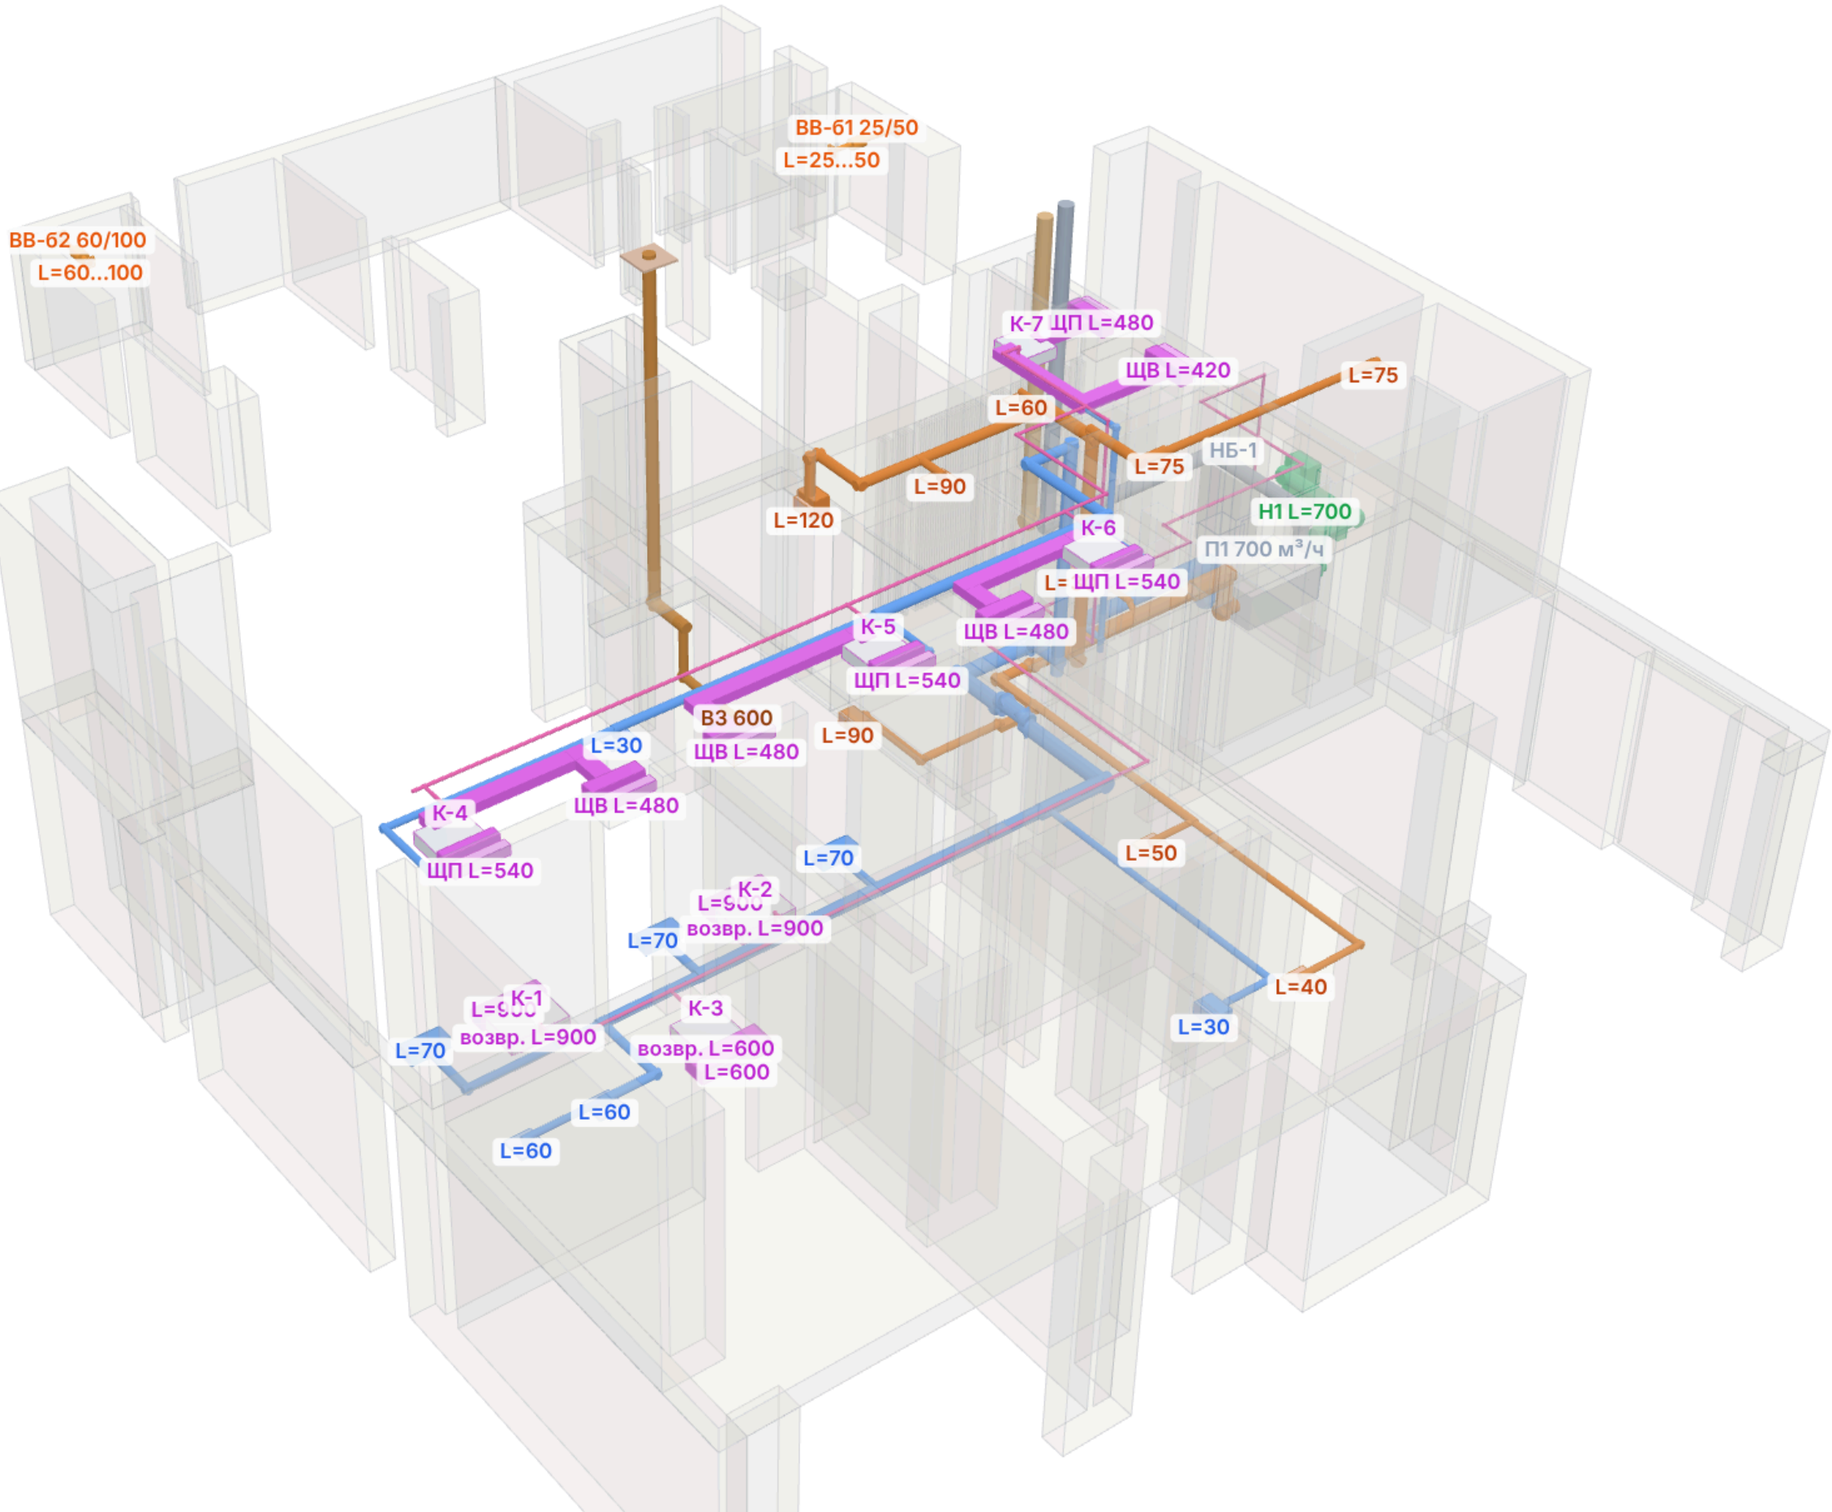

Баня — по ГП01: оси 1/А бани в 7,132 м восточнее и 25,000 м севернее осей 1/А дома.

Модель по трассам листов 9–12; файлы И05.09.26-ОВ 3D (DWG, IFC, просмотр в браузере). Дренаж конденсата — по листам 9, 10.