


1-1

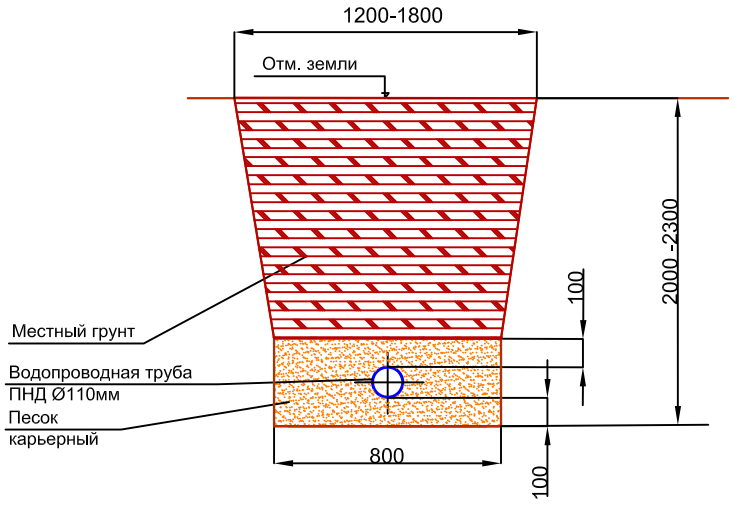


2-2

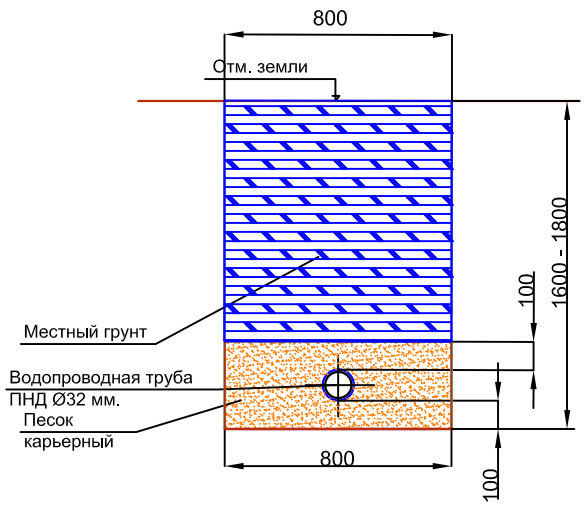


Ситуационный план:

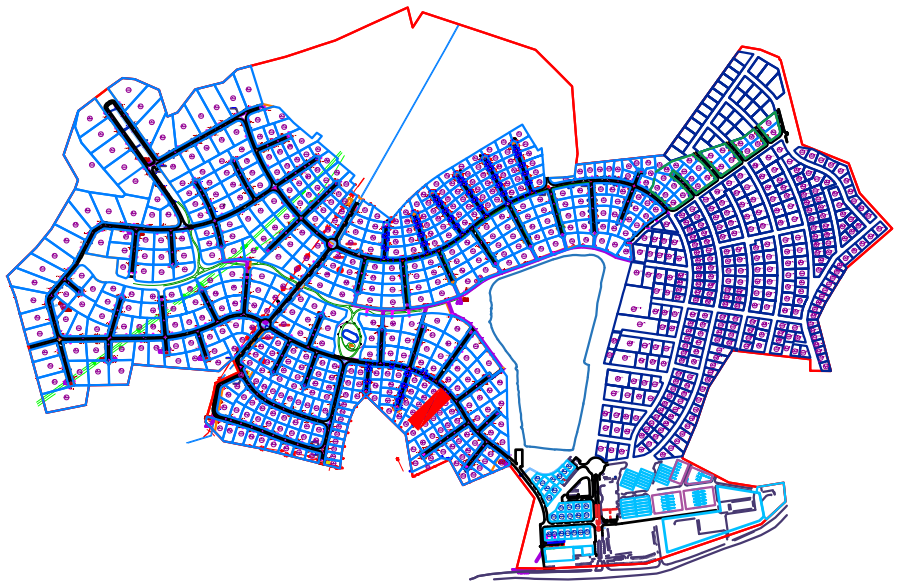

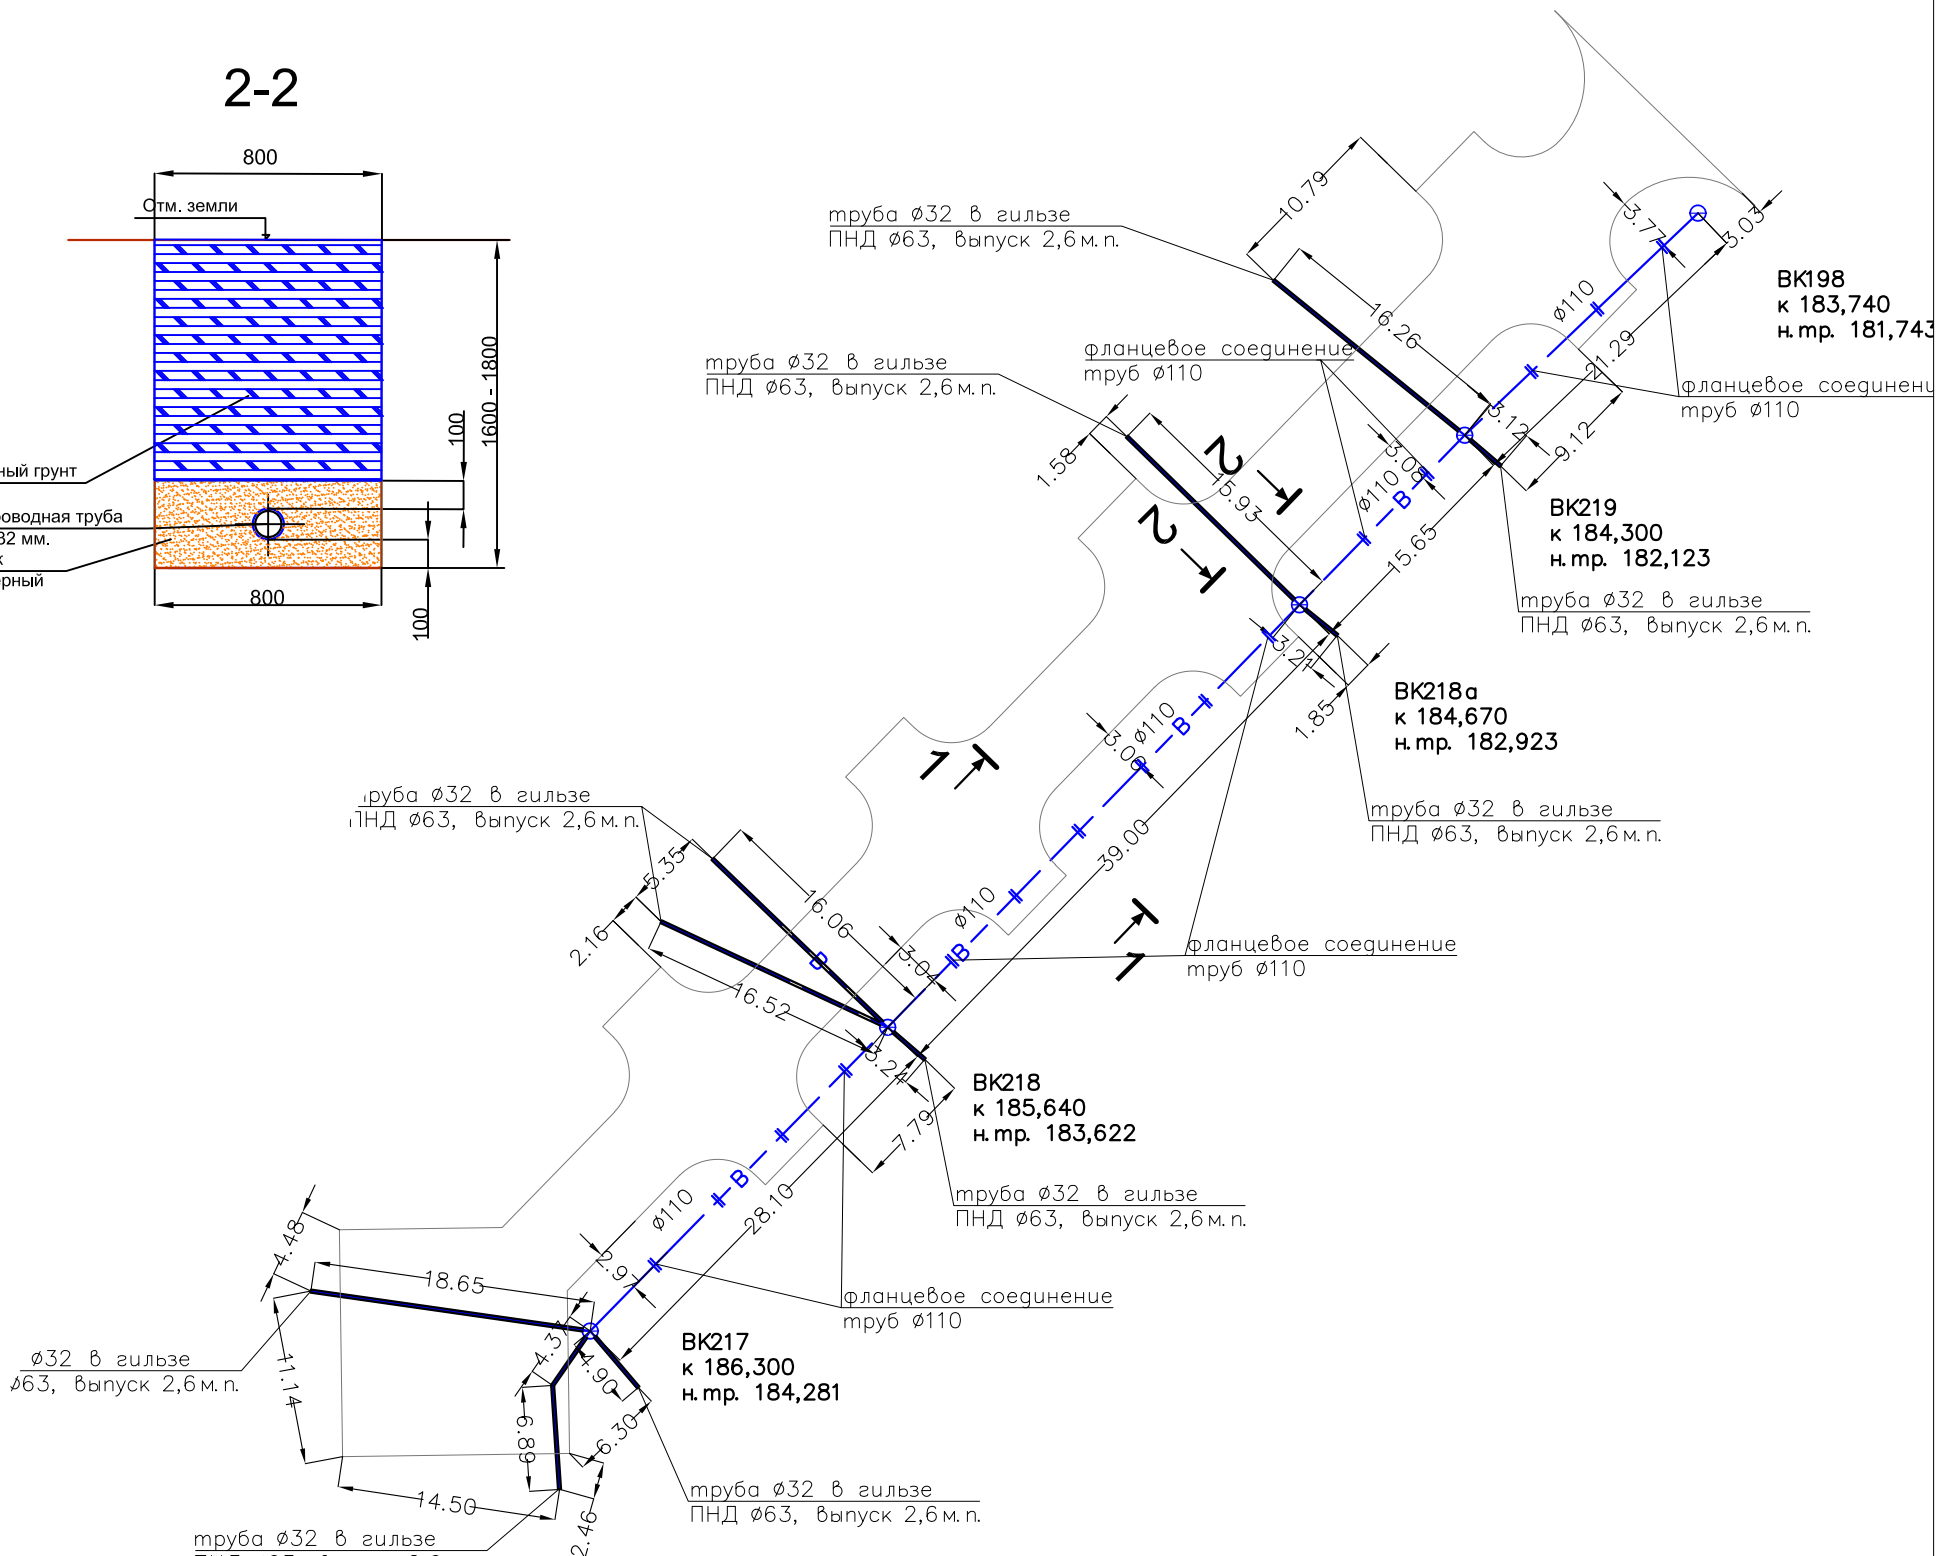

Типовой конструктив сборного Ж/Б колодца

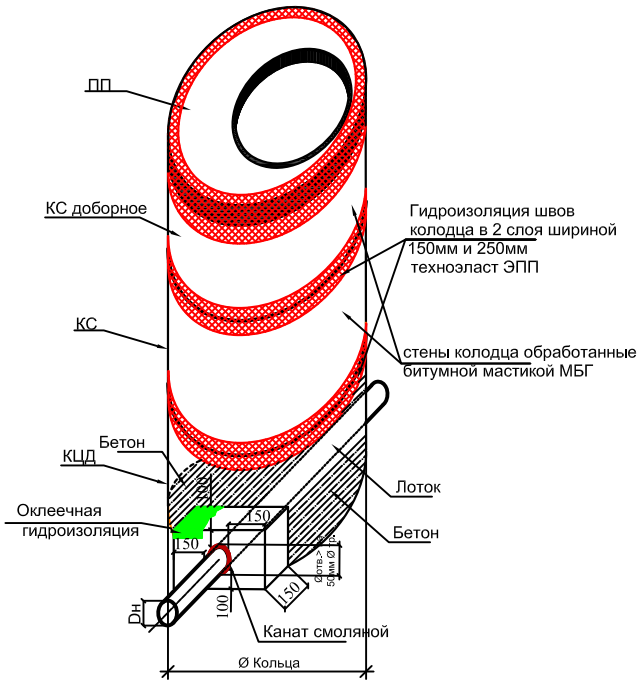

Ведомость расхода материалов:

– труба ø32 мм.: 18,65+2,6+4,9+2,6+4,37+6,89
+2,6+16,52+2,6+16,06+2,6
+3,24+2,6+15,93+2,6+3,21

+2,6+16,26+2,6+3,12+2,6=135,15 м. п.

– гильза ПНД ø63: 135,15 м. п.

– труба ø110 мм.: 104,04 м. п.

– фланцевое соединение труб ø110 мм.: 15 шт.

				ИС–3 ВК–30V		
				Московская область, городской округ Истра, с/п. Павло– Слободское, д. Исаково.		
Должность	Ф. И. О.	Подпись	Дата			
				Устройства трубопровода	стадия	лист	листов
геодезист	Голубев П. В.				ИД	4	8
				от колодца ВК217 до ВК198 план, разрезы	ООО "Лика"		