


Ситуационный план:

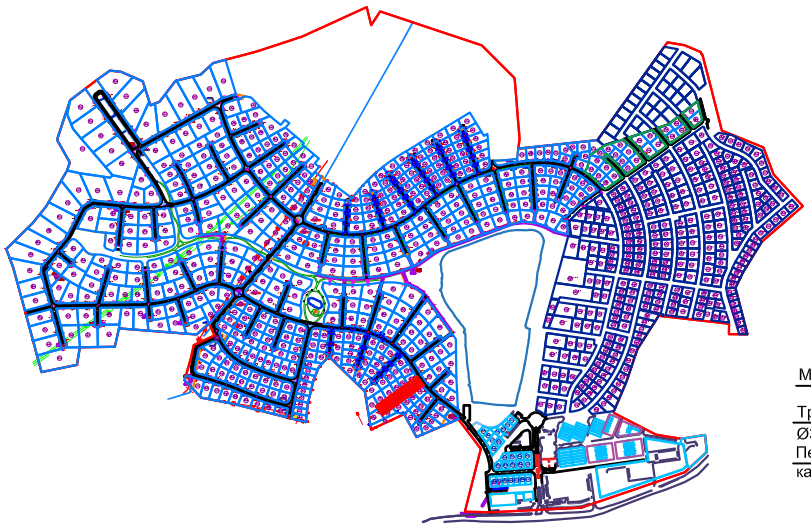


1-1

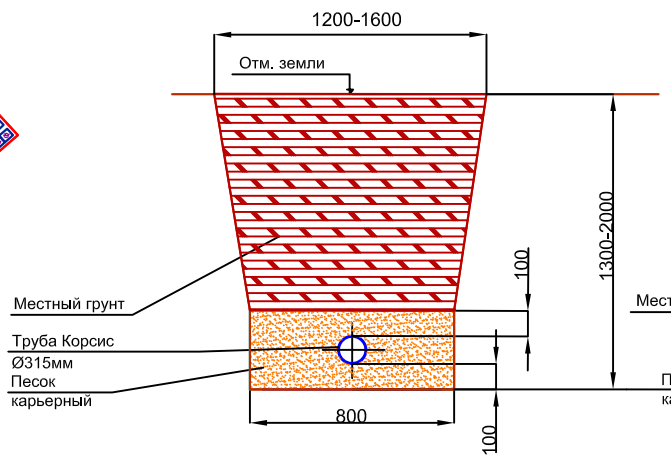


2-2

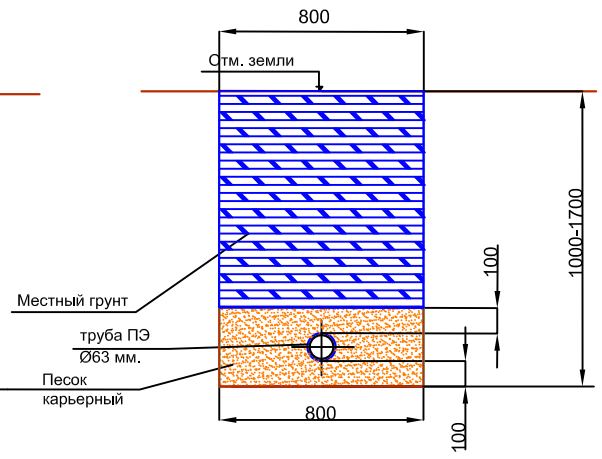

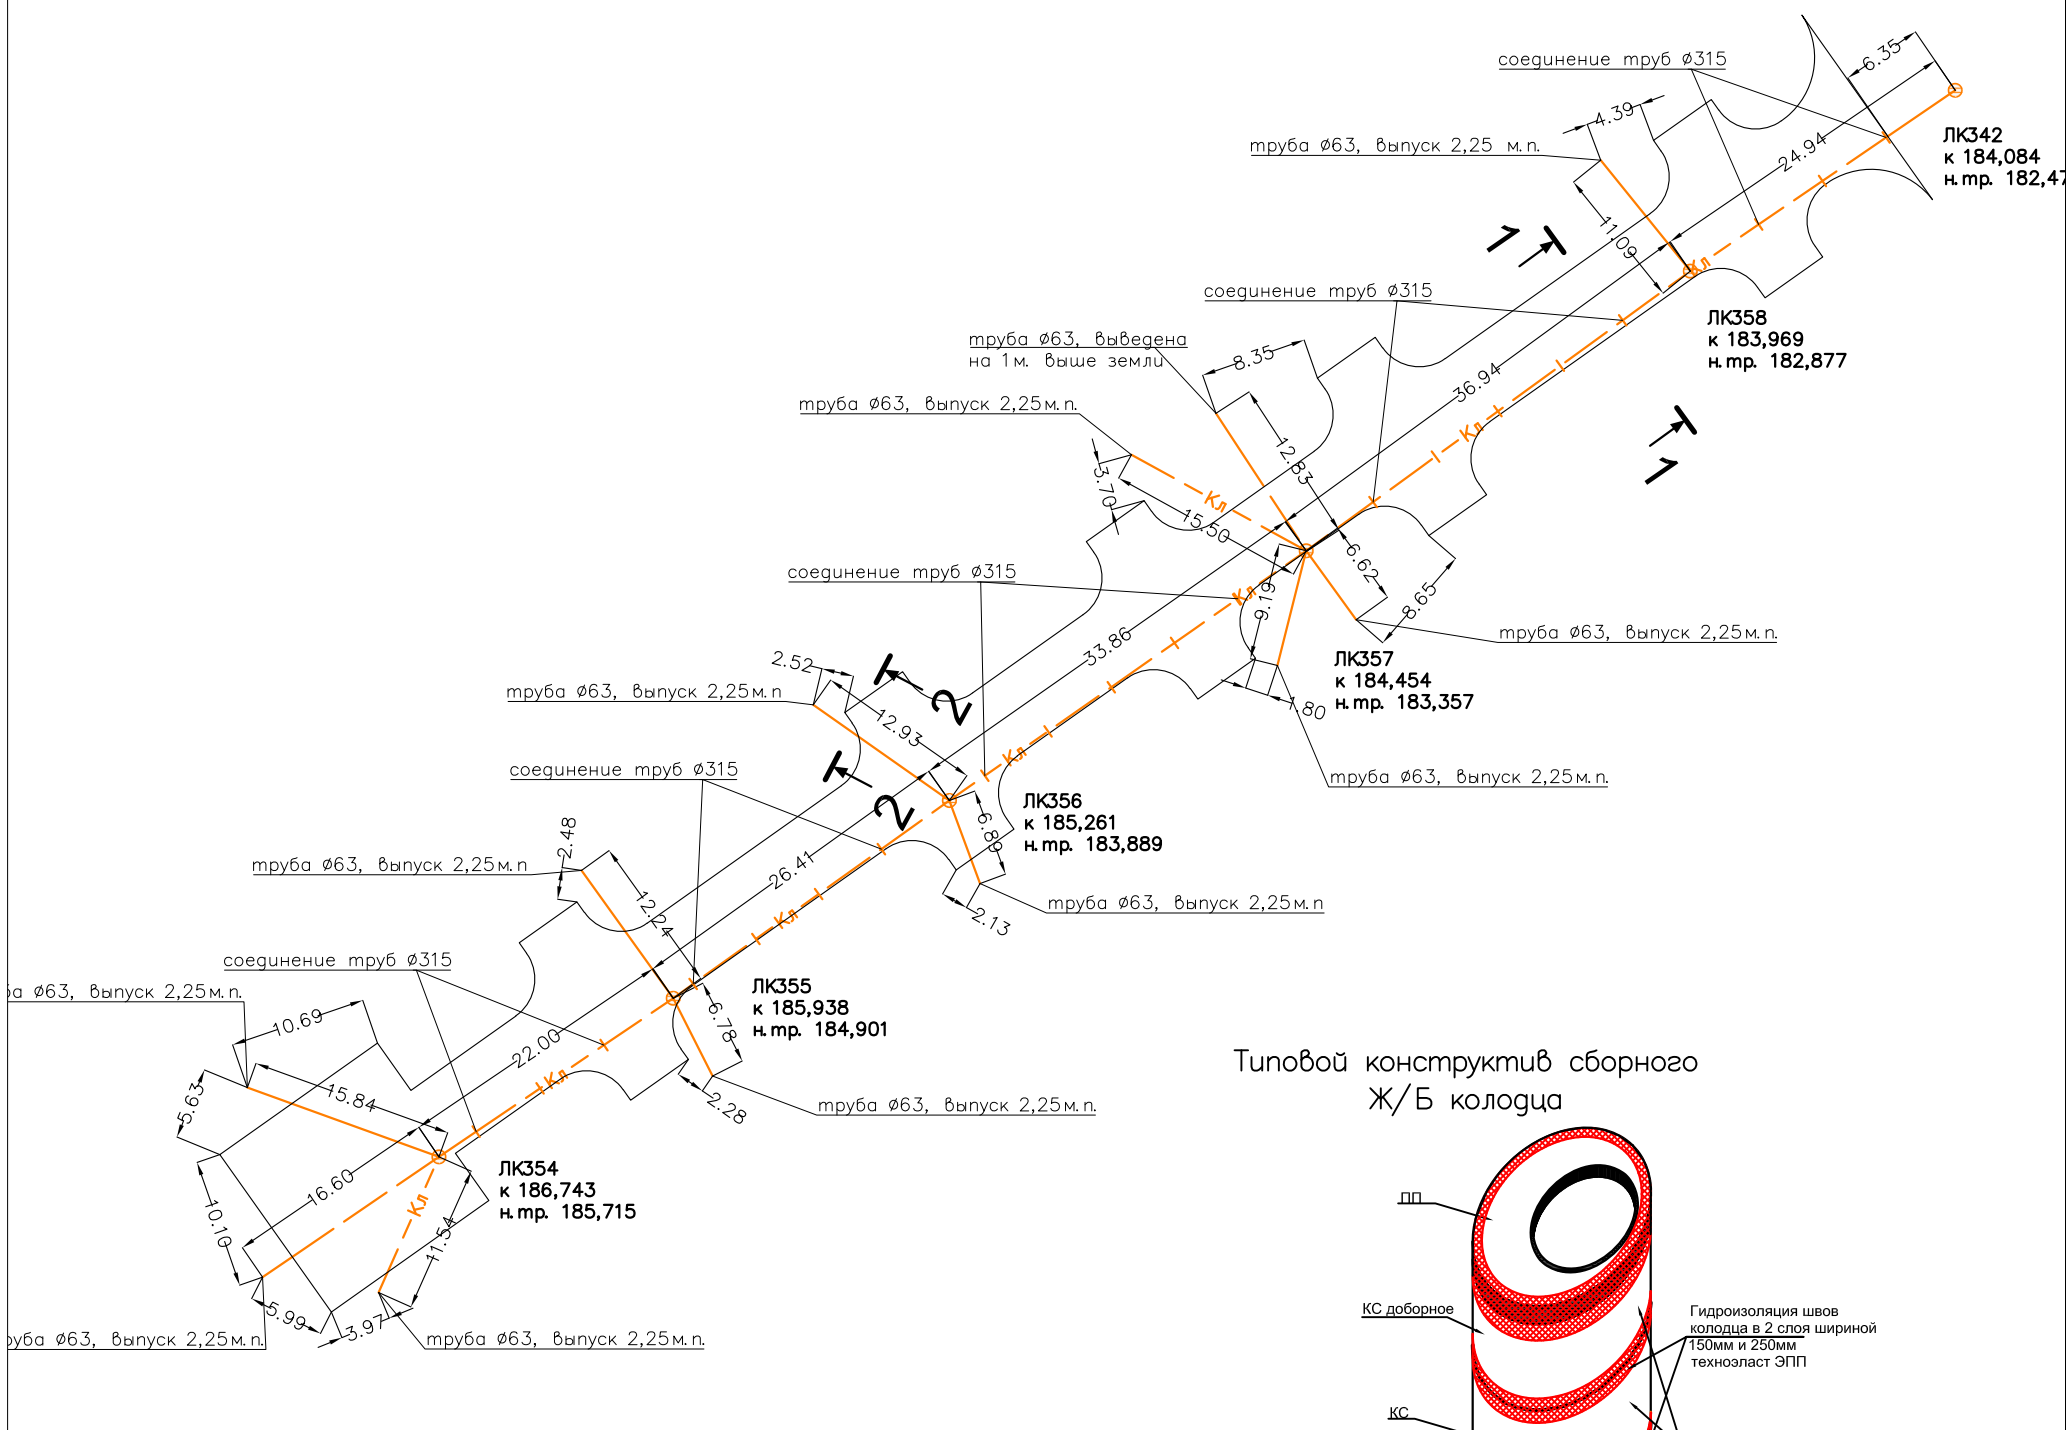

Типовой конструктив сборного Ж/Б колодца

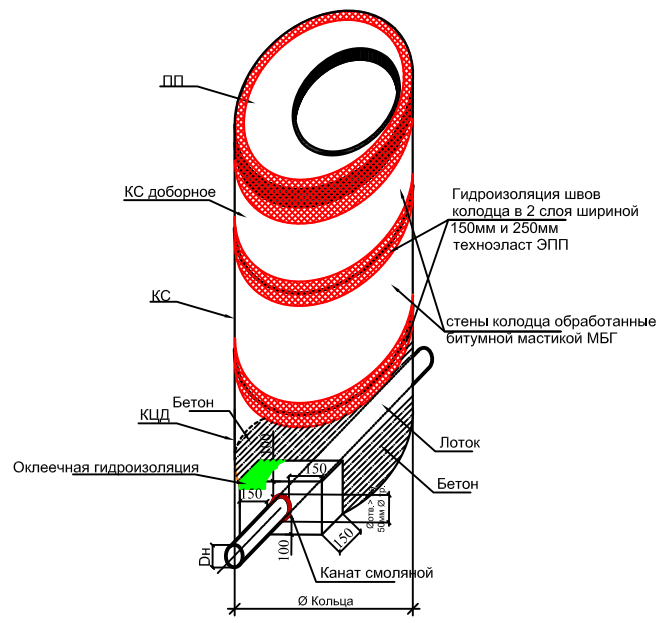

Ведомость расхода материалов:

– труба ø63 мм.:
15,84+2,25+16,6+2,25+11,54+2,25
+12,24+2,25+6,78+2,25+12,93+2,25
+6,89+2,25+12,83+2,25+15,5+2,25
+9,19+2,25+6,62+2,25+11,09+2,25
=165,05 м.п.

– труба корсис ø315 мм.: 160,75 м.п.

– соединение труб ø315 мм.: 20 шт.

				ИС–3ЛК–40V		
				Московская область, городской округ Истра, с/п. Павло– Слободское, д. Исаково.		
Должность	Ф. И. О.	Подпись	Дата			
геодезист	Голубев П. В.			Устройства трубопровода	стадия: ИД; лист: 4; листов: 8	
				от колодца ЛК354 до ЛК342 план, разрезы	ООО "Лика"	