

Оглавление

Введение.....3

1 Сведения о топографических, инженерно-геологических, гидрогеологических, метеорологических и климатических условиях земельного участка, предоставленного для размещения объекта капитального строительства.....4

2 Сведения об особых природных климатических условиях территории, на которой располагается земельный участок, предоставленный для размещения объекта капитального строительства.....4

3 Сведения о прочностных и деформационных характеристиках грунта в основании объекта капитального строительства.....4

4 Уровень грунтовых вод, их химический состав, агрессивность грунтовых вод и грунта по отношению к материалам, используемым при строительстве подземной части объекта капитального строительства.....5

5 Описание и обоснование конструктивных решений зданий и сооружений, включая их пространственные схемы, принятые при выполнении расчетов строительных конструкций.....5

6 Описание и обоснование технических решений, обеспечивающих необходимую прочность, устойчивость, пространственную неизменяемость зданий и сооружений объекта капитального строительства в целом, а также их отдельных конструктивных элементов, узлов, деталей в процессе изготовления, перевозки, строительства и эксплуатации объекта капитального строительства.....6

7 Описание конструктивных и технических решений подземной части объекта капитального строительства.....6

8 Обоснование проектных решений и мероприятий, обеспечивающих:.....7

 Соблюдение требуемых теплозащитных характеристик ограждающих конструкций.....7

 Снижение шума и вибраций.....7

 Гидроизоляция и пароизоляция помещений.....7

 Снижение загазованности помещений.....7

 Удаление избытков тепла.....7

 Соблюдение безопасного уровня электромагнитных и иных излучений, соблюдение санитарно-гигиенических условий.....7

 Пожарную безопасность.....7

 Соответствие зданий, строений и сооружений требованиям энергетической эффективности и требованиям оснащенности их приборами учета используемых энергетических ресурсов.....7

9 Характеристика и обоснование конструкций полов, кровли, подвесных потолков, перегородок, а также отделки помещений.....8

10 Перечень мероприятий по защите строительных конструкций и фундаментов от разрушения8

11 Описание инженерных решений и сооружений, обеспечивающих защиту территории объекта капитального строительства, отдельных зданий и сооружений объекта капитального строительства, а также жителей от опасных природных и техногенных процессов.....8

12 Перечень мероприятий по обеспечению соблюдения установленных требований энергетической эффективности к конструктивным решениям, влияющим на энергетическую эффективность здания.....8

13 Описание и обоснование принятых конструктивных, функционально-технологических и инженерно-технических решений, направленных на повышение энергетической эффективности объекта капитального строительства.....8

Согласовано					
Изм. №подл.	Интв. №подл.	Взам. инв. №	Подпись и дата		
Интв. №подл.	Интв. №подл.	Взам. инв. №	Подпись и дата	Изм.	Кол.
				Лист	№док
				Подпись	Дата

ОПР-01/24/2024-КР.ТЧ

"Современный оптово-продовольственный рынок (ОПР) по адресу: Донецкая область, г. Макеевка, Горняцкий район Док-павильон (рыба-мясо) №23, №23.2 (по генплану)	Стадия	Лист	Листов
	П	1	7

1 Сведения о топографических, инженерно-геологических, гидрогеологических, метеорологических и климатических условиях земельного участка, предоставленного для размещения объекта капитального строительства

На основании архивных и общедоступных материалов установлено, что в основании проектируемых сооружений принимают участие плейстоценовые отложения, четвертичной системы, верхне-нижнечетвертичные отложения.

Плейстоценовые отложения представлены эолово-делювиальными отложениями (vdQI-III), сложенными в основном глинистыми грунтами.

В соответствии со схемой климатического районирования (СП 131.13330.2020) для строительства, участок работ расположен в строительно-климатической зоне II-В. Зона влажности – 2 зона (согласно Приложения В СНиП 23-02-2003).

Рельеф преимущественно равнинный (высотой до 200 метров), расчленённый впадинами и балками. На северо-востоке находится Донецкий кряж высотой до 367 м, поверхность которого изрезана долинами рек. На западе кряж переходит в Приднепровскую низменность, на юге – в Приазовскую низменность с отдельными поднятиями (Могила-Гончариха, Саур-Могила и другие). На юге – узкая полоса Причерноморской низменности, которая уступами обрывается к Азовскому морю.

Абсолютная отметка территории по устью скважины составляет 198,24-208,42 м.

2 Сведения об особых природных климатических условиях территории, на которой располагается земельный участок, предоставленный для размещения объекта капитального строительства

Особые климатические условия на участке проектирования отсутствуют.

3 Сведения о прочностных и деформационных характеристиках грунта в основании объекта капитального строительства

В результате анализа и обобщения данных, полученных лабораторными методами, грунты, слагающие площадку изысканий до глубины 8,0/15,0 м выделено 2 инженерногеологических элемента (ИГЭ) и 1 слой.

Слой 1– Почвенно-растительный слой pdQIV

ИГЭ №1– Суглинок коричневый, тугопластичный, vdQI-III

ИГЭ №2– Суглинок коричневый, мягкопластичный, vdQI-III Характеристики физических и механических свойств грунтов получены по результатам лабораторных испытаний, по данным СП 22.13330.2016 и представлены в таблице 1.

Изм.	Кол.	Лист	№ док	Подпись	Дата	Инов. № подл.	Подпись и дата	Взам. инв. №	
------	------	------	-------	---------	------	---------------	----------------	--------------	--	--	

Перед монолитными работами установить фундаментные болты, по ГОСТ 24379.1-2012.

8 Обоснование проектных решений и мероприятий, обеспечивающих:

Соблюдение требуемых теплозащитных характеристик ограждающих конструкций

Проектируемое здание имеет прямоугольную энергетически эффективную форму, обеспечивающую существенное снижение расхода тепловой энергии на отопление здания. Ограждающие конструкции запроектированы с применением материалов и изделий, апробированных на практике и выпускаемых по стандартам со следующими параметрами сопротивления теплопередачи.

- Наружные стены (трехслойная сэндвич-панель на минераловатном утеплителе) - 2.79 (м²•°C)/Вт

- Кровля совмещенная с гидроизоляционным ковром - 3.42 (м²·°C)/Вт Остекление (стеклопакеты) - Ro = 0,54 м²·°C/Вт

Для увеличения энергетической эффективности предъявляются следующие требования к отдельным элементам и конструкциям здания:

- применение конструкций окон с повышенными теплозащитными свойствами, пониженной воздухопроницаемостью притворов и фальцев;

- элементы притворов дверей, окон, стыки панелей запроектированы с повышенной степенью уплотнения;

- сопряжение элементов в наружных ограждающих конструкциях принято с исключением возможных «мостиков холода».

Снижение шума и вибраций

Защита персонала, во время проведения работ, от шума обеспечивается индивидуальными средствами защиты.

Гидроизоляция и пароизоляция помещений

Процессов вызывающих повышенную влажность и образование пара проектом не предусматривается.

Для защиты металлических несущих конструкций здания от коррозии и повышения предела огнестойкости производится обработка огнезащитной краской для металла на органической основе GOODHIM METALUX 01 (атмосферостойкая), обеспечивающая предел огнестойкости металлических конструкций до 120 минут (R120).

Конструкции ниже отметки грунта окрашены битумной мастикой.

Снижение загазованности помещений

Процессов вызывающих повышенную загазованность помещений проектом не предусматривается.

Удаление избытков тепла

Процессов вызывающих повышенный избыток тепла проектом не предусматривается.

Изм.	Кол.	Лист	№ док	Подпись	Дата	Инов. №подл.	Подпись и дата	Взам. инв. №	Конструкции ниже отметки грунта окрашены битумной мастикой.
									<u>Снижение загазованности помещений</u>
									Процессов вызывающих повышенную загазованность помещений проектом не предусматривается.
									<u>Удаление избытков тепла</u>
									Процессов вызывающих повышенный избыток тепла проектом не предусматривается.
ОПР-01/24/2024-КР.ТЧ									
Лист									
5									

ВЕДОМОСТЬ ЛИСТОВ ОСНОВНОГО КОМПЛЕКТА

Лист	Наименование	Примечание	Лист	Наименование	Примечание
01	Ведомость листов графической части		25	Пандус П1	
02	Ведомость элементов		26	Пандус П2	
03	Схема расположения фундамента		27	Пандус П2	
04	Схема расположения фундаментных стен		28	Лестница Л1	
05	Схема пола по грунту, перекрытия подвала		29	Лестница Л2	
06	Схема расположения колонн и балок перекрытия		30	Схема расположения козырьков	
07	Схема расположения стоек перегородок 1-го этажа		31	Козырек Кр1	
08	Схема расположения стоек перегородок 2-го этажа				
09	Сечения I-I, II-II, III-III				
10	Схема расположения балок покрытия				
11	Развертки 1-18/А, 18-1/И				
12	Развертка 1-18/В, 1-18/Г				
13	Развертки 1-18/Д, 18-1/Е				
14	Развертки А-И/18, И-А/1				
15	Разрезы 1-1, 2-2				
16	Разрезы 3-3, 4-4				
17	Узлы 01-04				
18	Узлы 05-08				
19	Схема расположения перекрытия на отм. +3,500				
20	Схема каркаса лестницы, план ступеней				
21	Схема расположения крылец				
22	Площадка Пл01				
23	Площадка Пл02				
24	Пандус П1				

						ОПР-01/24/2024-КР.ГЧ					
						"Современный оптово-продовольственный рынок (ОПР) по адресу: Донецкая область, г Макеевка, Горняцкий район"					
Изм.	Кол.уч.	Лист	№Док.	Подп.	Дата						
Разраб.						Док-павильон (рыба-мясо) №23, №23.2 (по генплану)			Стадия	Лист	Листов
Пров.									П	01	
						Ведомость листов графической части			ООО "Технология"		
Н. контроль											

Согласовано									
	0623			кв. тр. 80×6					
	0624			кв. тр. 80×6					
	0625			кв. тр. 80×6					
	0626			кв. тр. 80×6					
	0627			кв. тр. 80×6					
	0628			кв. тр. 80×6					
	0629			кв. тр. 80×6					
	0630			кв. тр. 80×6					
	0631			кв. тр. 80×6					
Взам. инв. №	0632			кв. тр. 80×6					
	0633			кв. тр. 80×6					
	0634			кв. тр. 80×6					
	0635			кв. тр. 80×6					
Подп. и дата	P1			кв. тр. 80×6					
	P2			кв. тр. 80×6					
	P3			кв. тр. 120×6					
	P4			кв. тр. 120×6					
Инв. № подл.	P5			кв. тр. 120×6					


Марка эл-та	Сечение			Усилие прикреплeния			Марка металла	Примечани я
	Эскиз	Поз.	Состав	N, т	Q, т	M, тм		
K1			двутавр 25K2					
K1с			двутавр 25K2					
K2			двутавр 25K2					
K2-2			двутавр 25K2					
K2-2с			двутавр 25K2					
K2-3			двутавр 25K2					
K2с			двутавр 25K2					
БП1			двутавр 30Б2					
БП2			двутавр 30Б2					
Б1			двутавр 35Ш2					
Б2			двутавр 35Ш2					
С1			уголок 120×8					
С2			уголок 120×8					
С3			уголок 120×8					
П1			шв. №22					
П2			шв. №22					
П3			шв. №24					

ПРИМЕЧАНИЯ:

- 1) Двутавры по СТО АСЧ 20-93;
2) Квадратные и прямоугольные трубы по ГОСТ 30245-2012;
3) Уголки по ГОСТ 8509-93;


						ОПР-01/24/2024-КР.ГЧ			
						"Современный оптово-продовольственный рынок (ОПР) по адресу: Донецкая область, г Макеевка, Горняцкий район			
Изм.	Кол.уч.	Лист	№Док.	Подп.	Дата	Док-павильон (рыба-мясо) №23, №23.2 (по генплану)	Стадия	Лист	Листов
Разраб.							П	02	
Пров.									
						Ведомость элементов	ООО "Технология"		
Н. контроль									

1:200

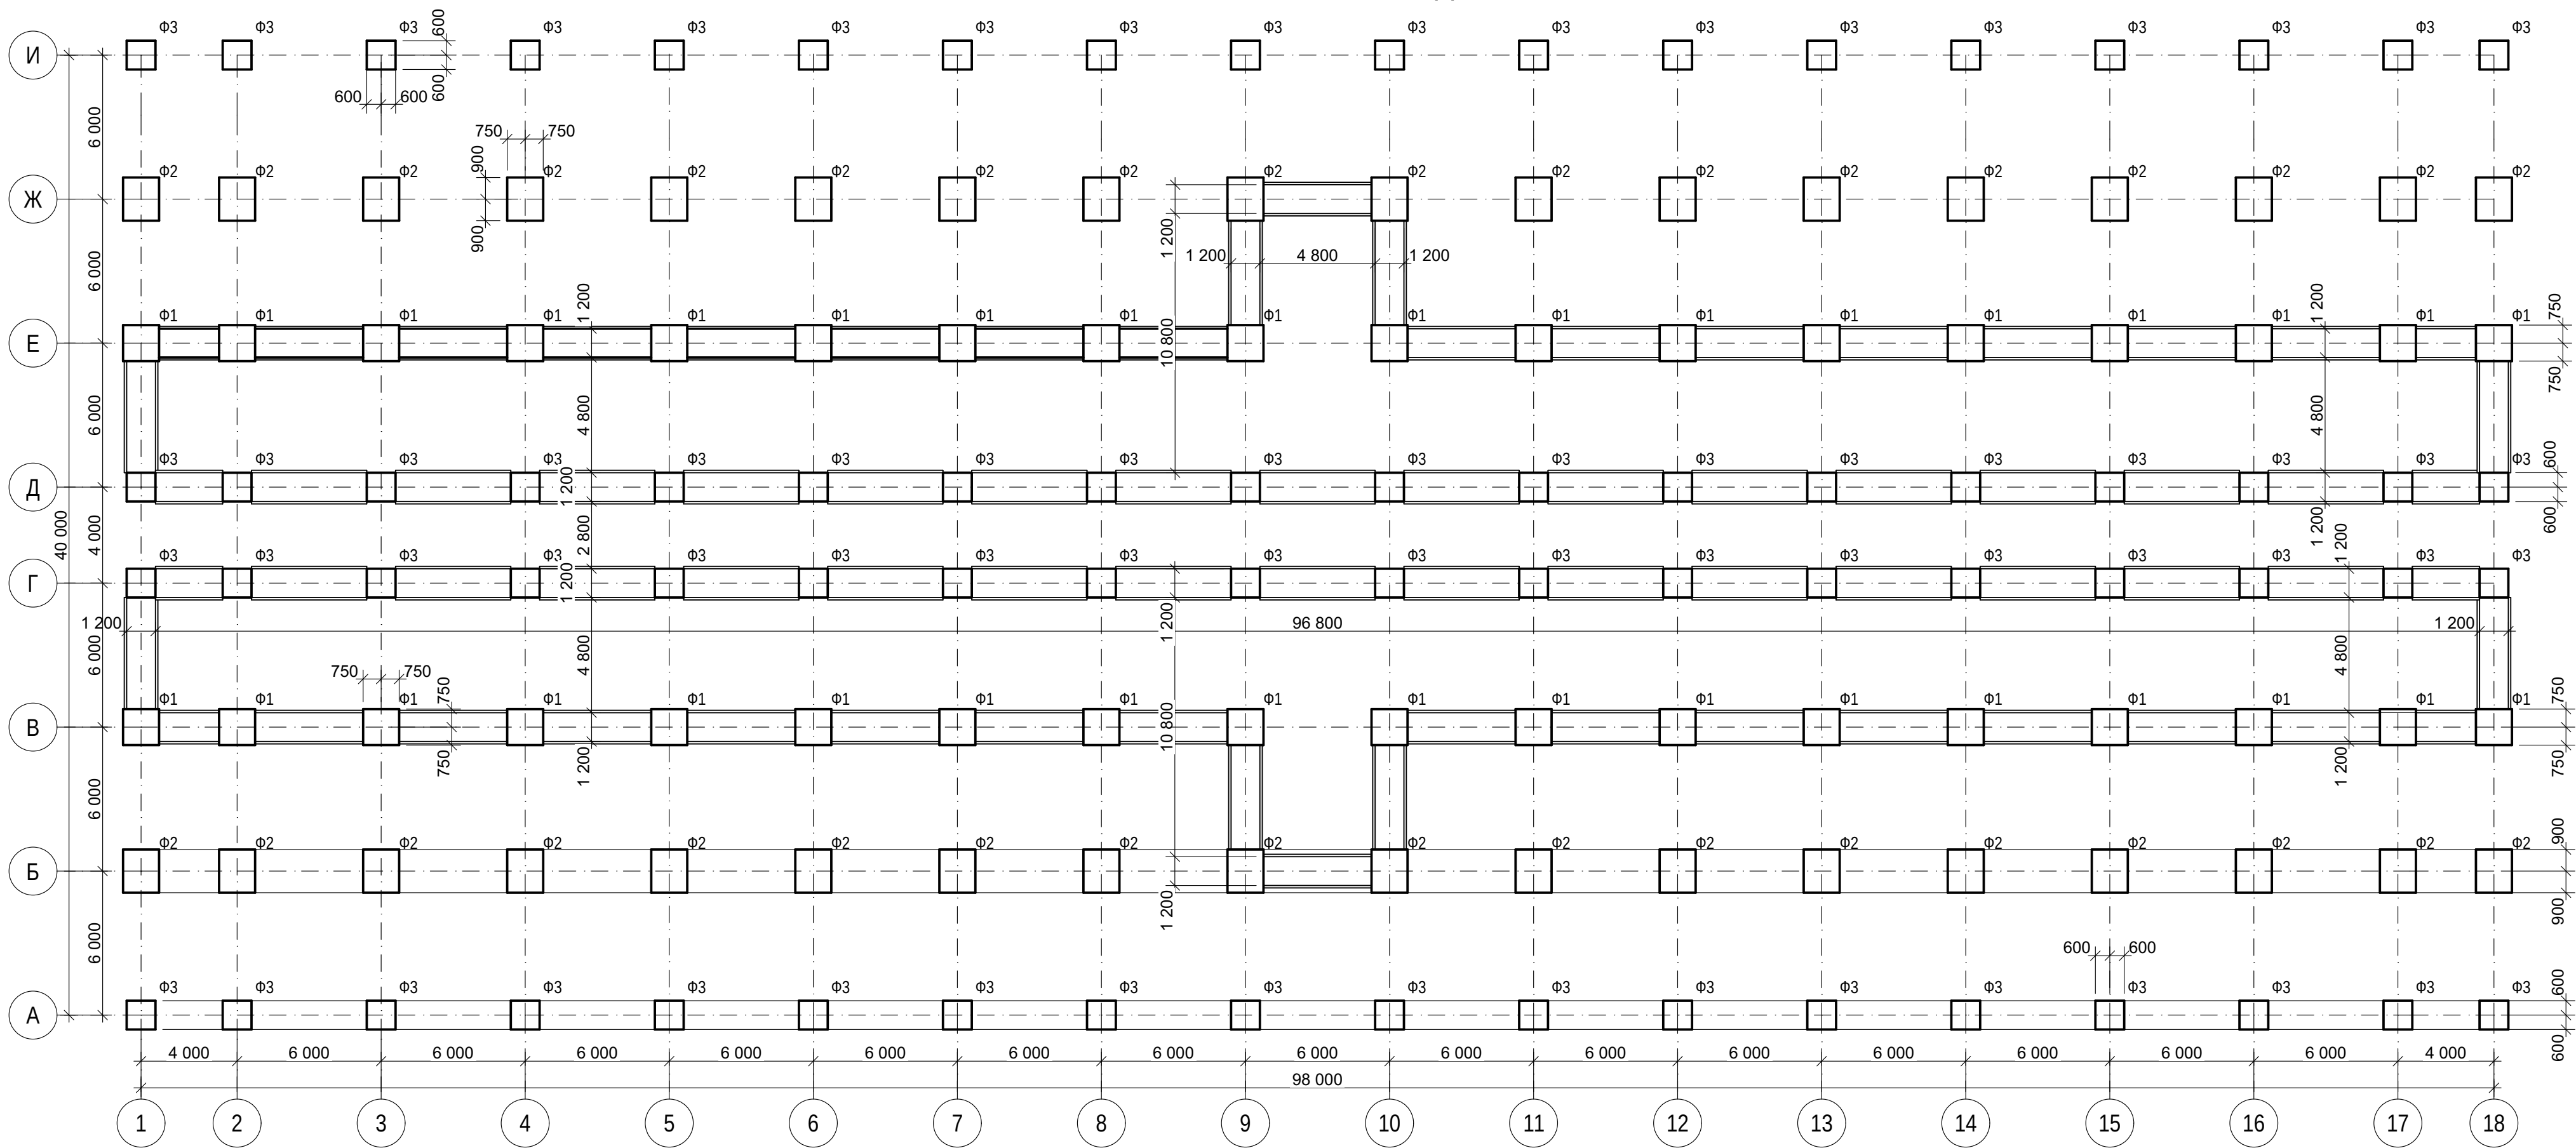

КОНСТРУКЦИЯ ФУНДАМЕНТА





Поз.	Обозначение	Наименование	Кол-во	Масса ед., кг	Приме чание
01	Подготовка	Бетон В7,5	44,72		м³
01	Фундаментная лента	Бетон В25, F100, W2	121,01		м³
01	засыпка между лентами	Песок	267,27		м³
01	засыпка между лентами	Бетон В20	123,47		м³

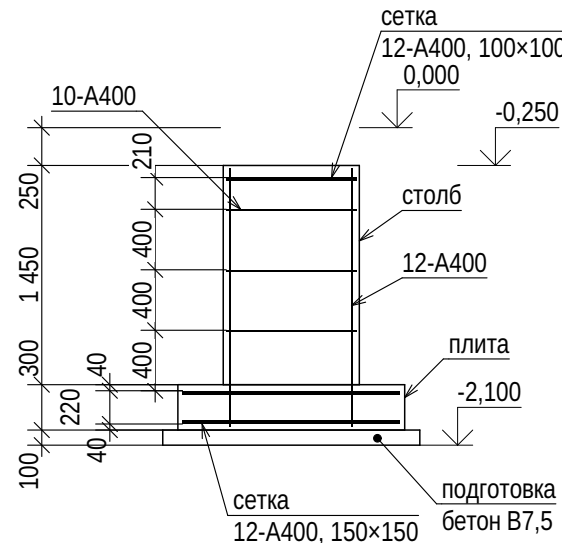

- 1) Отметка подошвы фундамента: -2,500; под фундаментами выполнить песчаную подготовку толщиной 100мм;
- 2) Материал фундаментов - бетон В20, W4, F100;
- 3) Основание фундамента - ИГЭ №1– Суглинок коричневого, тугопластичный;
- 4) Схема армирования ленты см. лист 04;
- 6) В фундаментах Ф1, в осях 9-10/В и 9-10/Е, в подливку установить закладные изделия МН134-6

						ОПР-01/24/2024-КР.ГЧ			
						"Современный оптово-продовольственный рынок (ОПР) по адресу: Донецкая область, г. Макеевка, Горняцкий район			
Изм.	Колуч.	Лист	№Док.	Подл.	Дата				
Разраб.						Док-павильон (рыба-мясо) №23, №23.2 (по генплану)	Стадия	Лист	Листов
Пров.							П	03	
						Схема расположения фундамента	ООО "Технология"		
Н. контроль									

Инв. № подл.	Подп. и дата	Взам. инв. №	Согласовано		

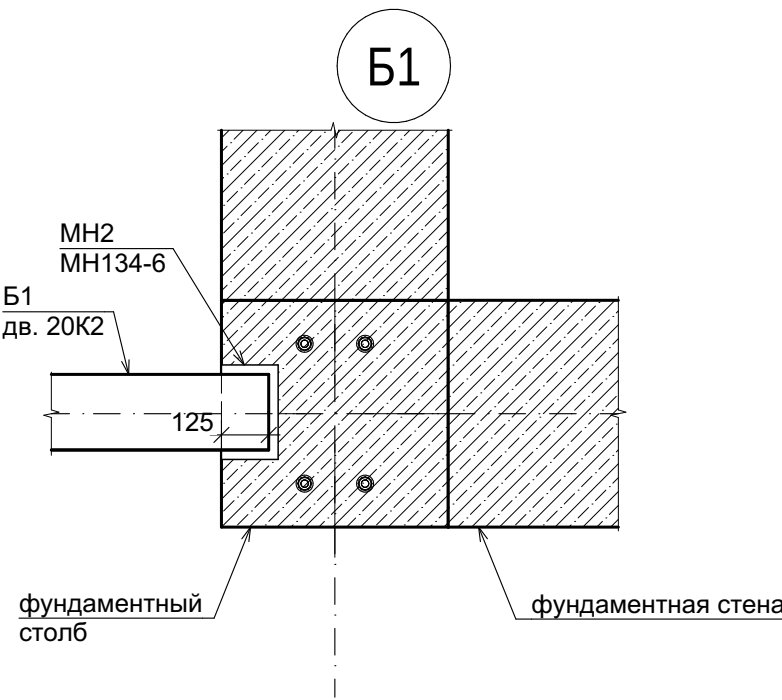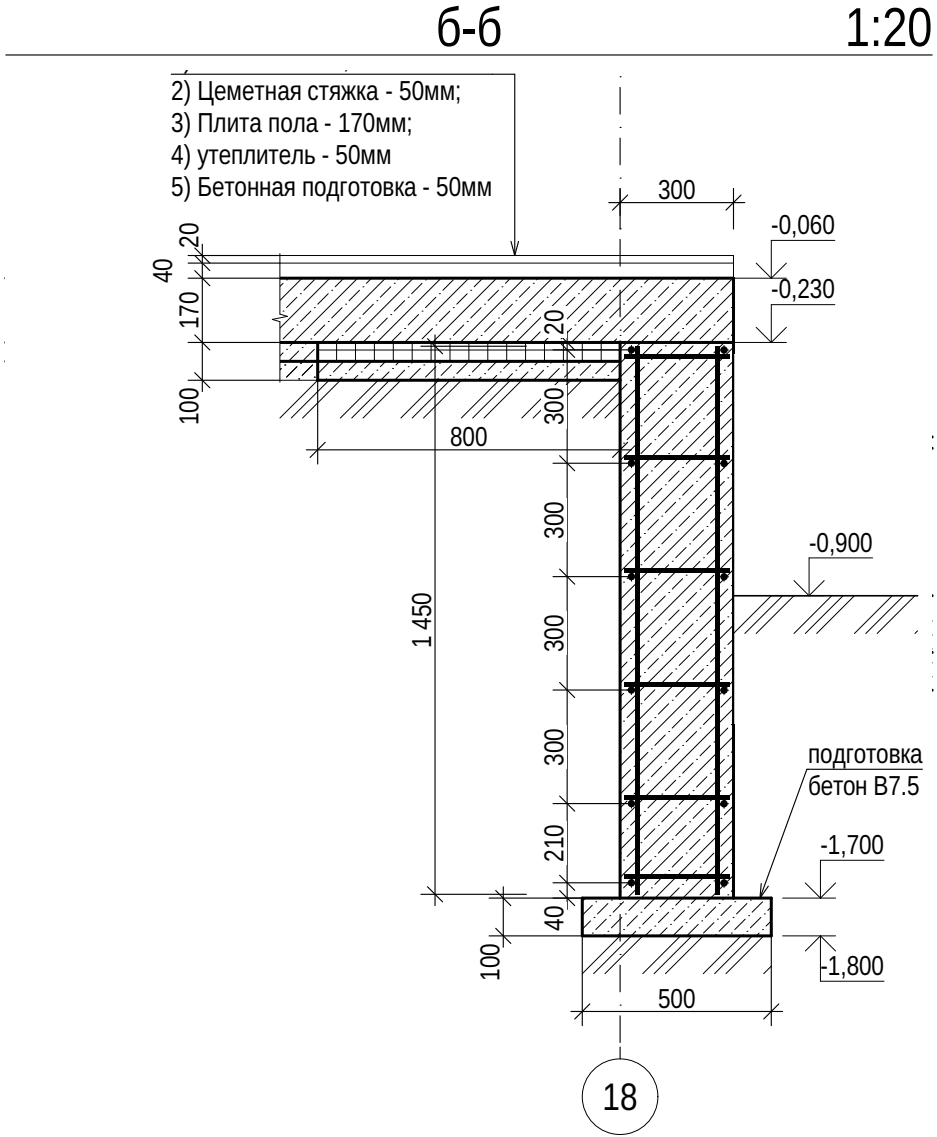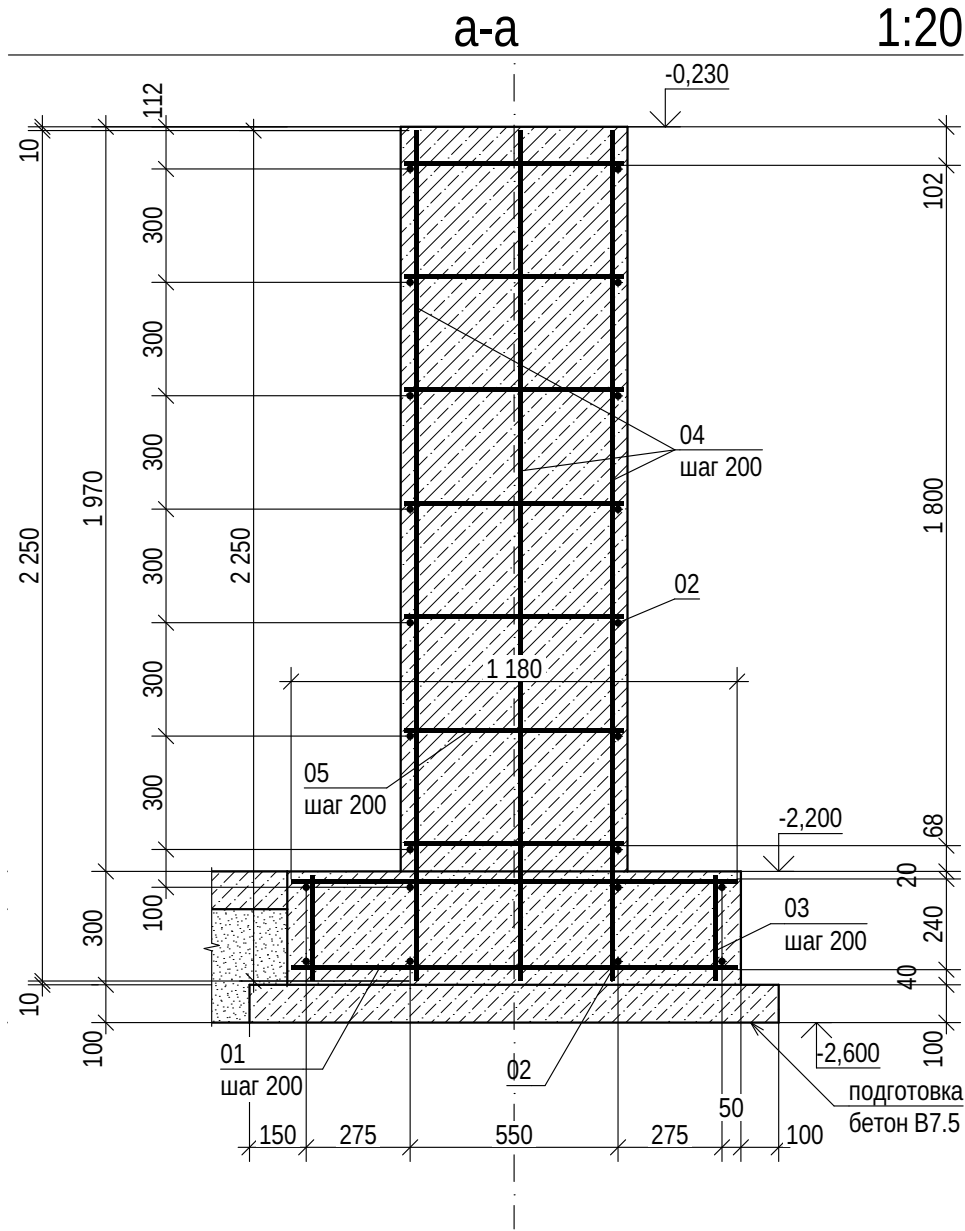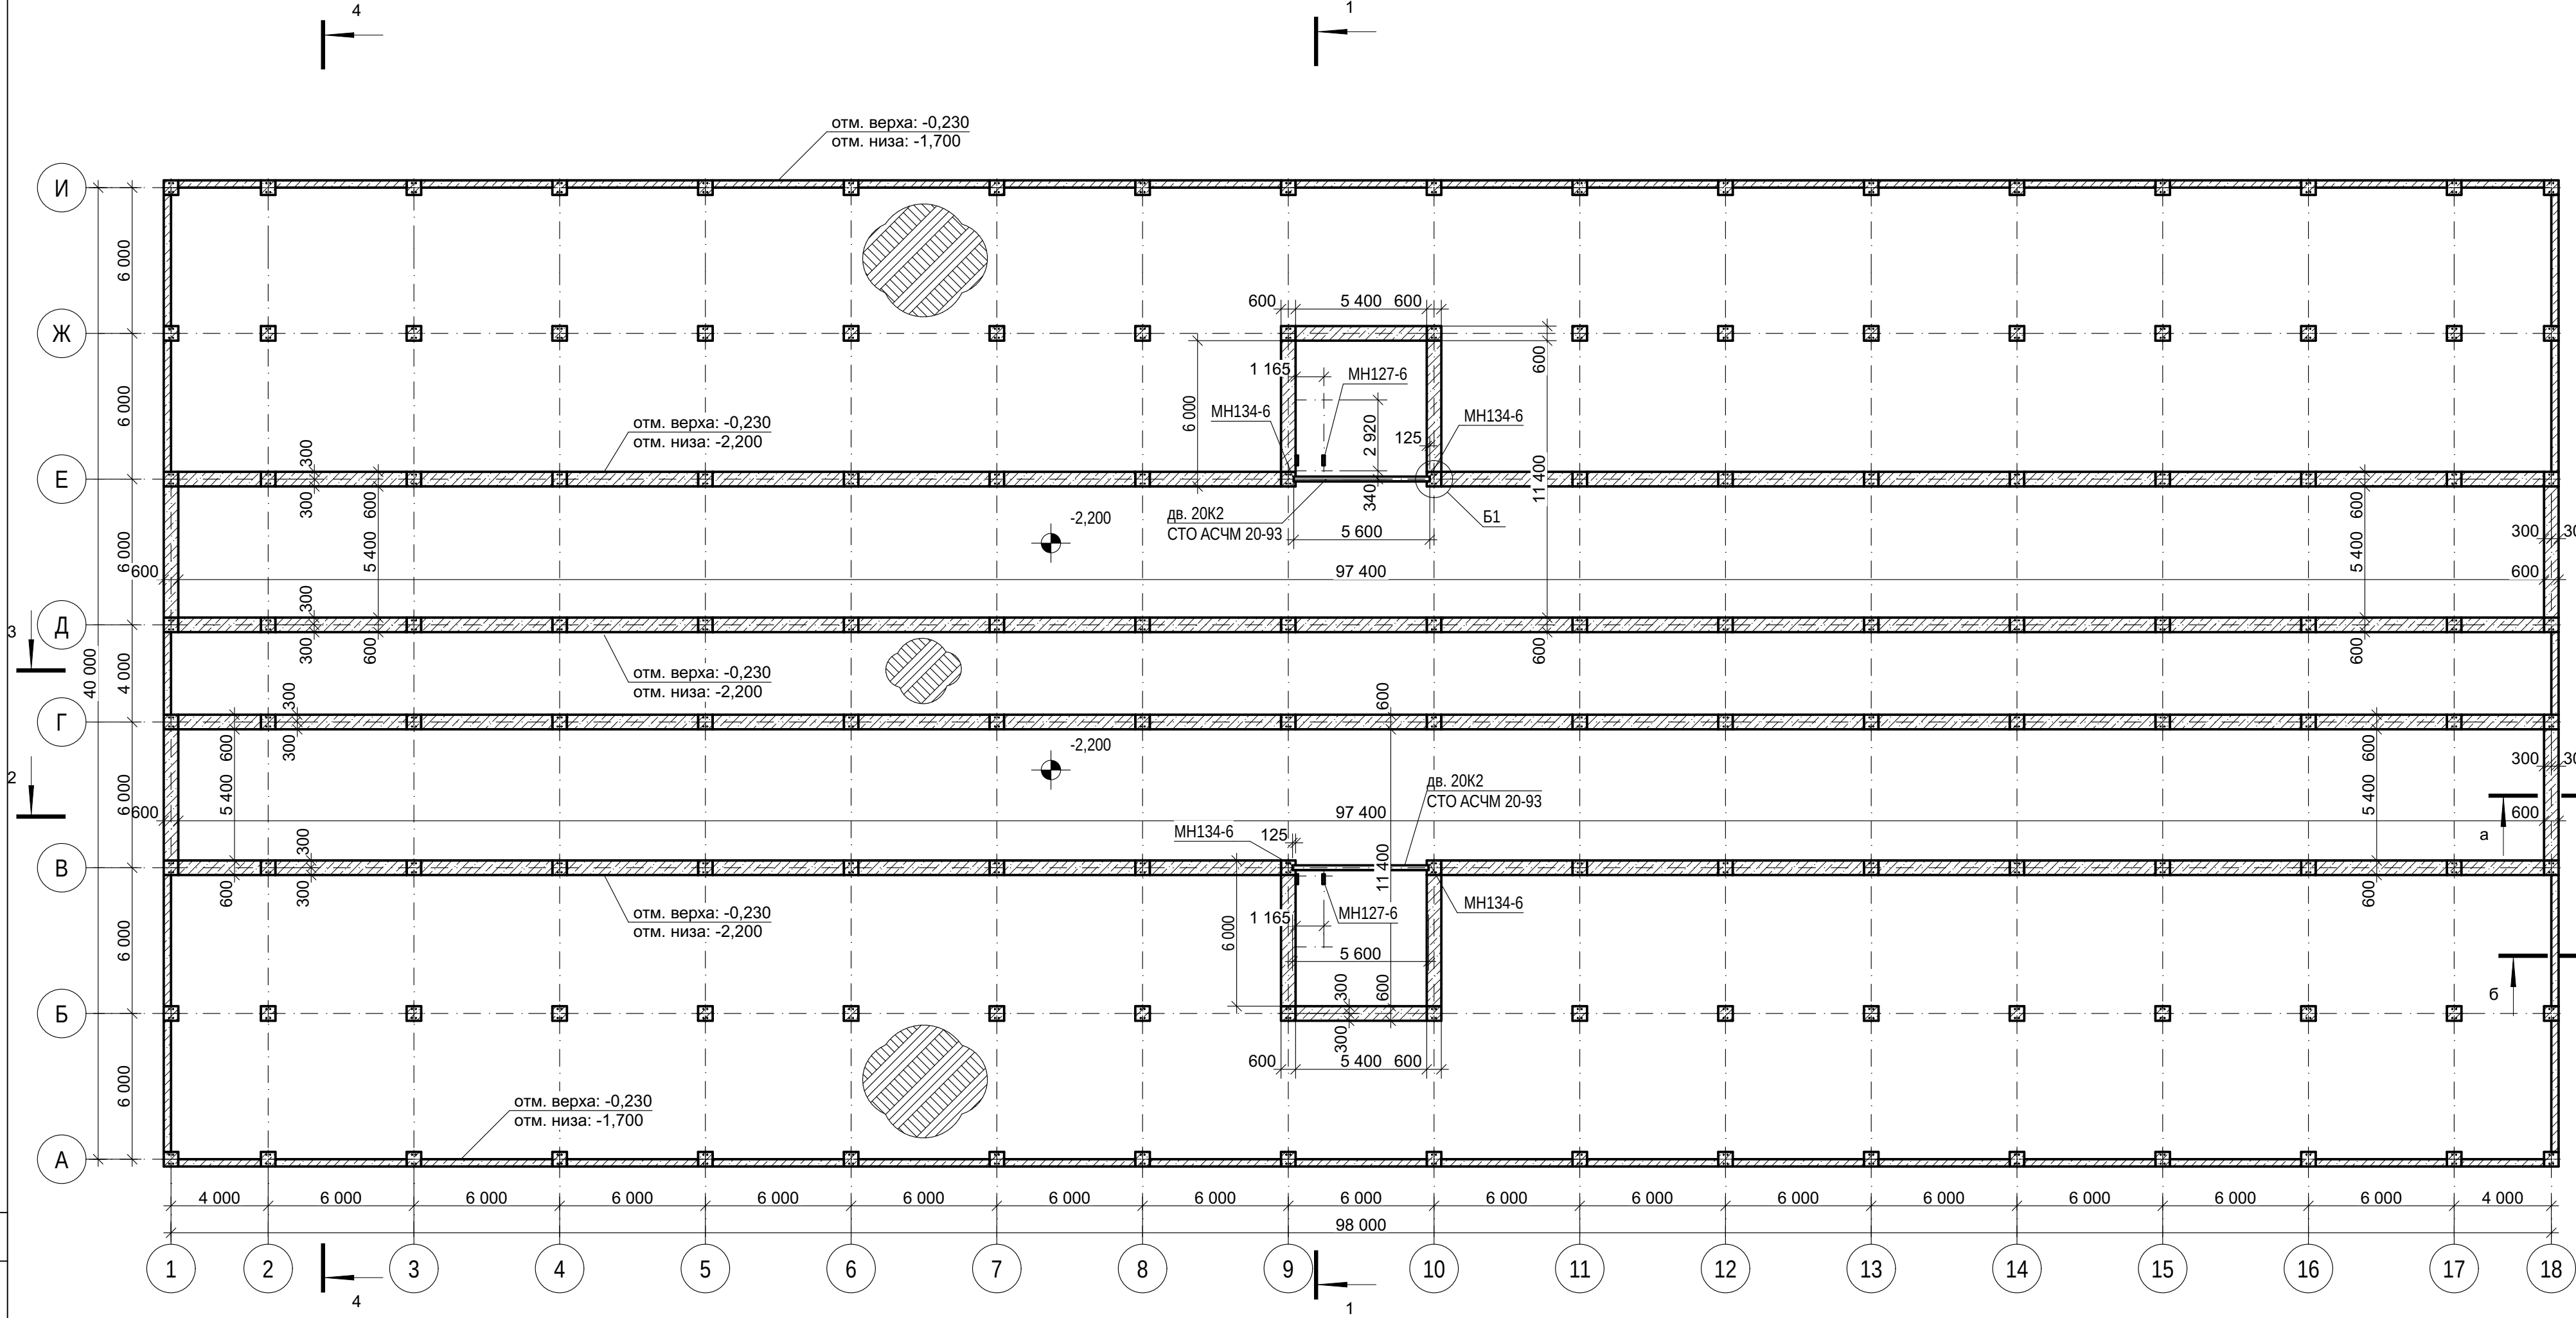


СПЕЦИФИКАЦИЯ МАТЕРИАЛОВ СТЕН

Поз.	Обозначение	Наименование	Кол-во	Маса ед., кг	Приме чание
01	стены	Бетон В20, W2, F50	466,00		м³
02	стены	Бетон В20, W2, F50	99,44		м³

ПРИМЕЧАНИЯ:

- Фундаментные стены - монолитные. Материал - бетон В20, W4, F100;
- Стены армировать: пространственным каркасом из арматуры 12-A400;
- Между стен выполнить обратную засыпку щебнем;
- Смотреть совместно с листом 03

							ОПР-01/24/2024-КР.ГЧ
							"Современный оптово-продовольственный рынок (ОПР) по адресу: Донецкая область, г. Макеевка, Горняцкий район
Изм.	Коп.уч.	Лист	Надп.	Подп.	Дата		Док-павильон (рыба-мясо) №23, №23.2
Разраб.					01.25		Стадия
Пров.					01.25		Лист
							Листов
							П 04
Н. контроль					01.25		Схема расположения фундаментных стен
							ООО "Технология"

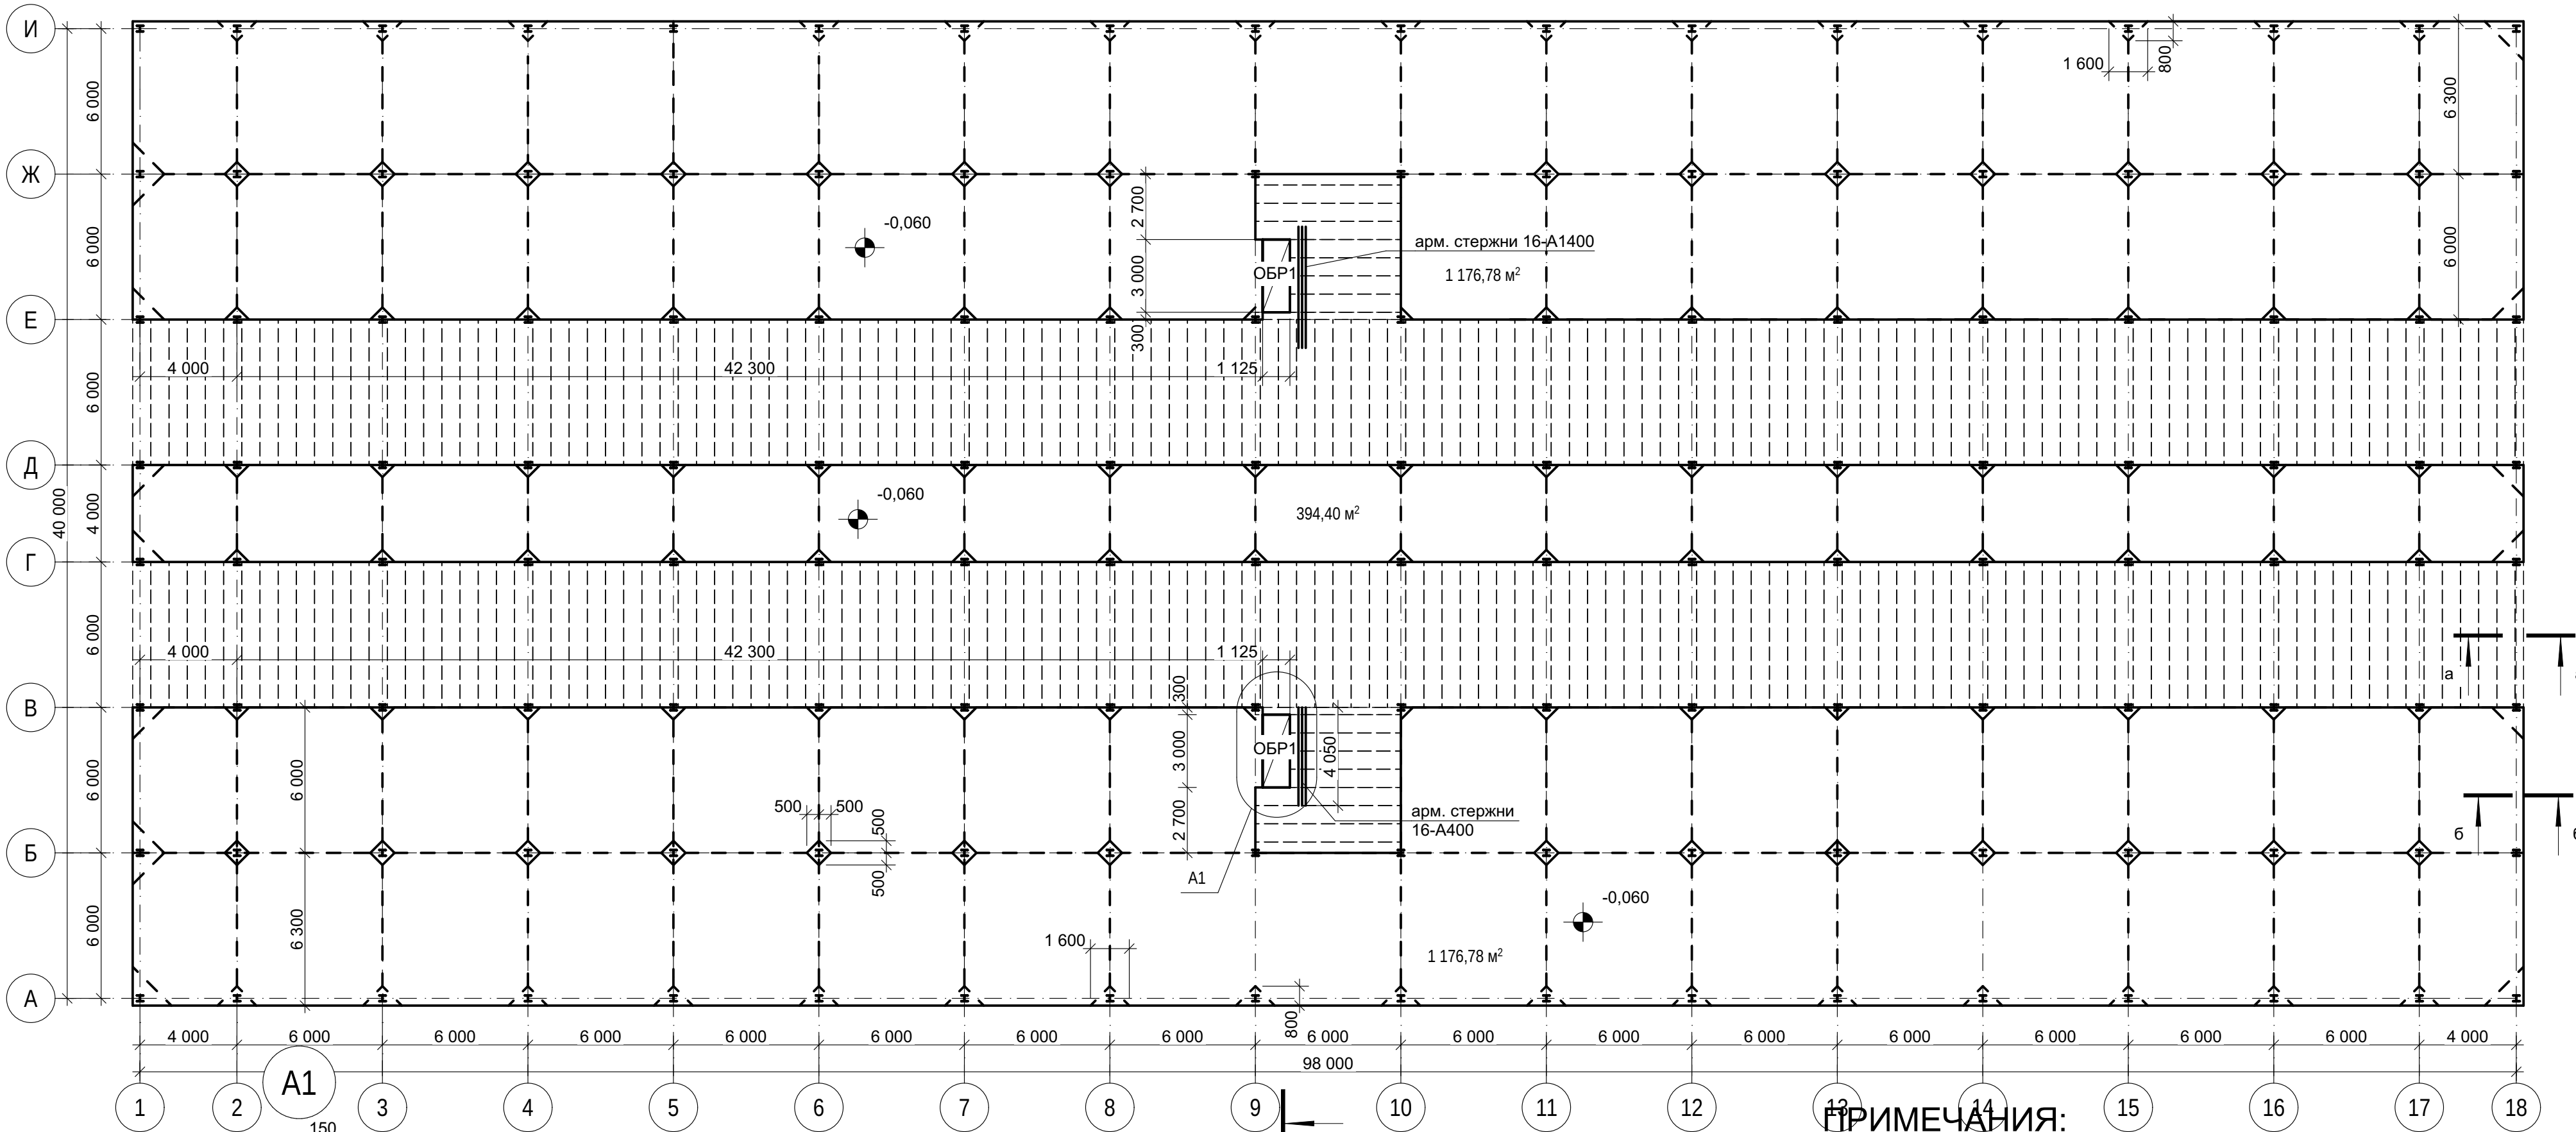

УСЛОВНЫЕ ОБОЗНАЧЕНИЯ

----- - граница листов профилированного настила монолитного перекрытия


СПЕЦИФИКАЦИЯ МАТЕРИАЛОВ ПОЛА ПО ГРУНТУ

Поз.	Обозначение	Наименование	Кол-во	Маса ед., кг	Приме чание
01	плита пола по грунту	Бетон В20	467,49		м³
02	утепление по периметру	ПЕНОПЛЭКС ФУНДАМЕНТ	19,12		м³
03	подготовка	Бетон В7,5	324,69		м³

ПРИМЕЧАНИЯ:

- 1) Отметка верха плиты по грунту/плиты перекрытия техподполья: -0,060.
- 2) Основание под пол - бетон В20; по периметру, под плиту, уложить на ширину 800мм утеплитель - плиты их экструзионного пенополистирола, толщиной 100мм.
- 3) Основание под армировать в нижнем слое сеткой 8-A240, с шагом 150×150;
- 4) В основании выполнить температурно-усадочные швы, во взаимно-перпендикулярном направлении и вокруг колонн; глубина швов - 50мм;
- 5) Швы заполнить жгутом из вспененного полиэтилена, сверху замазать мастикой;
- 6) Над техподпольем выполнить перекрытие по профлисту НС114-750-0,9; толщина перекрытия 170мм;
- 7) Профлисты крепить на саморезы, в каждой гофре, на каждой балке;
- 8) Армирование перекрытия выполнять плоскими каркасами уложенными в гофры; продольное армировнаие, в гофрах, 4 стержня арматуры 16-A400; поперечное армирование выполнять стержнями арматуры 12-A400 с шагом 150мм
- 9) В месте проемов под лестницы выполнить поперечное армировние арматурой 16-A400;
- 9) Смотреть совместно с листом 03

						ОПР-01/24/2024-КР.ГЧ			
						"Современный оптово-продовольственный рынок (ОПР) по адресу: Донецкая область, г. Макеевка, Горняцкий район			
Изм.	Колуч.	Лист	№Док.	Подп.	Дата	Док-павильон (рыба-мясо) №23, №23.2 (по генплану)	Стадия	Лист	Листов
Разраб.							П	05	
Пров.						Схема пола по грунту, перекрытия подвала	ООО "Технология"		
Н. контроль									

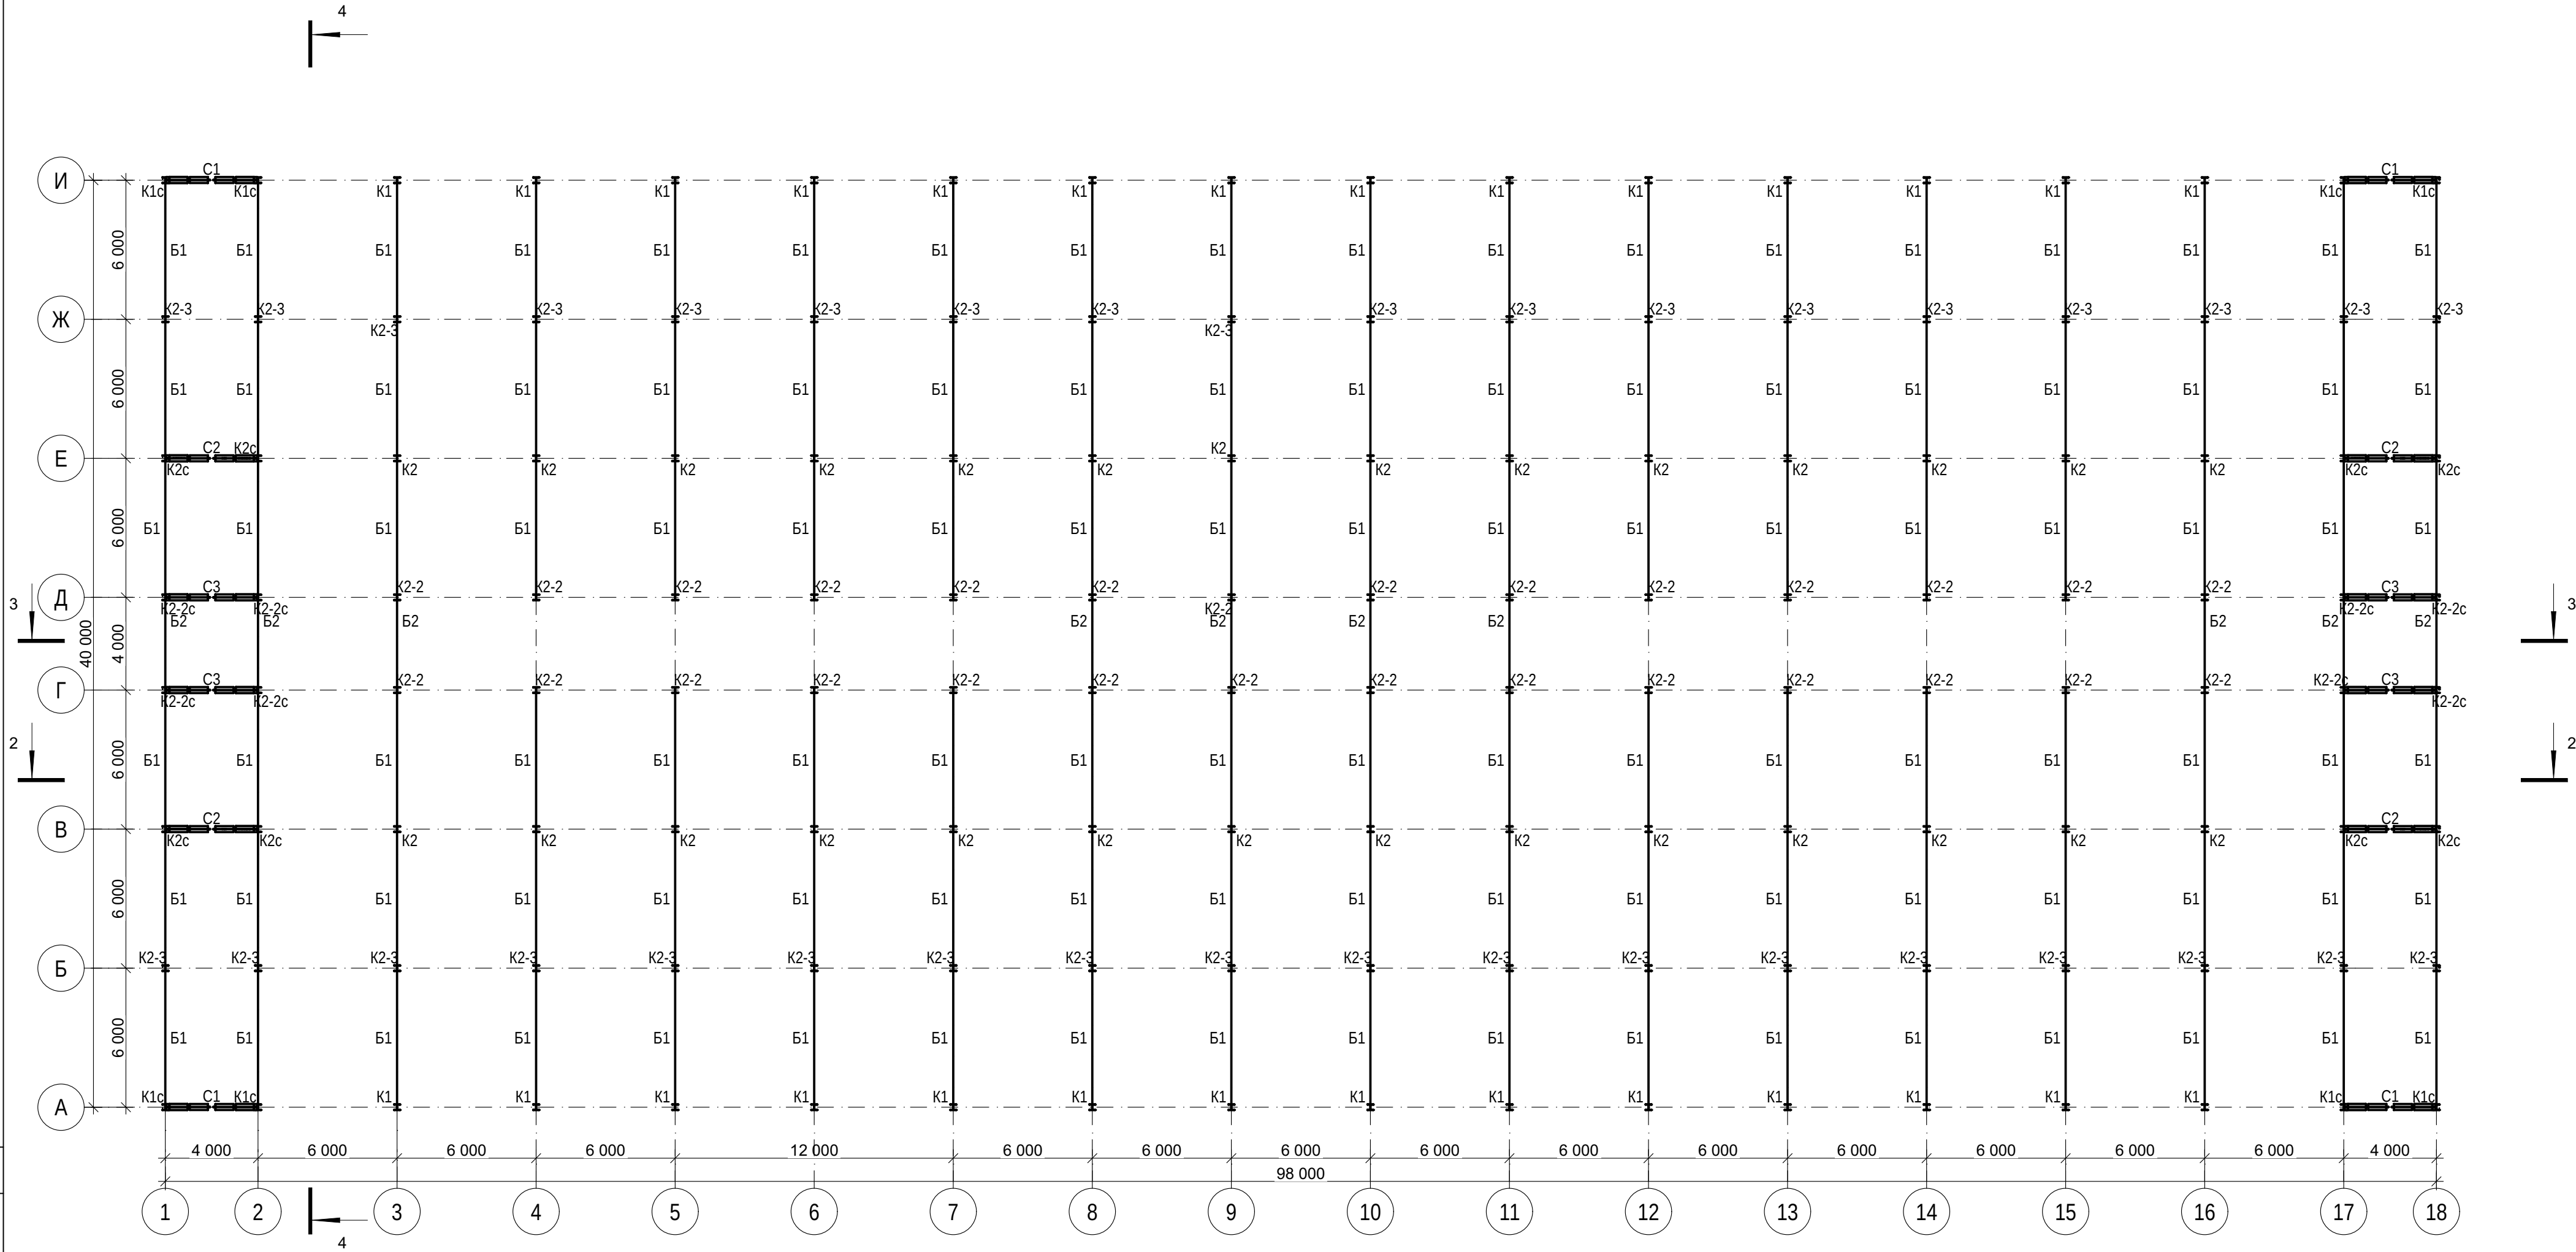

ПРИМЕЧАНИЯ:

- 1) Общие указания см. лист 10;
2) Отметка верха балки: +3,640;
3) Разрезы см. листы 15 - 16.

Согласовано					
Взам. инв. №					
Подп. и дата					
Инв. № подл.					

						ОПР-01/24/2024-КР.ГЧ			
						"Современный оптово-продовольственный рынок (ОПР) по адресу: Донецкая область, .г Макеевка, Горняцкий район			
Изм.	Колуч.	Лист	№Док.	Подп.	Дата	Док-павильон (рыба-мясо) №23, №23.2 (по генплану)	Стадия	Лист	Листов
Разраб.							П	06	
Пров.						Схема расположения колонн и балок перекрытия	ООО "Технология"		
Н. контроль									



ПРИМЕЧАНИЯ:

- 1) Смотреть с листами 08, 11, 14;
- 2) Стойки крепить к закладным в плите по грунту; к стальным пластинам в уровне перекрытия;

						ОПР-01/24/2024-КР.ГЧ			
						"Современный оптово-продовольственный рынок (ОПР) по адресу: Донецкая область, .г Макеевка, Горняцкий район			
Изм.	Колуч.	Лист	№Док	Подп.	Дата				
Разраб.						Док-павильон (рыба-мясо) №23, №23.2 (по генплану)	Стадия	Лист	Листов
Пров.							П	07	
Н. контроль						Схема расположения стоек перегородок 1-го этажа	ООО "Технология"		

Инв. № подл.	Подп. и дата	Взам. инв. №	Согласовано	






ПРИМЕЧАНИЯ:

1) Смотреть с листами 07, 11, 14;

2) Стойки крепить к закладным в плите по грунту; к конструкциям каркаса


Формат А2

Согласовано			Взам. инв. №	Подп. и дата	Инв. № подл.

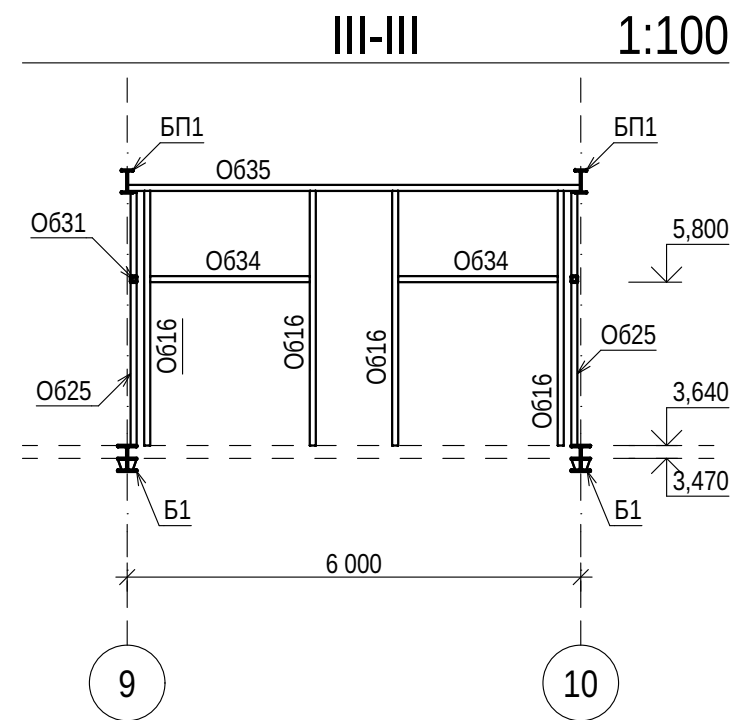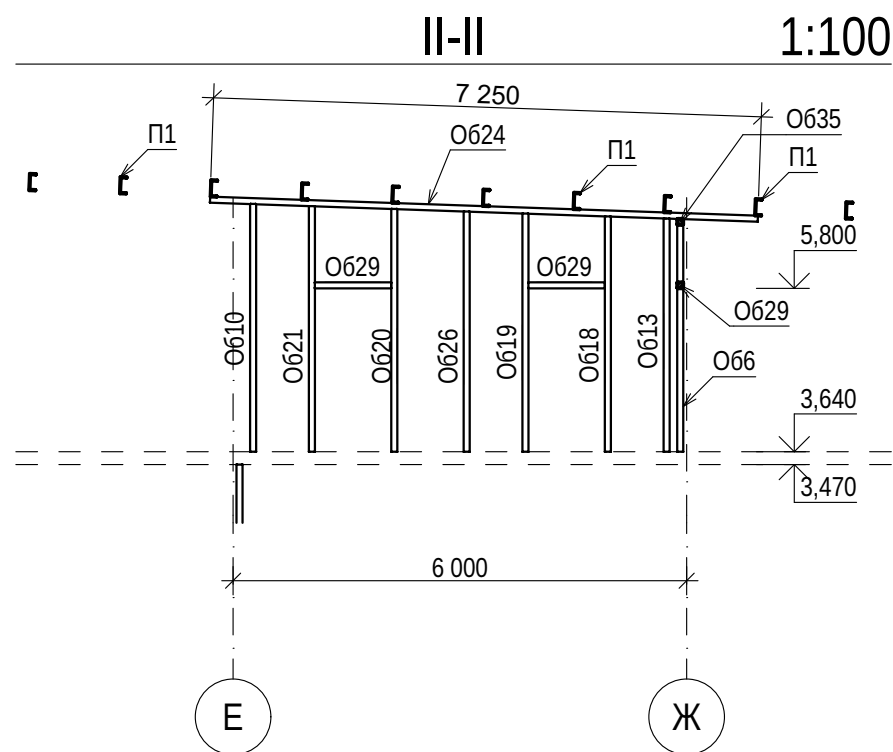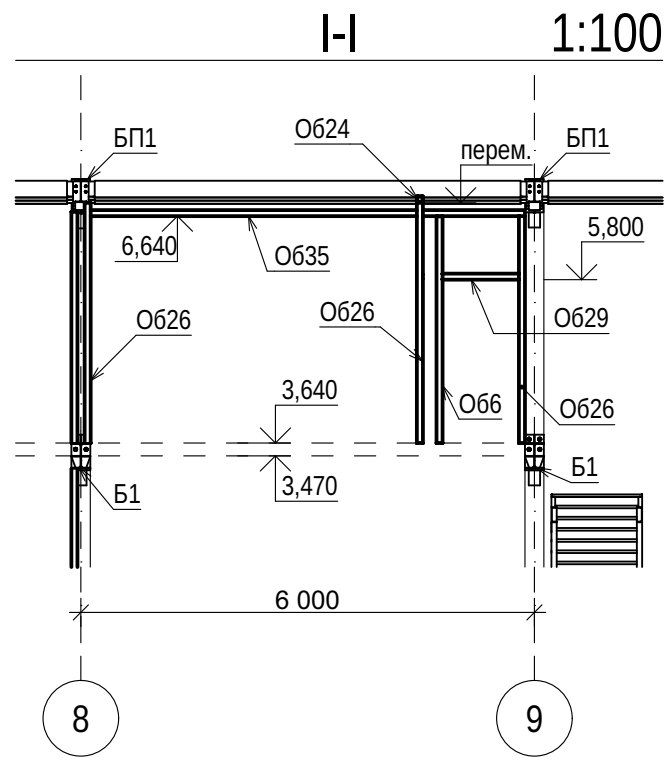

						ОПР-01/24/2024-КР.ГЧ			
						"Современный оптово-продовольственный рынок (ОПР) по адресу: Донецкая область, .г Макеевка, Горняцкий район			
Изм.	Кол.уч.	Лист	№Док.	Подп.	Дата	Док-павильон (рыба-мясо) №23, №23.2 (по генплану)	Стадия	Лист	Листов
Разраб.							П	09	
Пров.									
Н. контроль						Сечения I-I, II-II, III-III	ООО "Технология"		



СХЕМА РАСПОЛОЖЕНИЯ БАЛОК ПОКРЫТИЯ

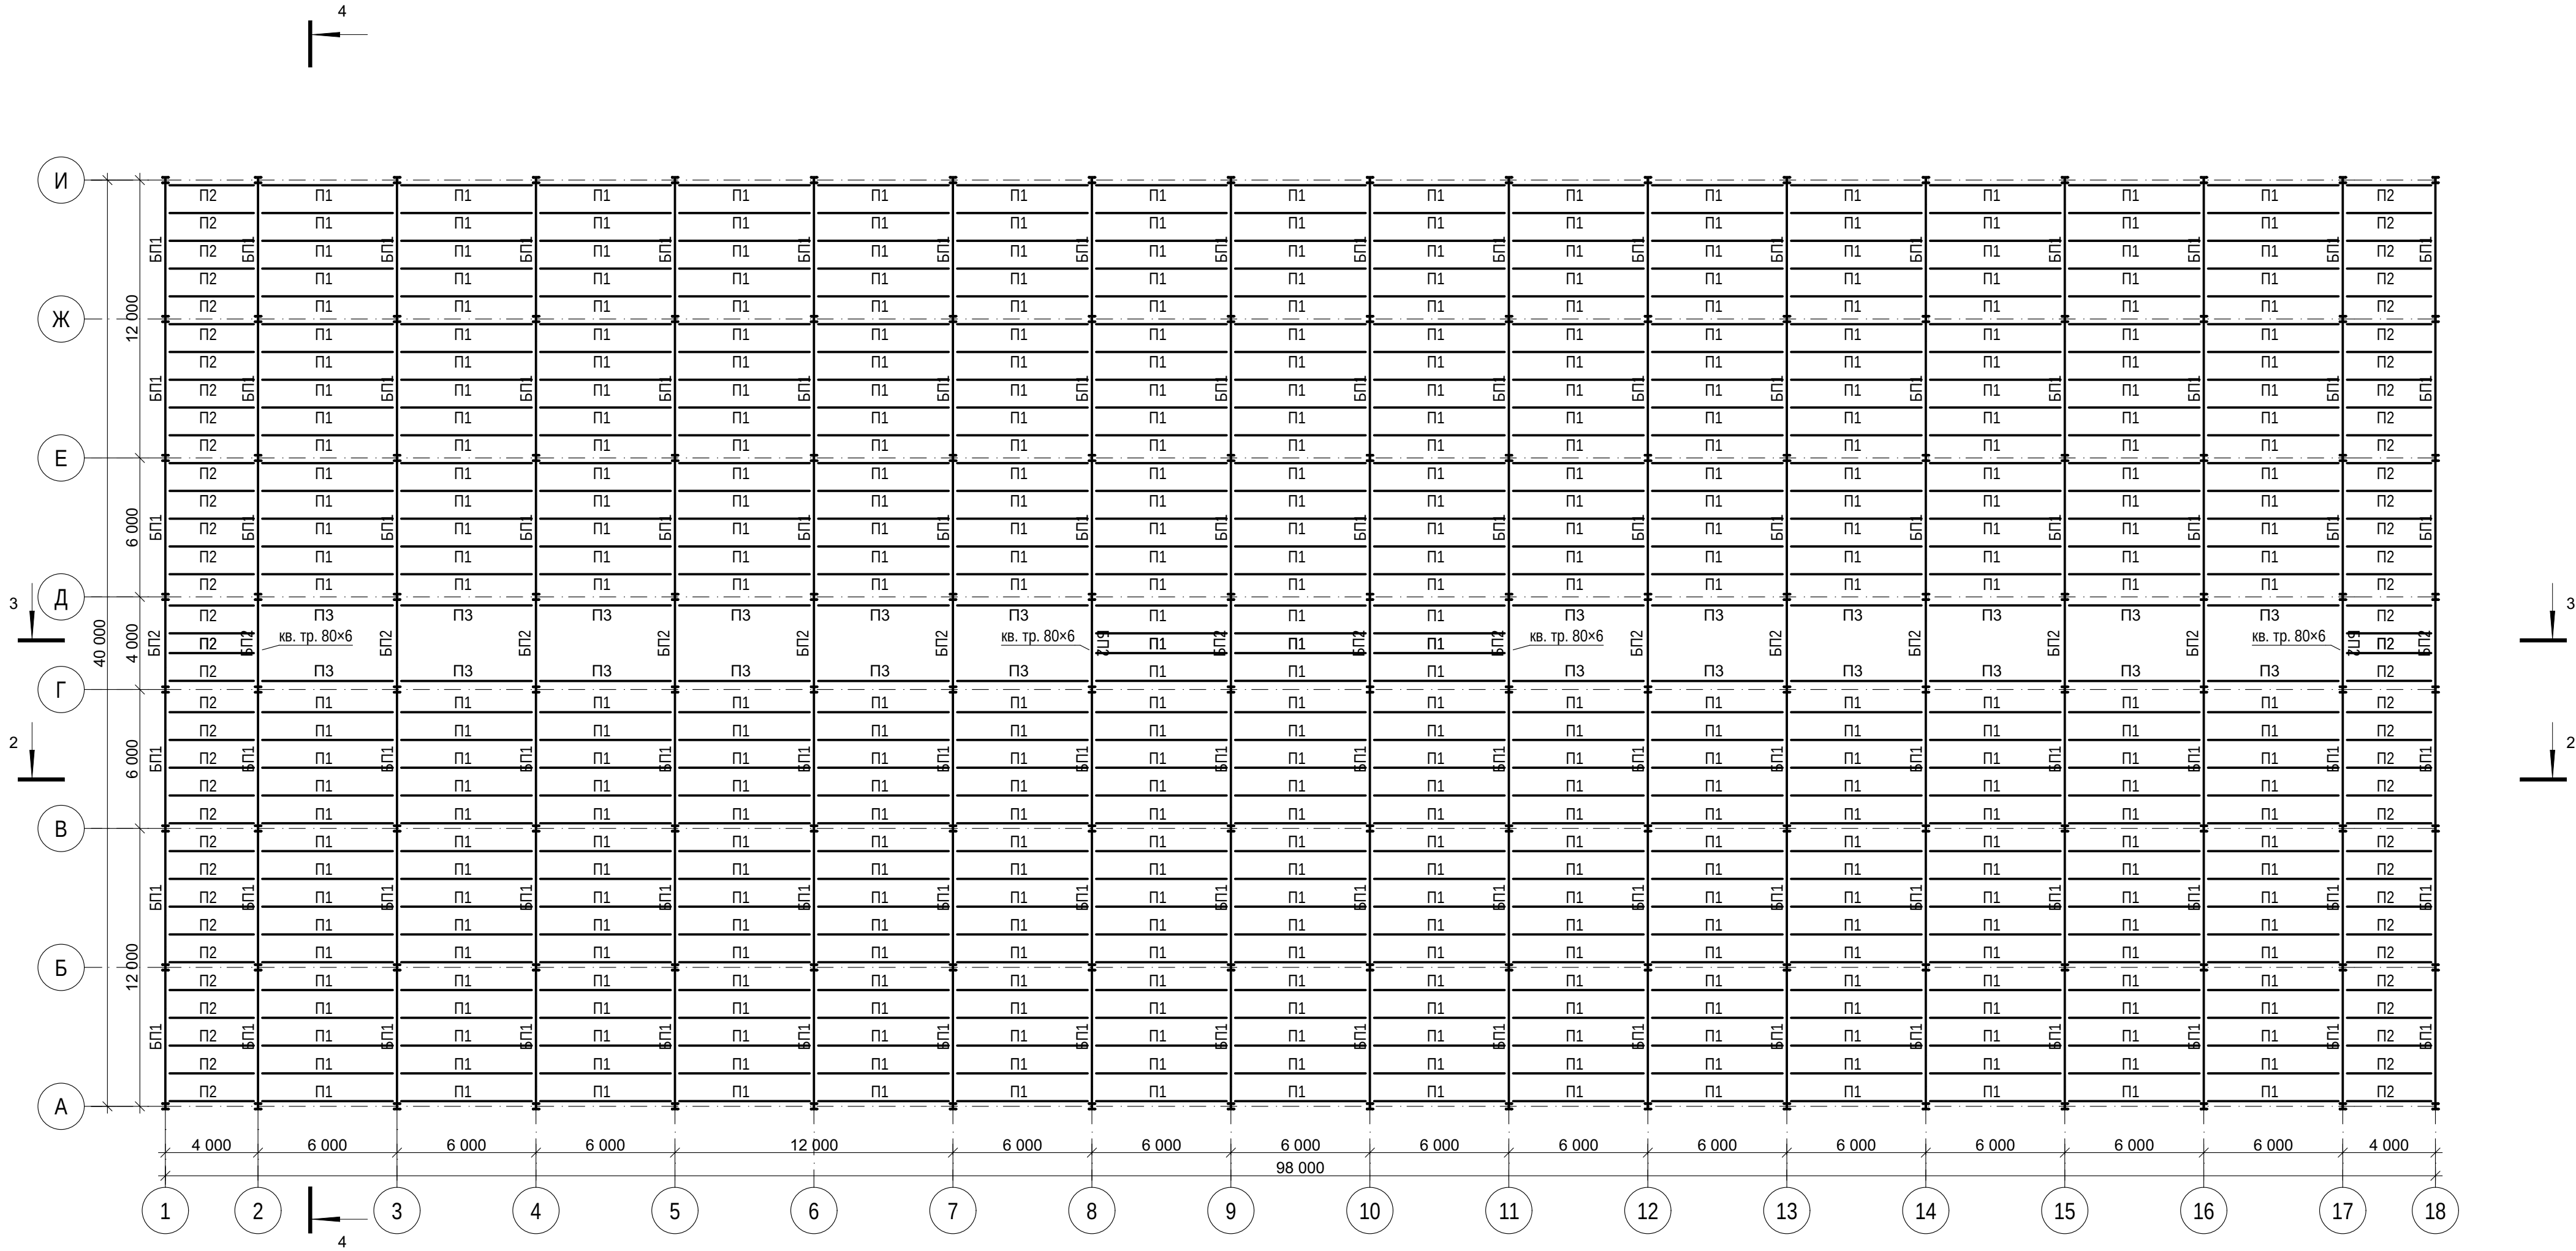

ПРИМЕЧАНИЯ:

- 1) Материал конструкций: фасонный и трубный прокат - сталь С255; листовой прокат - сталь С345;
- 2) Крепление балок выполнять на высокопрочные болты; крепление прогоны выполнять на болты класса прочнотси 5.8; соединение деталей в изделия выполнять на полуавтоматическую сварку в среде защитного газа;
- 3)Металлические конструкции окрасить грунтовкой ГФ-021 и эмалью ПФ-115 или эквивалентными составами;
- 4) Смотреть совместно с листом 06;


						ОПР-01/24/2024-КР.ГЧ			
						"Современный оптово-продовольственный рынок (ОПР) по адресу: Донецкая область, г. Макеевка, Горняцкий район			
Изм.	Колуч.	Лист	№Док.	Подп.	Дата				
Разраб.						Док-павильон (рыба-мясо) №23, №23.2 (по генплану)	Стадия	Лист	Листов
Пров.							П	10	
Н. контроль						Схема расположения балок покрытия	ООО "Технология"		

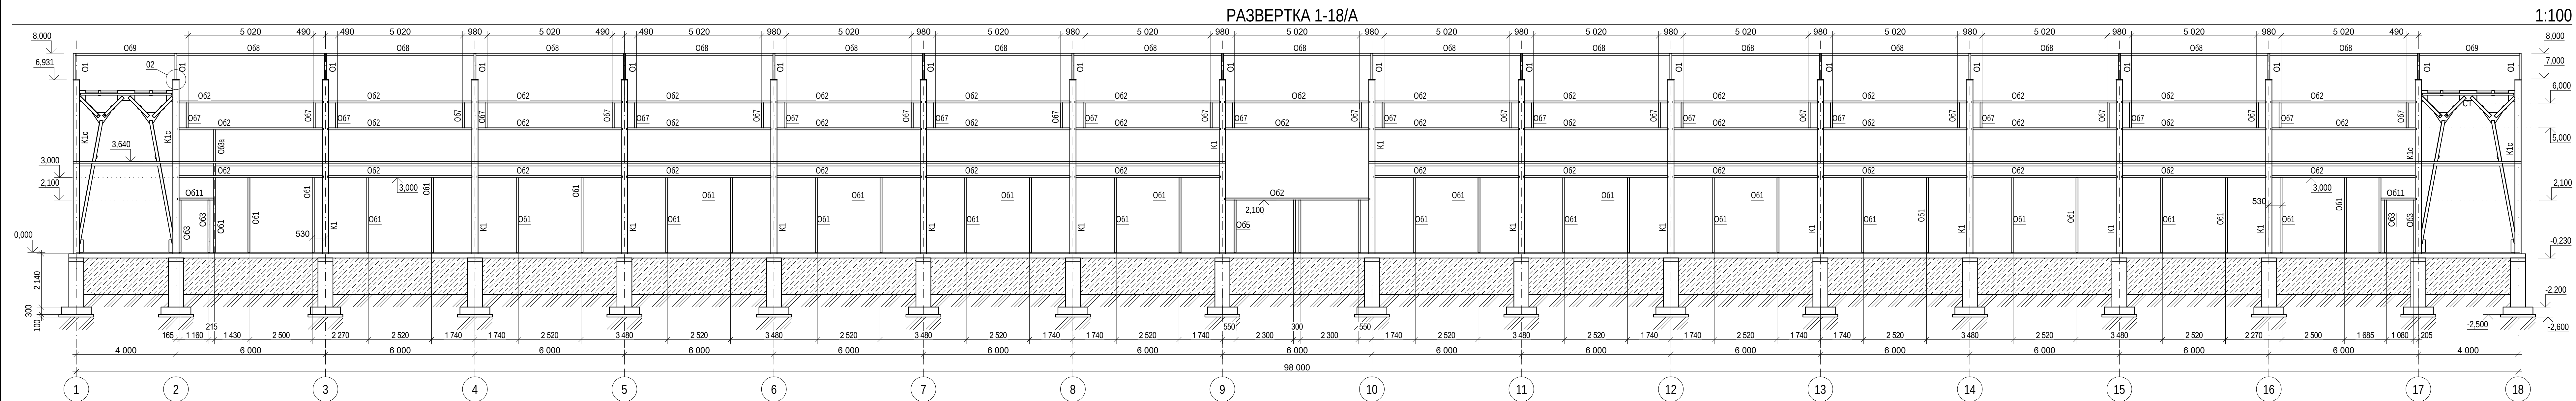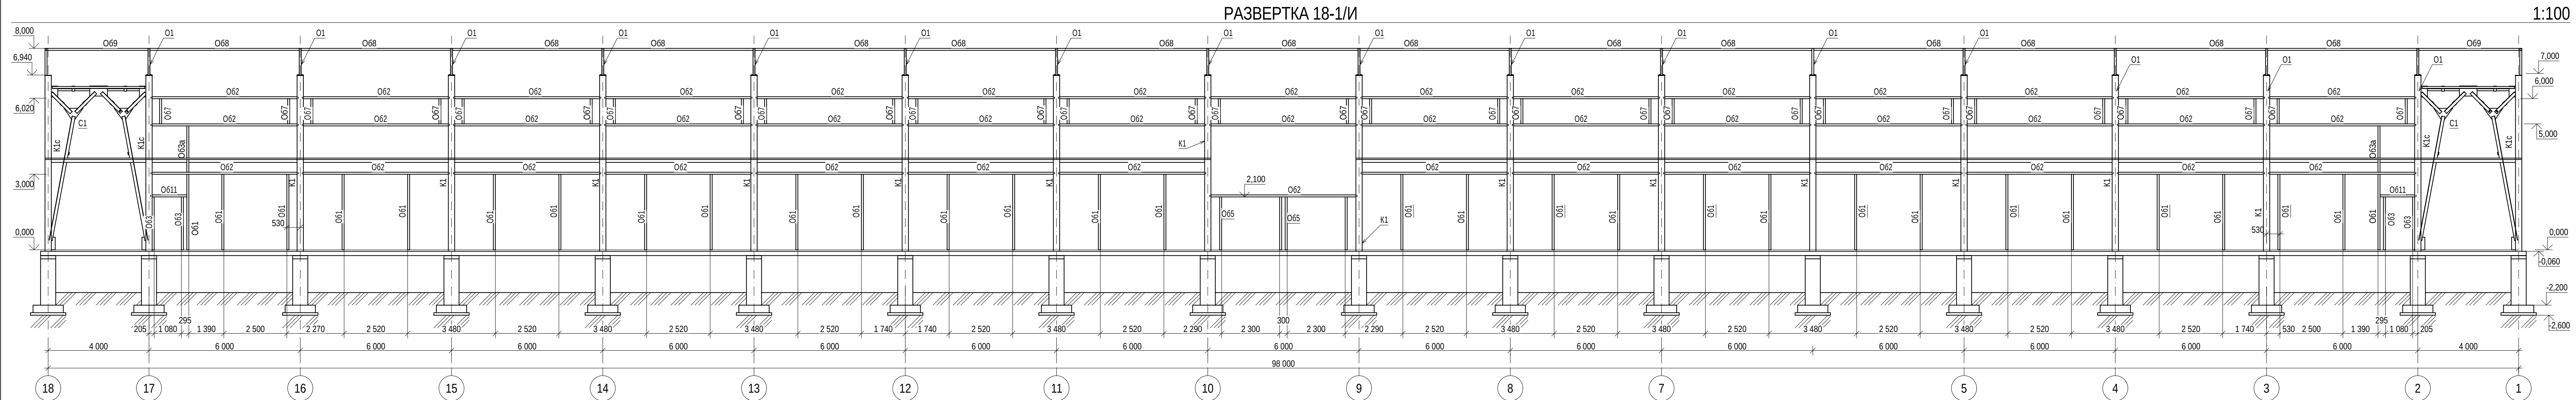

						ОПР-01/24/2024-КР.ГЧ			
						"Современный оптово-продовольственный рынок (ОПР) по адресу: Донецкая область, г. Макеевка, Горняцкий район			
Изм.	Колуч.	Лист	№док	Подп.	Дата	Док-павильон (рыба-мясо) №23, №23.2 (по генплану)	Стадия	Лист	Листов
Разраб.					01.25		П	11	
Пров.					01.25				
Н. контроль						Развертки 1-18/А, 18-1/И	ООО "Технология"		


РАЗВЕРТКА 1-18/В

1:200

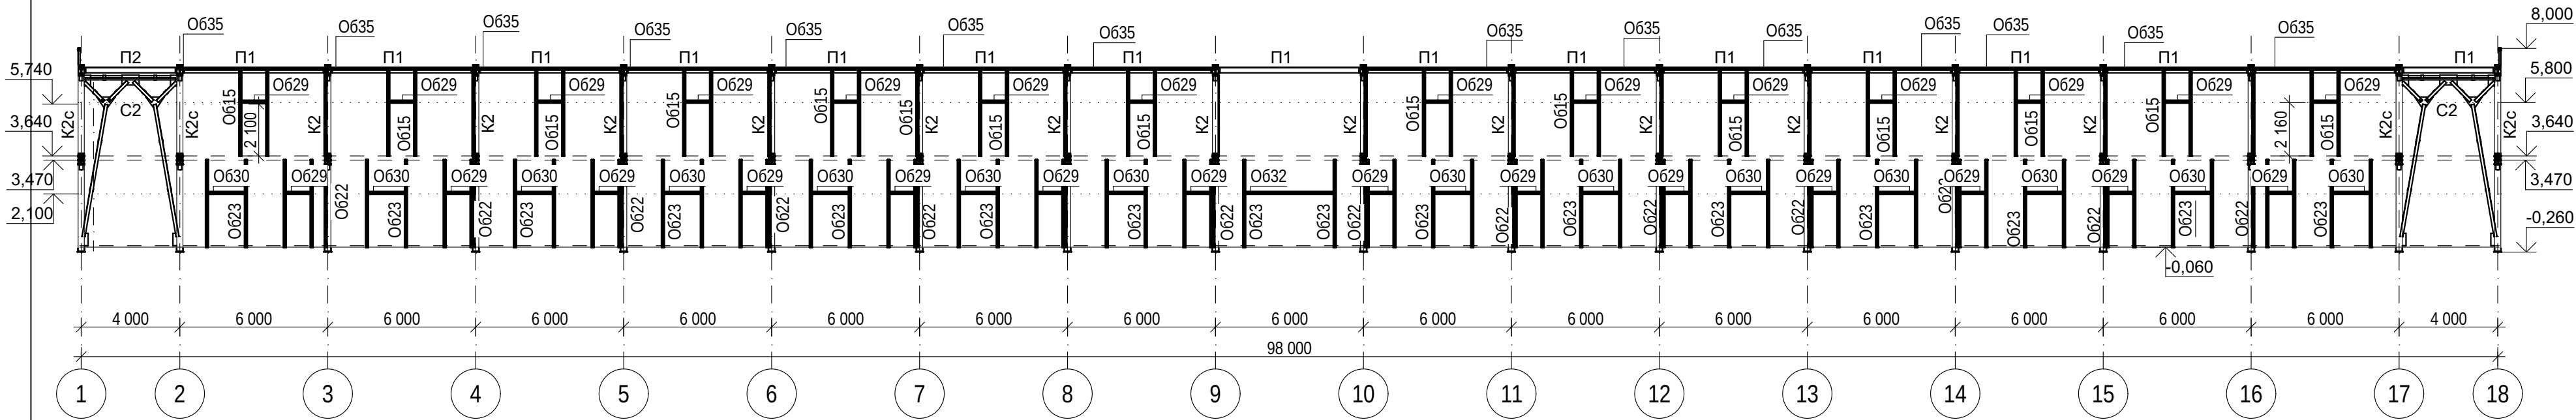

РАЗВЕРТКА 1-18/Г


1:200

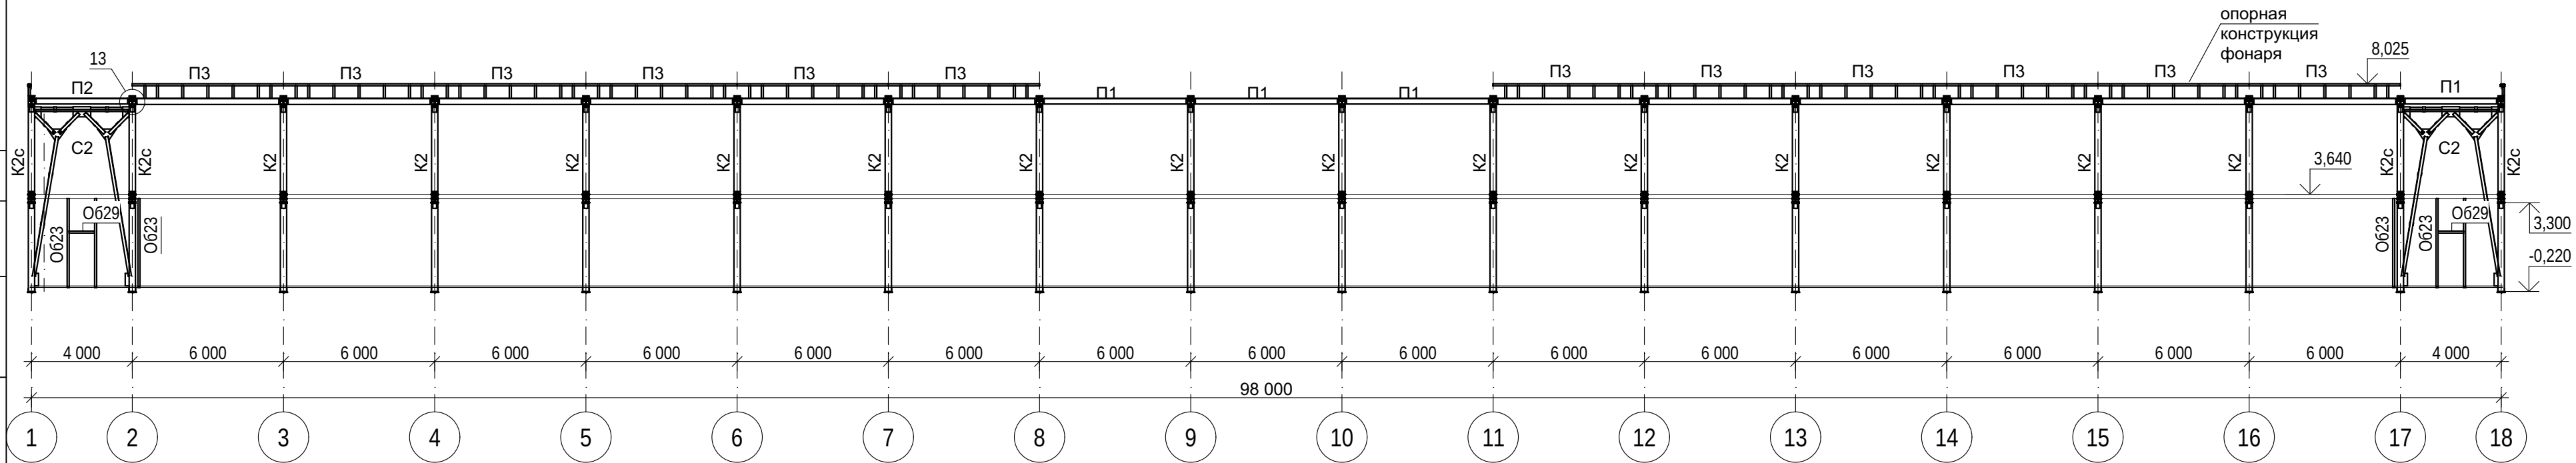


Согласовано					
Взам. инв. №					
Подп. и дата					
Инв. № подл.					

						ОПР-01/24/2024-КР.ГЧ				
						"Современный оптово-продовольственный рынок (ОПР) по адресу: Донецкая область, г.Макеевка, Горняцкий район				
Изм.	Кол.уч.	Лист	№Док.	Подп.	Дата	Док-павильон (рыба-мясо) №23, №23.2 (по генплану)	Стация	Лист	Листов	
Разраб.					01.25		П	12		
Пров.					01.25					
Н. контроль						Развертка 1-18/В, 1-18/Г	ООО "Технология"			

1:200

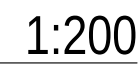


1:200

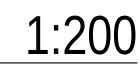

Формат А4х3


РАЗВЕРТКА А-И/18

1:100

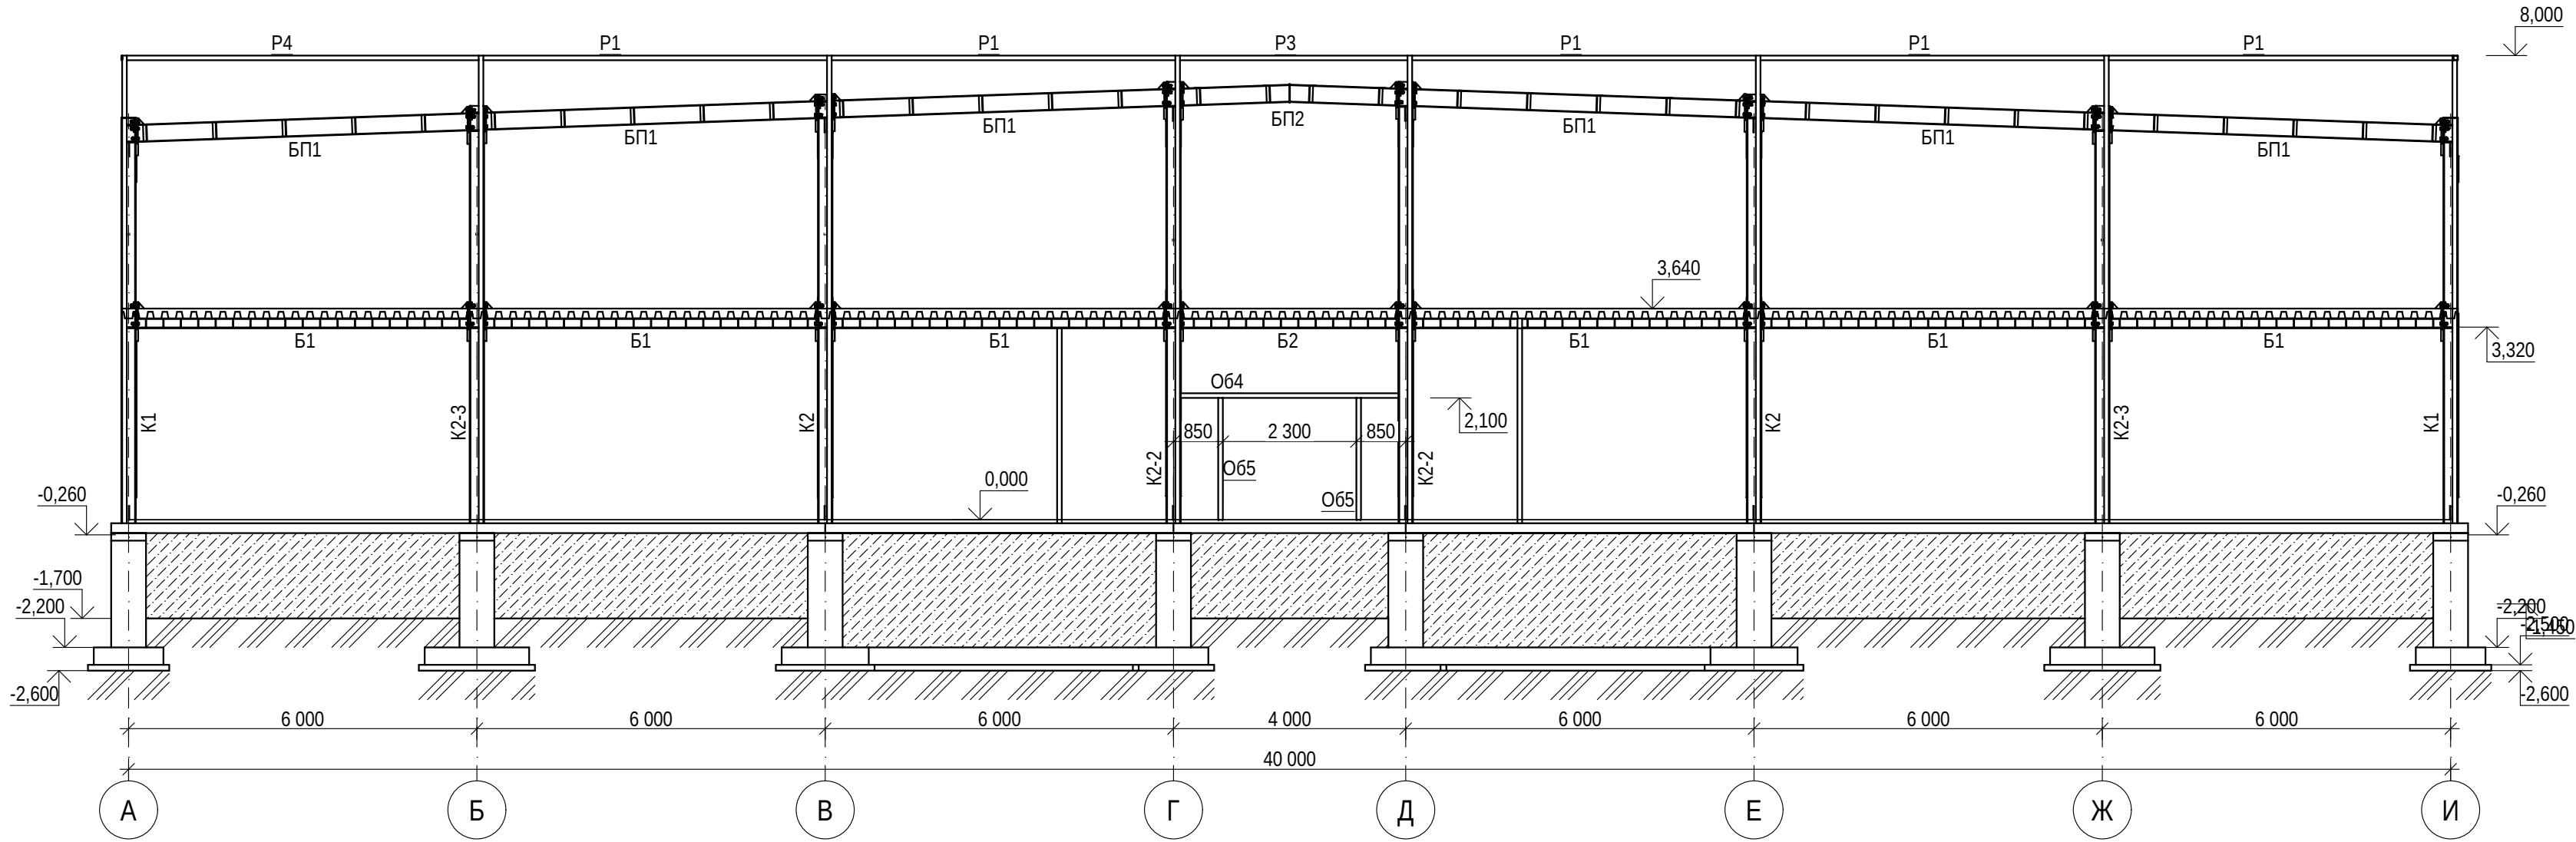

РАЗВЕРТКА И-А/1

1:100

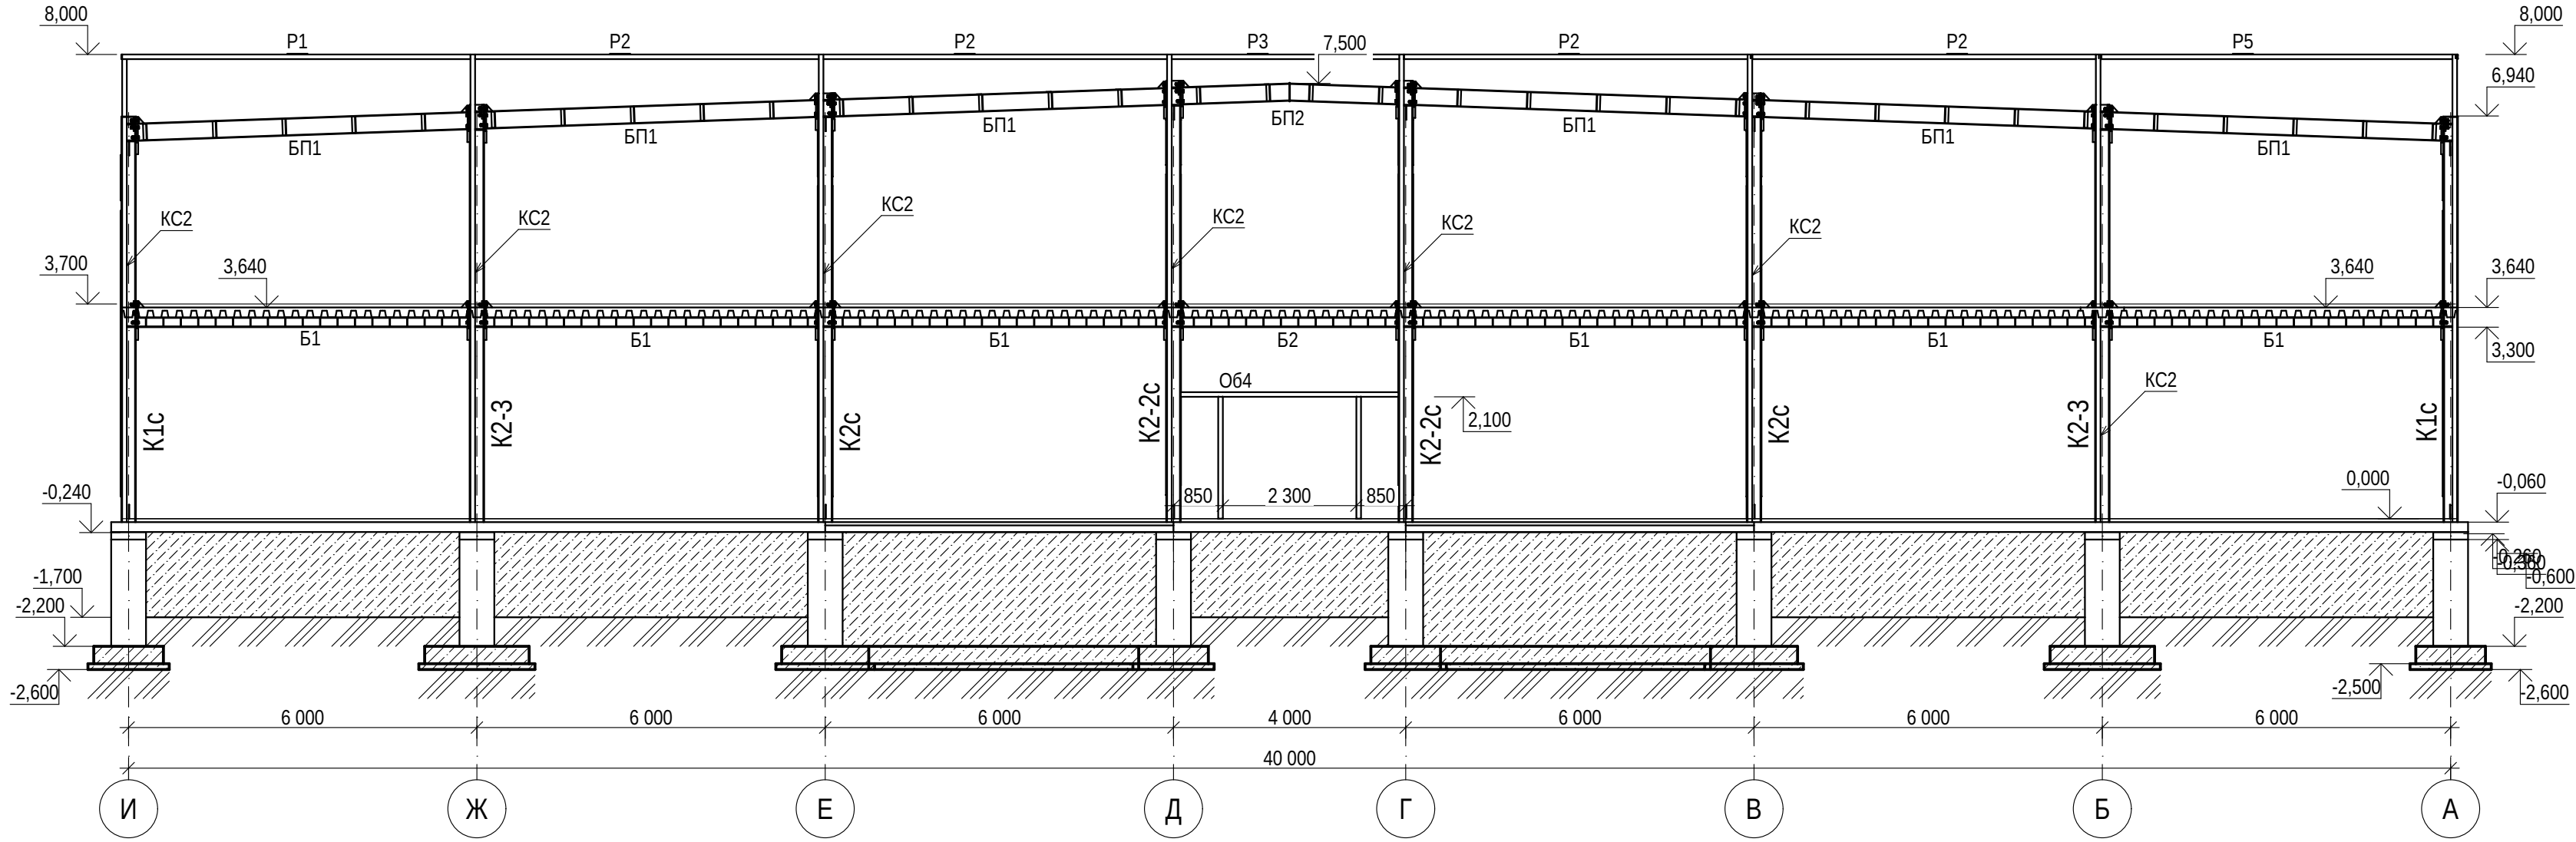


Согласовано	
Взам. инв. №	
Подп. и дата	
Инв. № подл.	

						ОПР-01/24/2024-КР.ГЧ					
						"Современный оптово-продовольственный рынок (ОПР) по адресу: Донецкая область, .г Макеевка, Горняцкий район					
Изм.	Колуч.	Лист	№Док	Подп.	Дата	Док-павильон (рыба-мясо) №23, №23.2 (по генплану)			Стадия	Лист	Листов
Разраб.									П	14	
Пров.						Развертки А-И/18, И-А/1			ООО "Технология"		
Н. контроль											





PA3PE3 1-1

1:100

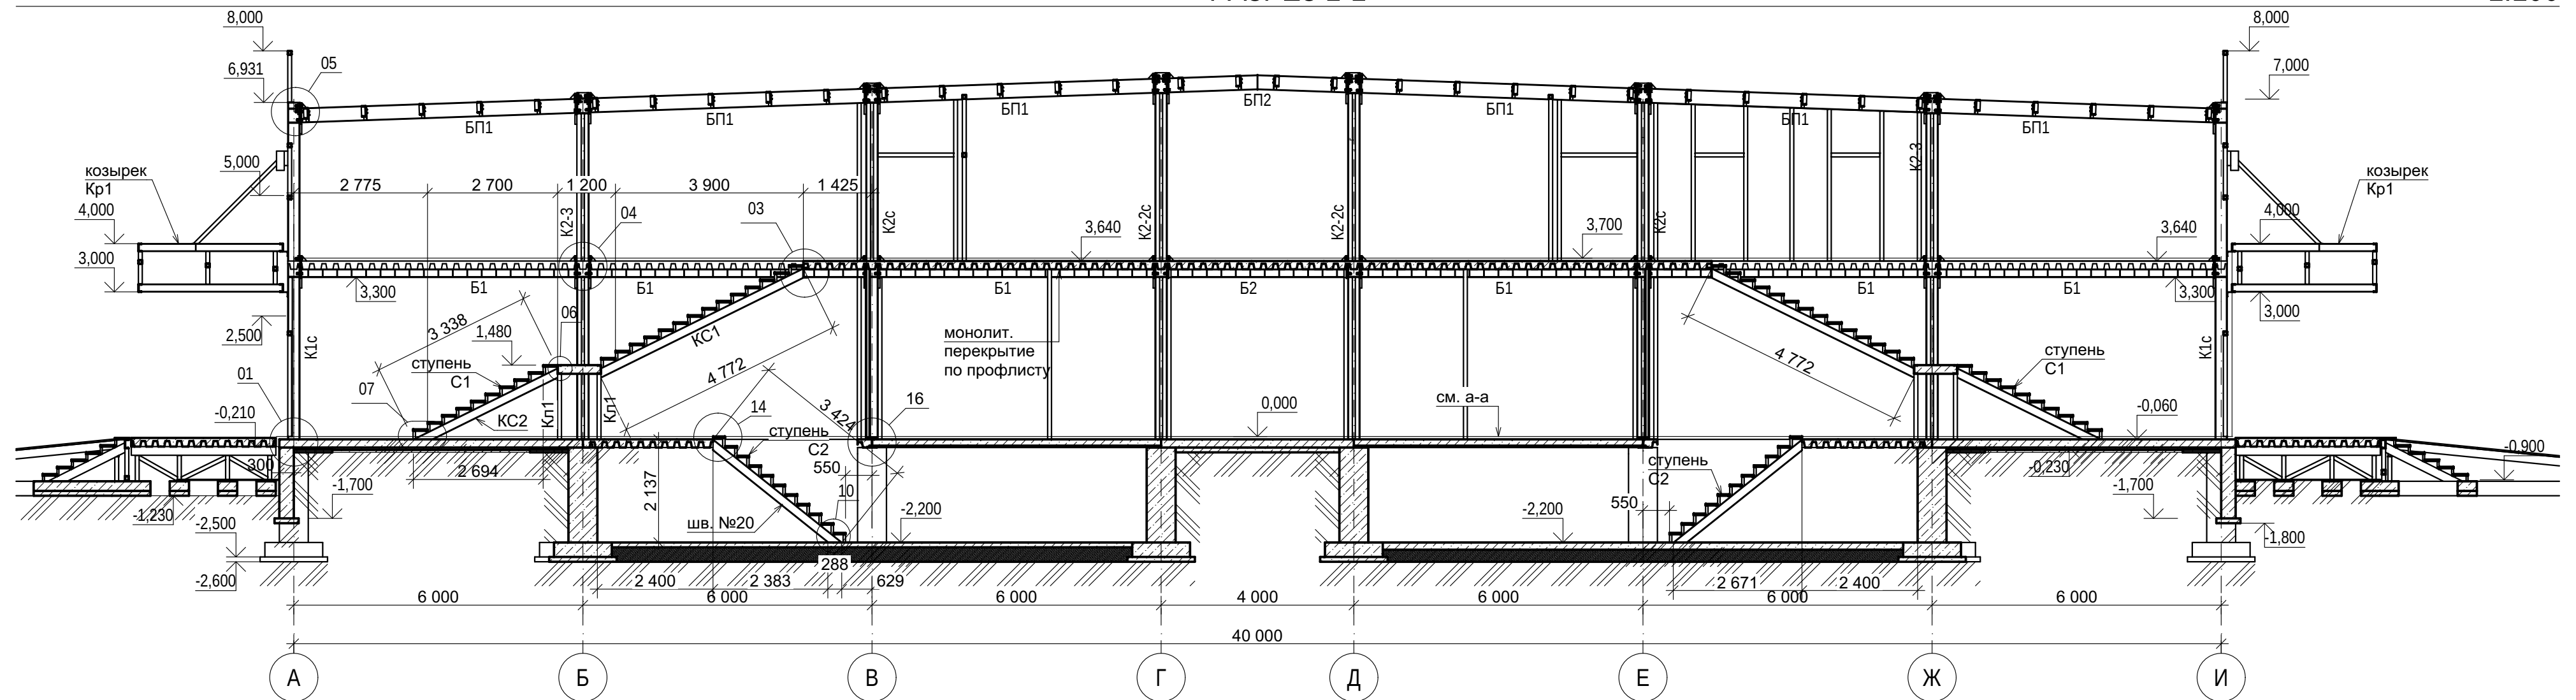

PA3PE3 2-2

1:200

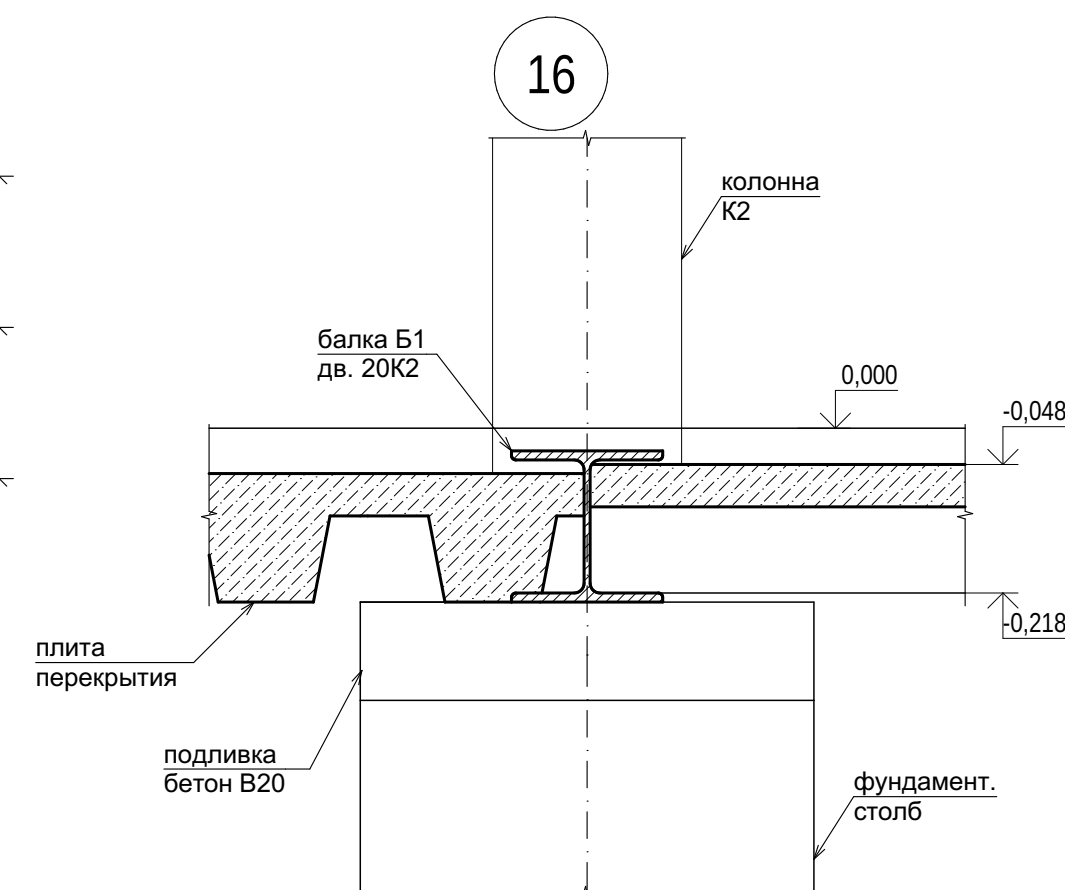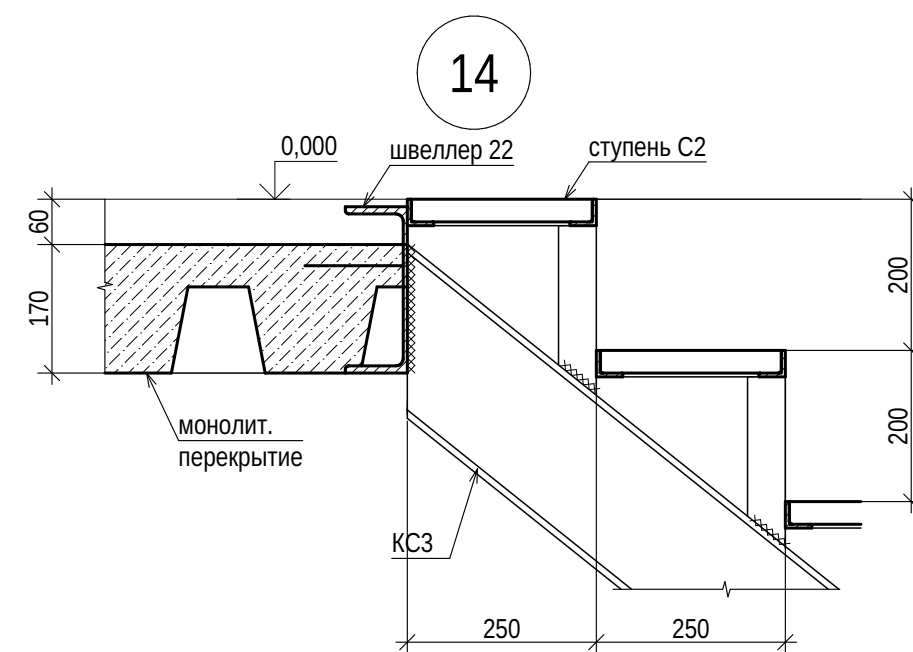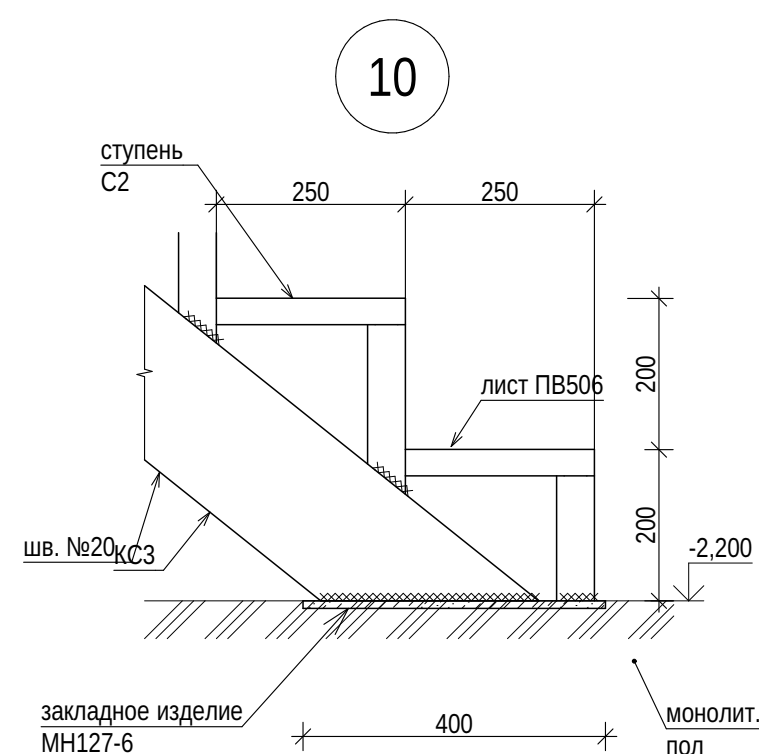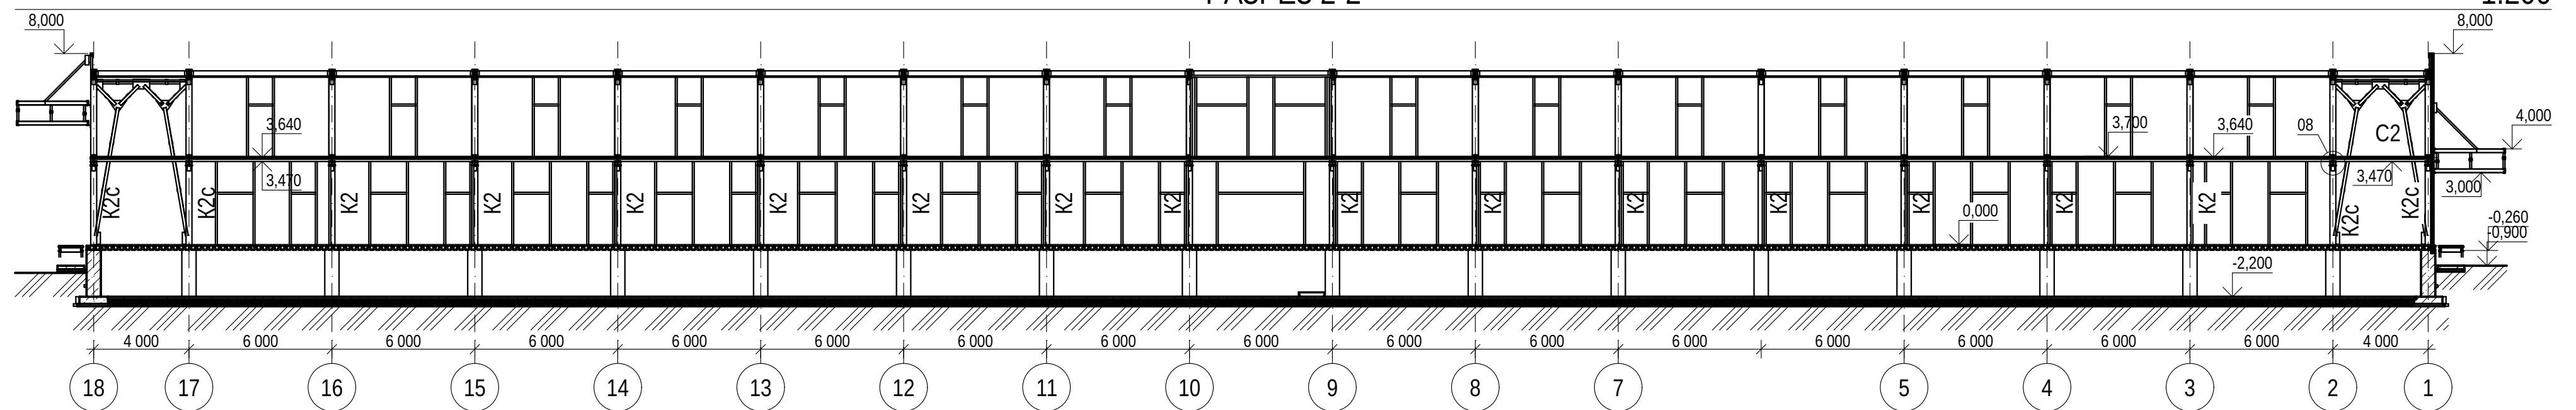

ПРИМЕЧАНИЯ:


1) Разреза замаркированы на листе 06

						ОПР-01/24/2024-КР.ГЧ			
						"Современный оптово-продовольственный рынок (ОПР) по адресу: Донецкая область, .г Макеевка, Горняцкий район			
Изм.	Колуч.	Лист	№Док.	Подп.	Дата	Док-павильон (рыба-мясо) №23, №23.2 (по генплану)	Стадия	Лист	Листов
Разраб.							П	15	
Пров.									
						Разрезы 1-1, 2-2	ООО "Технология"		
Н. контроль									

Формат А2



РАЗРЕЗ 3-3

1:200

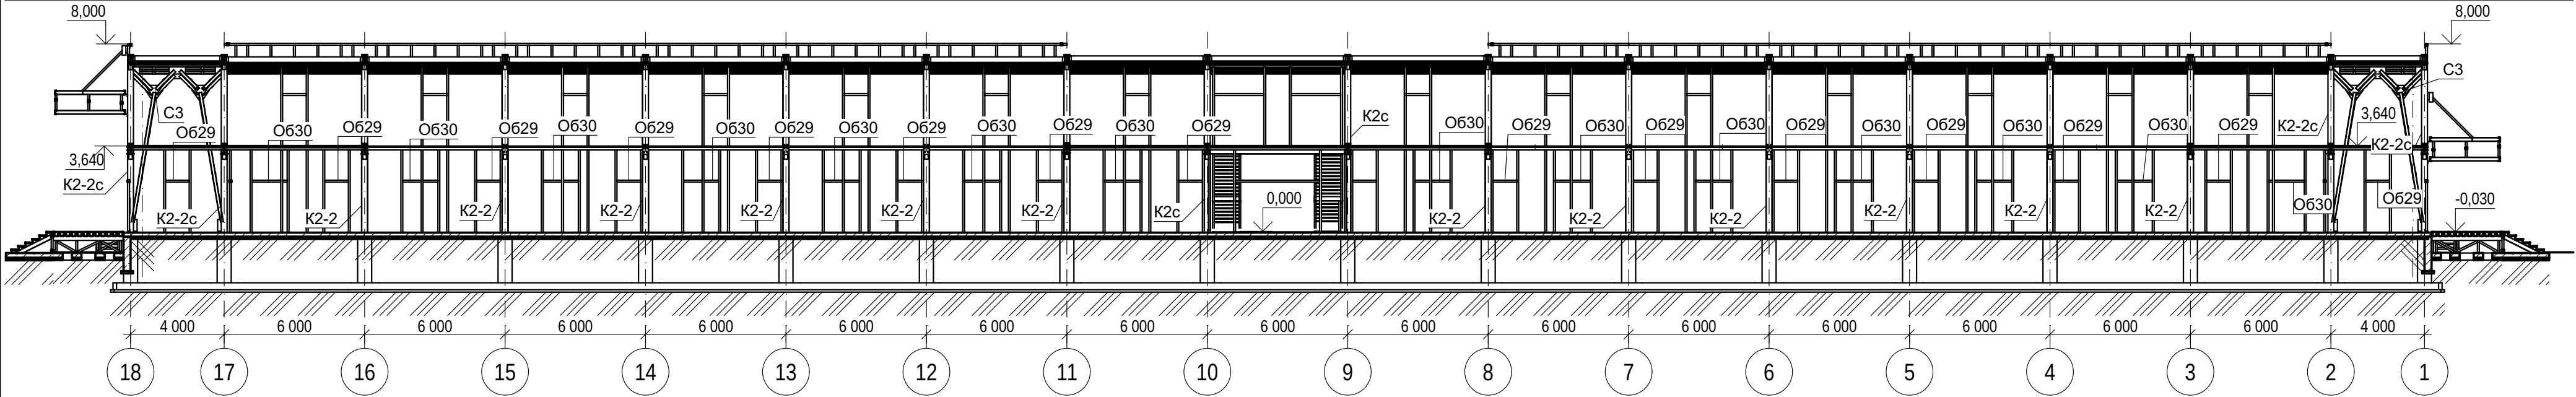





РАЗРЕЗ 4-4

1:200

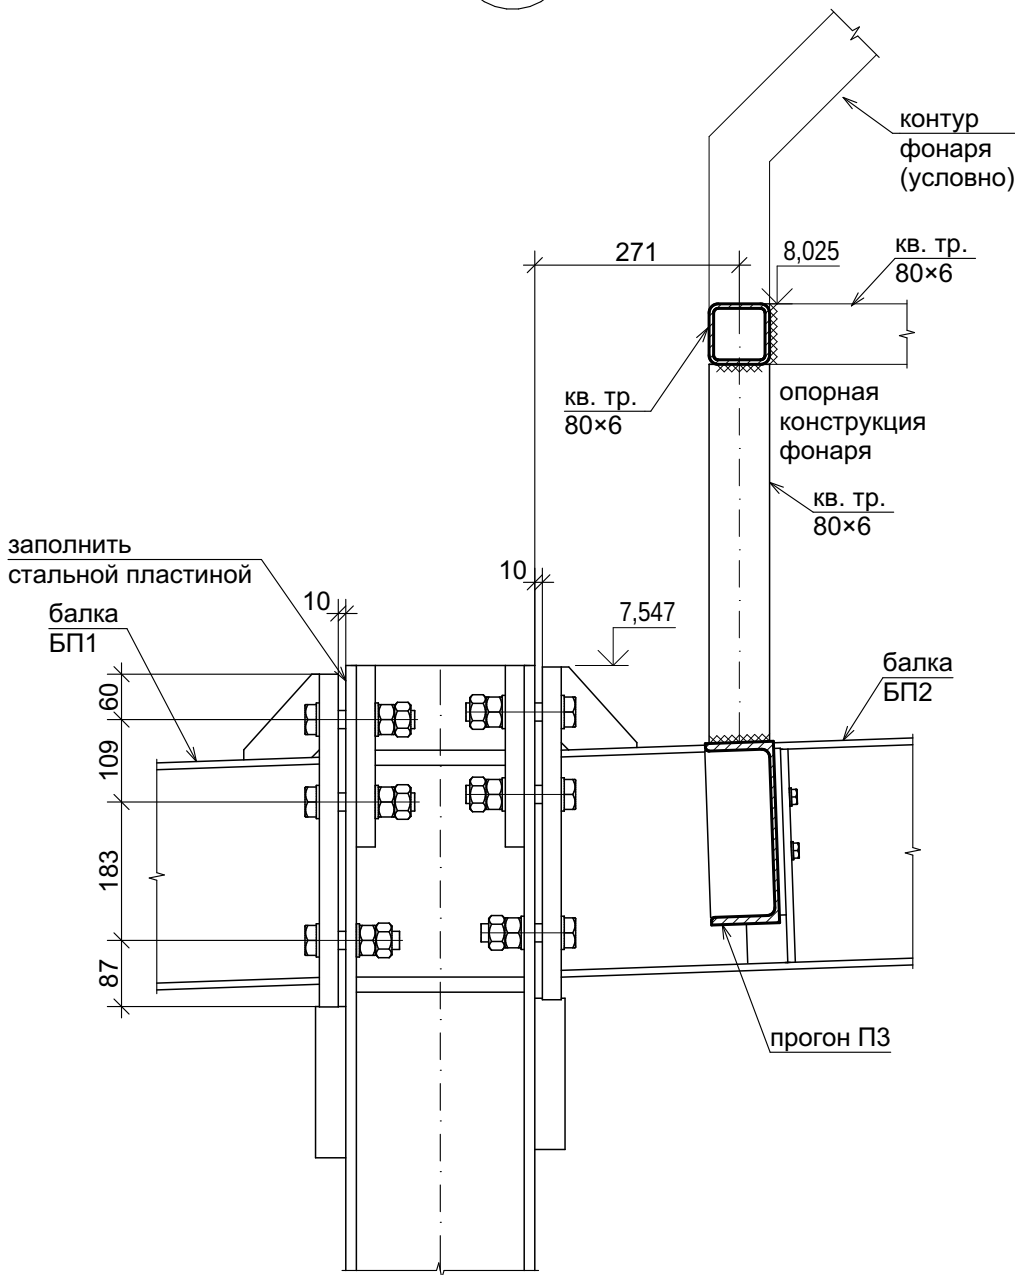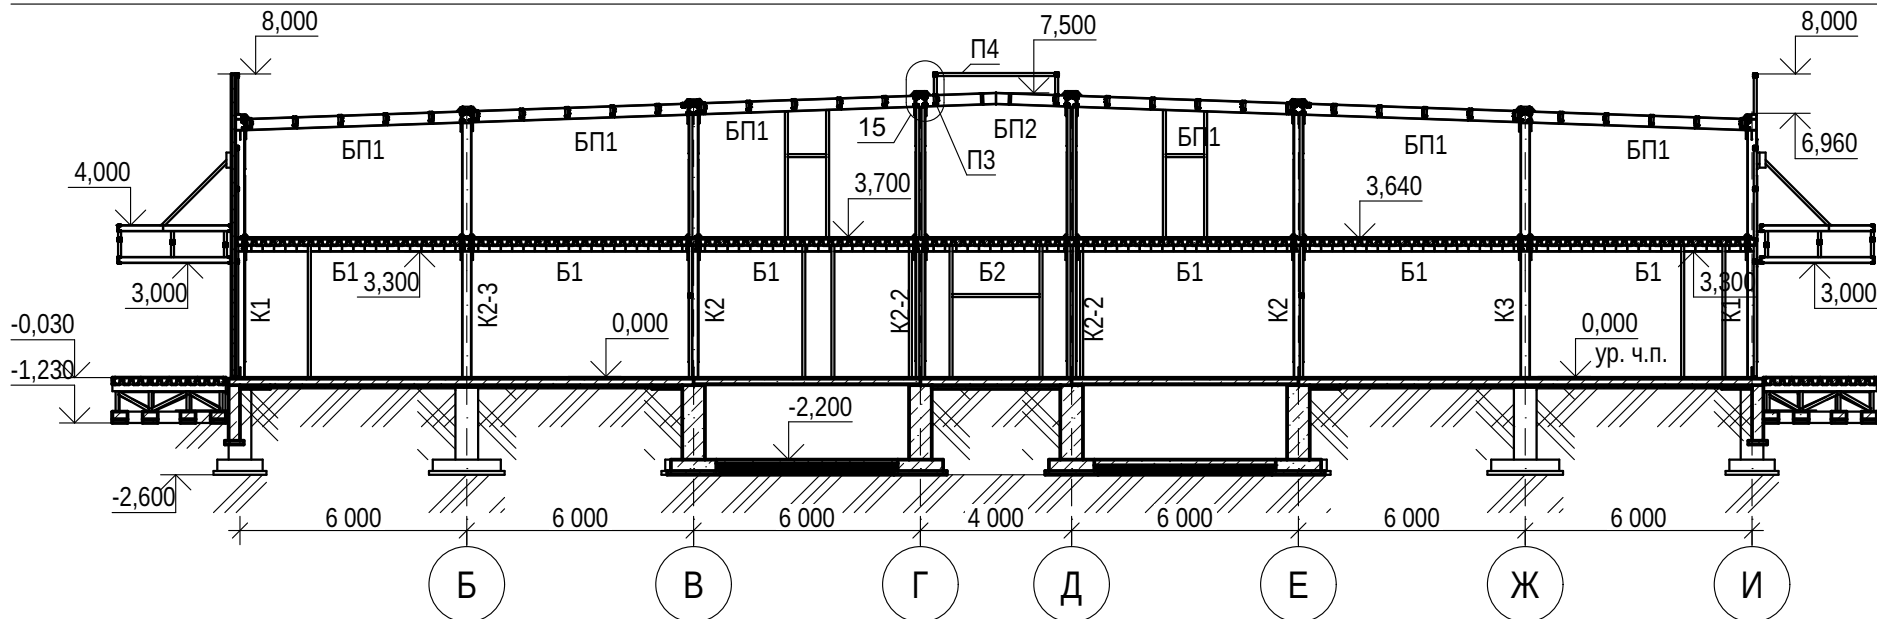

						ОПР-01/24/2024-КР.ГЧ			
						"Современный оптово-продовольственный рынок (ОПР) по адресу: Донецкая область, .г Макеевка, Горняцкий район			
Изм.	Кол.уч.	Лист	№Док.	Подп.	Дата	Док-павильон (рыба-мясо) №23, №23.2 (по генплану)	Стадия	Лист	Листов
Разраб.					01.25		П	16	
Пров.					01.25				
Н. контроль					01.25	Разрезы 3-3, 4-4	ООО "Технология"		

Согласовано					
Взам. инв. №					
Подп. и дата					
Инв. № подл.					

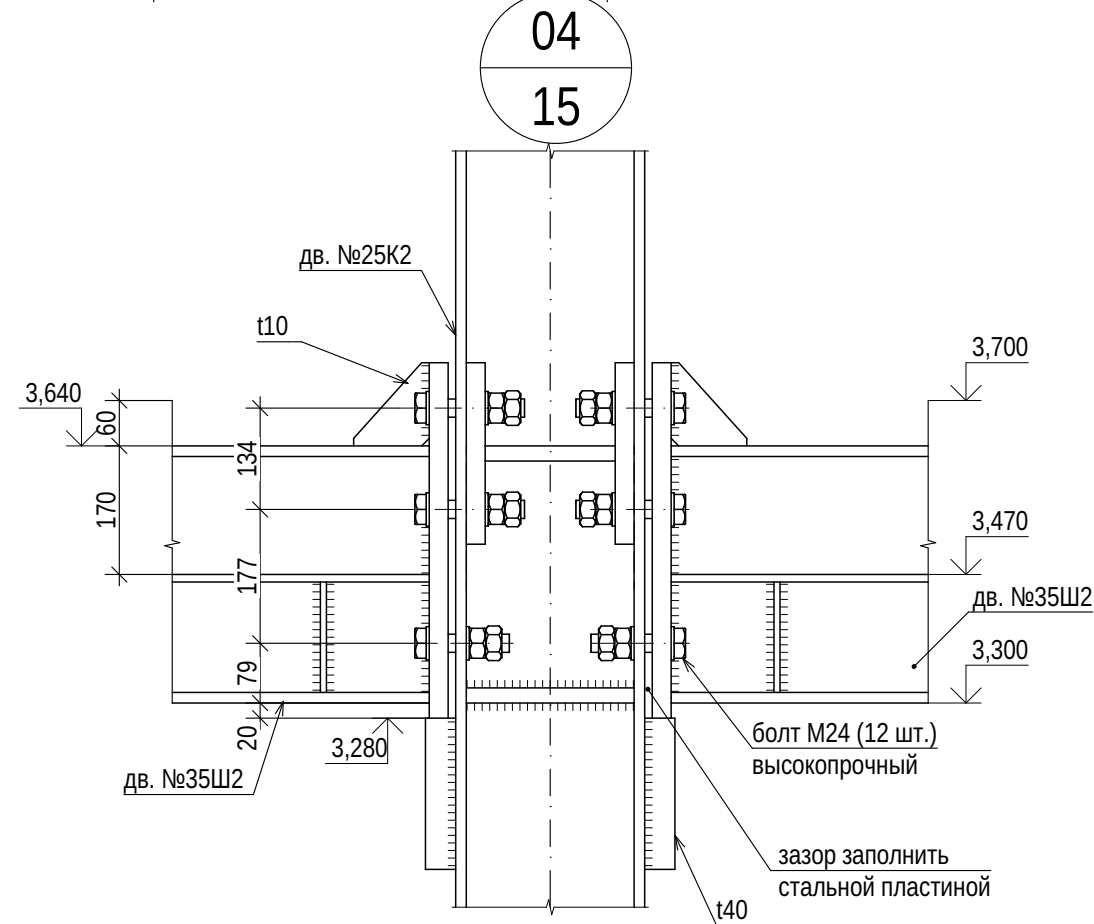
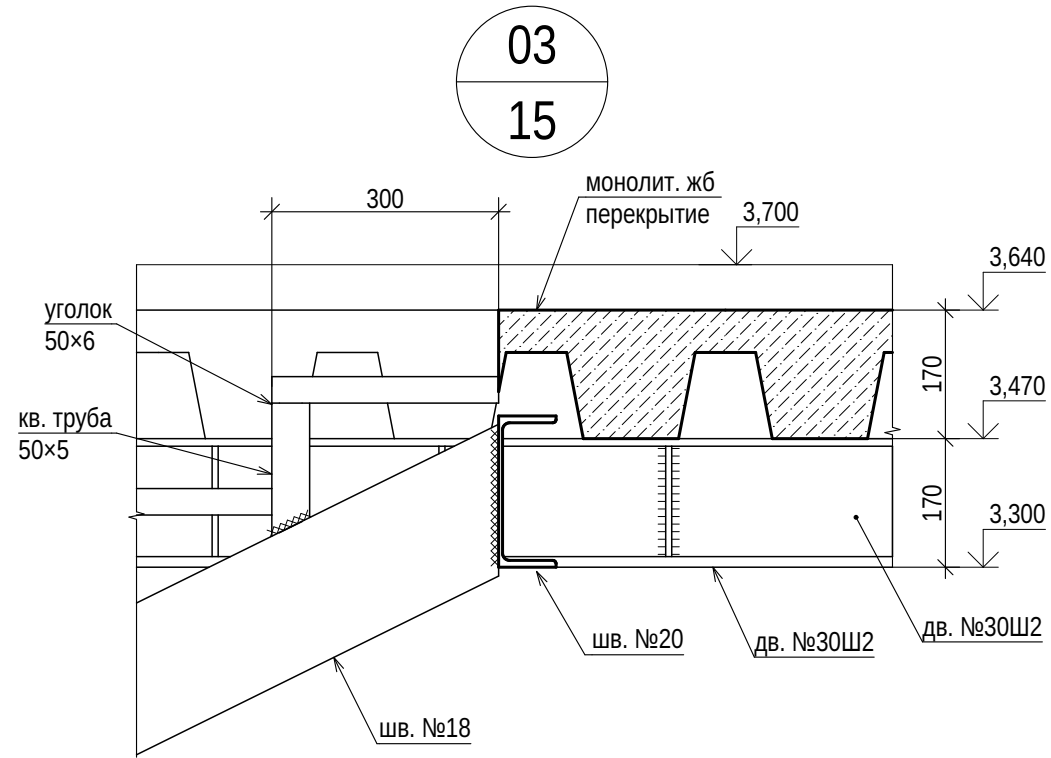
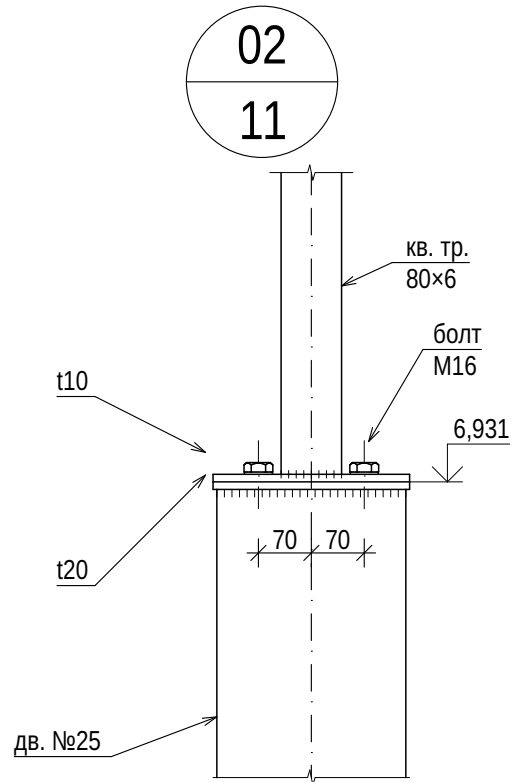
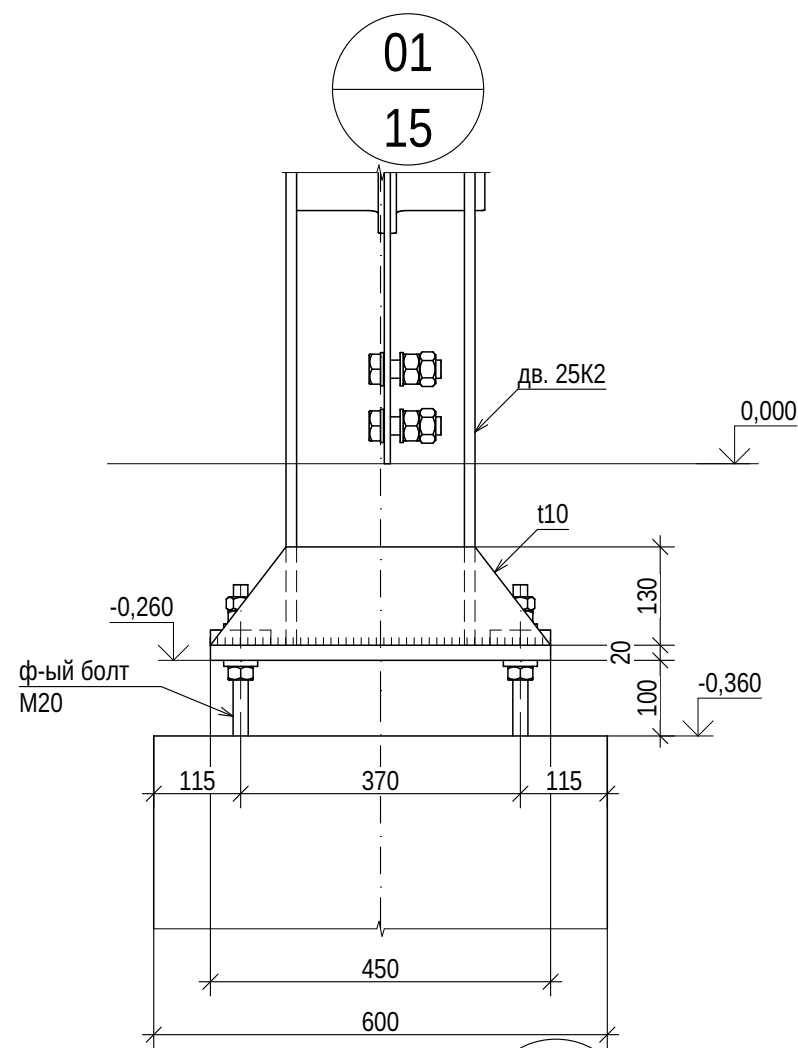


ПРИМЕЧАНИЯ:

- 1) Крепление балок выполнять на высокопрочные болты; крепление прогонов выполнять на сварку; сварка изделий плазменная, в среде защитного газа;
- 2) Металлические конструкции окрасить грунтовкой ГФ-021 и эмалью ПФ-115 или эквивалентными составами;
- 3) Узлы замаркированы на листах 11-15.

						ОПР-01/24/2024-КР.ГЧ			
						"Современный оптово-продовольственный рынок (ОПР) по адресу: Донецкая область, .г Макеевка, Горняцкий район			
Изм.	Кол.уч.	Лист	№Док.	Подп.	Дата	Док-павильон (рыба-мясо) №23, №23.2 (по генплану)	Стадия	Лист	Листов
Разраб.							П	17	
Пров.						Узлы 01-04	ООО "Технология"		
Н. контроль									

Согласовано					
Взам. инв. №					
Подп. и дата					
Инв. № подл.					

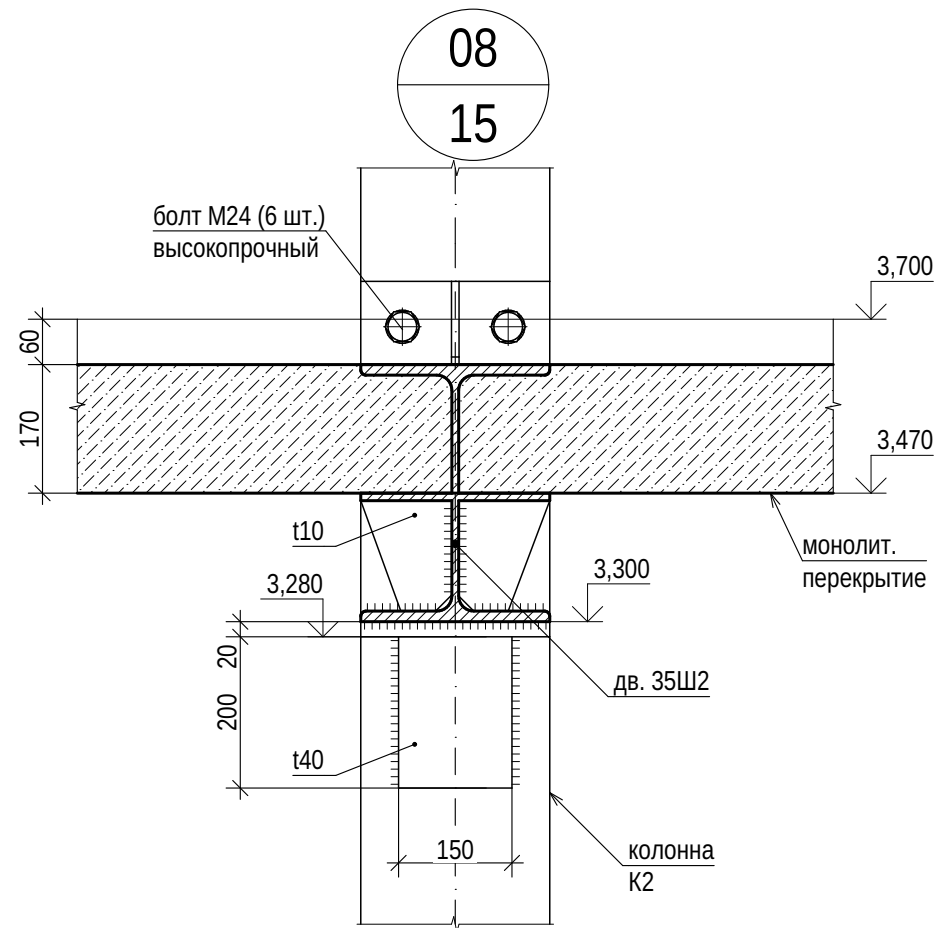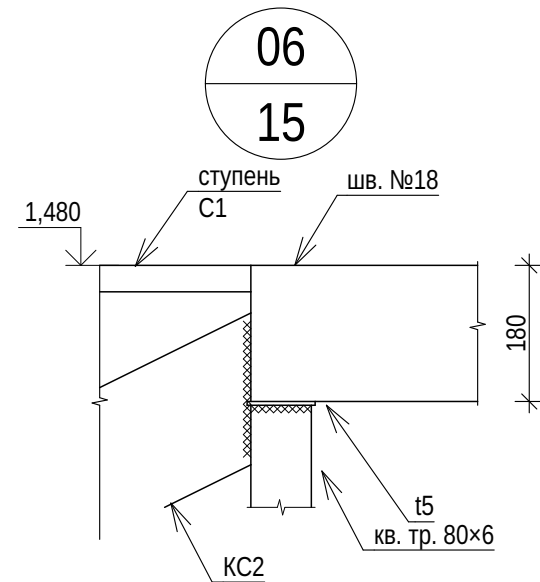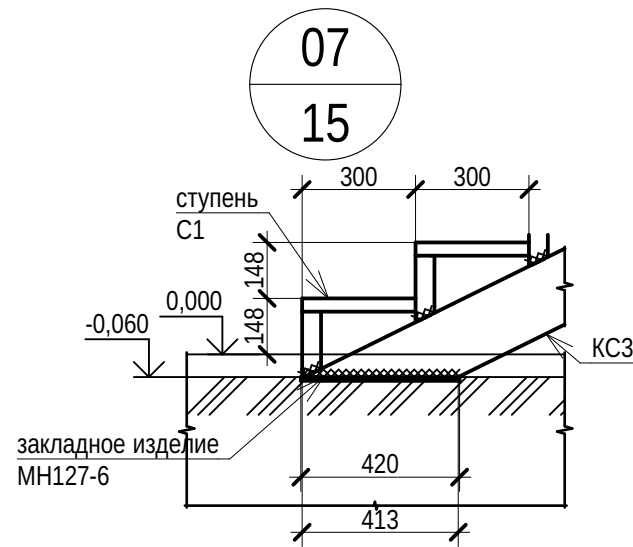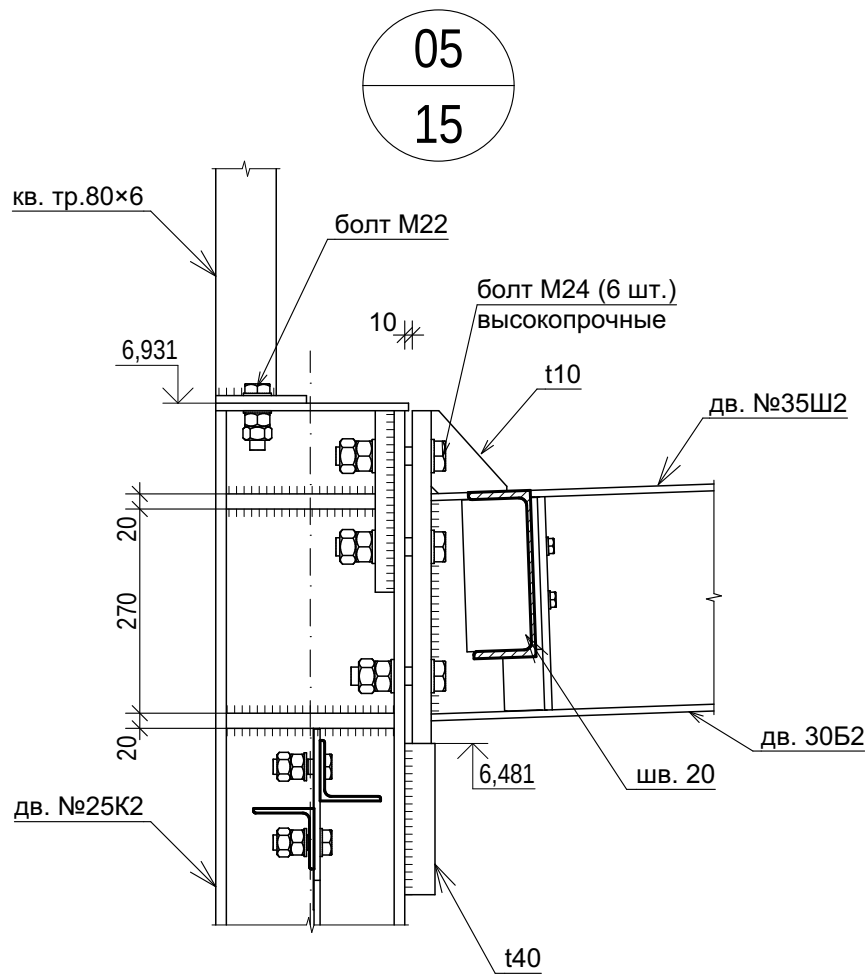


ПРИМЕЧАНИЯ:

- 1) Крепление балок выполнять на высокопрочные болты; крепление прогонов выполнять на сварку; сварка изделий плазмотронная, в среде защитного газа;
- 2) Металлические конструкции окрасить грунтовкой ГФ-021 и эмалью ПФ-115 или эквивалентными составами;
- 3) Узлы замаркированы на листах 11-15.

						ОПР-01/24/2024-КР.ГЧ				
						"Современный оптово-продовольственный рынок (ОПР) по адресу: Донецкая область, .г Макеевка, Горняцкий район				
Изм.	Кол.уч.	Лист	№Док.	Подп.	Дата	Док-павильон (рыба-мясо) №23, №23.2 (по генплану)		Стадия	Лист	Листов
Разраб.								П	18	
Пров.						Узлы 05-08		ООО "Технология"		
Н. контроль										


СХЕМА ПЕРЕКРЫТИЯ НА ОТМ. +3,640

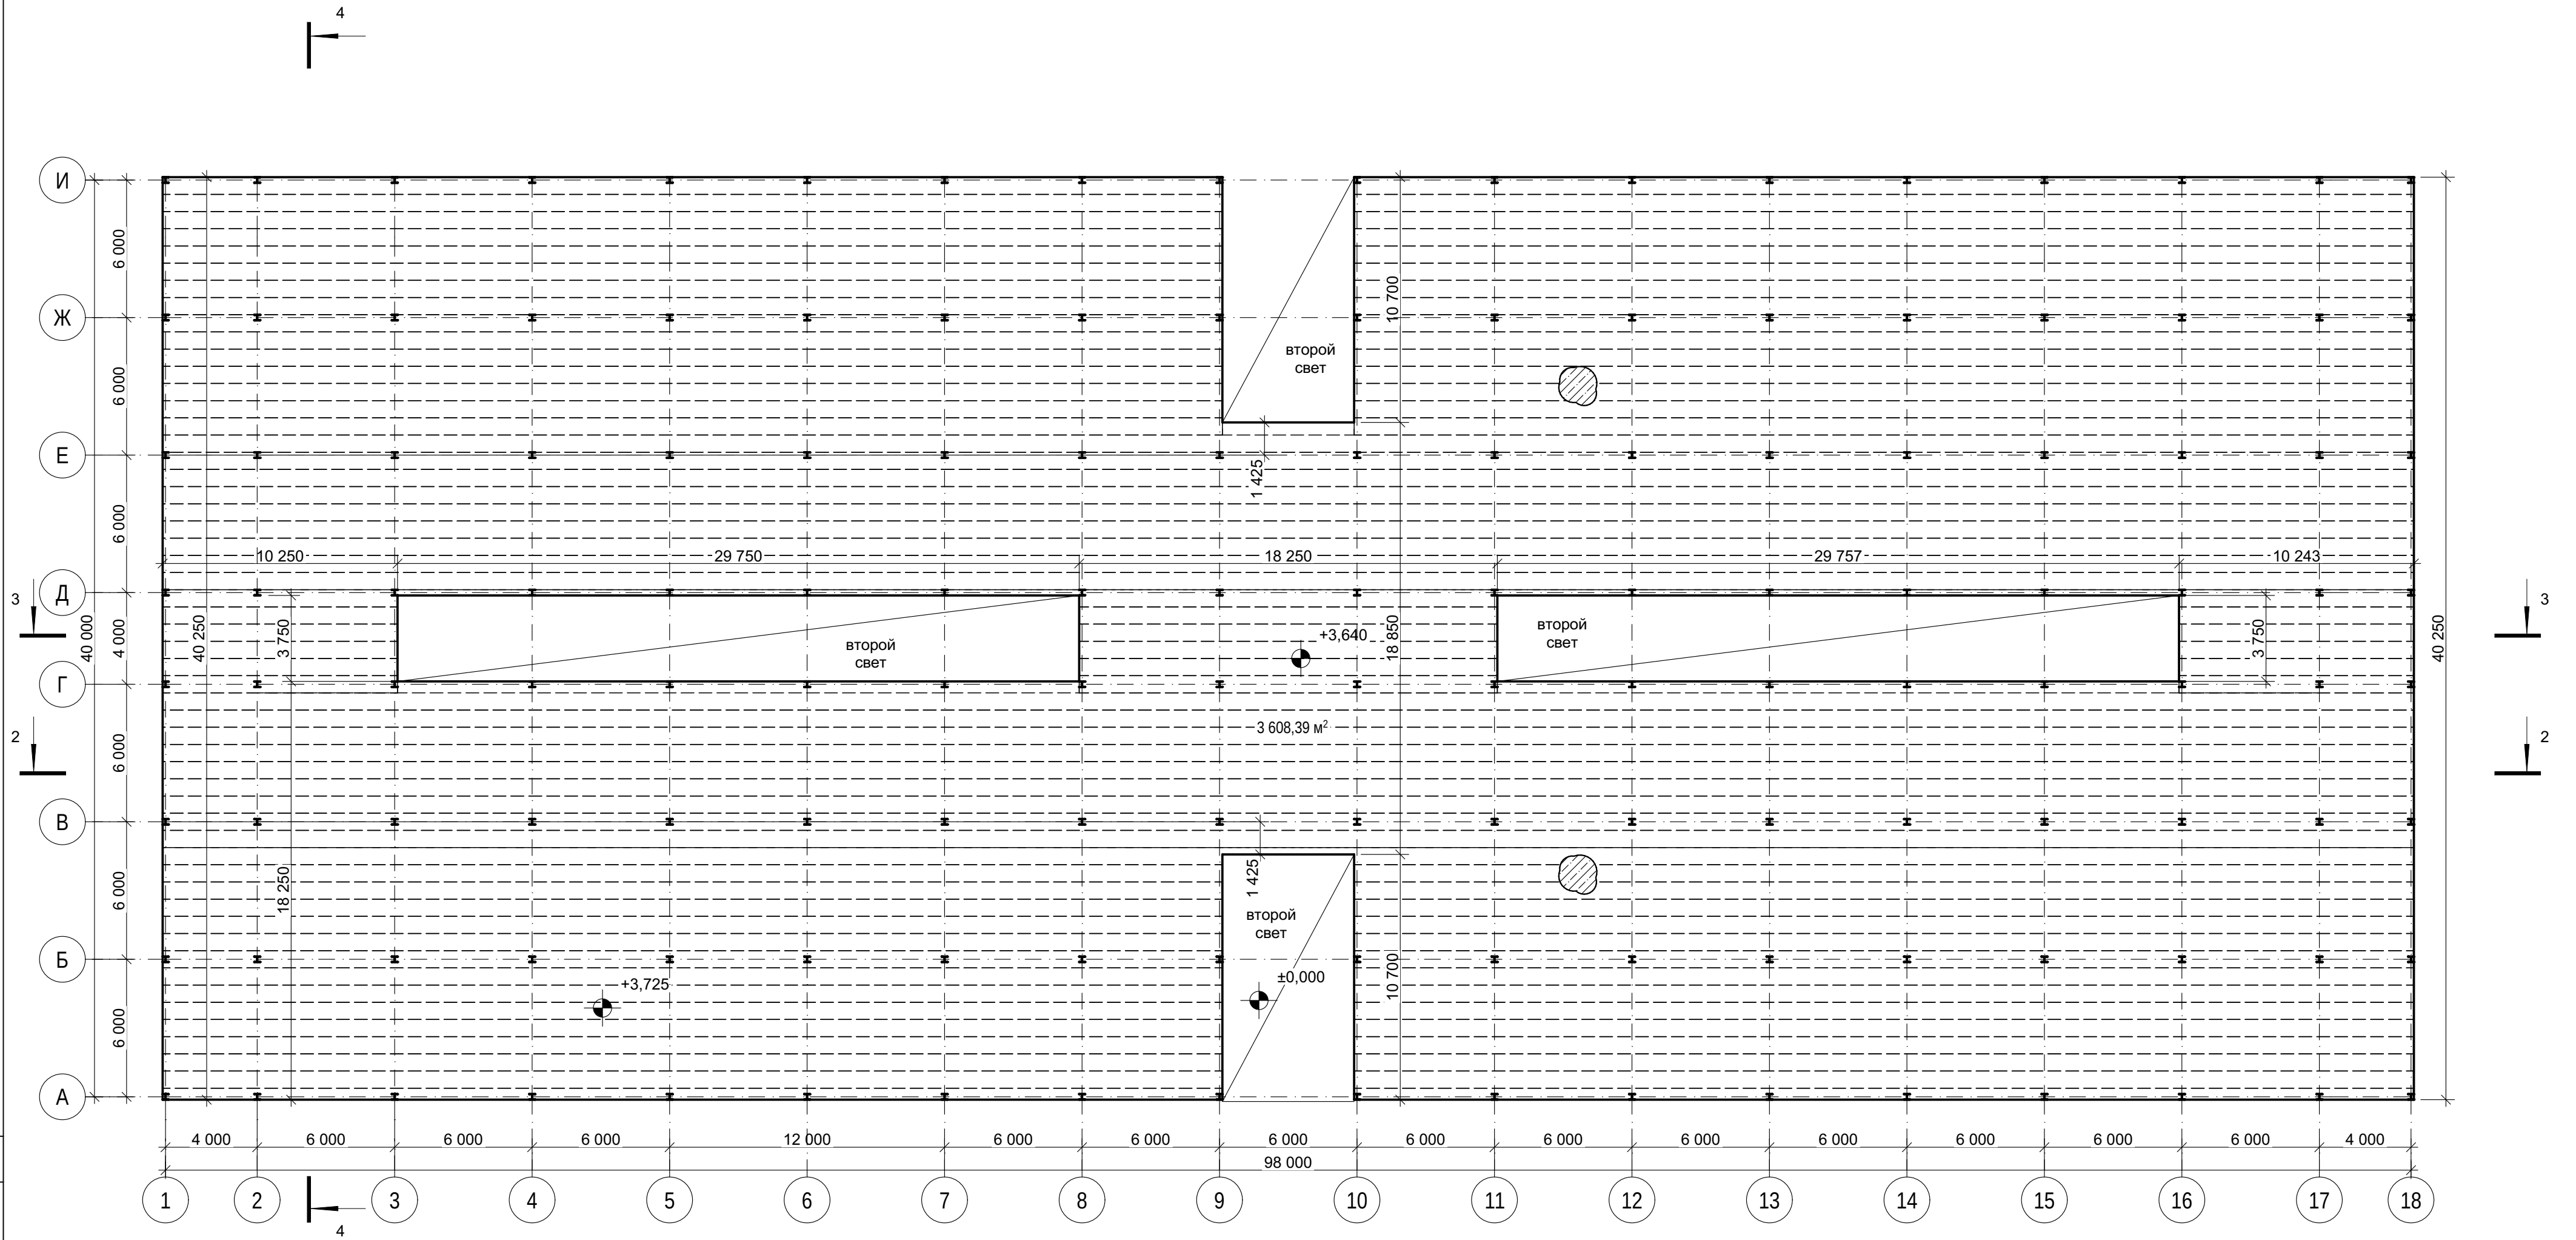

УСЛОВНЫЕ ОБОЗНАЧЕНИЯ

----- - граница листов профилированного настила

АРМИРОВАНИЕ ПЛИТЫ

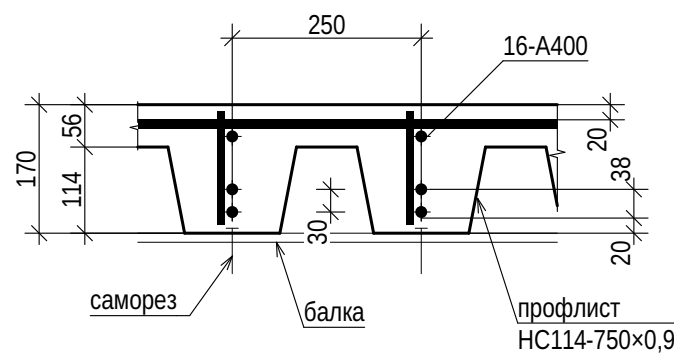


ПРИМЕЧАНИЯ:

- 1) Перекрытие монолитное, по профлисту НС114-750-0,9; толщиной 170мм;
- 2) Профлисты крепить к балкам перекрытия на саморезы, в каждой гофре, на каждой балке;
- 3) Схема опирания профлиста - 3-х точечная. Стыковка двух профлистов на балке - в стык;
- 4) Армирование перекрытия выполнять плоскими каркасами уложенными в гофры; поперечное армирование выполнять стержнями арматуры с шагом 150мм

						ОПР-01/24/2024-КР.ГЧ			
						"Современный оптово-продовольственный рынок (ОПР) по адресу: Донецкая область, г. Макеевка, Горняцкий район			
Изм.	Кол.уч.	Лист	Подп.	Дата					
Разраб.						Док-павильон (рыба-мясо) №23, №23.2 (по генплану)	Стадия	Лист	Листов
Пров.							П	19	
Н. контроль						Схема расположения перекрытия на отм. +3,500	ООО "Технология"		

Инв. № подл.	Подп. и дата	Взам. инв. №	Согласовано		

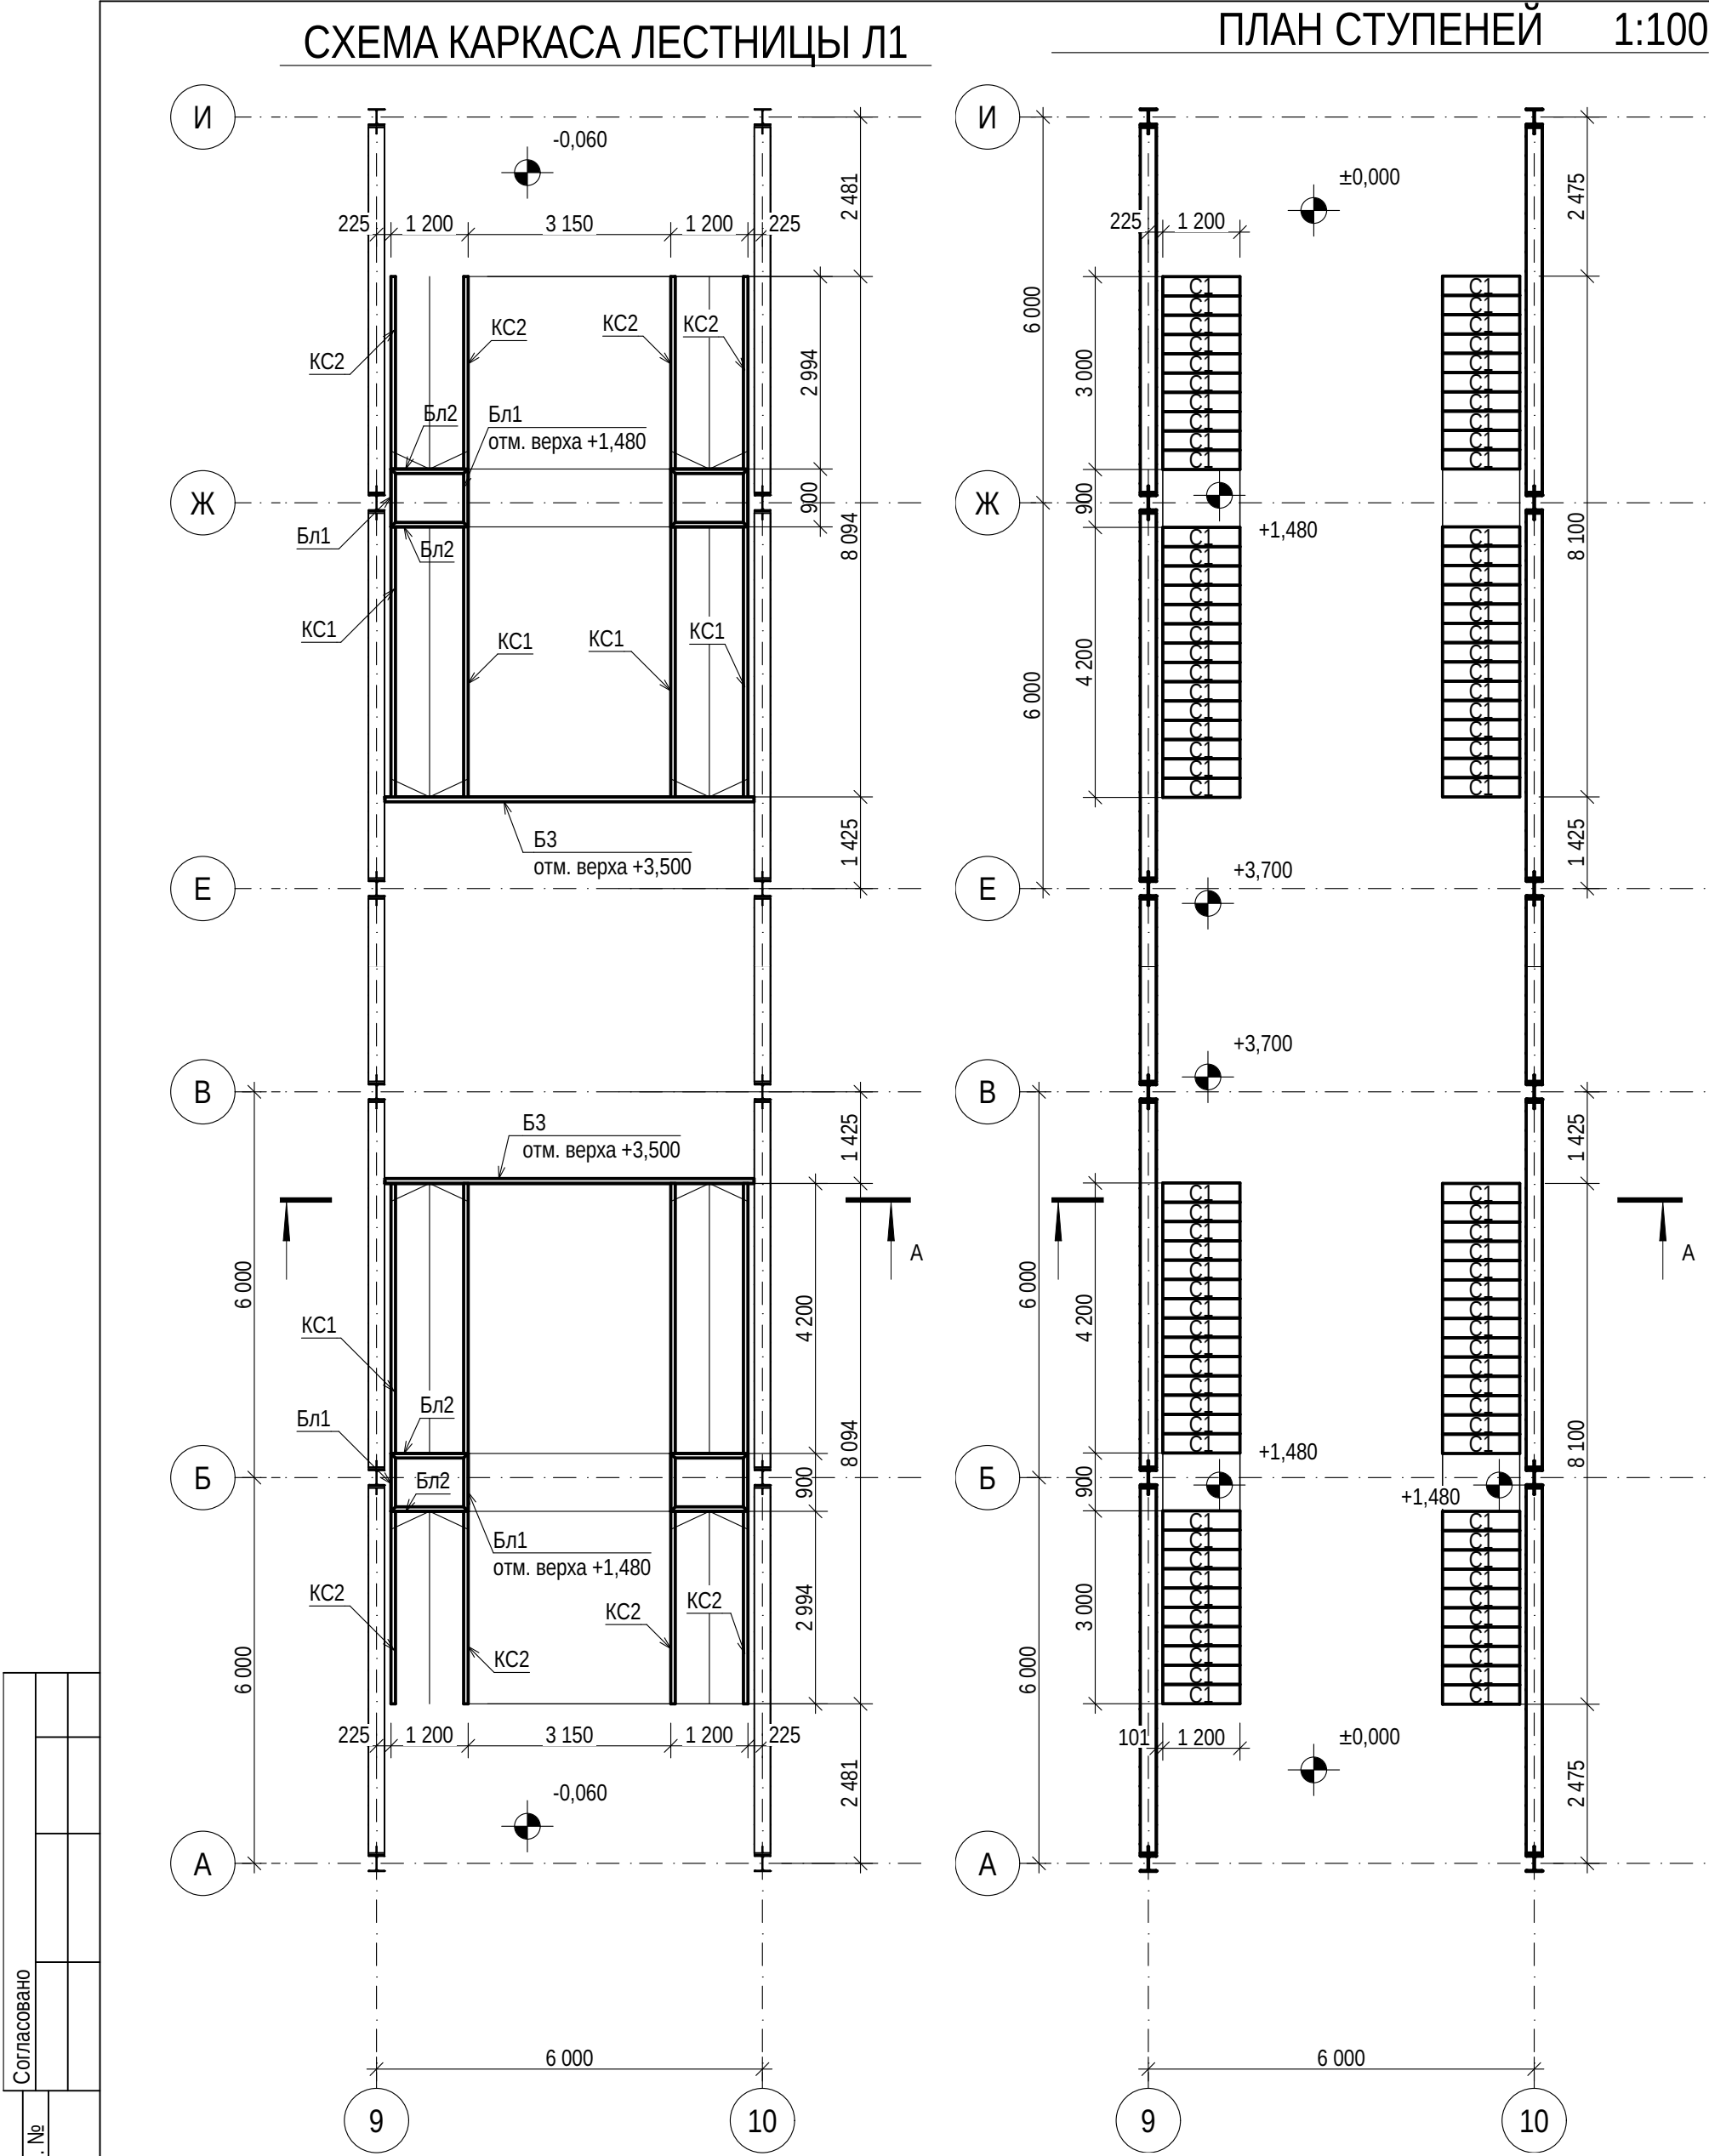


СПЕЦИФИКАЦИЯ СТУПЕНЕЙ					
Поз.	Обозначение	Наименование	Кол-во	Масс ед., кг	Примечание
С1			96		

СПЕЦИФИКАЦИЯ КАРКАСА ЛЕСТНИЦЫ Л1					
Поз.	Обозначение	Наименование	Кол-во	Масса ед., кг.	Примечание
01	ГОСТ 19904-90	--5x90x90	14	0,32	
Б3	ГОСТ 8240-97	20П L=5 740мм.	2	106,67	
Бл1	ГОСТ 8240-97	18П L=910мм.	8	14,98	
Бл2	ГОСТ 8240-97	18П L=1 210мм.	8	19,92	
Кл1	ГОСТ 30245-2012	80x6 L=1 355мм.	4	18,08	
КС1	ГОСТ 8240-97	18П L=4 773мм.	8	78,58	
КС2	ГОСТ 8240-97	18П L=3 338мм.	8	54,96	
				1637,66	

Согласовано	
Взам. инв. №	
Подп. и дата	
Инв. № подл.	

							ОПР-01/24/2024-КР.ГЧ		
							"Современный оптово-продовольственный рынок (ОПР) по адресу: Донецкая область, г. Макеевка, Горняцкий район		
Изм.	Кол.уч.	Лист	№ док.	Подп.	Дата				
Разраб.						Док-павильон (рыба-мясо) №23, №23.2	Стадия	Лист	Листов
Пров.						(по генплану)	П	20	
						Схема каркаса лестницы, план ступеней	ООО "Технология"		
Н. контроль									

СХЕМА РАСПОЛОЖЕНИЯ КРЫЛЕЦ

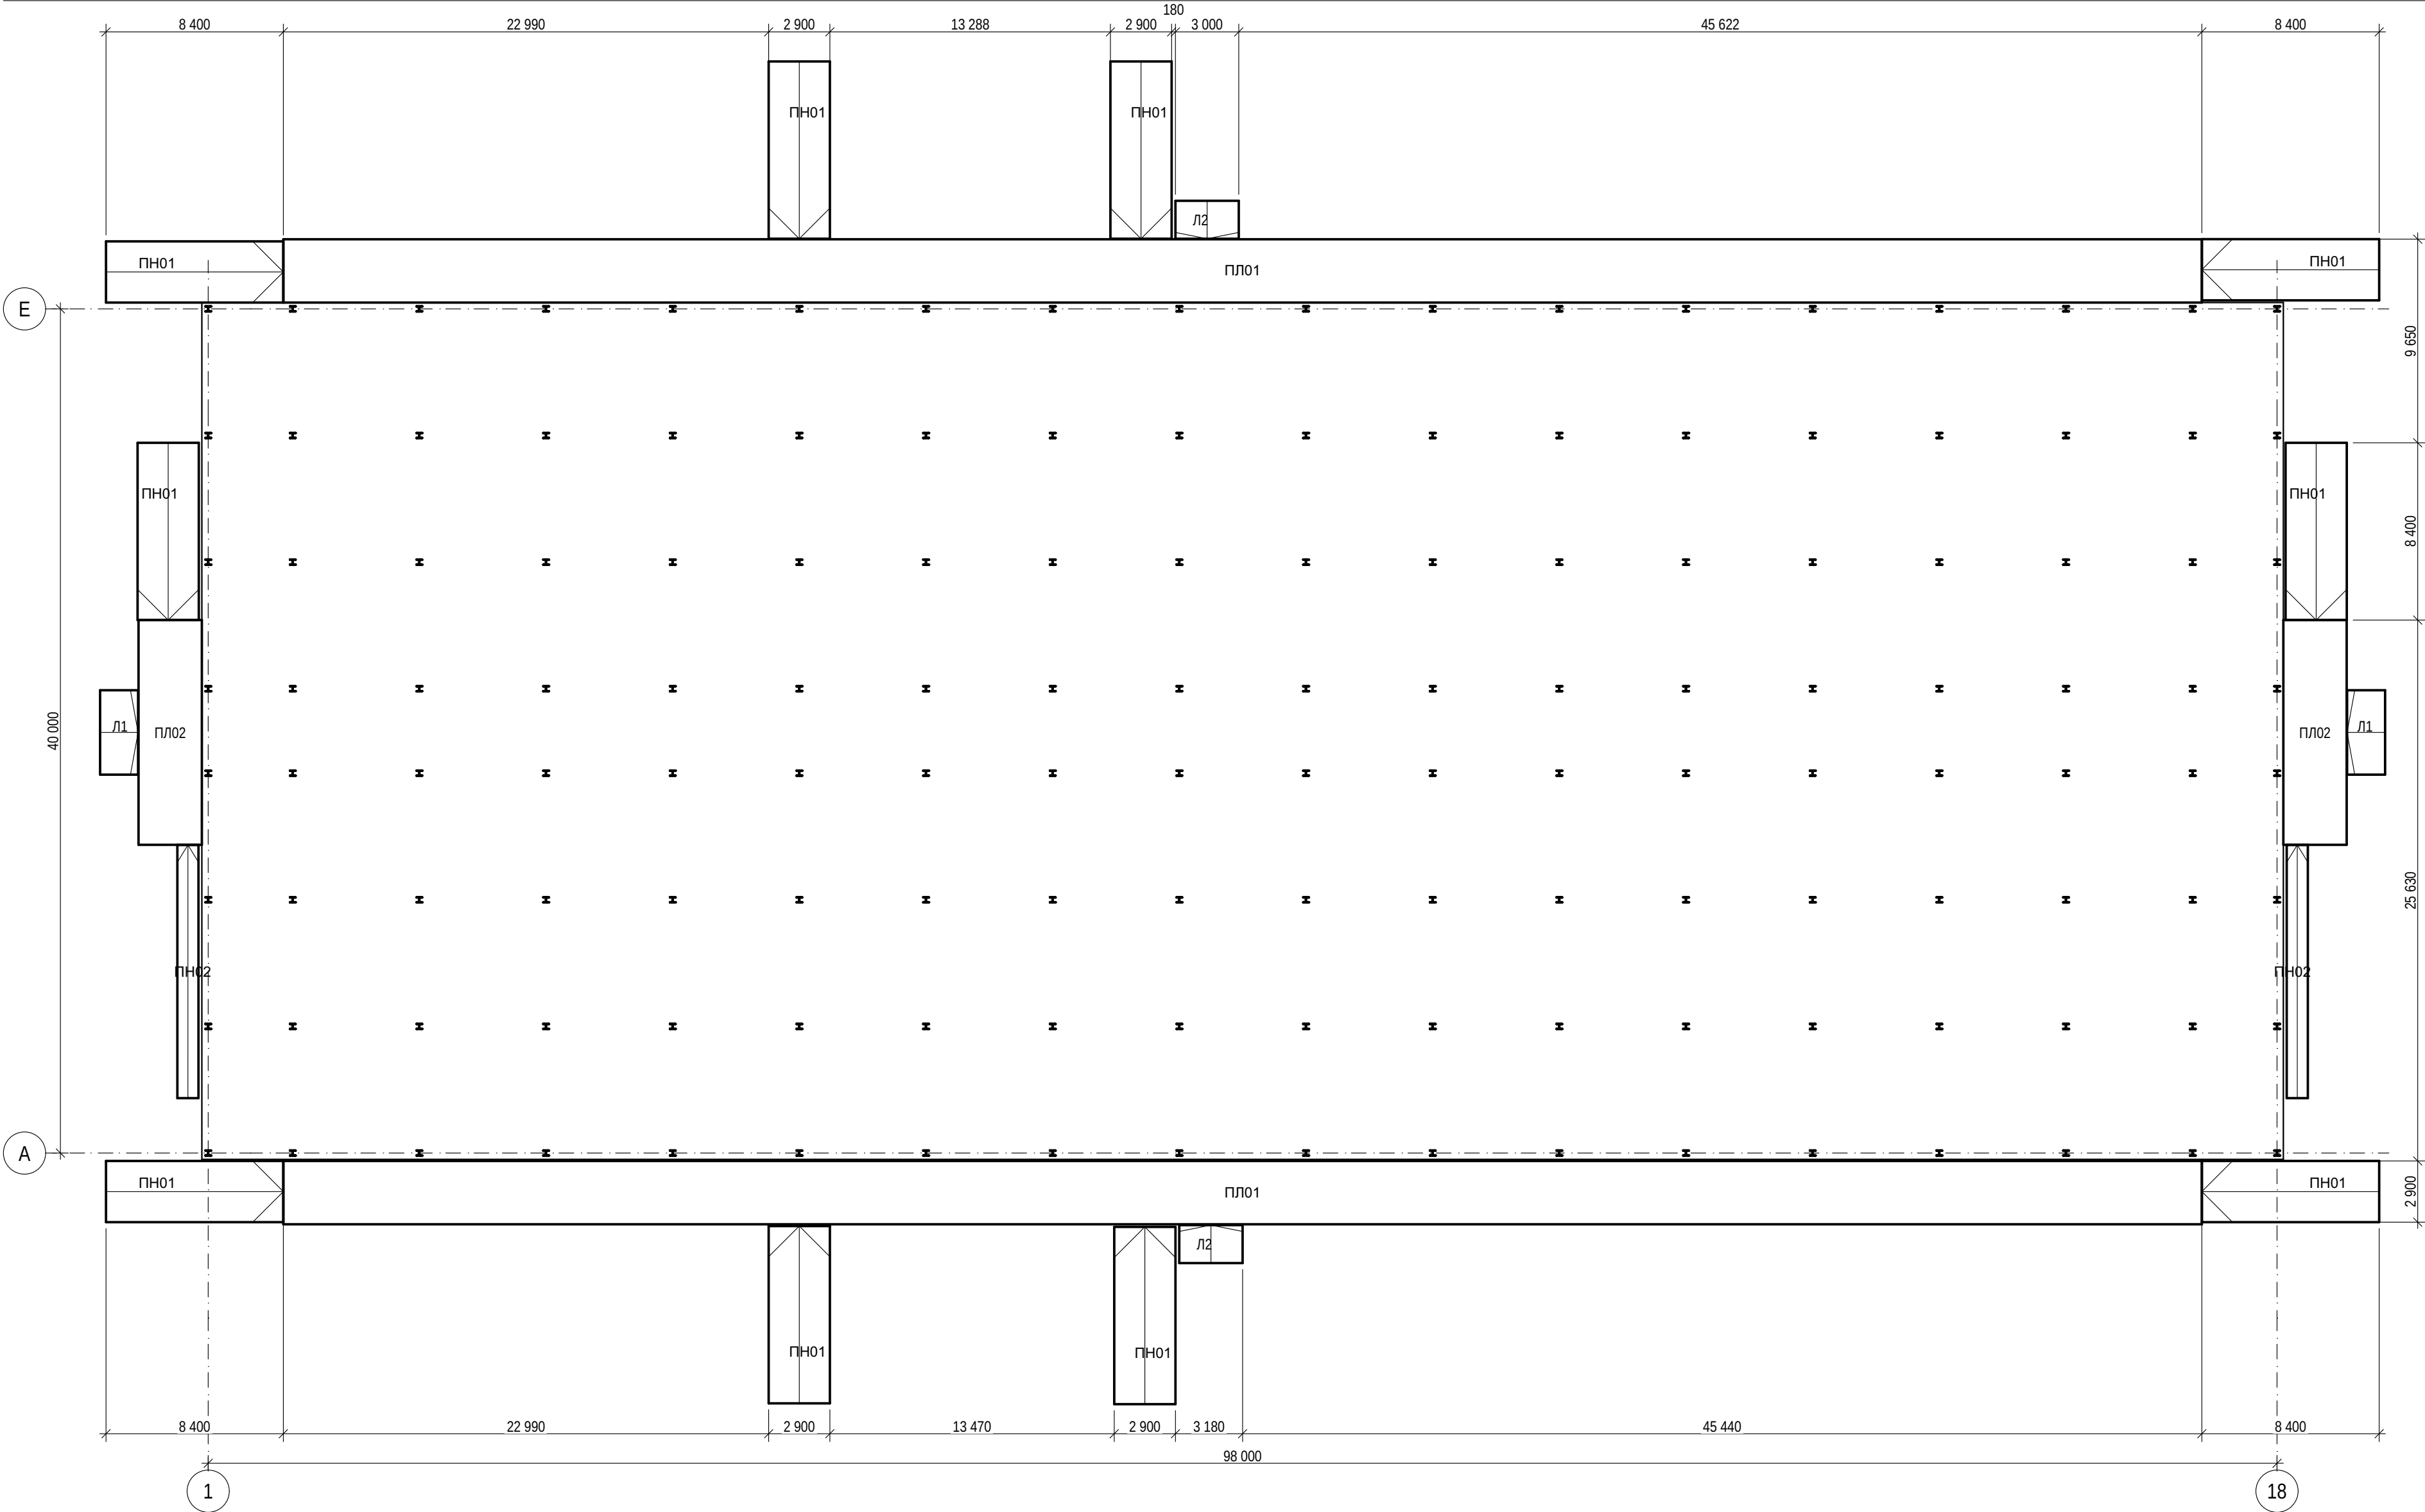

СПЕЦИФИКАЦИЯ КРЫЛЕЦ


Поз.	Обозначение	Наименование	Кол -во	Масса ед., кг.	Примечание
Л1	см. лист 28	Лестница	2	338,23	
Л2	см. лист 29	Лестница	2	264,90	
ПЛ01	см. лист 22	площадка	2	6700,60	
ПЛ02	см. лист 23	площадка	2	948,76	
ПН01	см. лист 24	Пандус	10	1431,08	
ПН02	см. лист 26	Пандус	2	780,39	
				32376,56	

ПРИМЕЧАНИЯ:



- 1) Каркас пандусов, площадок и лестниц выполнить из металла; ступени металлические, со сварным настилом; плиты площадок железобетонные, про профилированному настилу НС114-750-0,9;
- 2) Соединение элементов сварное, ручное электродуговое, катет швов по наименьшей толщине свариваемых элементов;
- 3) Металлические элементы окрасить грунтовкой ГФ-021, эмалью ПФ-115 или эквивалентными составами;
- 4) Фундамент крылец - лента железобетонная, из бетона В20, армированная арматурой 12-А400. Закладные под стойки по серии 1.400-15 Выпуск 1. Рабочие чертежи.

							ОПР-01/24/2024-КР.ГЧ			
							"Современный оптово-продовольственный рынок (ОПР) по адресу: Донецкая область, г. Макеевка, Горняцкий район			
Изм.	Кол.уч.	Лист	№Док.	Подп.	Дата		Док-павильон (рыба-мясо) №23, №23.2 (по генплану)	Стадия	Лист	Листов
Разраб.								П	21	
Пров.							Схема расположения крылец	ООО "Технология"		
Н. контроль										



1:200

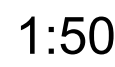

1:200

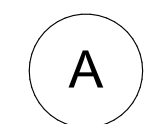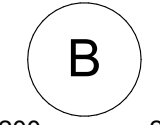

1:200

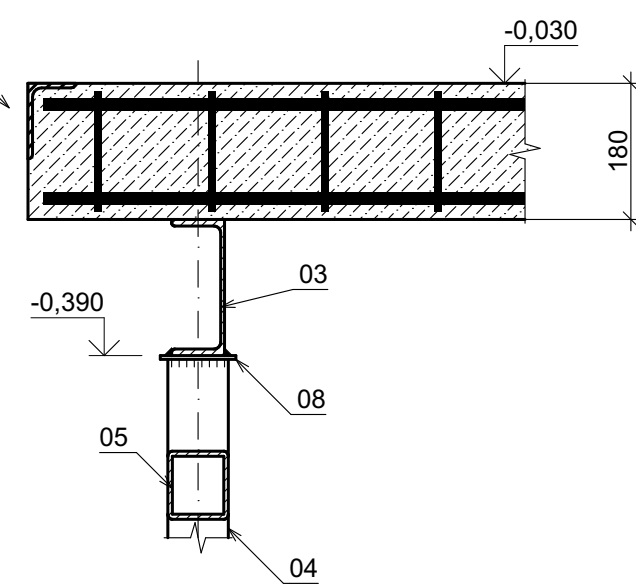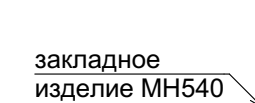


ПРИМЕЧАНИЯ:

- | | | | | | | | | | |
|-------------|--------|------|-------|-------|-------|--|------------------|------|--------|
| | | | | | | ОПР-01/24/2024-КР.ГЧ | | | |
| | | | | | | "Современный оптово-продовольственный рынок (ОПР) по адресу:
Донецкая область, г. Макеевка, Горняцкий район | | | |
| Изм. | Колуч. | Лист | №Док. | Подп. | Дата | Док-павильон (рыба-мясо) №23, №23.2
(по генплану) | Стадия | Лист | Листов |
| Разраб. | | | | | 01.25 | | П | 22 | |
| Пров. | | | | | 01.25 | | | | |
| | | | | | | | | | |
| | | | | | | Площадка Пл01 | ООО "Технология" | | |
| Н. контроль | | | | | 01.25 | | | | |

ИНВ. № подл.	
--------------	--

СХЕМА СТОЕК ПЛОЩАДКИ

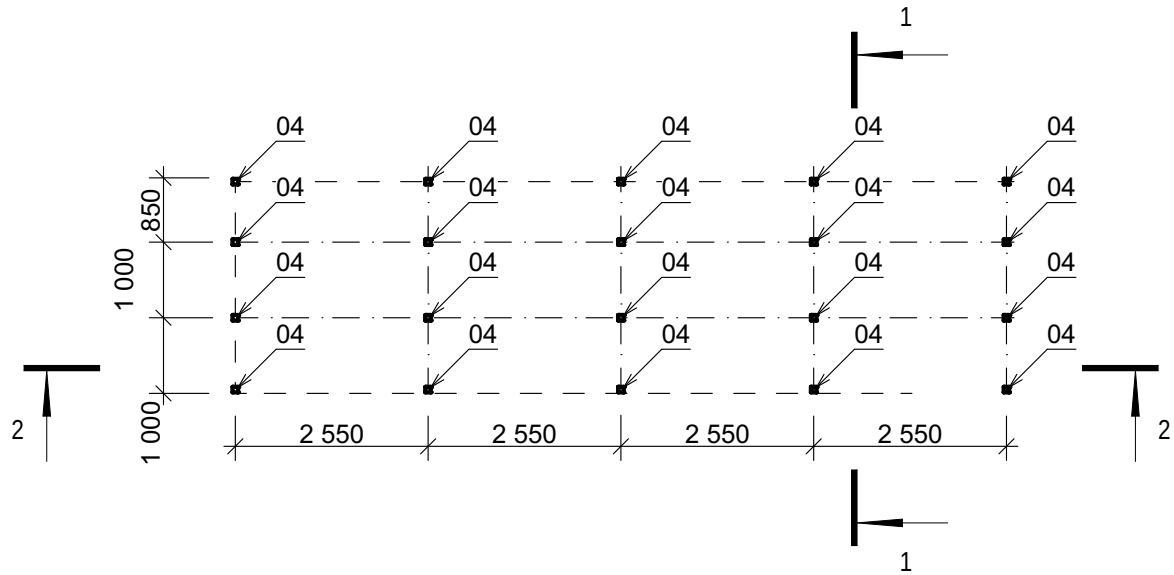

1-1 1:50




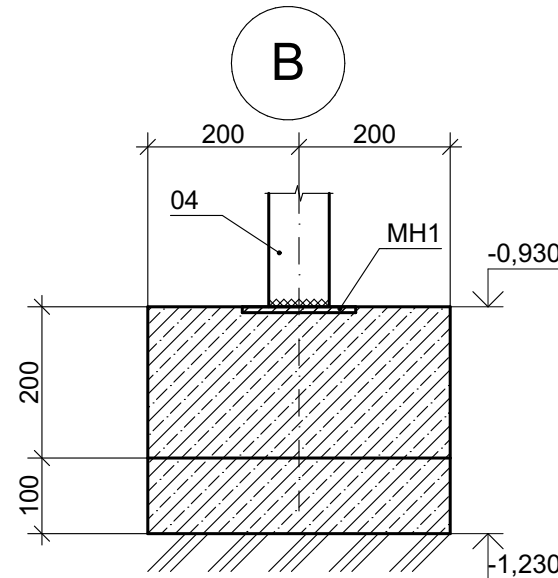



СХЕМА БАЛОК ПЛОЩАДКИ

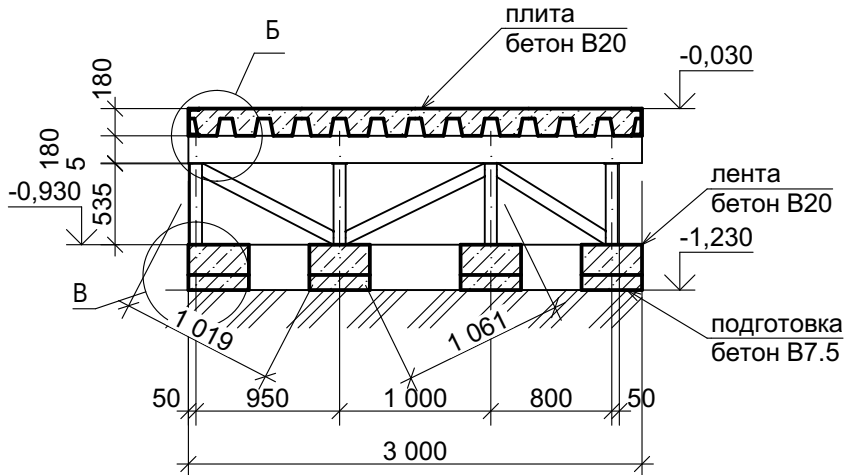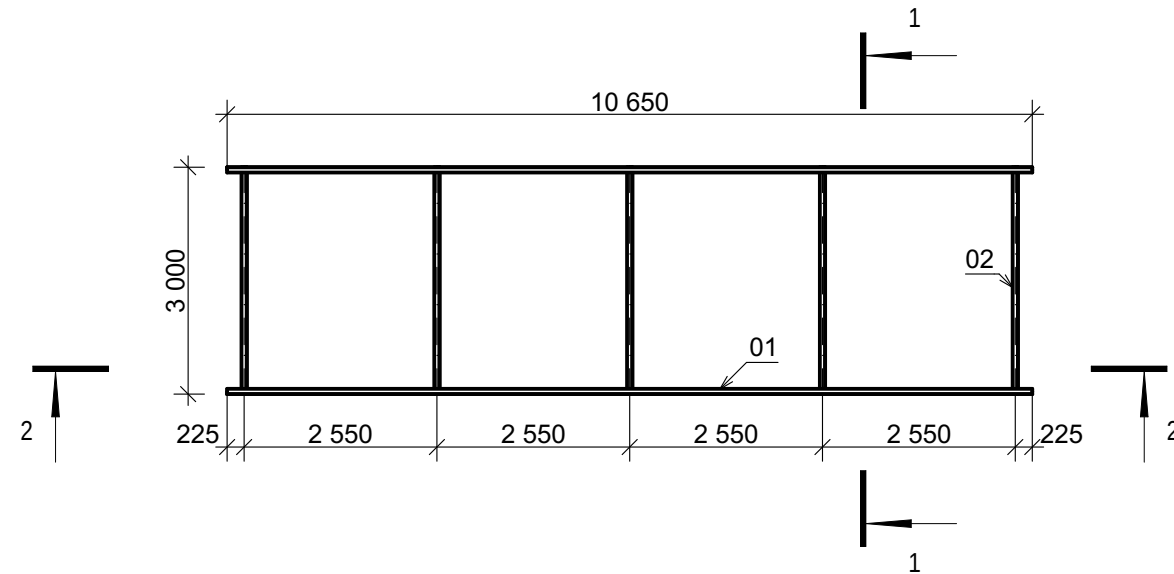


2-2 1:100

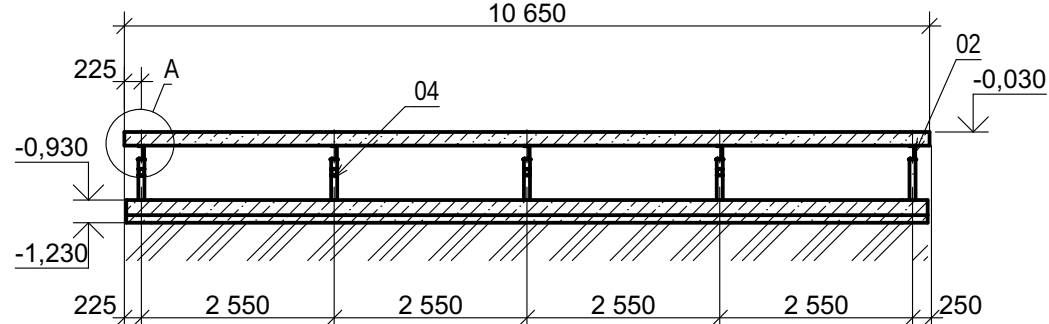

Б

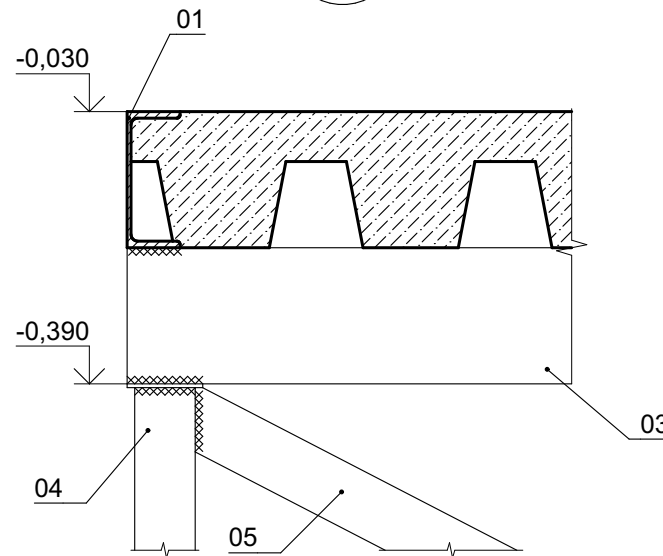

А

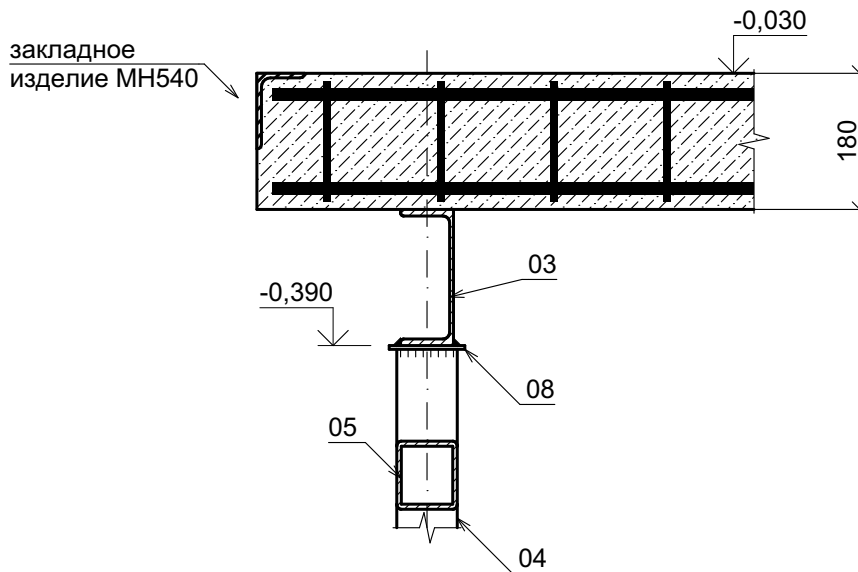

СПЕЦИФИКАЦИЯ ЭЛЕМЕНТОВ

Поз. дет.	Тип сечения	Наименование	Ко л-во	Масса ед., кг.	Прим ечани е
01	Швеллер	18П L=10 650мм.	2	175,33	
02	Швеллер	18П L=3 000мм.	5	48,90	
04	Квадратная труба	80x6 L=535мм.	20	7,27	
05	Квадратная труба	80x6 L=1 019мм.	4	13,89	
06	Квадратная труба	80x6 L=895мм.	4	12,24	
07	Квадратная труба	80x6 L=1 061мм.	4	14,46	
08	Лист	--5x100x100	20	0,40	
				910,92	

ПРИМЕЧАНИЯ:

- 1) Соединение элементов сварное, сварка ручная электродуговая;
2) Материал: сталь С255
3) Окрасить грунтовкой ГФ-021 и эмалью ПФ115;

						ОПР-01/24/2024-КР.ГЧ				
						"Современный оптово-продовольственный рынок (ОПР) по адресу: Донецкая область, .г Макеевка, Горняцкий район				
Изм.	Кол.уч.	Лист	№Док.	Подп.	Дата	Док-павильон (рыба-мясо) №23, №23.2 (по генплану)	Стадия	Лист	Листов	
Разраб.					01.25		П	23		
Пров.					01.25					
						Площадка Пл02	ООО "Технология"			
Н. контроль					01.25					

Согласовано				
Инов. № подл.	Подп. и дата	Взам. инв. №		

СХЕМА СТОЕК ПАНДУСА 1:100

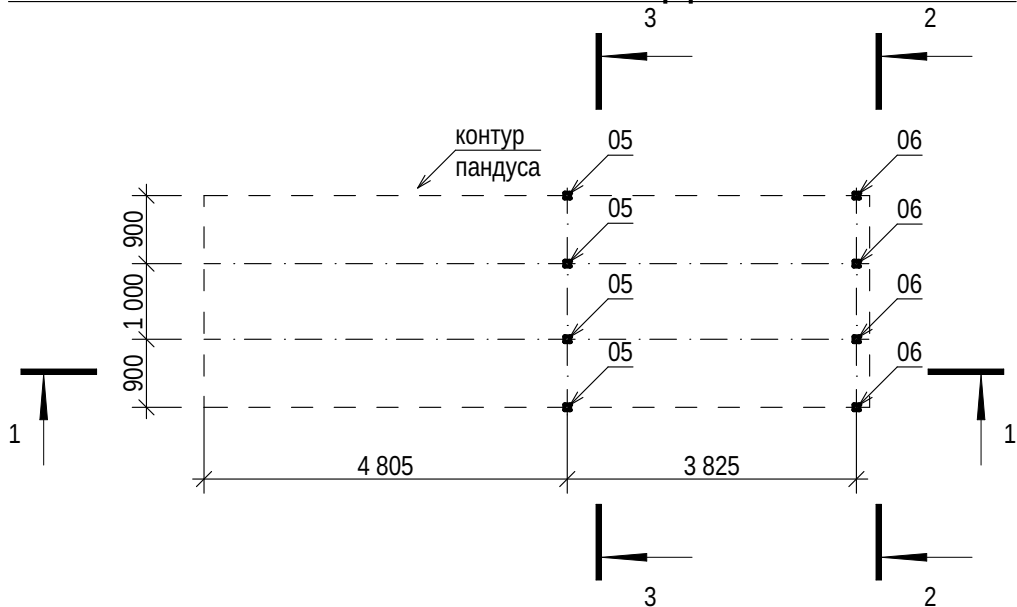


СХЕМА ЛИСТОВ ПОКРЫТИЯ 1:100


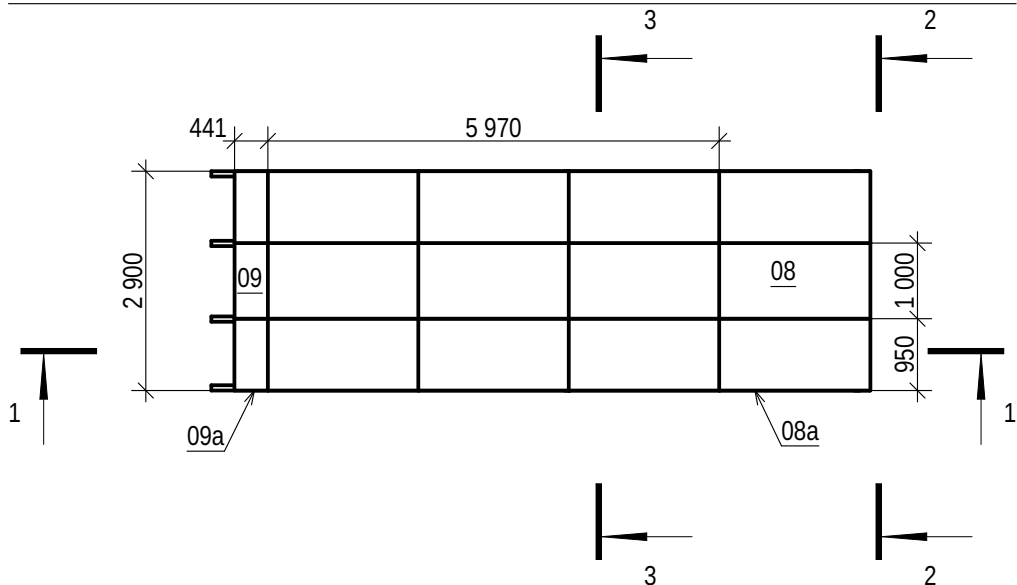


СХЕМА БАЛОК ПАНДУСА 1:100

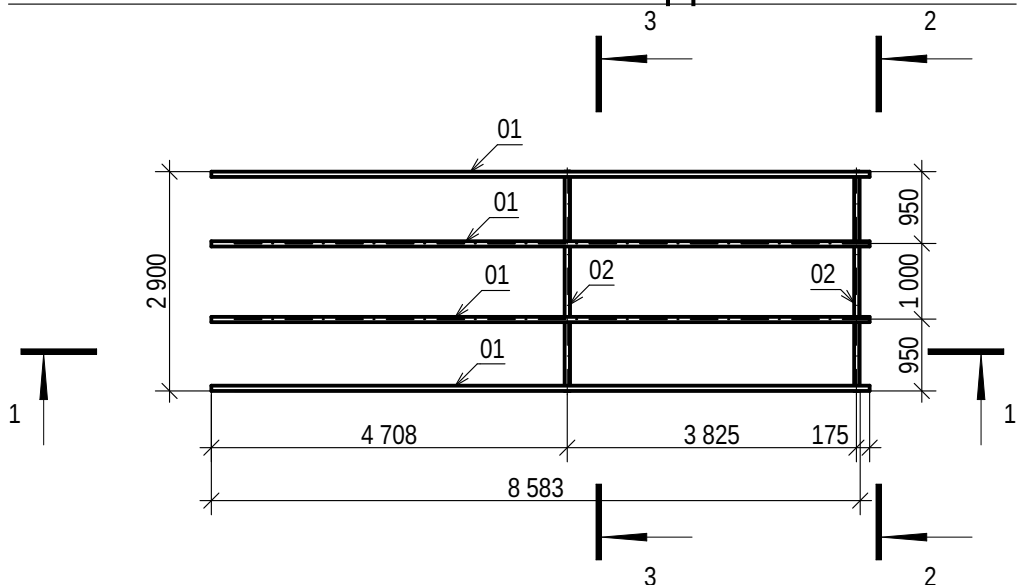

СПЕЦИФИКАЦИЯ ЭЛЕМЕНТОВ






Поз.	Тип сечения	Наименование	Кол -во	Масса ед., кг.	Приме чание
01	Швеллер	18П L=8 752мм.	4	144,08	
02	Швеллер	18П L=2 900мм.	2	47,74	
03	Квадратная труба	80x6 L=957мм.	2	13,02	
04	Квадратная труба	80x6 L=1 043мм.	1	14,19	
05	Квадратная труба	80x6 L=110мм.	3	1,50	
05	Квадратная труба	80x6 L=111мм.	1	1,51	
06	Квадратная труба	80x6 L=510мм.	4	6,93	
07	Лист	--5x100x100	8	0,40	
08	Лист	SP 34x38 30x3 (1 000x2 000)	4	56,00	
08a	Лист	SP 34x38 30x3 (950x2 000)	8	53,20	
09	Лист	SP 34x38 30x3 (1 000x441)	1	12,35	
09a	Лист	SP 34x38 30x3 (950x441)	2	10,91	
				1432,73	

ПРИМЕЧАНИЯ:

- 1) Соединение элементов сварное, сварка ручная электродуговая;
- 2) Материал: сталь С255;
- 3) Окрасить грунтовкой ГФ-021 и эмалью ПФ115;
- 4) Разрезы см. лист 25.

						ОПР-01/24/2024-КР.ГЧ			
						"Современный оптово-продовольственный рынок (ОПР) по адресу: Донецкая область, .г Макеевка, Горняцкий район			
Изм.	Кол.уч.	Лист	№Док.	Подп.	Дата	Док-павильон (рыба-мясо) №23, №23.2 (по генплану)	Стадия	Лист	Листов
Разраб.							П	24	
Пров.									
Н. контроль						Пандус П1	ООО "Технология"		

Согласовано			Взам. инв. №	
			Подп. и дата	
Инв. № подл.				

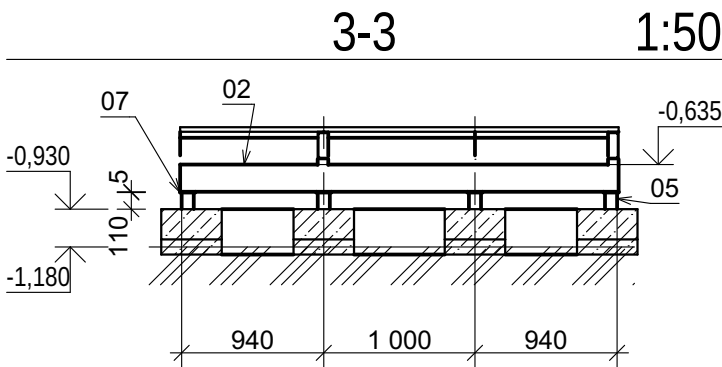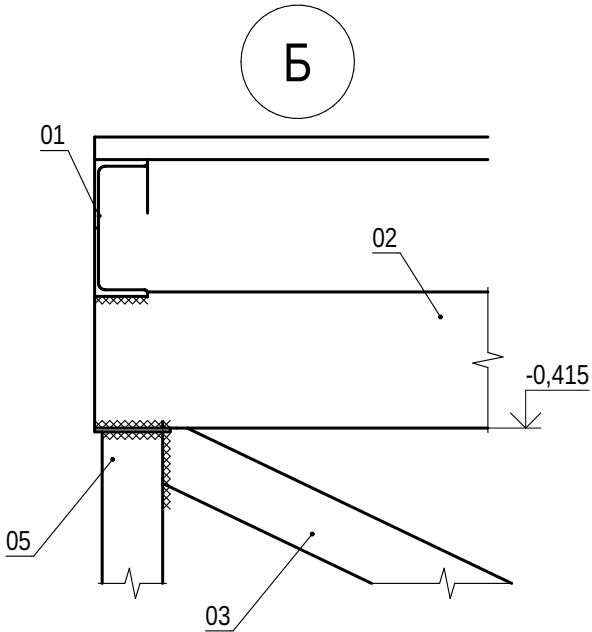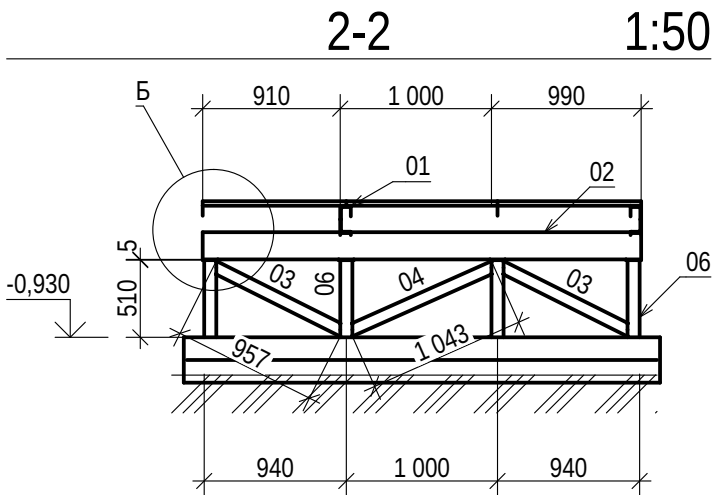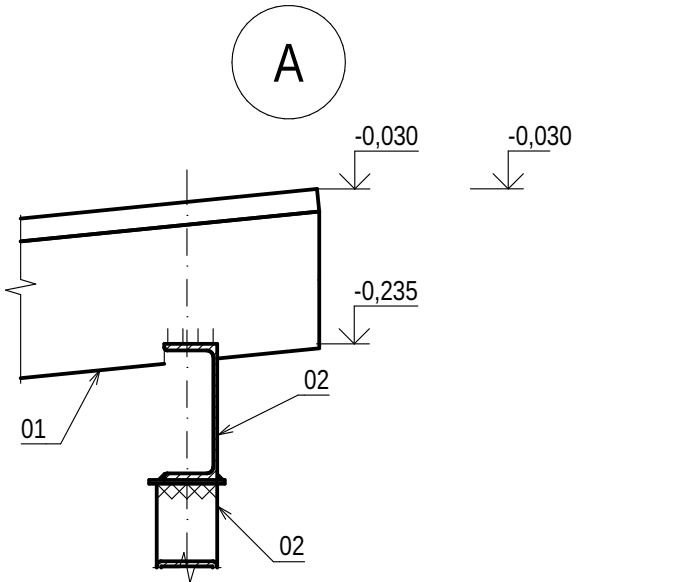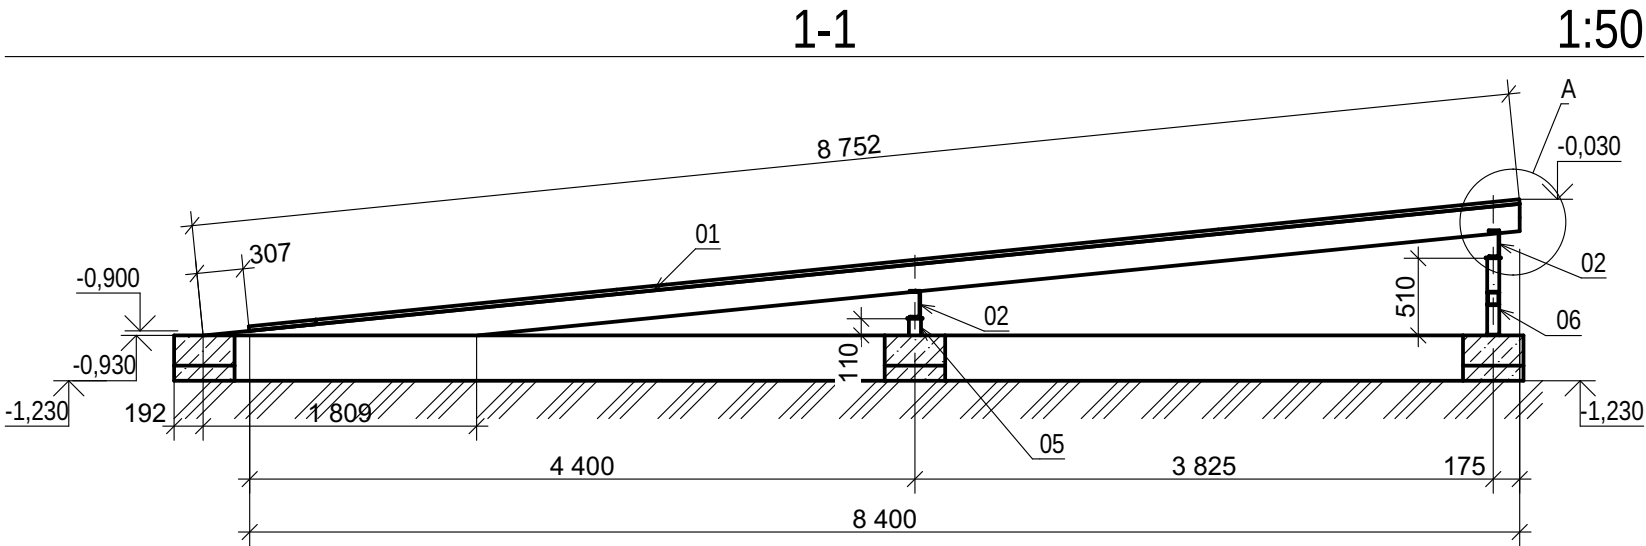

ПРИМЕЧАНИЯ:
1) Разрезы замаркированы на листе 24.

						ОПР-01/24/2024-КР.ГЧ		
						"Современный оптово-продовольственный рынок (ОПР) по адресу: Донецкая область, г. Макеевка, Горняцкий район		
Изм.	Кол.уч.	Лист	№Док.	Подп.	Дата			
Разраб.						Док-павильон (рыба-мясо) №23, №23.2 (по генплану)	Стадия	Лист
Пров.							П	25
						Пандус П1	ООО "Технология"	
Н. контроль								

Согласовано			
Инов. № подл.	Подп. и дата	Взам. инв. №	

СХЕМА СТОЕК ПАНДУСА 1:100

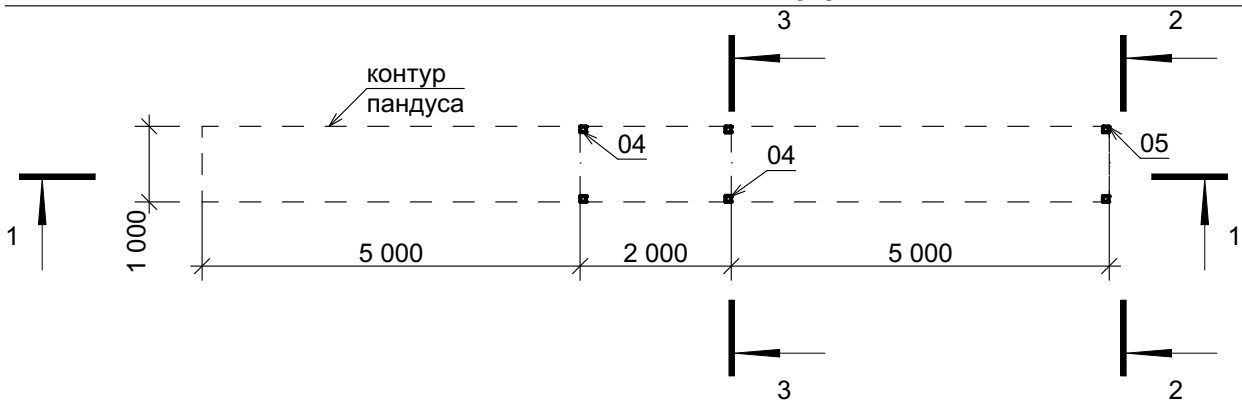


СХЕМА БАЛОК ПАНДУСА 1:100


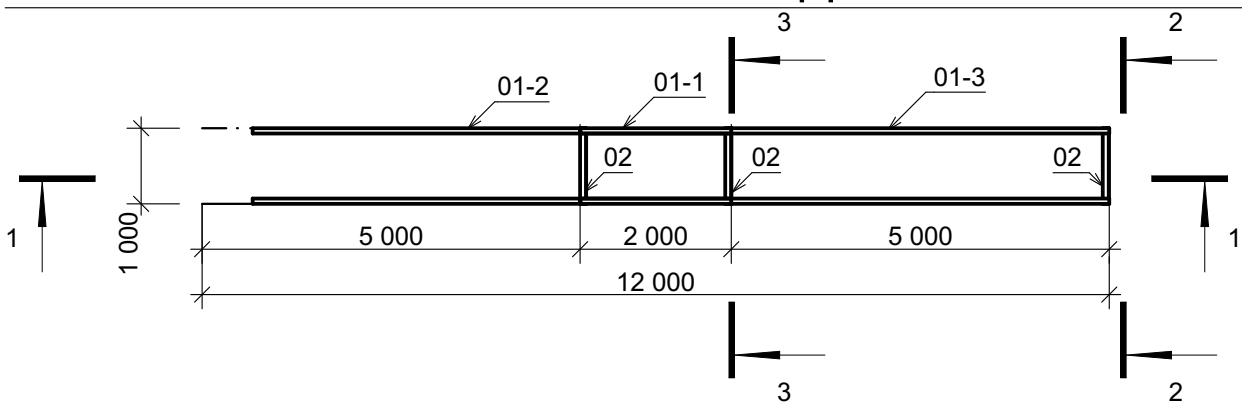


СХЕМА ЛИСТОВ ПОКРЫТИЯ 1:100

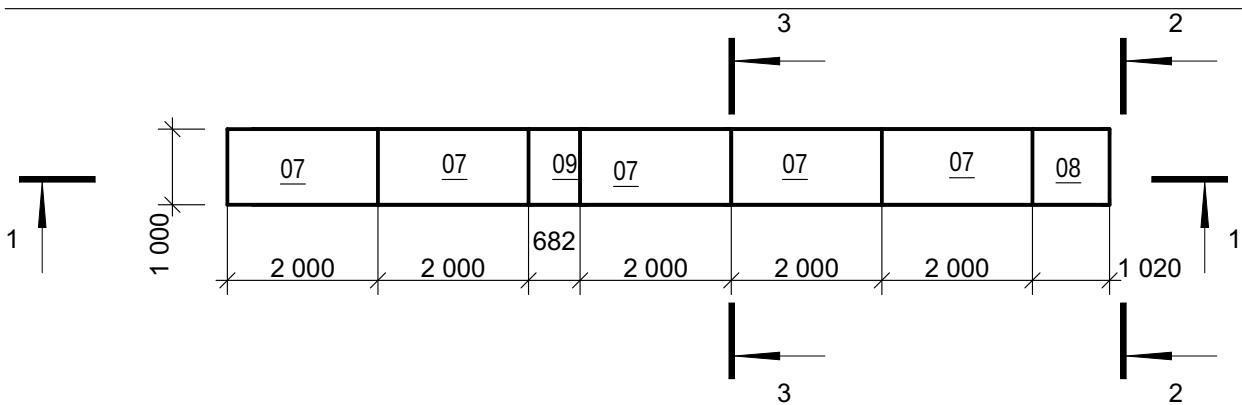

СПЕЦИФИКАЦИЯ ЭЛЕМЕНТОВ







Поз.	Тип сечения	Наименование	Ко л- во	Масса ед., кг.	Прим ечани е
01-1	Швеллер	18П L=2 009мм.	2	33,07	
01-2	Швеллер	18П L=4 349мм.	2	71,59	
01-3	Швеллер	18П L=5 029мм.	2	82,79	
02	Квадратная труба	80x6 L=1 000мм.	3	13,34	
03	Квадратная труба	80x6 L=1 014мм.	1	13,65	
04	Квадратная труба	80x6 L=125мм.	4	1,70	
05	Квадратная труба	80x6 L=568мм.	2	7,72	
06	Лист	--5x100x100	6	0,40	
07	Лист	SP 34x38/30x3 (1 000x2 000)	5	56,00	
08	Лист	SP 34x38/30x3 (1 000x1 000)	1	28,00	
09	Лист	SP 34x38/30x3 (685x1 000)	1	19,18	
				780,39	

ПРИМЕЧАНИЯ:

- 1) Соединение элементов сварное, сварка ручная электродуговая;
- 2) Материал: сталь С255;
- 3) Окрасить грунтовкой ГФ-021 и эмалью ПФ115;
- 4) Разрезы см. лист 27.

						ОПР-01/24/2024-КР.ГЧ			
						"Современный оптово-продовольственный рынок (ОПР) по адресу: Донецкая область, .г Макеевка, Горняцкий район			
Изм.	Кол.уч.	Лист	№Док.	Подп.	Дата	Док-павильон (рыба-мясо) №23, №23.2 (по генплану)	Стадия	Лист	Листов
Разраб.							П	26	
Пров.									
Н. контроль						Пандус П2	ООО "Технология"		

Согласовано					
Взам. инв. №					
Подп. и дата					
Инв. № подл.					

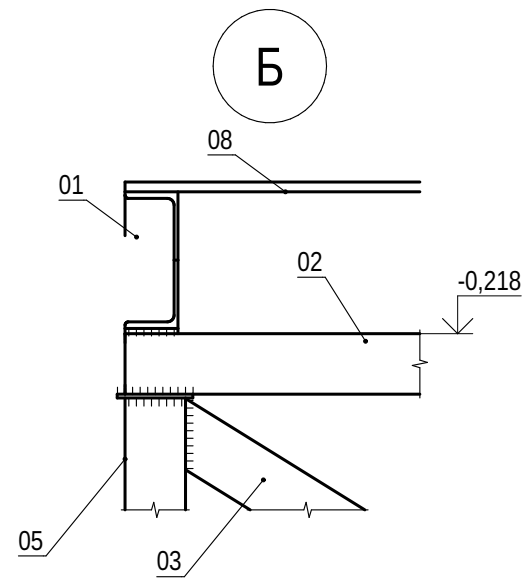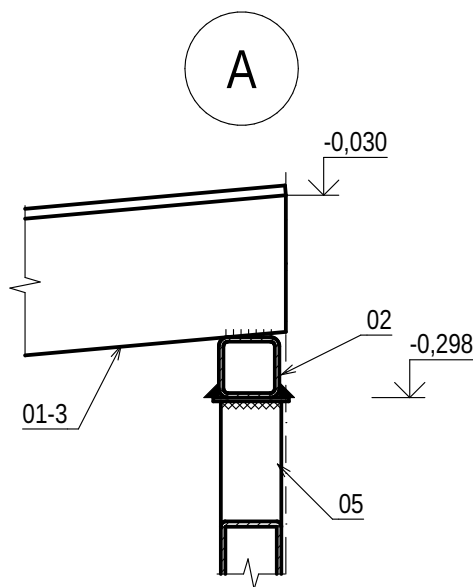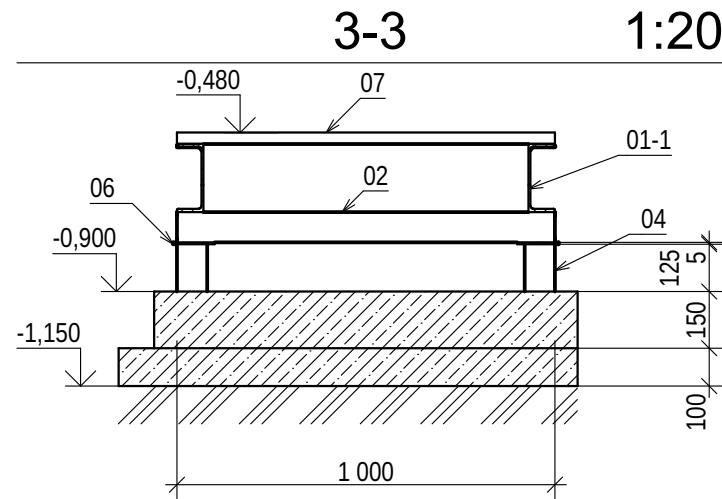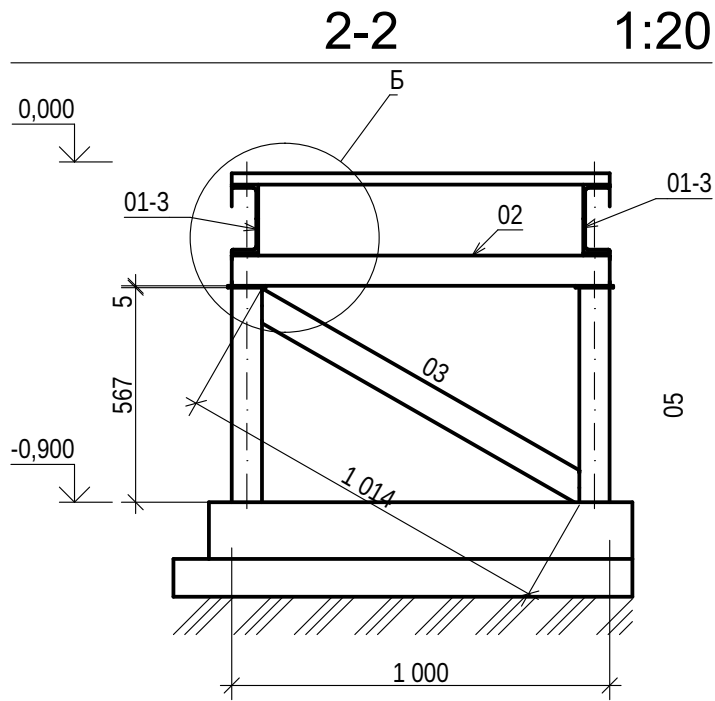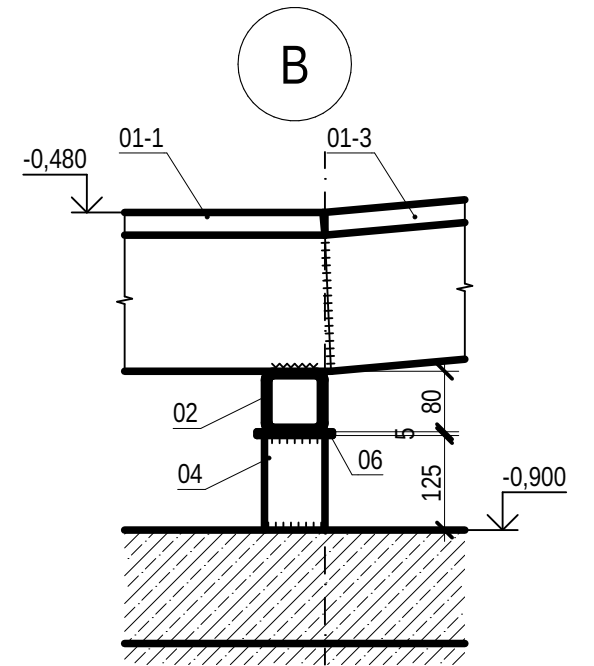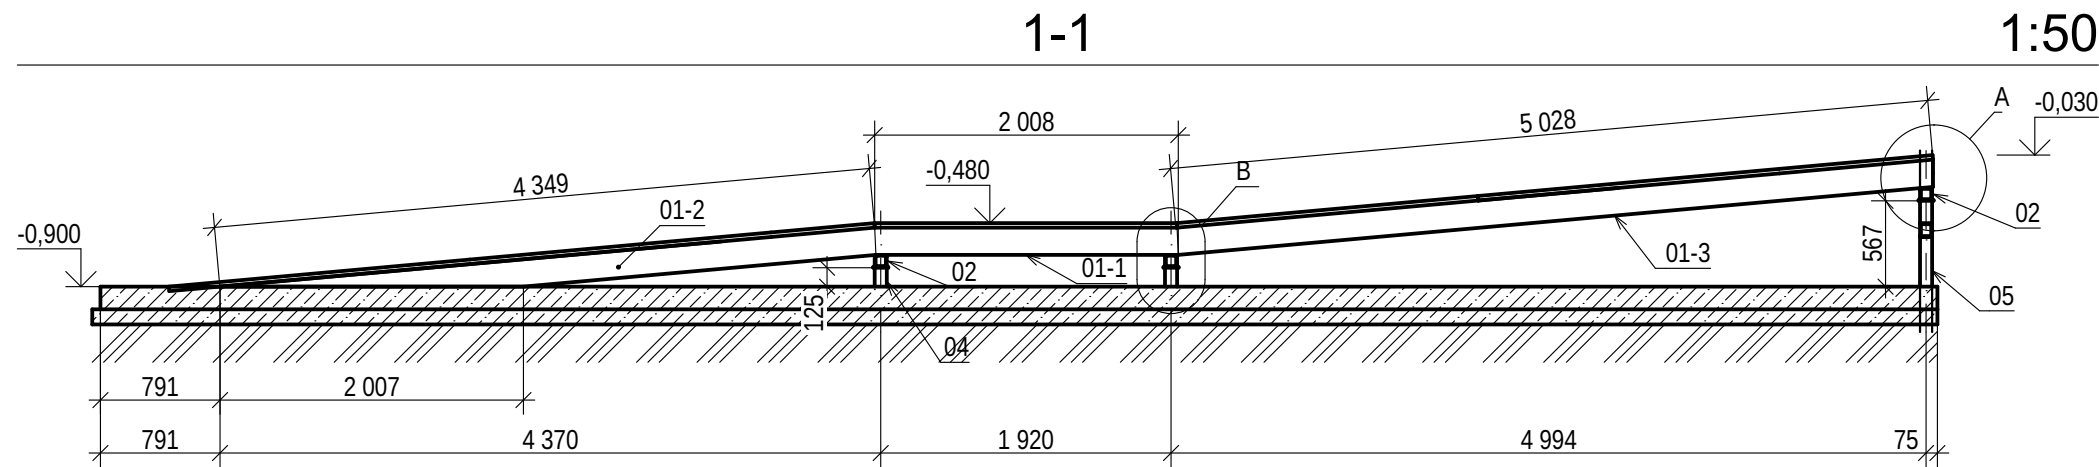

ПРИМЕЧАНИЯ:

1) Разрезы замаркированы на листе 26.

						ОПР-01/24/2024-КР.ГЧ					
						"Современный оптово-продовольственный рынок (ОПР) по адресу: Донецкая область, г. Макеевка, Горняцкий район					
Изм.	Кол.уч.	Лист	№Док.	Подп.	Дата	Док-павильон (рыба-мясо) №23, №23.2 (по генплану)		Стадия	Лист	Листов	
Разраб.								П	27		
Пров.						Пандус П2		ООО "Технология"			
Н. контроль											

СХЕМА СТОЕК ЛЕСТНИЦЫ Л1 СХЕМА БАЛОК ЛЕСТНИЦЫ Л1


СПЕЦИФИКАЦИЯ ЭЛЕМЕНТОВ

Поз. дет.	Тип сечения	Наименование	Кол -во	Масса ед., кг.	Примечание
01	Швеллер	18П L=1 791мм.	5	29,19	
02	Швеллер	18П L=4 000мм.	1	65,85	
03	Квадратная труба	80x6 L=1 126мм.	2	15,61	
04	Квадратная труба	80x6 L=1 165мм.	2	16,13	
05	Квадратная труба	80x6 L=726мм.	5	9,87	
06	Лист	--5x100x100	5	0,40	
				326,63	


СПЕЦИФИКАЦИЯ СТУПЕНЕЙ

Поз. дет.	Тип сечения	Наименование	Кол -во	Масса ед., кг.	Примечание
Ст2	---	ступень	24	16,26	
				390,24	


СХЕМА СТУПЕНЕЙ Л1

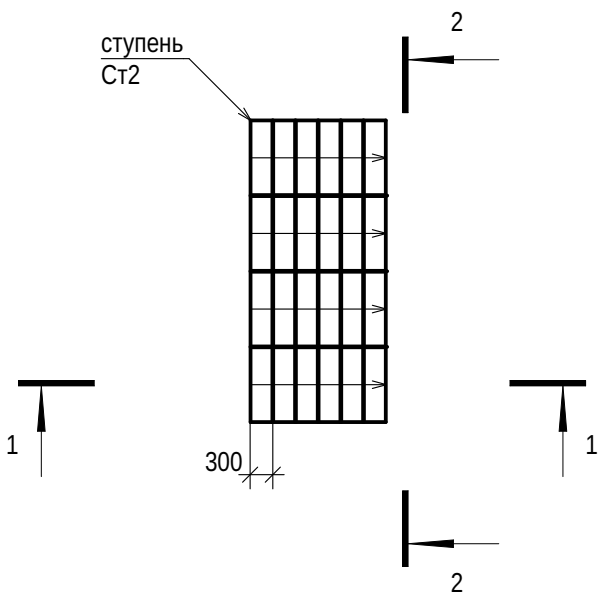


1-1 1:50

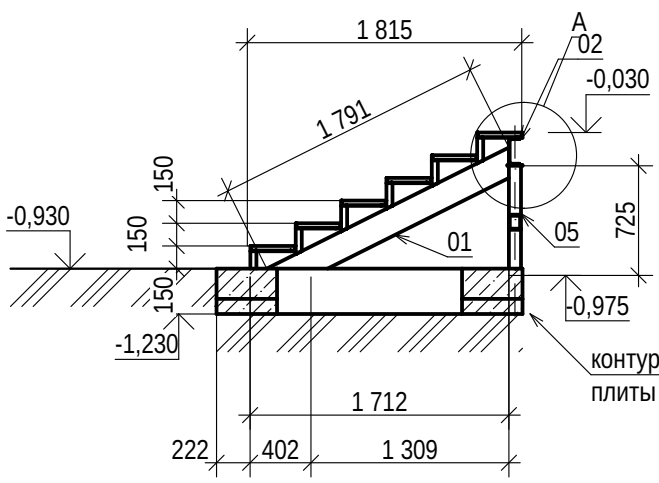


2-2 1:50

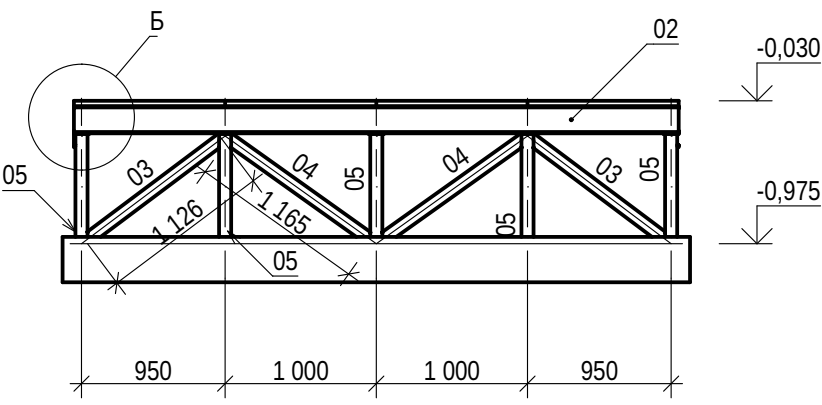

А

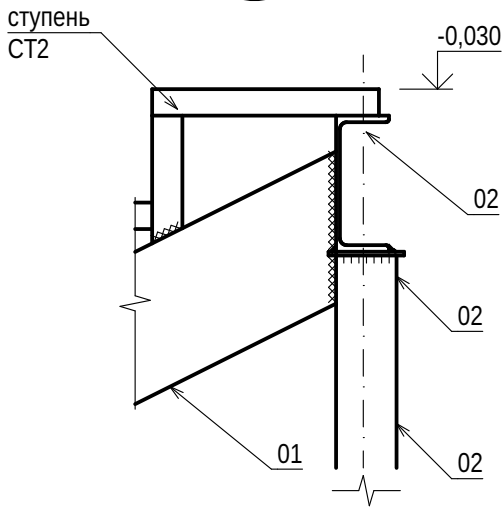

Б

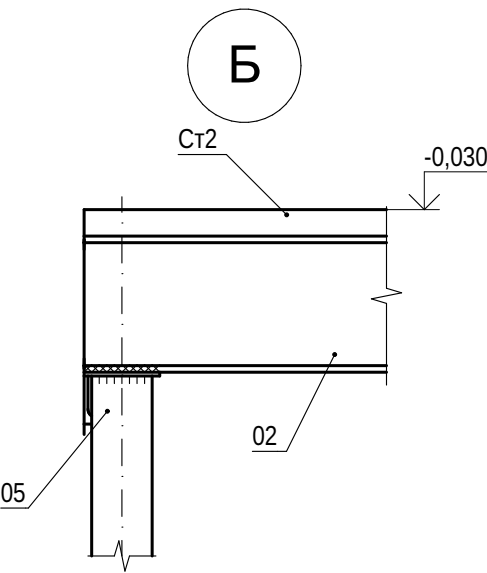

ПРИМЕЧАНИЯ:

- 1) Соединение элементов сварное, сварка ручная электродуговая;
2) Материал: сталь С255
3) Окрасить грунтовкой ГФ-021 и эмалью ПФ115;

ОПР-01/24/2024-КР.ГЧ					
"Современный оптово-продовольственный рынок (ОПР) по адресу: Донецкая область, г. Макеевка, Горняцкий район					
Изм.	Кол.уч.	Лист	№Док.	Подп.	Дата
Разраб.					
Пров.					
Док-павильон (рыба-мясо) №23, №23.2 (по генплану)					
Лестница Л1					
ООО "Технология"					

Technical drawing of a staircase layout. The drawing shows a rectangular area with dimensions 3 000 (vertical) and 1 750 (horizontal). The vertical dimension is divided into segments of 50, 950, 1 000, 950, and 50. The horizontal dimension is divided into segments of 50, 1 000, and 700. The drawing includes a staircase structure with a landing and a flight. The staircase is labeled "контур лестницы" (staircase outline). The drawing also shows structural elements like walls and columns, labeled with "1" and "2".

Technical drawing of a staircase section (Ст2). The drawing shows a grid of 12 steps (3 rows by 4 columns). Dimensions include a width of 1800 and a depth of 300. The drawing includes structural supports and reinforcement details.

Поз. дет.	Тип сечения	Наименование	Кол -во	Масса ед., кг.	Приме чание
01	Швеллер	18П L=1 791мм.	4	29,19	
02	Швеллер	18П L=3 000мм.	1	49,39	
03	Квадратная труба	80x6 L=1 126мм.	2	15,61	
04	Квадратная труба	80x6 L=1 165мм.	1	16,13	
05	Квадратная труба	80x6 L=726мм.	4	9,87	
06	Лист	--5x100x100	4	0,40	
				254,58	

Поз. дет.	Тип сечения	Наименование	Кол -во	Масса ед., кг.	Приме чание
Ст2	---	ступень	18	16,26	
				292,68	

- 1) Соединение элементов сварное, сварка ручная электродуговая;
- 2) Материал: сталь С255
- 3) Окрасить грунтовкой ГФ-021 и эмалью ПФ115;

						ОПР-01/24/2024-КР.ГЧ			
						"Современный оптово-продовольственный рынок (ОПР) по адресу: Донецкая область, .г Макеевка, Горняцкий район			
Изм.	Кол.уч.	Лист	№Док.	Подп.	Дата				
Разраб.						Док-павильон (рыба-мясо) №23, №23.2 (по генплану)	Стадия	Лист	Листов
Пров.							П	29	
						Лестница Л2	ООО "Технология"		
Н. контроль									

Согласовано


Взам. инв. №

Подп. и дата

ЛНВ. № подл.

СХЕМА РАСПОЛОЖЕНИЯ КОЗЫРЬКОВ

1:200

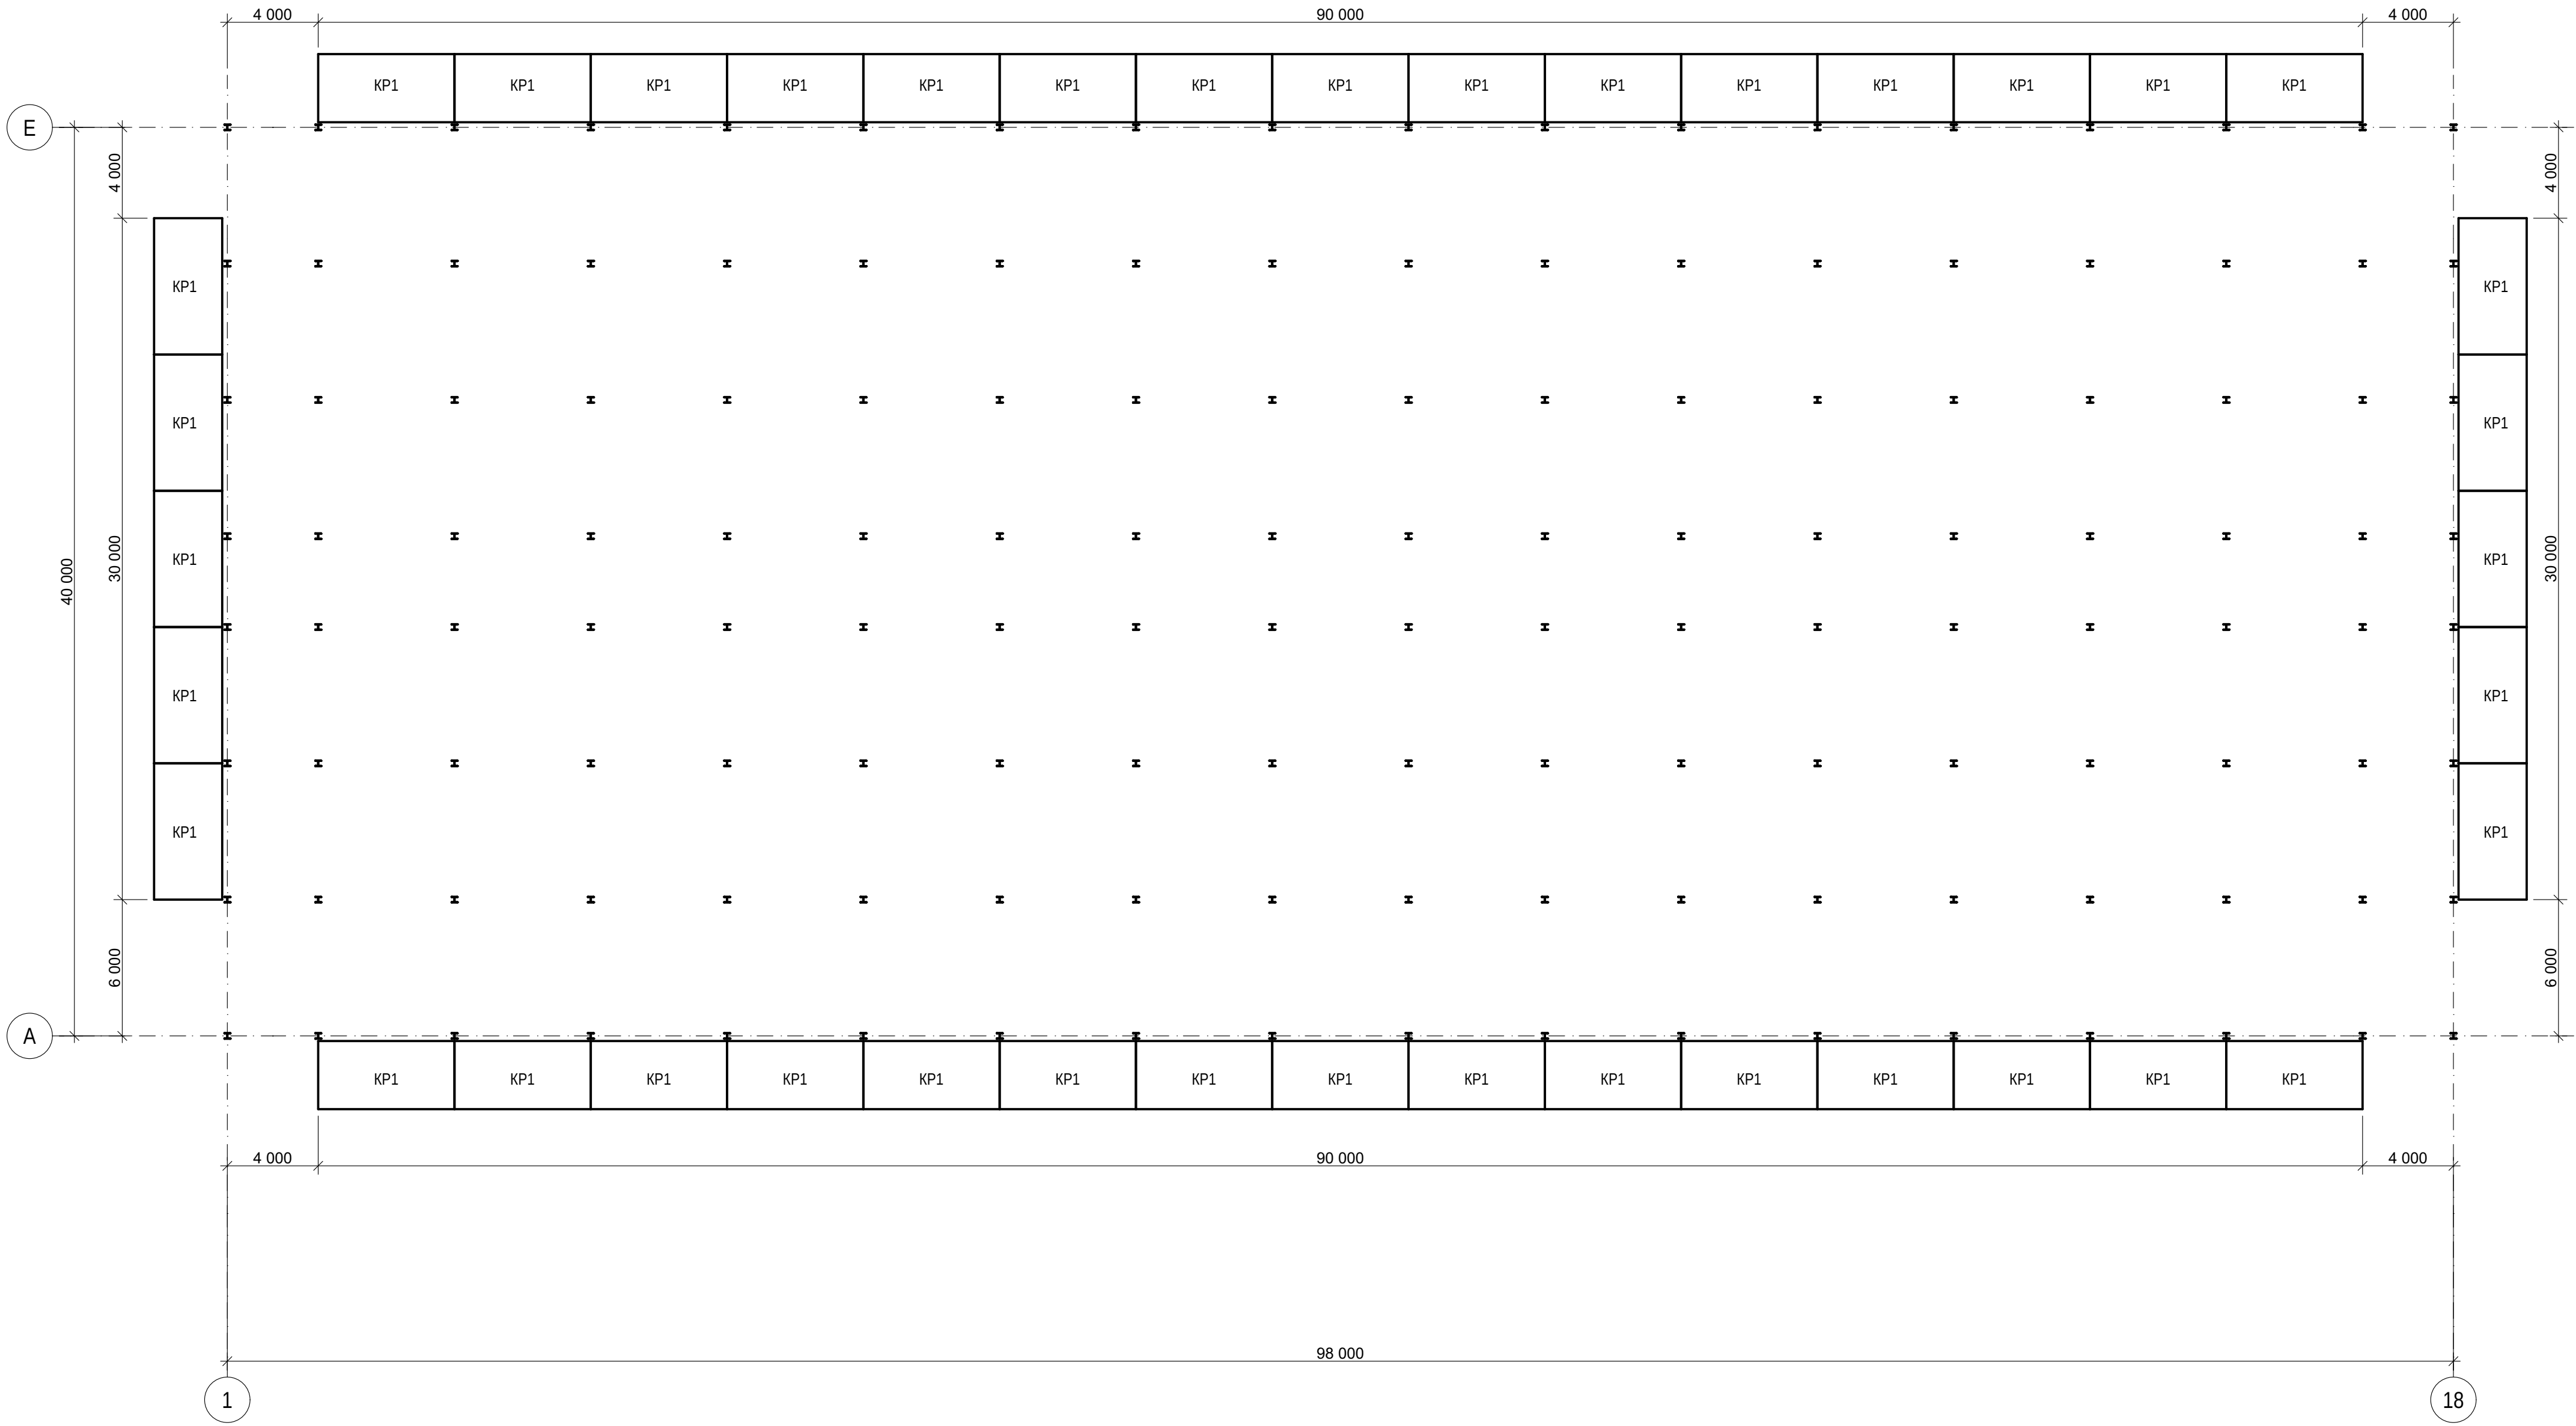


СПЕЦИФИКАЦИЯ КОЗЫРЬКОВ


Поз.	Обозначение	Наименование	Кол -во	Масса ед., кг.	Приме чание
КР1		козырек	40	885,84	
				35433,60	

							ОПР-01/24/2024-КР.ГЧ					
							"Современный оптово-продовольственный рынок (ОПР) по адресу: Донецкая область, г. Макеевка, Горняцкий район					
Изм.	Кол.уч.	Лист	№Док.	Подп.	Дата		Док-павильон (рыба-мясо) №23, №23.2 (по генплану)			Стадия	Лист	Листов
Разраб.										П	30	
Пров.												
							Схема расположения козырьков			ООО "Технология"		
Н. контроль												


1:50

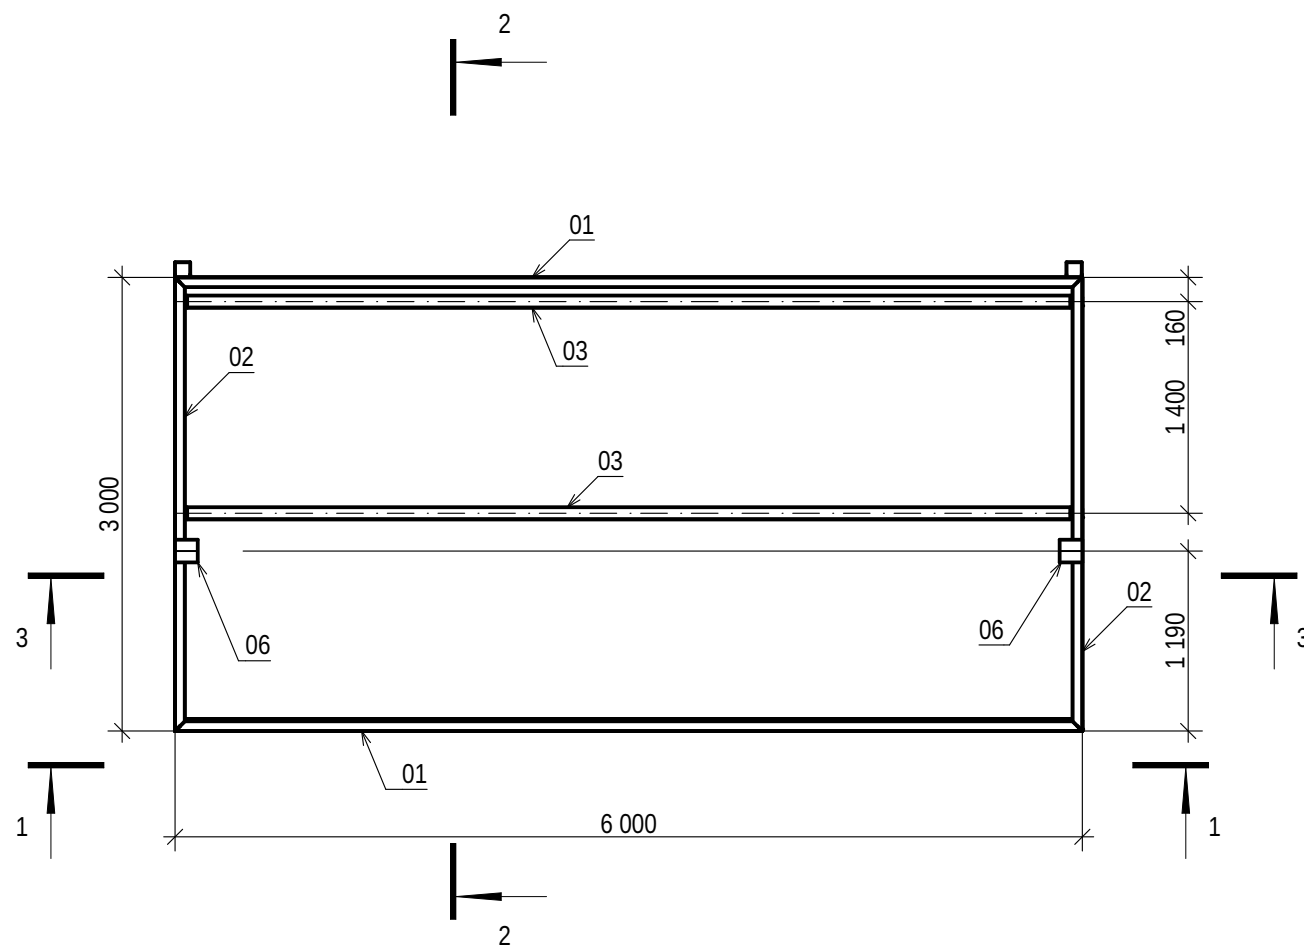


1:50

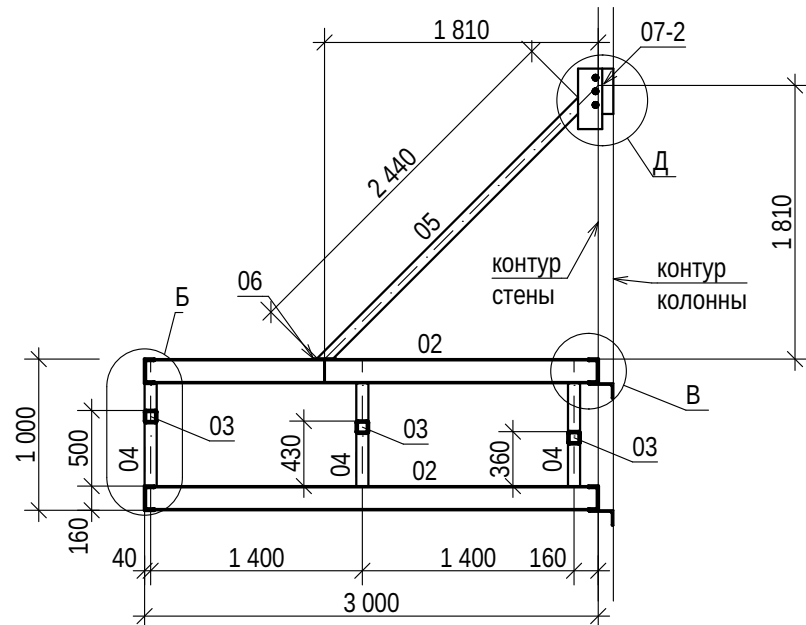


1:50

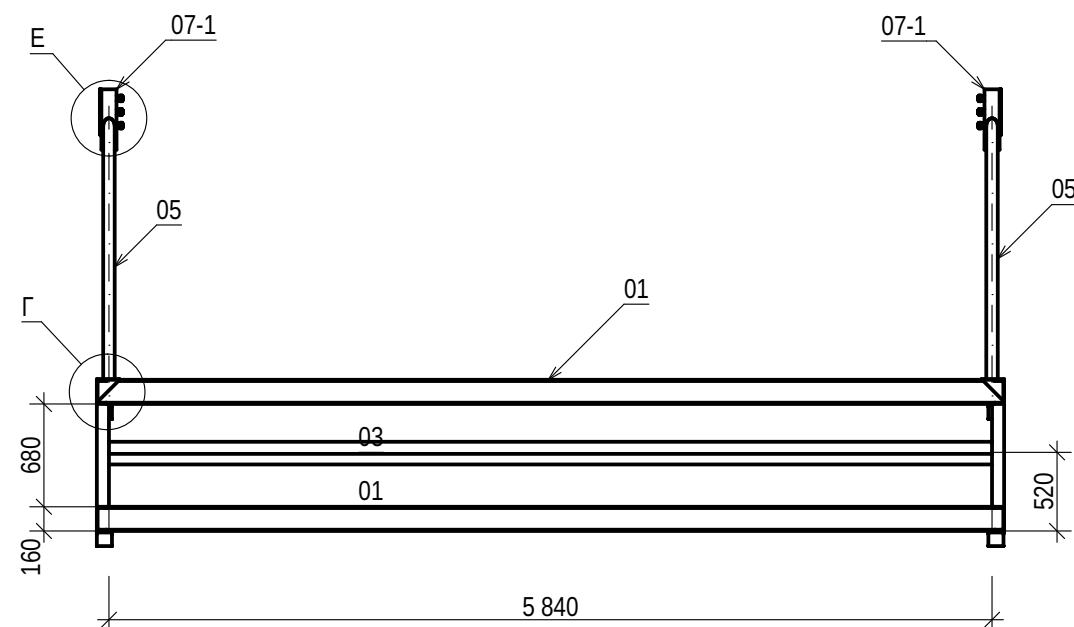



1:50

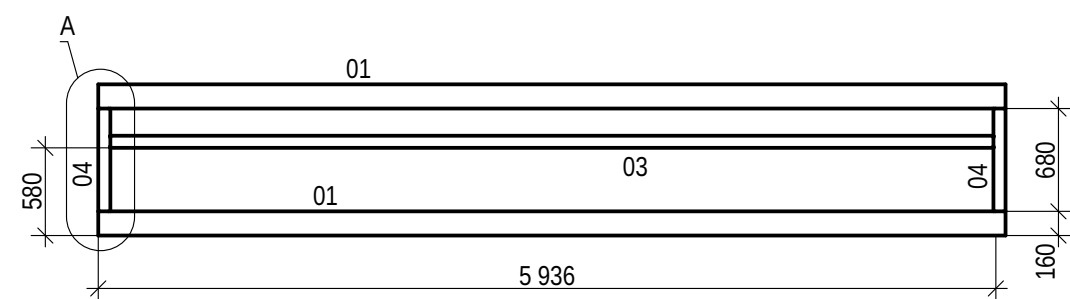


7

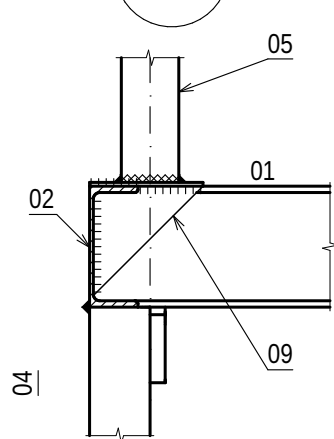


Ε

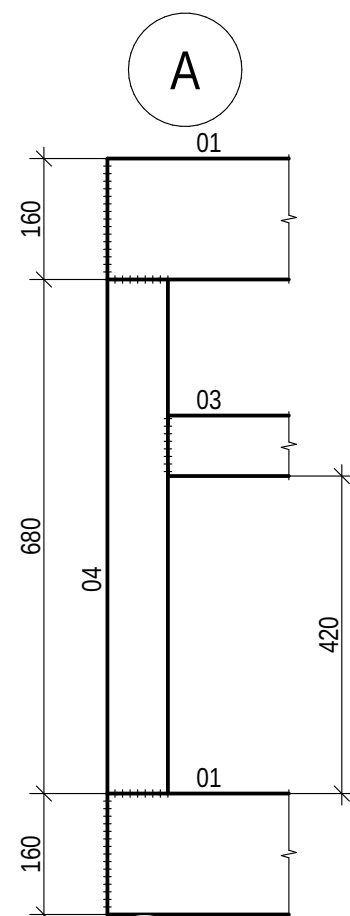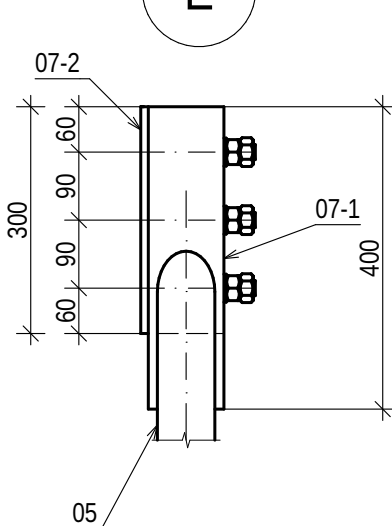


Б

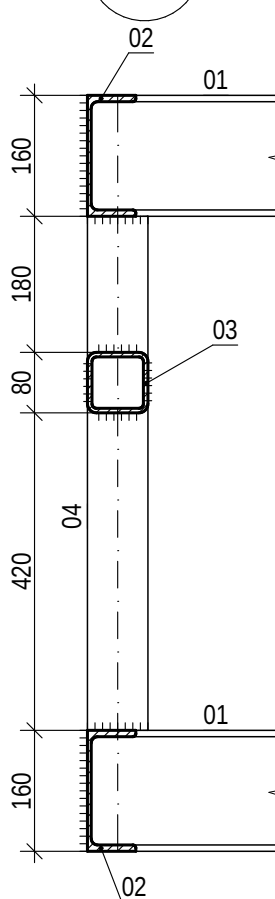

B

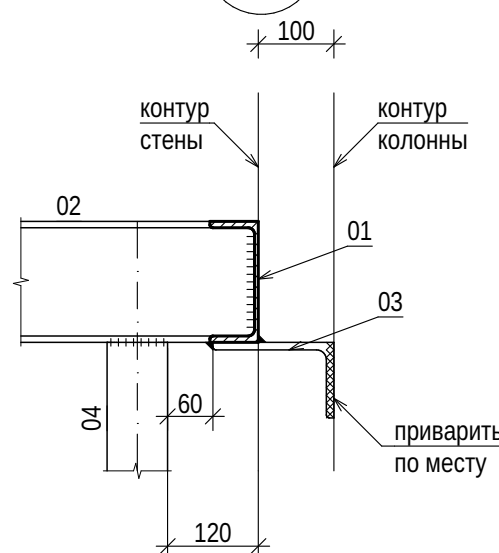

Д

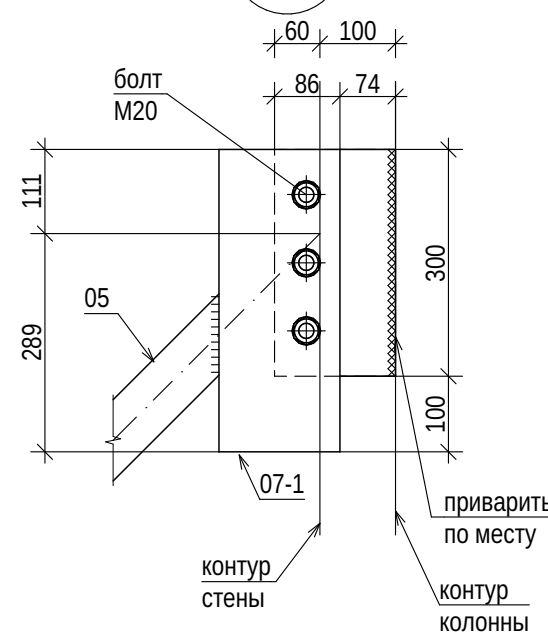

СПЕЦИФИКАЦИЯ ЭЛЕМЕНТОВ

Поз.	Тип сечения	Наименование	Кол-во	Масса ед., кг.	Примечание
01	Швеллер	16П L=6 000мм.	4	86,05	
02	Швеллер	16П L=2 968мм.	1	42,57	
02	Швеллер	16П L=3 000мм.	3	43,03	
03	Квадратная труба	80x6 L=5 840мм.	3	77,92	
04	Квадратная труба	80x6 L=680мм.	6	9,07	
05	Круглая труба	76.0x5.0 L=2 440мм.	2	21,56	
06	Лист	--5x150x150	2	0,89	
07-1	Уголок	L160x100x10 L=400мм.	2	8,02	
07-2	Уголок	L160x100x10 L=300мм.	2	6,01	
08	Уголок	L160x100x10 L=100мм.	4	2,00	
09	Лист	-- 140x140x5	2	0,42	
				885,84	

ПРИМЕЧАНИЯ:					
1) Соединение элементов сварное, сварка ручная электродуговая;					
2) Материал: сталь С255					
3) Окрасить грунтовкой ГФ-021 и эмалью ПФ115;					
ОПР-01/24/2024-КР.ГЧ					
"Современный оптово-продовольственный рынок (ОПР) по адресу: Донецкая область, г. Макеевка, Горняцкий район					
Изм.	Колуч.	Лист	№Док.	Подп.	Дата
Разраб.					
Пров.					
Док-павильон (рыба-мясо) №23, №23.2				Стадия	Лист
(по генплану)				П	31
Н. контроль				ООО "Технология"	