
План 1 этажа. Подключения ОВ к системам ВК. М 1:100

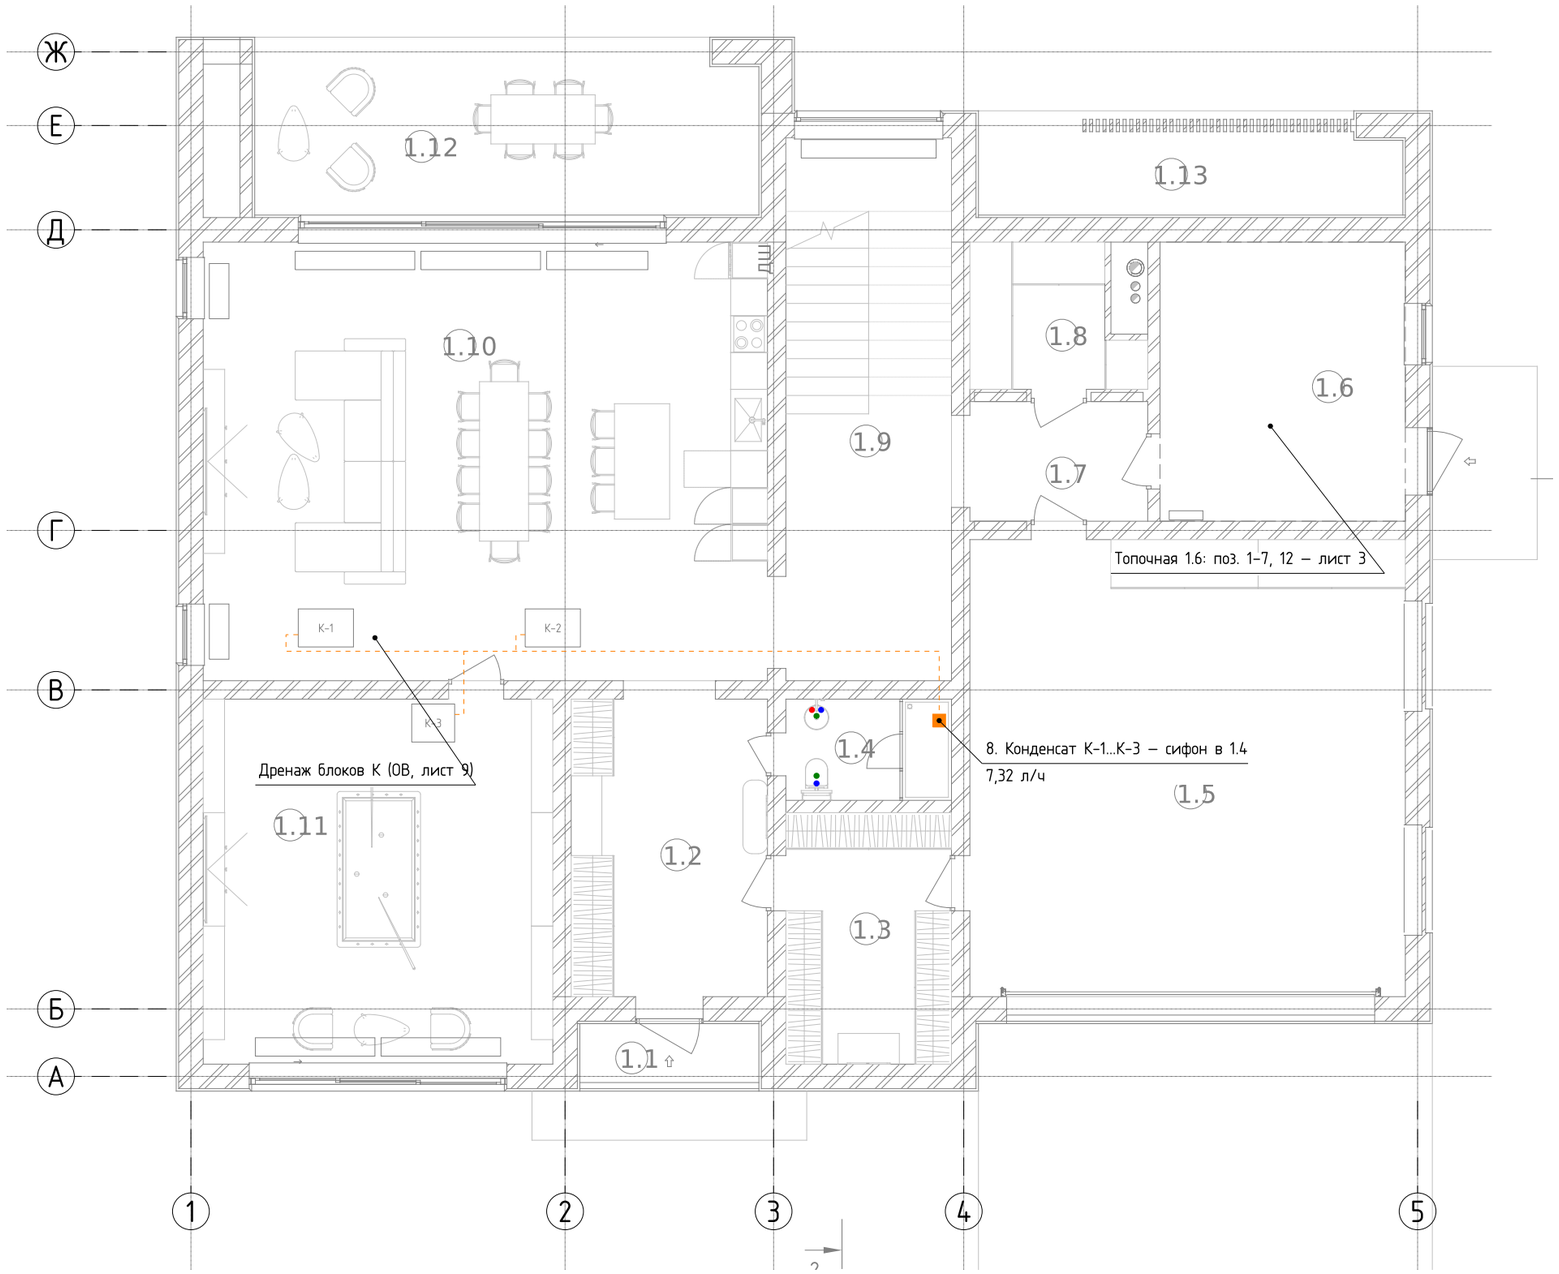

Условные обозначения

- подключение к водопроводу (В1, Т3, Т4, вода СПА)
- выпуск в канализацию (конденсат, трап, сбросы)
- дренаж конденсата, сбросы (ОВ) – для увязки
- оборудование ОВ (по листам РД ОВ) – для ориентации

Примечания

1. Точки подключения показаны условно – у оборудования; привязки и отметки уточнить по месту и паспортам выбранного оборудования. Номер у точки – позиция таблицы (лист 4).
2. Подложка – АР03, АР09, план бани (выгрузка из Revit 19.10.2026); оборудование ОВ – по листам 3–14 И05.09.26-ОВ.
3. Топочная 1.6 (поз. 1–7, 12) – фрагмент в М 1:50 на листе 3.

Согласовано

Взам.инв.№

Подпись и дата


Инв.№ подл.

Изм.	Кол.уч	Лист	№ док	Подп.	Дата	И05.09.26-ОВ.ТЗ-3			
						Двухэтажный индивидуальный жилой дом с баней. Московская область, кадастровый номер участка 50:08:0050209:1600			
Разраб.						Отопление, вентиляция и кондиционирование	Стадия	Лист	Листов
Пров.							Р	1	4
						Задание на водопровод и канализацию (ВК). План 1 этажа			
Н.контр.									
ГИП									

Копировал

Формат А3

План 2 этажа. Подключения ОВ к системам ВК. М 1:100

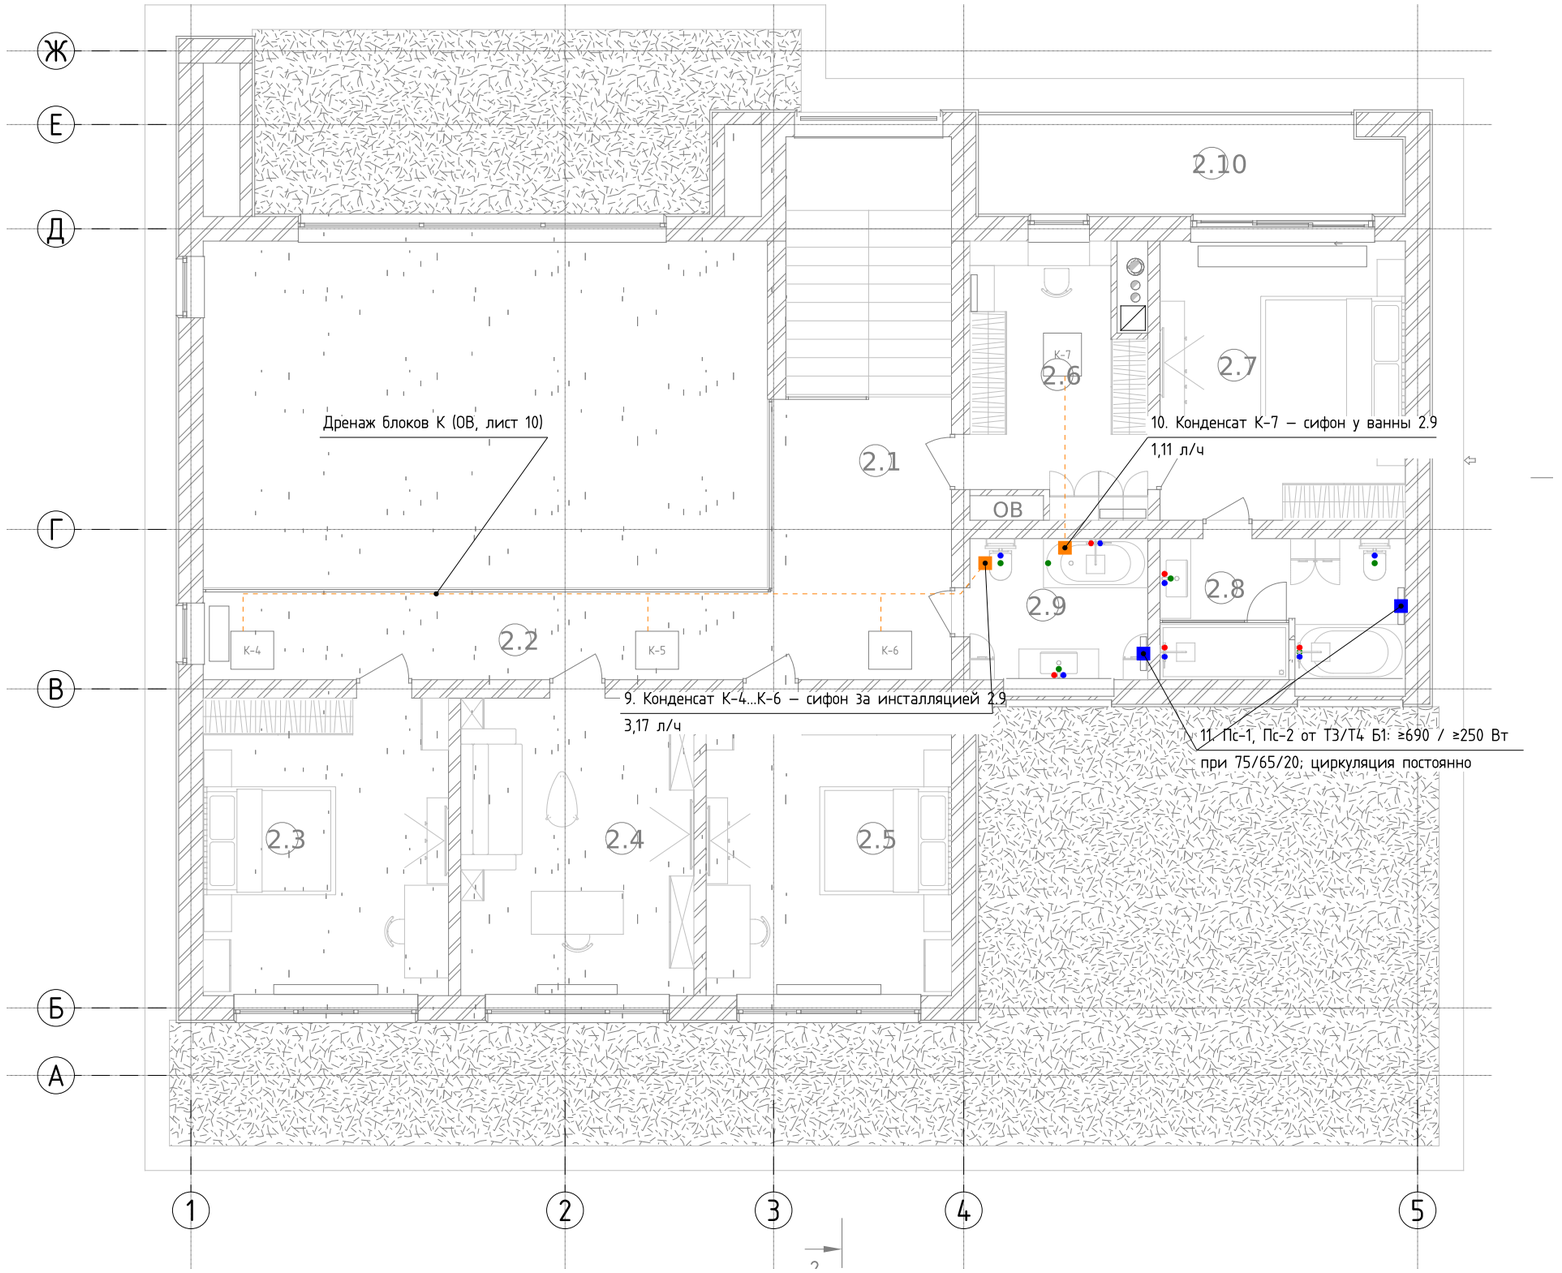

Условные обозначения

- подключение к водопроводу (В1, Т3, Т4, вода СПА)
- выпуск в канализацию (конденсат, трап, сбросы)
- дренаж конденсата, сбросы (ОВ) – для увязки
- оборудование ОВ (по листам РД ОВ) – для ориентации

Примечания

1. Точки подключения показаны условно – у оборудования; привязки и отметки уточнить по месту и паспортам выбранного оборудования. Номер у точки – позиция таблицы (лист 4).
2. Подложка – АР03, АР09, план бани (выгрузка из Revit 19.10.2026); оборудование ОВ – по листам 3–14 И05.09.26-ОВ.

Изм.	Кол.уч	Лист	№ док	Подп.	Дата	И05.09.26-ОВ.Т3-3			
						Двухэтажный индивидуальный жилой дом с баней. Московская область, кадастровый номер участка 50:08:0050209:1600			
Разраб.						Отопление, вентиляция и кондиционирование	Стадия	Лист	Листов
Пров.							Р	2	4
Н.контр.						Задание на водопровод и канализацию (ВК). План 2 этажа			
ГИП									

Согласовано

Взам.инв.№


Подпись и дата

Инв.№ подл.


Копировал

Формат А3

Топочная 1.6. М 1:50

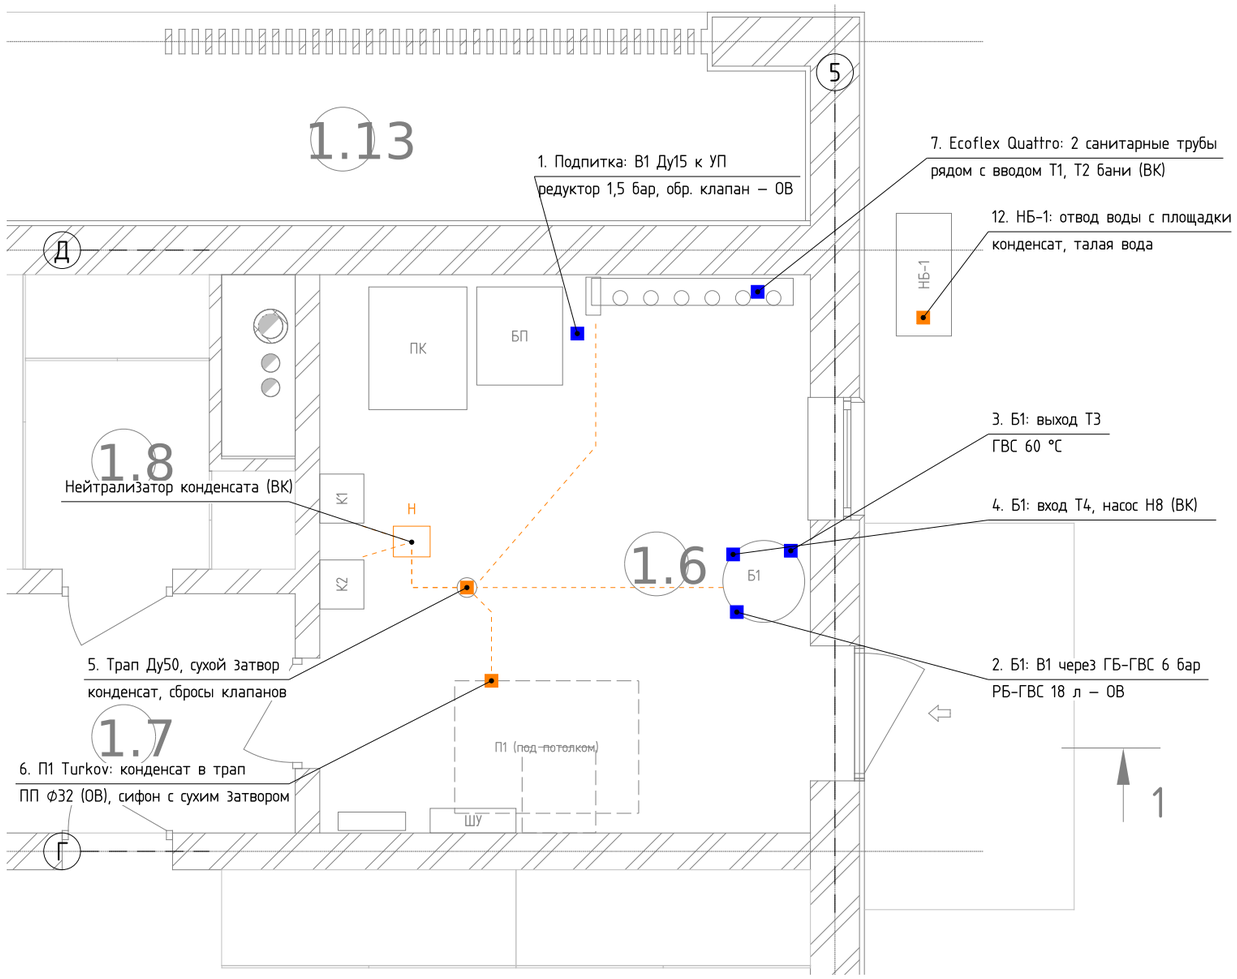

Баня. План. М 1:100

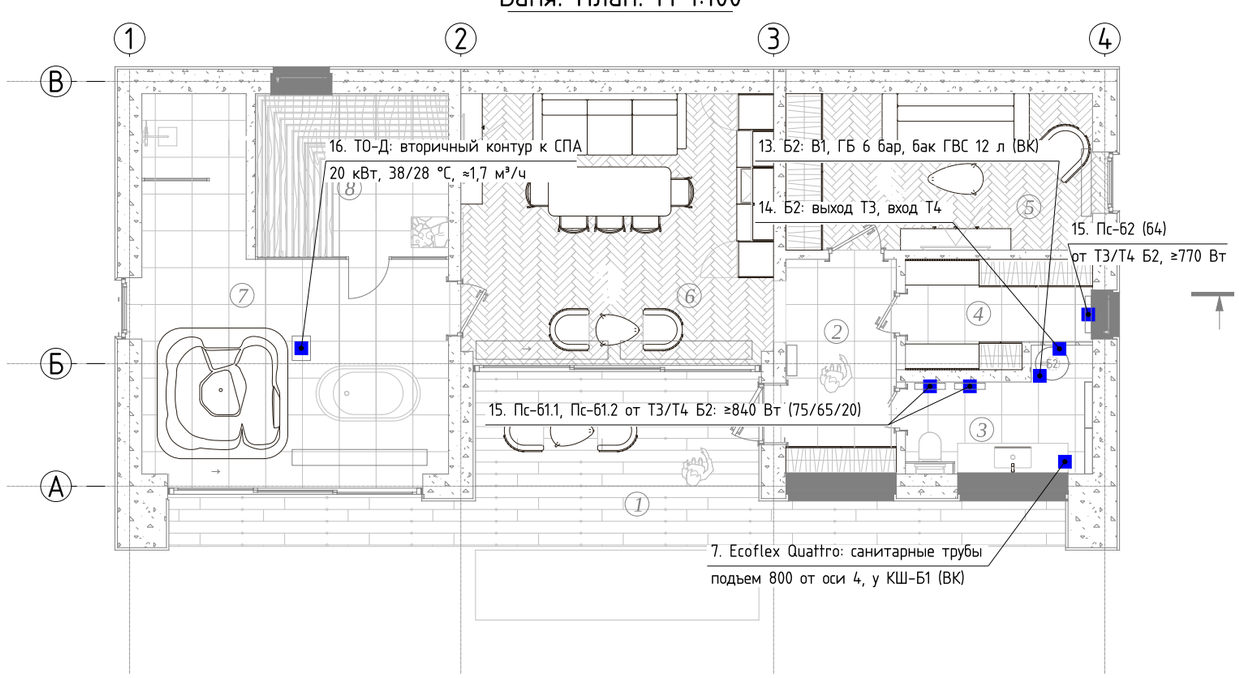

Условные обозначения

- подключение к водопроводу (В1, Т3, Т4, вода СПА)
- выпуск в канализацию (конденсат, трап, сбросы)
- дренаж конденсата, сбросы (ОВ) — для увязки
- оборудование ОВ (по листам РД ОВ) — для ориентации

Примечания

1. Точки подключения показаны условно — у оборудования; привязки и отметки уточнить по месту и паспортам выбранного оборудования. Номер у точки — позиция таблицы (лист 4).
2. Подложка — АР03, АР09, план бани (выгрузка из Revit 19.10.2026); оборудование ОВ — по листам 3–14 И05.09.26-ОВ.
3. Конденсат газовых котлов кислый — в трап только через нейтрализатор (ВК). Сбросы предохранительных клапанов — через воронки с разрывом струи.
4. Теплотрасса Ecoflex Quattro: Т1, Т2 — ОВ, две санитарные трубы — ВК; проходы через фундамент и плиту пола — общие (лист 13 ОВ, узлы 1, 2).

Изм.	Кол.уч	Лист	№ док	Подп.	Дата	И05.09.26-ОВ.ТЗ-3			
						Двухэтажный индивидуальный жилой дом с баней. Московская область, кадастровый номер участка 50:08:0050209:1600			
Разраб.						Отопление, вентиляция и кондиционирование	Стадия	Лист	Листов
Пров.							Р	3	4
Н.контр.						Задание на водопровод и канализацию (ВК). Топочная 1.6. Баня			
ГИП									

Согласовано

Взам.инв.№

Подпись и дата

Инв.№ подл.

Копировал

Формат А3

Подключения систем ОВиК к водопроводу и канализации

Поз.	Марка	Подключение	Помещение	Система	Расход, режим	Примечание
1	УП	Подпитка системы отопления: подвод ХВС с краном к узлу подпитки УП (фильтр, редуктор 1,5 бар, обратный клапан — оборудование ОВ, лист 8)	1.6, у ГС	В1, Ду15	при заполнении и по падению давления; объем системы ≈592 л	защита сети ХВС от обратного потока — по СП 30.13330 (обратный клапан или разделитель систем)
2	Б1	Подвод ХВС к бойлеру Б1 300 л через группу безопасности ГБ-ГВС 6 бар; бак РБ-ГВС 18 л — оборудование ОВ (лист 8)	1.6	В1	по расчету ВК	диаметр — по патрубку Б1 и расчету ВК; сброс ГБ — в трап (поз. 5) через воронку с разрывом струи
3	Б1	Выход ГВС от Б1 в сеть Т3	1.6	Т3, 60 °С	по расчету ВК	термическая дезинфекция Б1 — по программе контроллера (выше 60 °С); защита от ожогов у приборов — по ВК
4	Б1, Н8	Вход рециркуляции Т4 в Б1; насос рециркуляции Н8 — подбор и обвязка ВК (питание — Т3-2, поз. 12)	1.6	Т4	по таймеру	обратный клапан на Т4 перед Б1 — по ВК
5	Т	Трап Ду50 с сухим затвором в полу топочной	1.6	К1, Ду50	конденсат К1, К2 через нейтрализатор (по паспорту котлов Viessmann); сброс предохранительных клапанов (котловой контур 3 бар, ГБ-ГВС 6 бар); конденсат дымохода ПК; слив при опорожнении — шлангом	нейтрализатор конденсата котлов перед трапом — ВК; трап большую часть времени сухой — затвор сухого типа; уклон пола к трапу — АР; сюда же — конденсат П1 (поз. 6)
6	П1	Дренаж конденсата приточно-вытяжной установки П1 (Turkov Zenit 750 Heco W): труба ПП ⌀32 (ОВ) — сифон с сухим затвором — трап топочной (поз. 5)	1.6, под потолком	К1	по паспорту Turkov (зимой)	сифон с сухим затвором (установка под разрежением — высота затвора по паспорту Turkov); уклон не менее 0,01
7	Ecoflex	Две санитарные трубы PE-Xa в общей оболочке Ecoflex Quattro с Т1, Т2 бани (дом — баня, ≈16,4 м по трассе)	1.6 / баня, с/у Б3	по ВК	—	назначение и подключение — ВК; выходы — рядом с Т1, Т2: в топочной у северной стены, в бане — в с/у Б3 в 800 мм от оси 4 (западнее пилона АР), в коробе у КШ-Б1; диаметры — по комплектации трубы; гильзы и проходы — общие (лист 13 ОВ)
8	К-1…К-3	Дренаж конденсата внутренних блоков: трубы ПП ⌀32 с уклоном не менее 0,01 (ОВ) — сифон с сухим затвором	1.4	К1	7,32 л/ч летом (К-1, К-2 — по 2,81, К-3 — 1,70)	присоединение с разрывом струи; место сифона — по ВК
9	К-4…К-6	То же — сифон за инсталляцией унитаза	2.9	К1	3,17 л/ч летом	то же
10	К-7	То же — сифон у ванны	2.9	К1	1,11 л/ч летом	то же
11	Пс-1, Пс-2	Полотенцесушители в с/у 2.8 (Пс-1) и 2.9 (Пс-2) от Т3/Т4 бойлера Б1: не менее 690 и 250 Вт при 75/65/20 °С (359 и 128 Вт при 60/50 °С и tв 25 °С; показатель 1,25)	2.8, 2.9	Т3/Т4 60/50 °С	в отопительный период — циркуляция постоянно (закрывают недостачу тепла санузлов); уставка Б1 — не ниже 60 °С	рекомендуются комбинированные (вода + ТЭН ≈300 Вт); питание ТЭН — Т3-2, поз. 32; к КШ-4 не подключаются (лист 5 ОВ, решение Заказчика 20.10.2026)
12	НБ-1	Отвод воды с площадки наружного блока: конденсат и талая вода при оттайке (режим обогрева)	снаружи, у восточной стены 1.6	—	по паспорту НБ-1	не на отмостку и не под блок; зимой — без наледи (дренаж в грунт или лоток) — ВК и благоустройство
13	Б2	Обвязка ГВС бойлера бани Б2 200 л: подвод ХВС через группу безопасности 6 бар, мембранный бак ГВС 12 л (объем — по расчету ОВ)	баня, с/у Б3 (выгородка)	В1	по расчету ВК	ГБ и бак — раздел ВК (на листах ОВ их нет); сброс ГБ — в канализацию с разрывом струи; загрузка Б2 — с приоритетом (УК1, лист 13 ОВ)
14	Б2	Выход ГВС Т3 от Б2 к приборам бани; вход рециркуляции Т4 в Б2	баня, с/у Б3	Т3 60 °С, Т4	по расчету ВК	рециркуляция Т4 обязательна — через полотенцесушители поз. 15; насос рециркуляции бани и обратный клапан — подбор ВК
15	Пс-Б1.1, Пс-Б1.2, Пс-Б2	Полотенцесушители от Т3/Т4 бойлера Б2 при 75/65/20 °С: Пс-Б1.1, Пс-Б1.2 (с/у Б3) — каждый не менее 840 Вт (436 Вт при 60/50 °С и tв 25 °С); Пс-Б2 (раздевалка Б4) — не менее 770 Вт (419 Вт при tв 24 °С); показатель 1,25	баня, с/у Б3, раздевалка Б4	Т3/Т4 60/50 °С	в отопительный период — циркуляция постоянно (закрывают недостачу тепла Б3: 871 Вт, Б4: 419 Вт); уставка Б2 — не ниже 60 °С	рекомендуются комбинированные (вода + ТЭН ≈300 Вт) — греют и при выключенной рециркуляции; питание ТЭН — Т3-2, поз. 41; в систему отопления не входят (лист 12 ОВ)
16	ТО-Д	Вторичный контур теплообменника ТО-Д 20 кВт (38/28 °С) — к контуру фильтрации СПА (джакузи 1,8 м³)	баня, помывочная Б7	вода СПА	≈1,7 м³/ч при перепаде 10 °С; уточнить по насосу фильтрации	насос фильтрации, фильтр, обвязка — по паспорту СПА и ВК; материал пластин ТО — по химии воды СПА

Примечания

1. Задание разделу ВК на подключение оборудования отопления, вентиляции и кондиционирования по И05.09.26-ОВ. Точки — на листах 1-3.
2. Дренаж конденсата от блоков К до сифона (трубы ПП ⌀32, уклон не менее 0,01) — ОВ; сифоны с сухим затвором и присоединение к канализации — ВК. Расход конденсата — расчетный, летом при полной нагрузке.
3. Горячая вода — 60 °С на выходе Б1, Б2; рециркуляция Т4 и насос Н8 — подбор ВК. Циркуляция в отопительный период постоянная: через нее греют полотенцесушители Пс-1, Пс-2 (дом, поз. 11) и Пс-Б1.1, Пс-Б1.2, Пс-Б2 (баня, поз. 15), которые закрывают недостачу тепла санузлов и раздевалки бани.
4. Вторичный контур ТО-Д — по паспорту СПА: насос фильтрации, фильтр и химия воды определяют расход и материал теплообменника.

Изм.	Кол.уч	Лист	№ док	Подп.	Дата	И05.09.26-ОВ.Т3-3		
						Двухэтажный индивидуальный жилой дом с баней. Московская область, кадастровый номер участка 50:08:0050209:1600		
Разраб.						Отопление, вентиляция и кондиционирование	Стадия: Р	Лист: 4 / Листов: 4
Пров.								
Н.контр.						Задание на водопровод и канализацию (ВК). Таблица подключений. Примечания		
ГИП								

Согласовано

Взам.инв.№

Подпись и дата

Инв.№ подл.

Копировал

Формат А3